

213 MAPLE ST, WEEHAWKEN, NEW JERSEY

INTERIOR RENOVATION

APPLICABLE CODES

-INTERNATIONAL BUILDING CODE (IBC), 2021, NJ EDITION
-INTERNATIONAL RESIDENTIAL CODE (IRC), 2021, NJ EDITION
-NATIONAL ELECTRICAL CODE (NFPA 70), 2020
-NATIONAL STANDARD PLUMBING CODE, 2021
-INTERNATIONAL ENERGY CONSERVATION CODE, 2021, NJ EDITION (Low Rise Residential)
-ASHRAE 90.1-20189 (Commercial & all other Residential)
-INTERNATIONAL MECHANICAL CODE, 2021
-AMERICAN NATIONAL STANDARD, ICC 300-2017/ANSI A117.1-2017
(Chapter 11 of IBC/2021 & NJAC 5.23-7) -INTERNATIONAL FIRE CODE, 2021
-NJAC 5.23-6.7 RE-CONSTRUCTION



AREA OF WORK
213 MAPLE ST.,
WEEHAWKEN,
NEW JERSEY

1 LOCATION MAP

Scale:N.T.S

NO NEW AREAS NOR NEW VOLUME AS PART OR SCOPE OF WORK.
NOR ADDITIONAL BEDROOMS.

BUILDING:

1. PROVIDE TEMPORARY SUPPORTS AND DEMOLISH AS SHOWN.
2. PROVIDE RATED WALLS AND FLOOR/CEILING ASSEMBLY.
3. PROVIDE NEW WALL AND PARTITIONS PER SCHEDULE.
4. REMOVE COUNTER AND CABINETS AND PROVIDE NEW CABINETS AND APPLIANCES KITCHEN.
5. REMOVE, REPLACE EXISTING PLUMBING FIXTURES.
6. PROVIDE DOORS AS SHOWN.
7. PROVIDE FINISH ACCORDING TO FINISHING SCHEDULE.PAINT EXISTING/NEW WALLS, PARTITIONS AND CEILINGS.

2 SCOPE OF WORK

Scale:N.T.S

PROJECT DATA

ADDRESS : 213 MAPLE ST., WEEHAWKEN , **BLOCK:** 29 **LOT:** 6
NJ
ZONE: R-3. One, Two and Three Family Residence Zone including
Townhouses
PROJECT DESCRIPTION: INTERIOR RENOVATION.

N.J.U.C.C. DATA:

USE GROUP: R3-Two family

TYPE OF CONSTRUCTION : VA

EXISTING TOTAL FLOOR AREA: 2,763.00 SQFT

PROPOSED TOTAL FLOOR AREA: 2,763.00 SQFT

NO CHANGE IN AREA

EXISTING TOTAL VOLUME: 49,734.00 C.F.

PROPOSED TOTAL VOLUME: 49,734.00 C.F.

NO CHANGE IN VOLUME

- NO CHANGES OF USE.
- ALL FIRE ALARM DEVICES INSIDE RESIDENTIAL
UNITS SHALL BE HIGH VOLTAGE INTERCONNECTED
WITH BATTERY BACK-UP

3 PROJECT DATA

Scale:N.T.S

FIRE RESISTANCE RATING REQUIREMENTS FOR BUILDING ELEMENTS AS PER TABLE 601 IBC NJ 2021 TYPE V-B

BUILDING ELEMENT	REQUIRED	PROVIDED	REMARK
STRUCTURAL FRAME	1 HOURS	1 HOURS	
BEARING EXTERIOR WALLS	1 HOURS	1 HOURS	
BEARING INTERIOR WALLS	1 HOURS	1 HOURS	
NON-BEARING EXTERIOR WALLS	1 HOURS	1 HOURS	
NON-BEARING INTERIOR WALLS	0 HOURS	0 HOURS	
FLOOR CONSTRUCTION	1 HOURS	1 HOURS	
ROOF CONSTRUCTION	1 HOURS	1 HOURS	

2-FAMILY	EXISTING SQ. FOOT AREA	PROPOSED SQ. FOOT AREA	PROPOSED NET AREA	# OF BEDROOM	
				EXISTING	PROPOSED
UNI.#1	864.00	864.00	1255	2	2
UNI.#2	922.00	922.00	565	2	2
BASEMENT	977.00	977.00	-	-	-

GENERAL NOTES

RESPONSIBILITY OF CONTRACTOR

1. ALL WORK SHALL BE IN CONFORMANCE WITH ALL APPLICABLE REQUIREMENTS OF THE NEW JERSEY UNIFORM CONSTRUCTION CODE, IT'S SUBCODES, LOCAL CODES AND ORDINANCES AND SAFETY SEISMIC REQUIREMENTS. ALL WORK SHALL BE SUBJECT TO INSPECTION BY LOCAL OFFICIALS AND MUST MEET THEIR APPROVAL.
2. CONTRACTOR SHALL OBSERVE ALL LAWS AND ORDINANCES GOVERNING THE WORK OF HIS CONTRACT.
3. THE CONTRACTOR SHALL, BEFORE SUBMITTING HIS PROPOSAL FOR THE WORK, VISIT THE SITE AND/OR PREMISES AND OBTAIN ALL INFORMATION THAT WILL AFFECT HIS BID. FAILURE TO DO SO WILL NOT RELIEVE THE CONTRACTOR'S RESPONSIBILITY TO CONFORM TO THE REQUIREMENTS OF THE CONSTRUCTION DOCUMENTS.
4. THE CONTRACTOR SHALL COORDINATE HIS WORK WITH ALL OTHER TRADES AND THE OWNER SO AS TO CAUSE NO DELAY IN THE WORK. HE SHALL CONSULT WITH VARIOUS TRADES INVOLVED TO DETERMINE THE AREAS OF POTENTIAL INTERFERENCE PRIOR TO STARTING WORK AND FURNISH TO THE APPROPRIATE TRADES ADVANCE NOTICE AND INFORMATION REQUIRED FOR THE WORK OF OTHERS.
5. THE CONTRACTOR SHALL PROVIDE ALL PROTECTION MEASURES FOR THE SAFETY OF THE PUBLIC AND WORKMEN DURING THE COURSE OF WORK.
6. THE CONTRACTOR SHALL PERFORM ALL OPERATIONS AND FURNISH ALL MISCELLANEOUS ITEMS NECESSARY FOR THE PROPER INSTALLATION AND PERFECT APPEARANCE OF THE WORK.
7. THE CONTRACTOR SHALL PROVIDE ALL ITEMS, ARTICLES, MATERIALS, EQUIPMENT, OPERATIONS OR METHOD LISTED, MENTIONED, SCHEDULED OR REASONABLY INFERABLE FROM THE DRAWINGS, INCLUDING ALL LABOR, MATERIALS, EQUIPMENT AND INCIDENTALS NECESSARY AND REQUIRED FOR THE COMPLETION OF THE WORK.
8. THE CONTRACTOR SHALL NOTIFY THE ARCHITECT IN WRITING PRIOR TO HIS BID OF ANY DISCREPANCIES SHOWN ON THE DRAWINGS THAT DO NOT REFLECT ACTUAL FIELD CONDITIONS.
9. THE CONTRACTOR SHALL COORDINATE ALL WORK AND SCHEDULING WITH THE OWNER.
10. THE CONTRACTOR SHALL COORDINATE ALL FINISHES AND EQUIPMENT WITH THE OWNER.
11. THE CONTRACTOR SHALL SUBMIT ALL REQUIRED SHOP DRAWINGS. NO WORK SHALL PROCEED WITHOUT SHOP DRAWINGS BEING REVIEWED BY THE ARCHITECT AND/OR ENGINEER.

PERMITS, FEES AND NOTICES

1. THE CONTRACTOR SHALL FILE PLANS TO THE PROPER AUTHORITIES.
2. THE CONTRACTOR SHALL SECURE AND PAY FOR THE BUILDING PERMITS AND FOR ALL OTHER PERMITS AND GOVERNMENTAL FEES, LICENSES, AND INSPECTIONS NECESSARY FOR THE PROPER EXECUTION AND COMPLETION OF THE WORK. THE FEES FOR PERMITS SHALL BE REIMBURSED BY THE OWNER. THE GENERAL CONTRACTOR SHALL OBSERVE ALL LAWS AND ORDINANCES COVERING THE WORK OF THIS CONTRACT.
3. THE CONTRACTOR SHALL PROVIDE THE OWNER WITH CERTIFICATE OF INSPECTIONS AND OCCUPANCY.

DOCUMENTS AND SAMPLES

1. THE CONTRACTOR SHALL MAINTAIN AT SITE FOR THE OWNER TWO (2) RECORD COPIES OF ALL DRAWINGS, APPROVED SHOP DRAWINGS, PRODUCT DATA AND SAMPLES, CONSTRUCTION SPECIFICATIONS, ADDENDA, CHANGE ORDERS AND OTHER MODIFICATIONS. DOCUMENTS SHALL BE KEPT IN GOOD ORDER AND UPDATED TO RECORD ALL CHANGES MADE DURING CONSTRUCTION.

SUPERVISION AND CONSTRUCTION PROCEDURES

1. THE CONTRACTOR SHALL SUPERVISE AND DIRECT THE WORK USING HIS BEST SKILL AND ATTENTION. HE SHALL BE SOLELY RESPONSIBLE FOR ALL SAFETY STANDARDS AND OSHA REQUIREMENTS, CONSTRUCTION MEANS, METHODS, TECHNIQUES, SEQUENCES, AND PROCEDURES AND FOR COORDINATING ALL PORTIONS OF THE WORK.
2. THE CONTRACTOR SHALL BE RESPONSIBLE FOR THE ACTS AND OMISSIONS OF HIS EMPLOYEES, SUBCONTRACTORS AND THEIR AGENTS, AND OTHER PERSONS PERFORMING ANY OF THE WORK UNDER THE CONSTRUCTION DOCUMENTS.

WORKMANSHIP

1. ALL WORK SHALL BE PERFORMED BY CRAFTSMEN SKILLED IN THEIR RESPECTIVE TRADES WHO SHALL AT ALL TIMES, BE UNDER THE SUPERVISION OF A COMPETENT PERSON, WHO IS TRAINED IN THEIR CRAFT.
2. ALL WORK ON THIS PROJECT SHALL BE DONE IN THE BEST WORKMANSHIP MANNER. WORK THAT IS NOT CONSISTENT WITH THE STANDARDS GENERALLY REGARDED IN THE TRADE AS "FIRST-CLASS" WORK WILL NOT BE ACCEPTABLE.

4 GENERAL NOTES

Scale:N.T.S

DRAWING APPROVAL PROCESS:

DESIGN: RVV	DRAW: JGR	CHECKED: RVV	APPROVED: RVV
----------------	--------------	-----------------	------------------

DESIGN PROFESSIONAL:

RUDY V. VAZQUEZ, PE

(NY) LIC.# 083403-1
(NJ) LIC.# 24GE04511500
(FL) LIC.# 63722
NCEES Reg. # 27048

ENGINEER HAS NOT BEEN RETAINED FOR FIELD
INSPECTIONS

DESIGN PROFESSIONAL:

JAI
ARCHITECT LLC
ARCHITECT / PLANNER

201-240-7484
jaiarchitects@gmail.com

JOSE A. IZQUIERDO, AIA

(NY) LIC.#017014-1
(NJ) LIC.#09143
(NJ) PLN.#03385

DRAWING SHEET SCHEDULE:

SHT#:	NAME:
G-01	LOCATION MAP, PROJECT DATA, SCOPE OF WORK AND
GENERAL NOTES	
G-02	PENETRATIONS THROUGH RATED ASSEMBLIES
G-03	PARTITION TYPE
G-04	FLOORS EGRESS PLAN AND NOTES
G-05	DEMOLITION PLAN AND NOTES
G-06	CONSTRUCTIONS PLAN AND NOTES
G-07	PLAN INTERIOR FINISH
G-08	DOOR ELEVATIONS, SCHEDULE AND HARDWARE SET
G-09	ELEVATION, SECTION AND DETAILS

NO CHANGES SHALL BE MADE UNLESS A
WRITTEN CONSENT FOR THE DEVIATION IS
APPROVED BY THE ARCHITECT OR ENGINEER

REVISION RELEASE SCHEDULE:

REV#:	DATE:	RELEASE / CHANGES:
0	11-10-25	CUSTOMER RELEASE

KEY PLAN:

BLOCK
29
LOT
6

DEVIATIONS:

ALL CONDITIONS ON THIS SET OF PRINTS ARE
TO BE USED EXACTLY AS PRESCRIBED. ANY
DEVIATION WILL DISRUPT THE SYSTEM AND
MAY CAUSE OTHER ITEMS NOT TO FUNCTION
AS INTENDED OR FAIL.

DRAWING TITLE:
LOCATION MAP, PROJECT DATA, SCOPE OF WORK
AND GENERAL NOTES

PROJECT:

INTERIOR RENOVATION

SITE:

213 MAPLE ST, WEEHAWKEN, NEW JERSEY

OWNER: ZHANG, CHI & JIE,
YANG

PROJECT:
PR25-0096

SIZE:

D

SCALE:

AS NOTED


DRAWING:

DC25-0127

SHEET:


G-01

NOTES AND DETAILS FOR PENETRATIONS
THROUGH RATED ASSEMBLIES

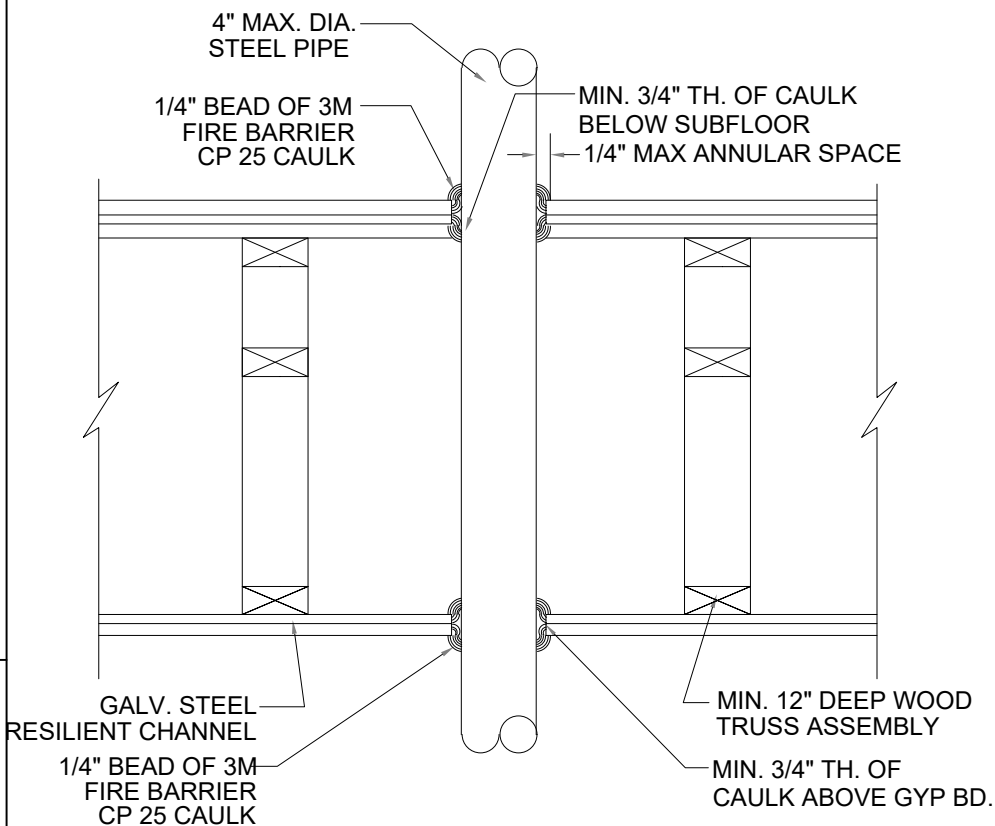


PENETRATION FIRESTOP OF A 4" MAX. DIA. STEEL PIPE 3" COPPER PIPE 4" CAST IRON PIPE STEEL EMT CONDUIT THROUGH A WOOD & METAL PIPE TRUSS FLOOR/ CEILING ASSEMBLY- 1 HR. RATED U.L. LISTING - F-C-1006

SCALE: NTS

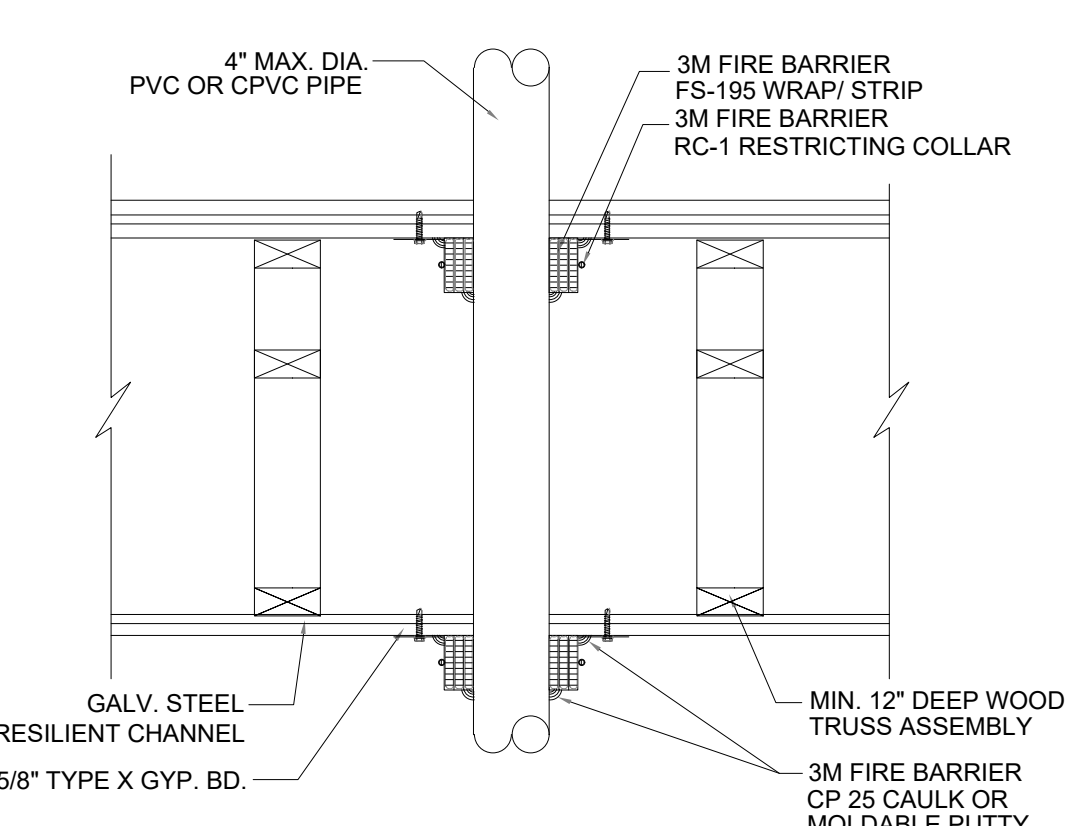


PENETRATION FIRESTOP FOR 4" MAX. DIA. PLASTIC PIPE THROUGH A WOOD & METAL PIPE TRUSS FLOOR/ CEILING ASSEMBLY- 1 HR. RATED U.L. LISTING - F-C-2029

SCALE: NTS

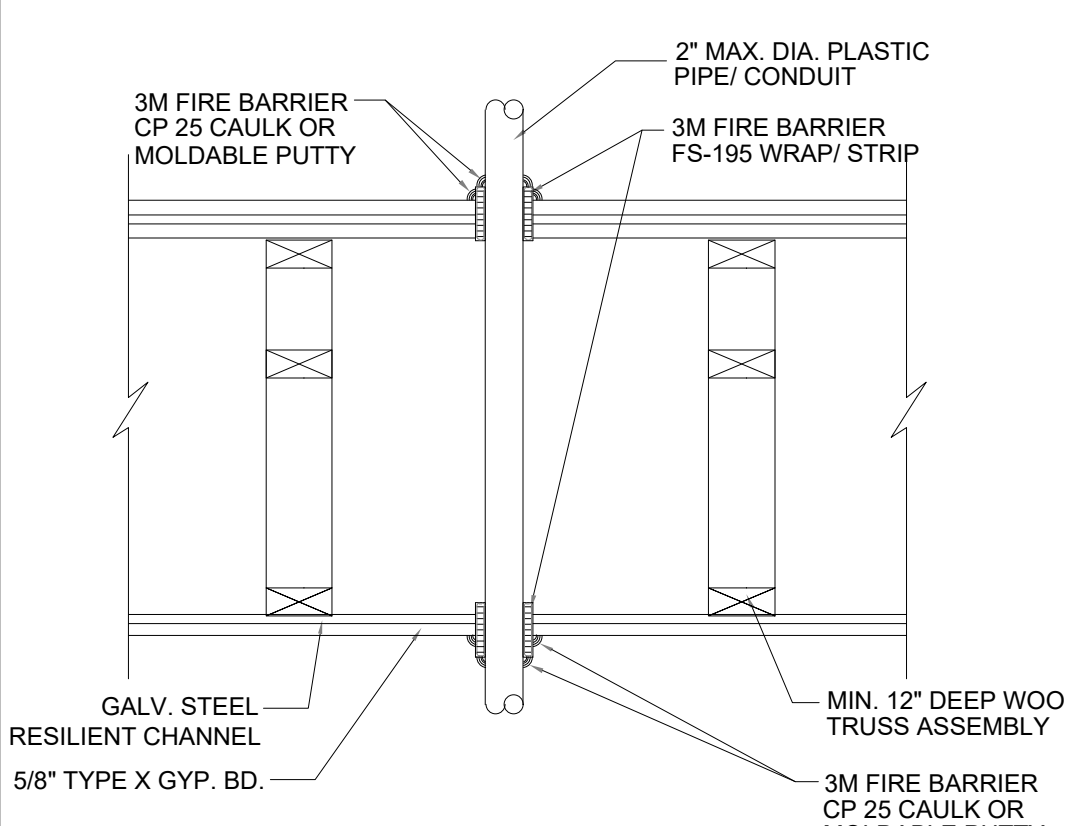


PENETRATION FIRESTOP FOR 2" MAX. DIA. PLASTIC PIPE/ CONDUIT THROUGH A WOOD & METAL PIPE TRUSS FLOOR/ CEILING ASSEMBLY- 1 HR. RATED U.L. LISTING - F-C-2008

SCALE: NTS

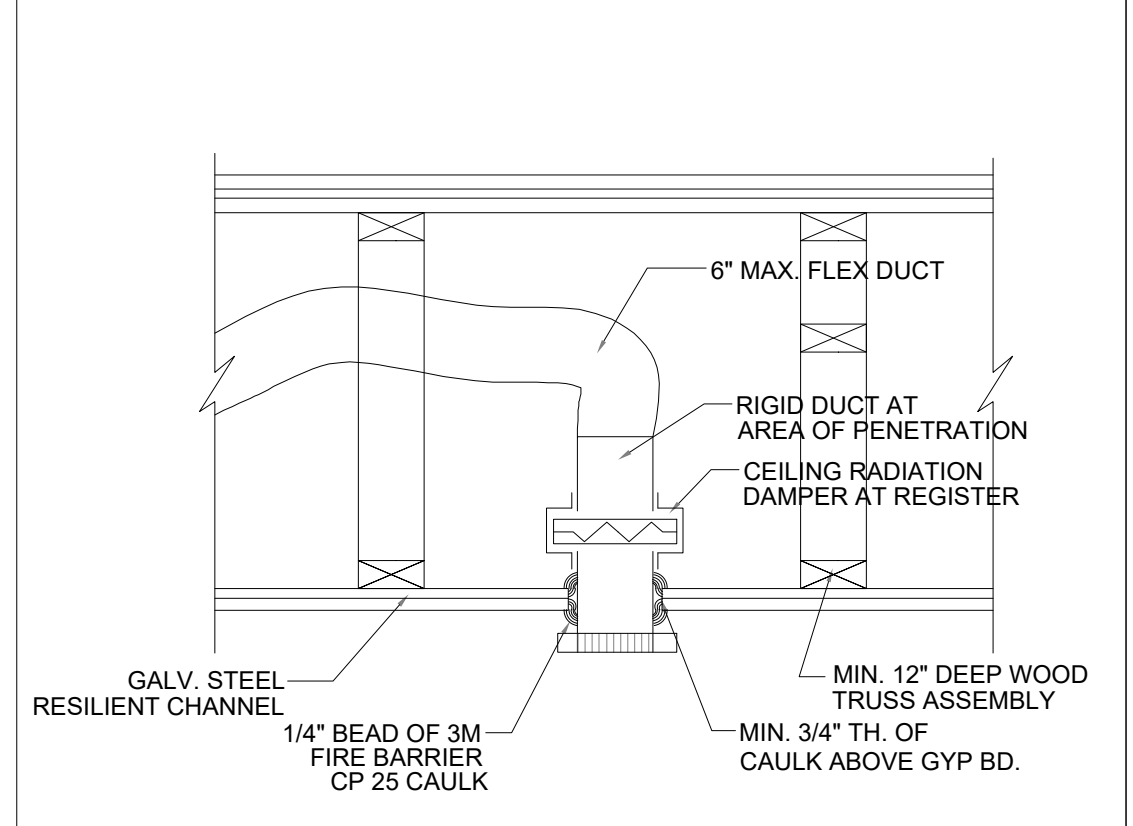


PENETRATION FIRESTOP FOR NOM. 6" MAX. DIA. RIGID SHEET METAL AIR SUPPLY/ RETURN DUCT THROUGH WOOD & METAL PIPE FLOOR ASSEMBLY - 1 HR. RATED U.L. LISTING - F-C-2008

SCALE: NTS

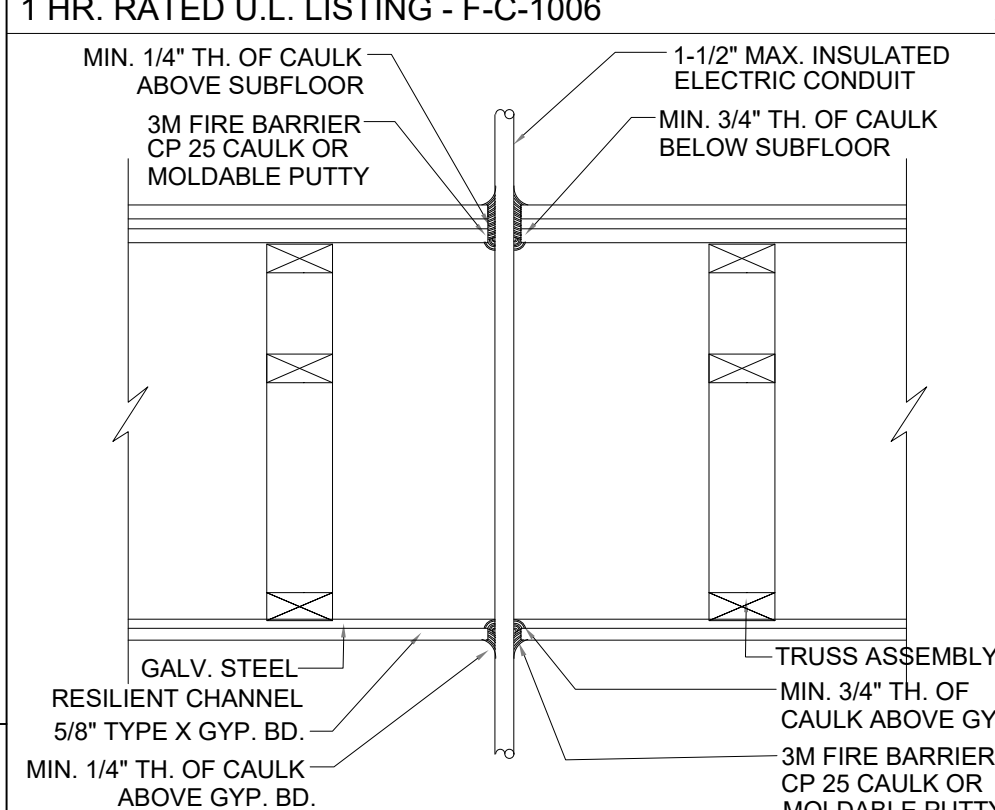


PENETRATION FIRESTOP FOR 1-1/2" MAX. DIA. ELECTRIC CONDUIT THROUGH A WOOD & METAL PIPE TRUSS FLOOR/ CEILING ASSEMBLY- 1 HR. RATED U.L. LISTING - F-C-3007

SCALE: NTS

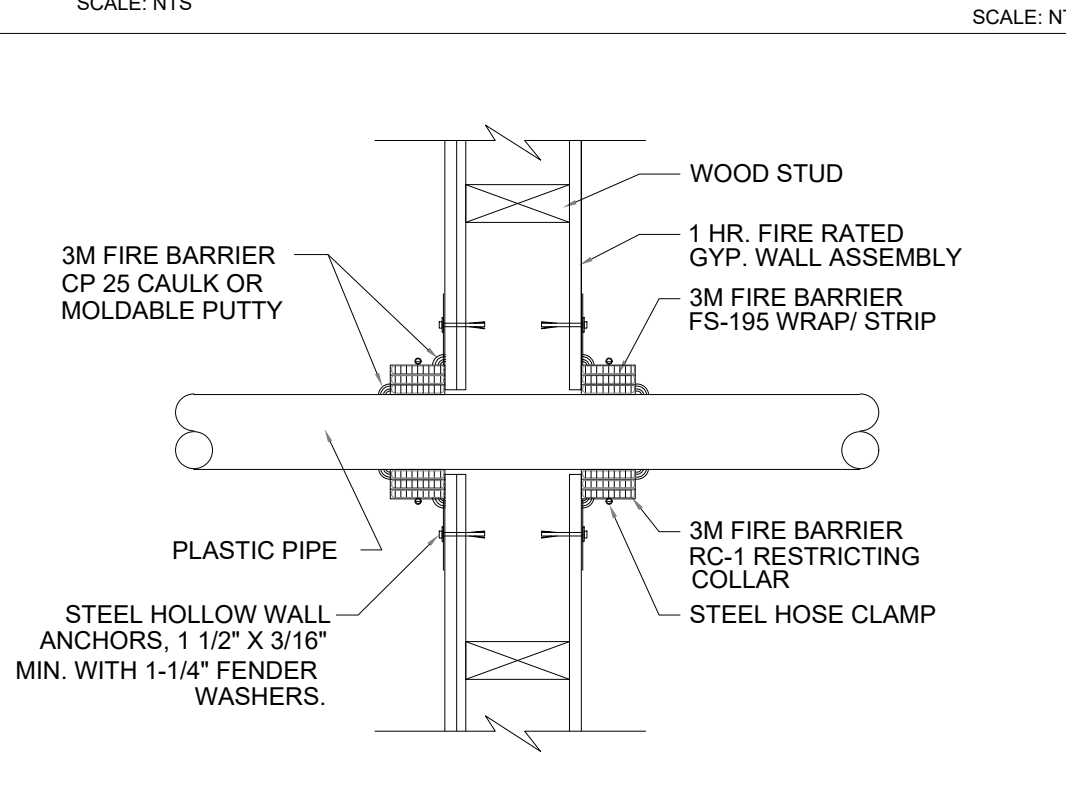


PENETRATION FIRESTOP FOR 4" MAX. DIA. ABS & PVC PLASTIC PIPE THROUGH A GYPSUM WALLBOARD ASSEMBLY- 1 HR. RATED U.L. LISTING - W-L-2059

SCALE: NTS

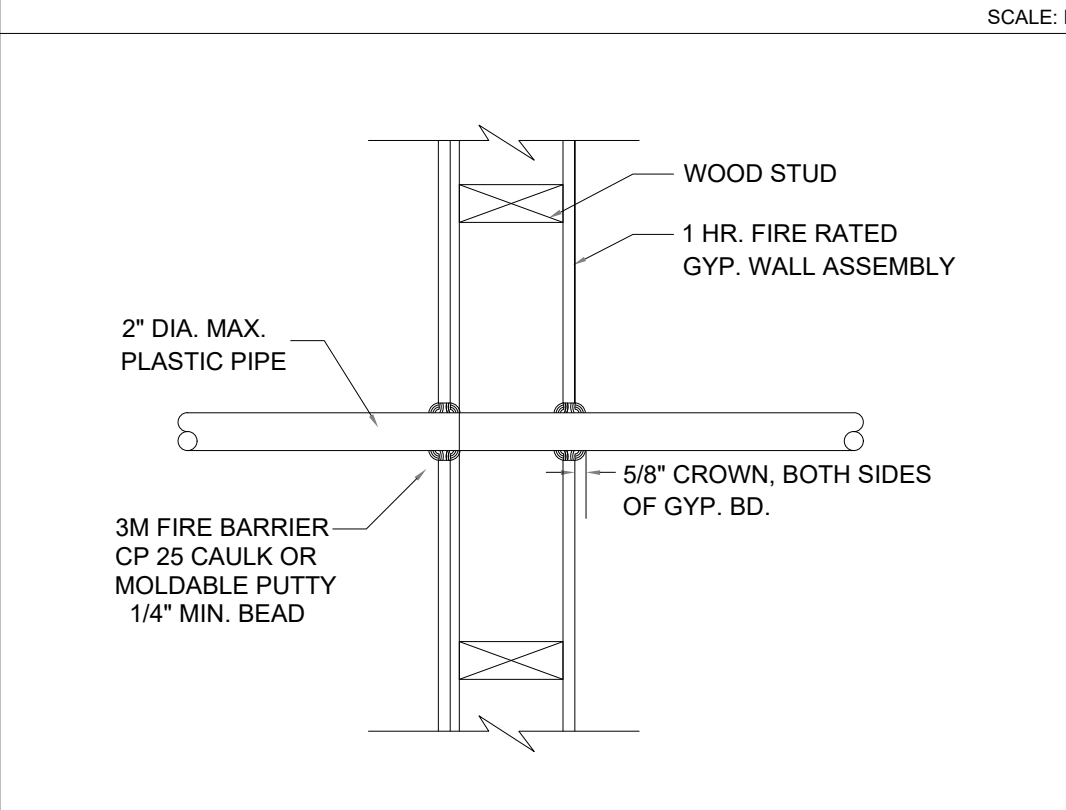


PENETRATION FIRESTOP FOR 2" MAX. DIA. PB, PP, PVC PLASTIC PIPE/ CONDUIT/ COPPER PIPE THROUGH A GYPSUM WALLBOARD ASSEMBLY- 1 HR. RATED U.L. LISTING - W-L-2067

SCALE: NTS

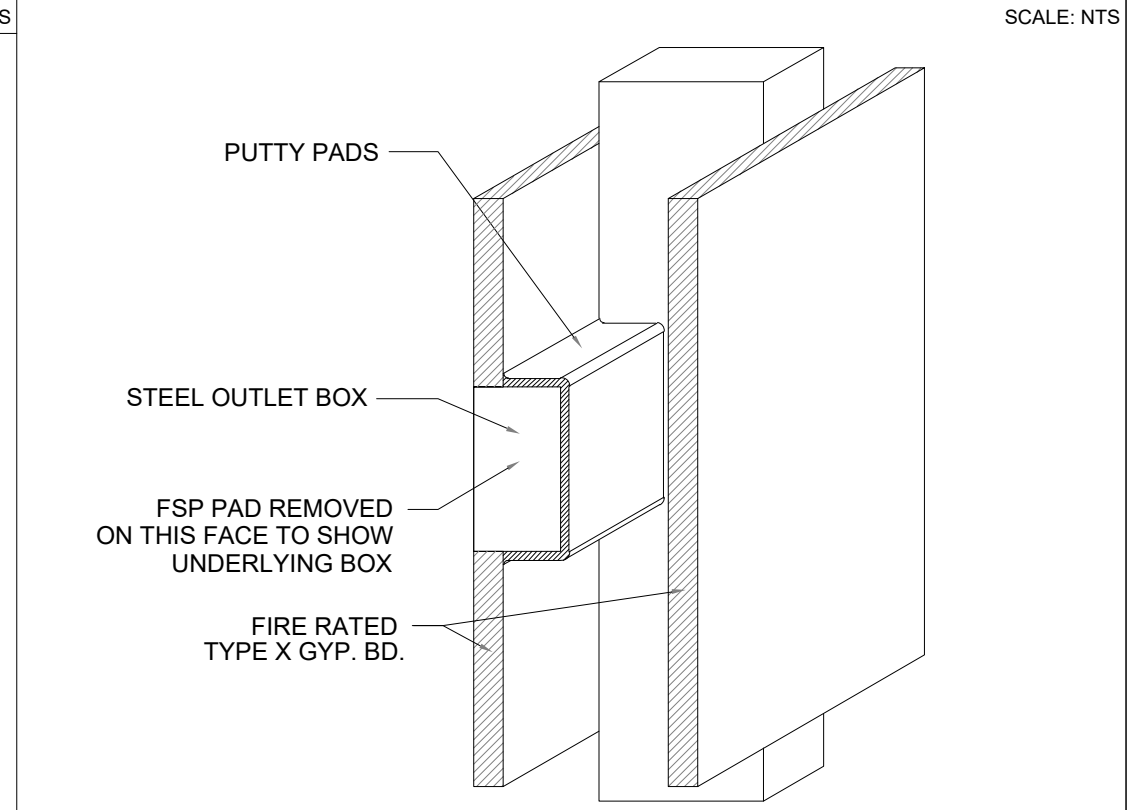


GYPSUM WALL ELECTRICAL OUTLET BOX WALLBOARD ASSEMBLY- 1 HR. ASSEMBLY

SCALE: NTS

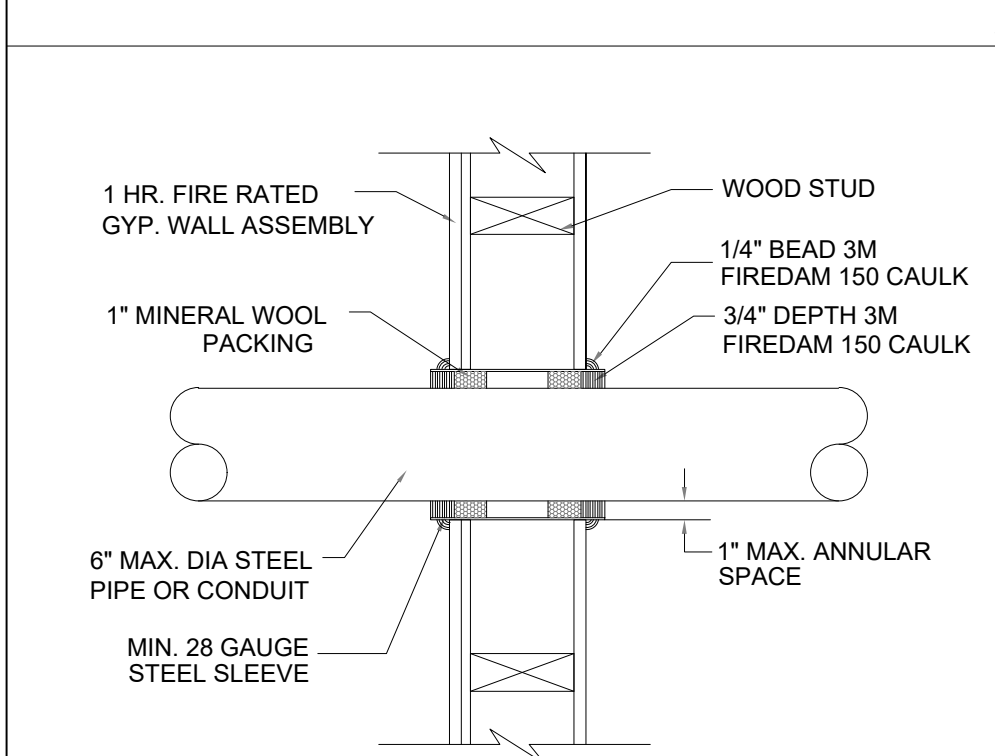


PENETRATION FIRESTOP FOR NOM. 6" MAX. DIA. STEEL PIPE/ COPPER PIPE/ CONDUIT THROUGH A GYPSUM WALLBOARD ASSEMBLY - 1 HR. RATED U.L. LISTING - W-L-1291

SCALE: NTS

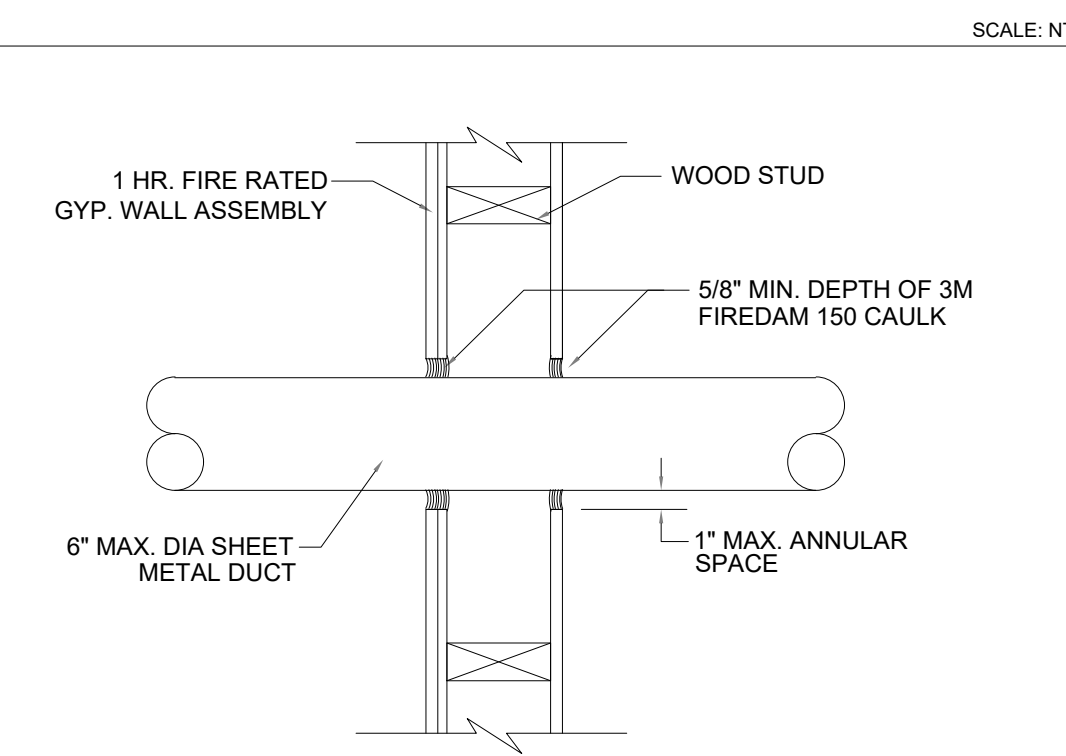

PENETRATION FIRESTOP FOR NOM. 6" MAX. DIA. RIGID SHEET METAL AIR INTAKE / EXHAUST DUCT THROUGH A GYPSUM WALLBOARD ASSEMBLY - 1 HR. RATED U.L. LISTING - W-L-1167

SCALE: NTS

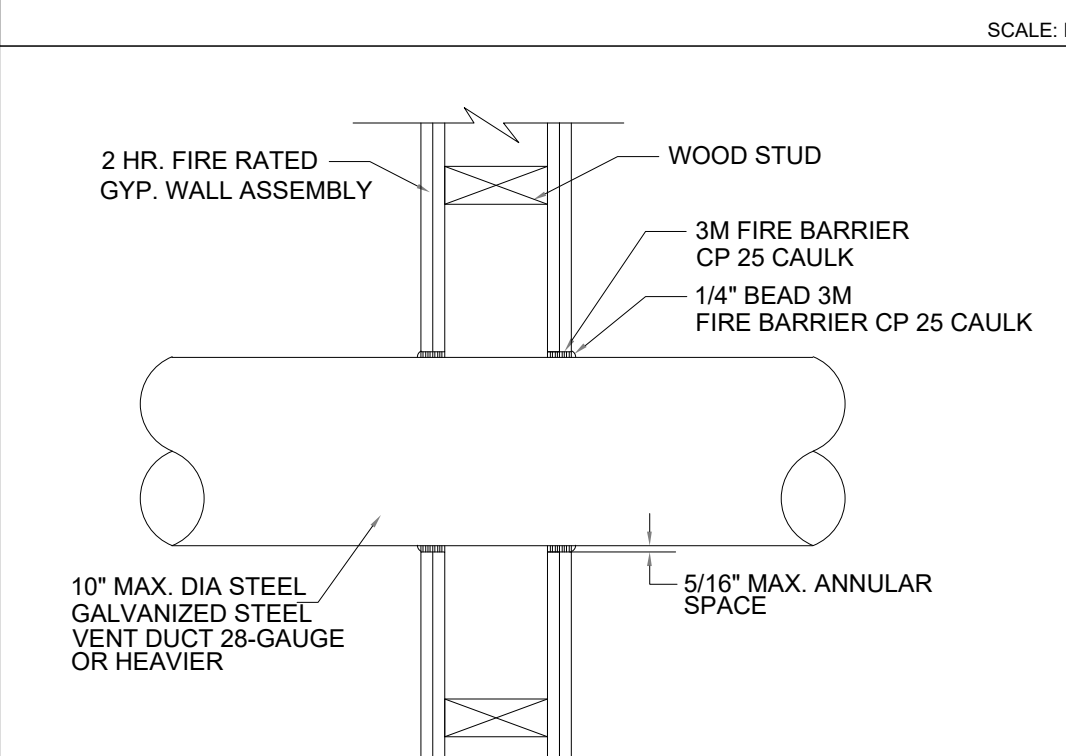

PENETRATION FIRESTOP FOR 10" MAX. DIA. STEEL VENT DUCT THROUGH A GYPSUM WALLBOARD ASSEMBLY - 2 HR. RATED U.L. LISTING - NO. 147

SCALE: NTS

WALL ASSEMBLY - CONSTRUCTED IN THE MANNER SPECIFIED IN THE U400 SERIES DESIGNS AS SHOWN IN THE UL FIRE RESISTANCE DIRECTORY.
METALLIC OUTLET BOX - MAX 4-11/16" X 4-11/16" STEEL OUTLET BOX INSTALLED IN ACCORDANCE WITH NFPA 70 REGULATIONS. THE BOX CAN BE THE SAME STUD CAVITY, PROVIDED THEY ARE NOT INSTALLED BACK-TO-BACK.
NELSON FSP PUTTY PADS SHALL BE APPLIED 1/8" THICK OR 1/4" THICK PADS TO COVER THE OUTLET BOX COMPLETELY WITHIN THE STUD CAVITY. MOLD THE PAD SO THAT NO GAPS ARE PRESENT BETWEEN THE PAD AND THE GYPSUM WALL.
TESTED IN ACCORDANCE WITH: ASTM E-119 ANSI/UL 263

DRAWING APPROVAL PROCESS:
DESIGN: RVV
DRAW: JGR
CHECKED: RVV
APPROVED: RVV
DESIGN PROFESSIONAL: RUDY V. VAZQUEZ, PE
(NY) LIC.# 083403-1
(NJ) LIC.# 24GE04511500
(FL) LIC.# 63722
NCEES Reg. # 27048

ENGINEER HAS NOT BEEN RETAINED FOR FIELD INSPECTIONS

DESIGN PROFESSIONAL: JAI
ARCHITECT LLC
ARCHITECT / PLANNER
201-240-7484
jaiarchitects@gmail.com
JOSE A. IZQUIERDO, AIA
(NY) LIC.# 017014-1
(NJ) LIC.# 09143
(NJ) PLN.# 03385

DRAWING SHEET SCHEDULE:	
SHT#:	NAME:
G-01	LOCATION MAP, PROJECT DATA, SCOPE OF WORK AND GENERAL NOTES
G-02	PENETRATIONS THROUGH RATED ASSEMBLIES
G-03	PARTITION TYPE
G-04	FLOORS EGRESS PLAN AND NOTES
G-05	DEMOLITION PLAN AND NOTES
G-06	CONSTRUCTIONS PLAN AND NOTES
G-07	PLAN INTERIOR FINISH
G-08	DOOR ELEVATIONS, SCHEDULE AND HARDWARE SET
G-09	ELEVATION, SECTION AND DETAILS


NO CHANGES SHALL BE MADE UNLESS A WRITTEN CONSENT FOR THE DEVIATION IS APPROVED BY THE ARCHITECT OR ENGINEER

REVISION RELEASE SCHEDULE:		
REV#	DATE:	RELEASE / CHANGES:
0	11-10-25	CUSTOMER RELEASE


KEY PLAN: BLOCK 29 LOT 6

DEVIATIONS:
ALL CONDITIONS ON THIS SET OF PRINTS ARE TO BE USED EXACTLY AS PRESCRIBED. ANY DEVIATION WILL DISRUPT THE SYSTEM AND MAY CAUSE OTHER ITEMS NOT TO FUNCTION AS INTENDED OR FAIL.


DRAWING TITLE: PENETRATIONS THROUGH RATED ASSEMBLIES
PROJECT: INTERIOR RENOVATION
SITE: 213 MAPLE ST, WEEHAWKEN, NEW JERSEY
OWNER: ZHANG, CHI & JIE, YANG
PROJECT: PR25-0096
SIZE: D
SCALE: AS NOTED
DRAWING: DC25-0127
SHEET: G-02

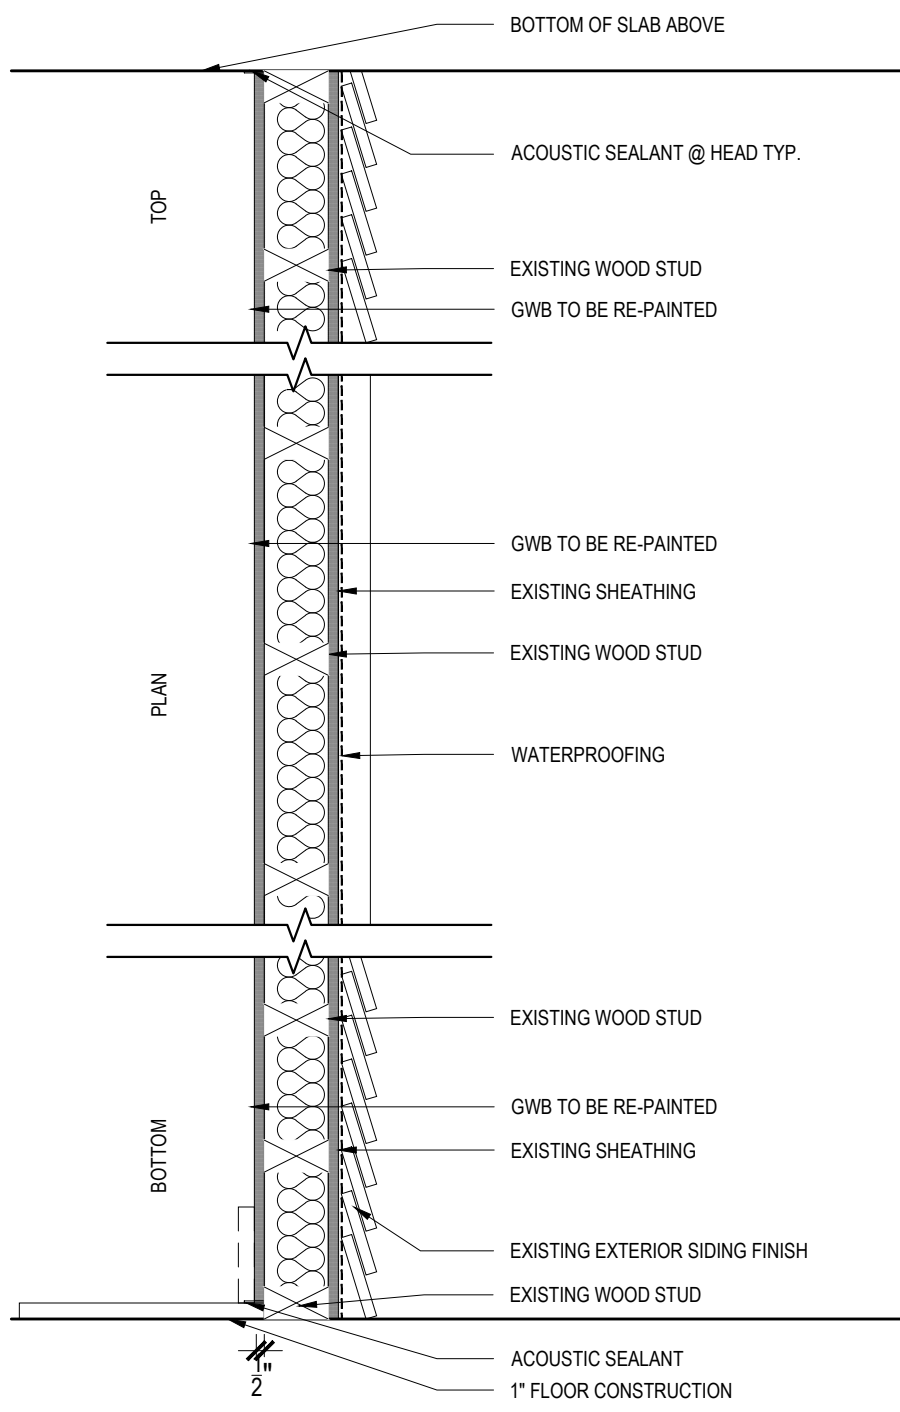


EXISTING EXTERIOR WALL
 1A EXISTING EXTERIOR WALL
 KEEP EXTERIOR UNTOUCHED IF POSSIBLE
 KEEP EXTERIOR SIDING FINISH, REPAIR AS NEEDED
 KEEP EXTERIOR SHEATHING, REPAIR AS NEEDED
 KEEP WOOD FRAME AS IT IS, REPAIR AS NEEDED

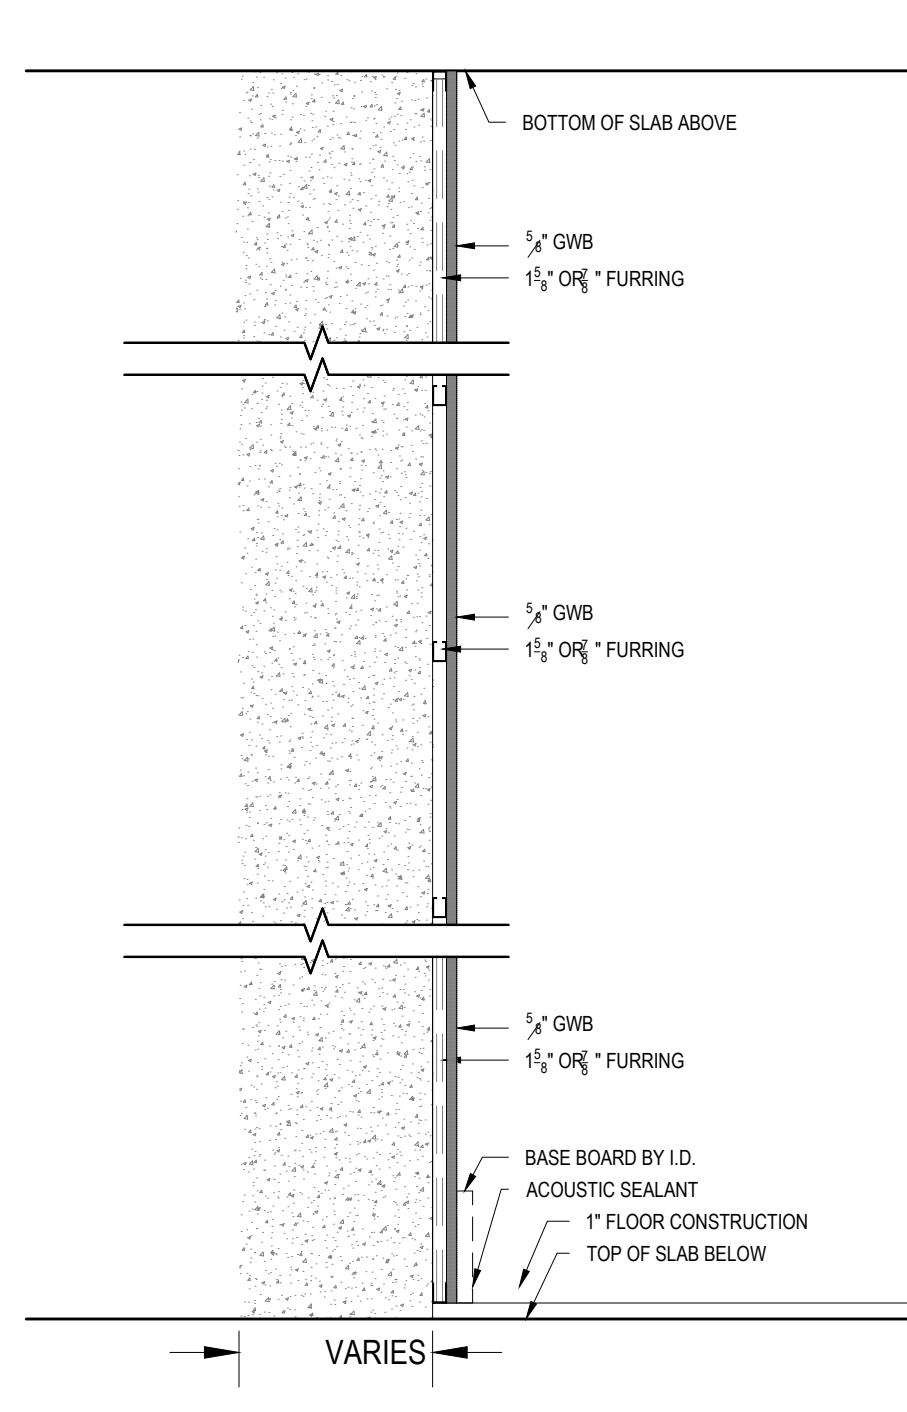


INTERIOR FURRING WALL
 1A 0HR FIRE-RTD CONSTRUCTION
 5/8\"/>

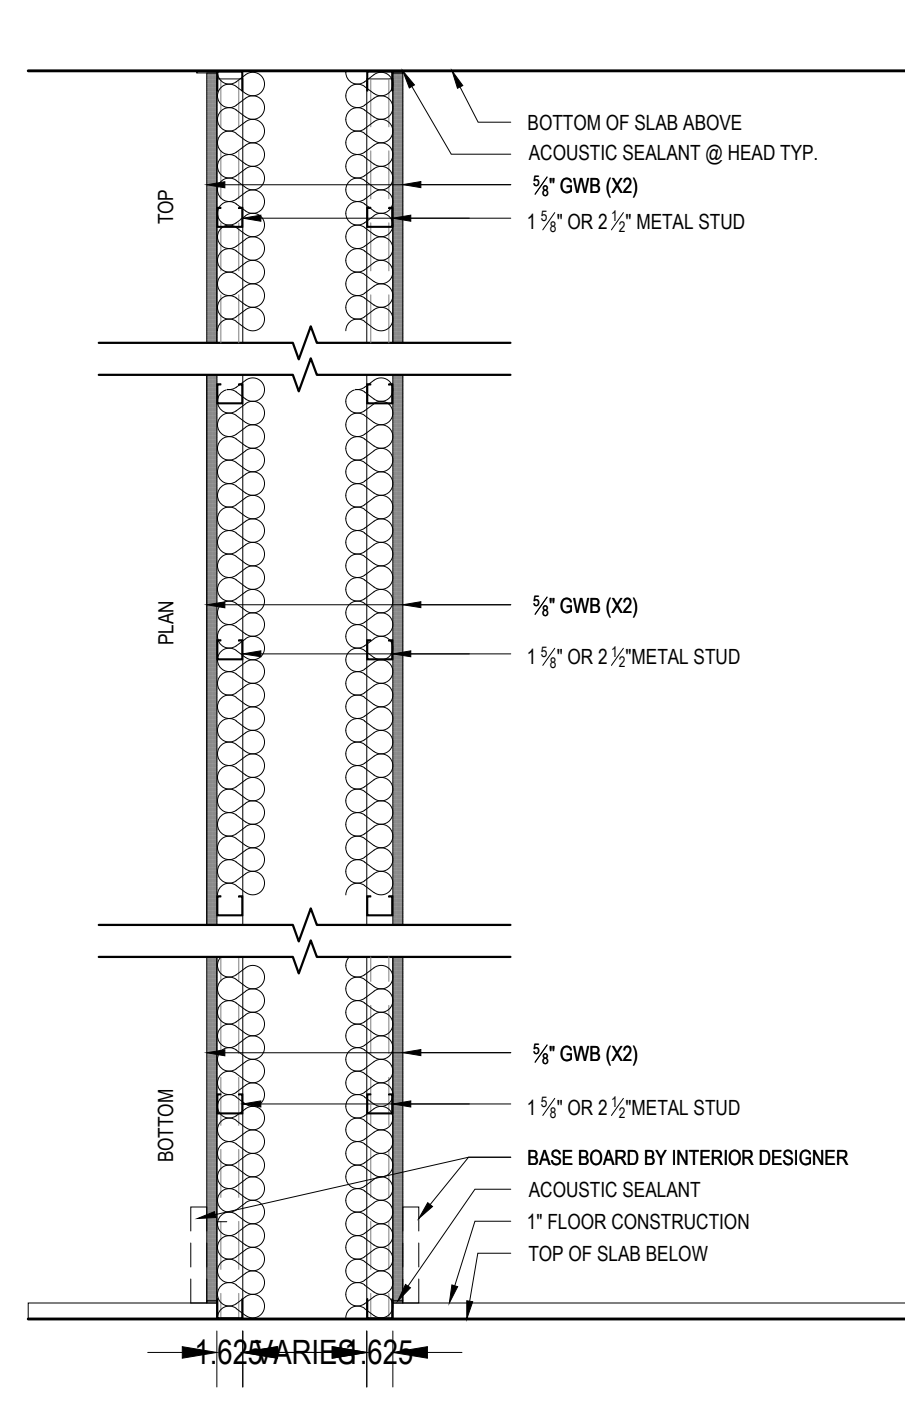


INTERIOR CHASE WALL
 1A UL 1410 - 1HR FIRE-RTD CONSTRUCTION
 5/8\"/>

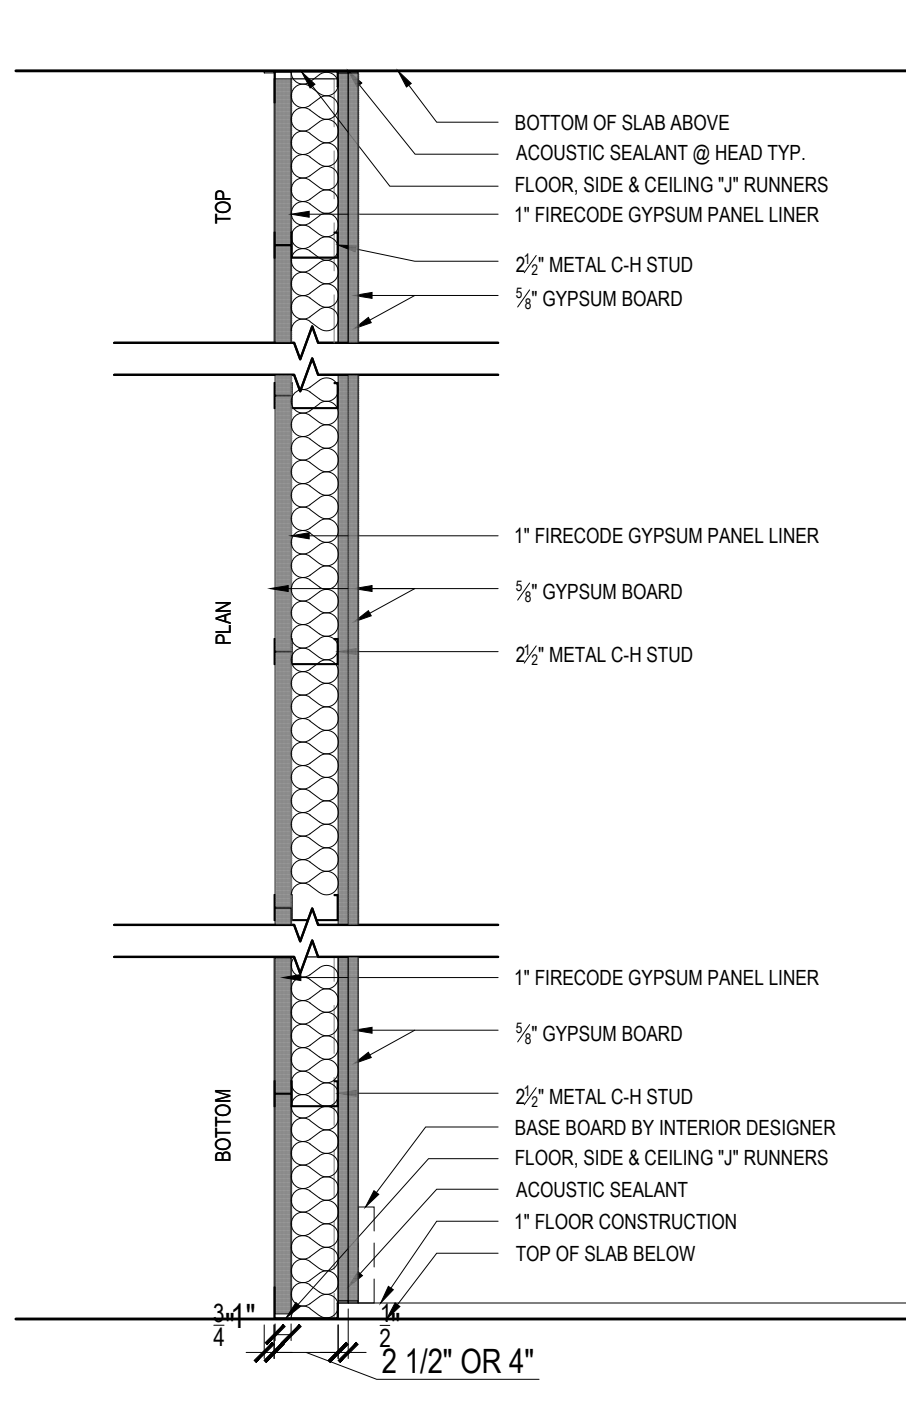

INTERIOR SHAFT WALL
 1A UL 415 SYSTEM B- 1HR FIRE-RTD CONSTRUCTION
 1\"/>

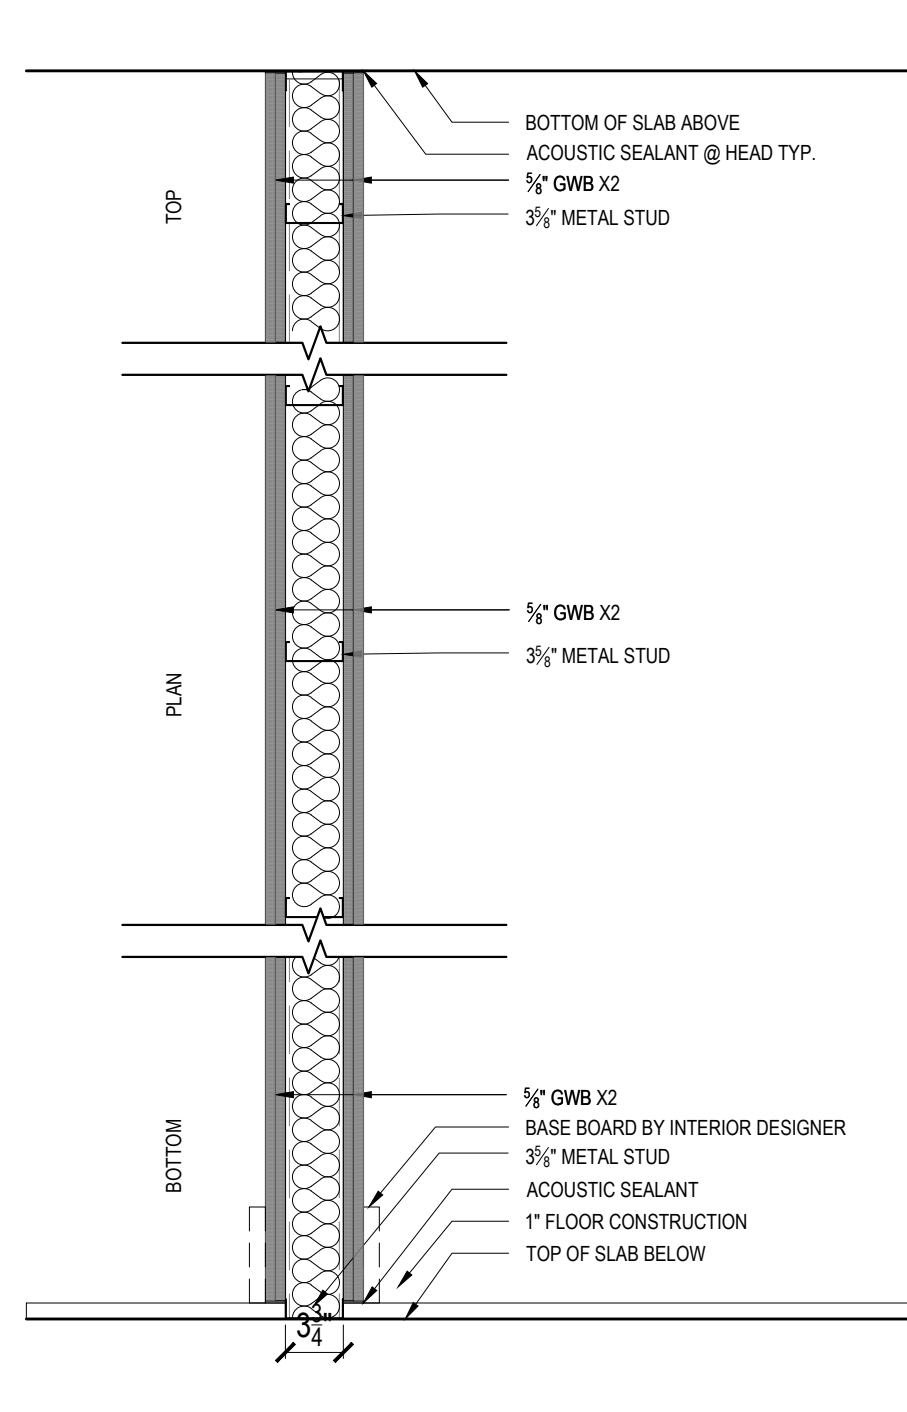


INTERIOR DEMISING WALL
 1A UL 1419 - 2HR FIRE-RTD CONSTRUCTION
 2 LAYERS 5/8\"/>

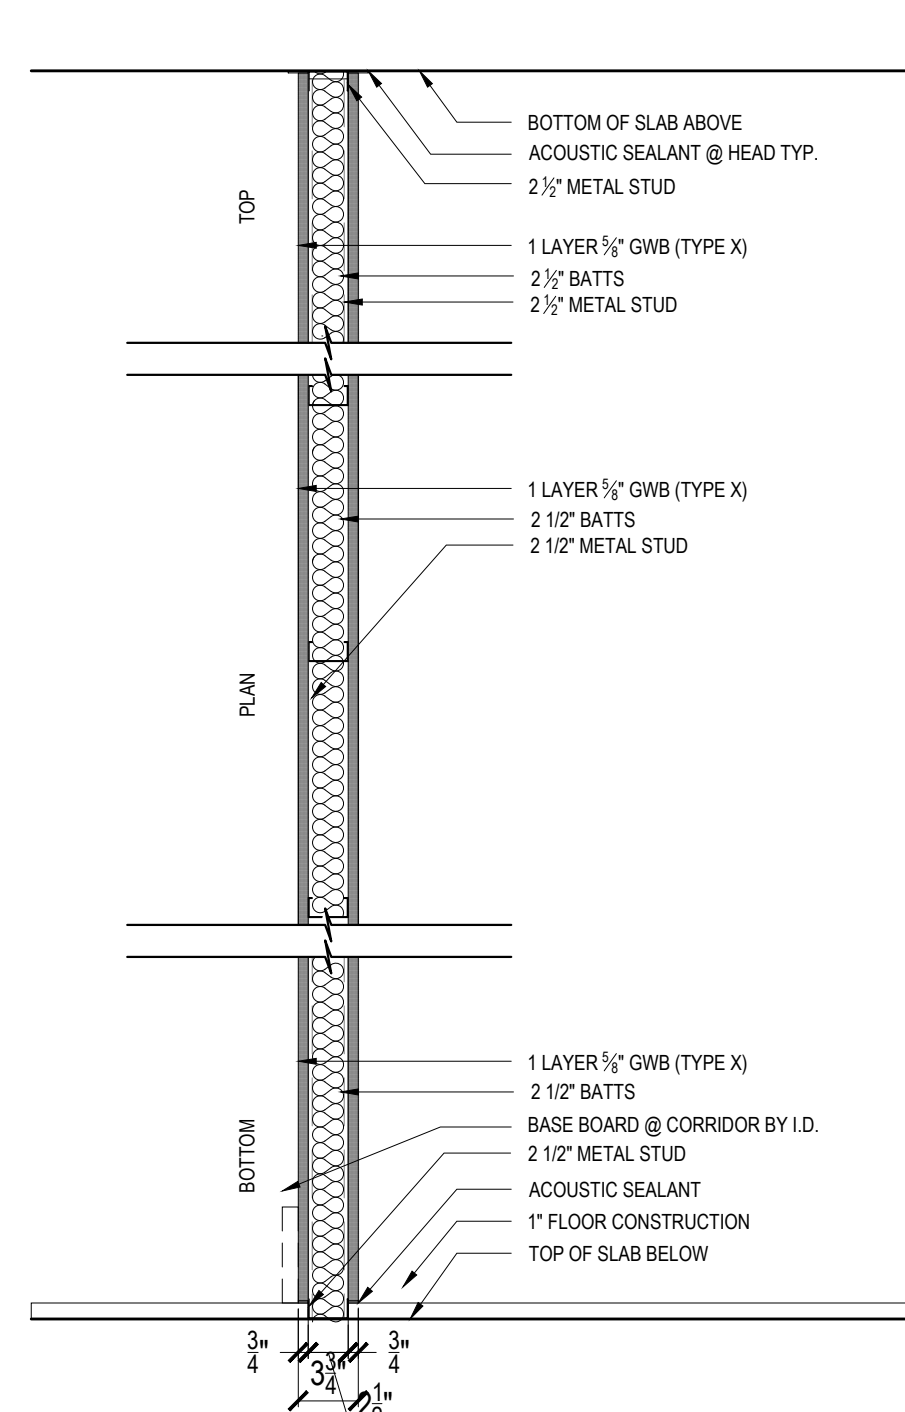


INTERIOR PARTITION WALL
 1A 0HR FIRE-RTD CONSTRUCTION
 1 LAYERS 5/8\"/>

01 WALL SCHEDULE

RTS

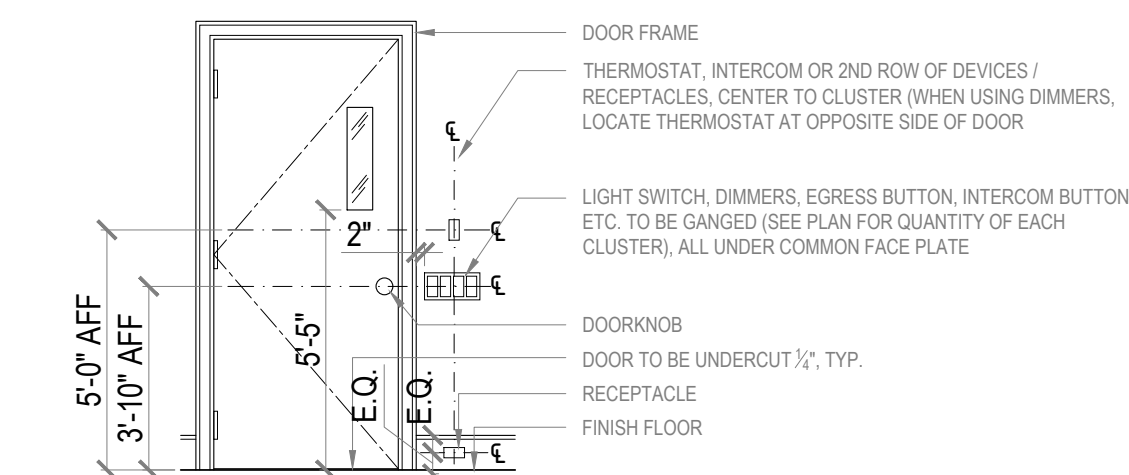

TYPICAL MOUNTING HEIGHTS / LOCATION FOR LIGHT SWITCHES, DIMMERS, EGRESS BUTTONS, THERMOSTATS ETC, UNLESS OTHERWISE NOTED
 NOTES:
 ALL DOORS THROUGH THE BUILDING SHALL BE PROVIDED WITH DISABLED PERSON COMPLIANT DOOR HARDWARE, AND DOOR SADDLES

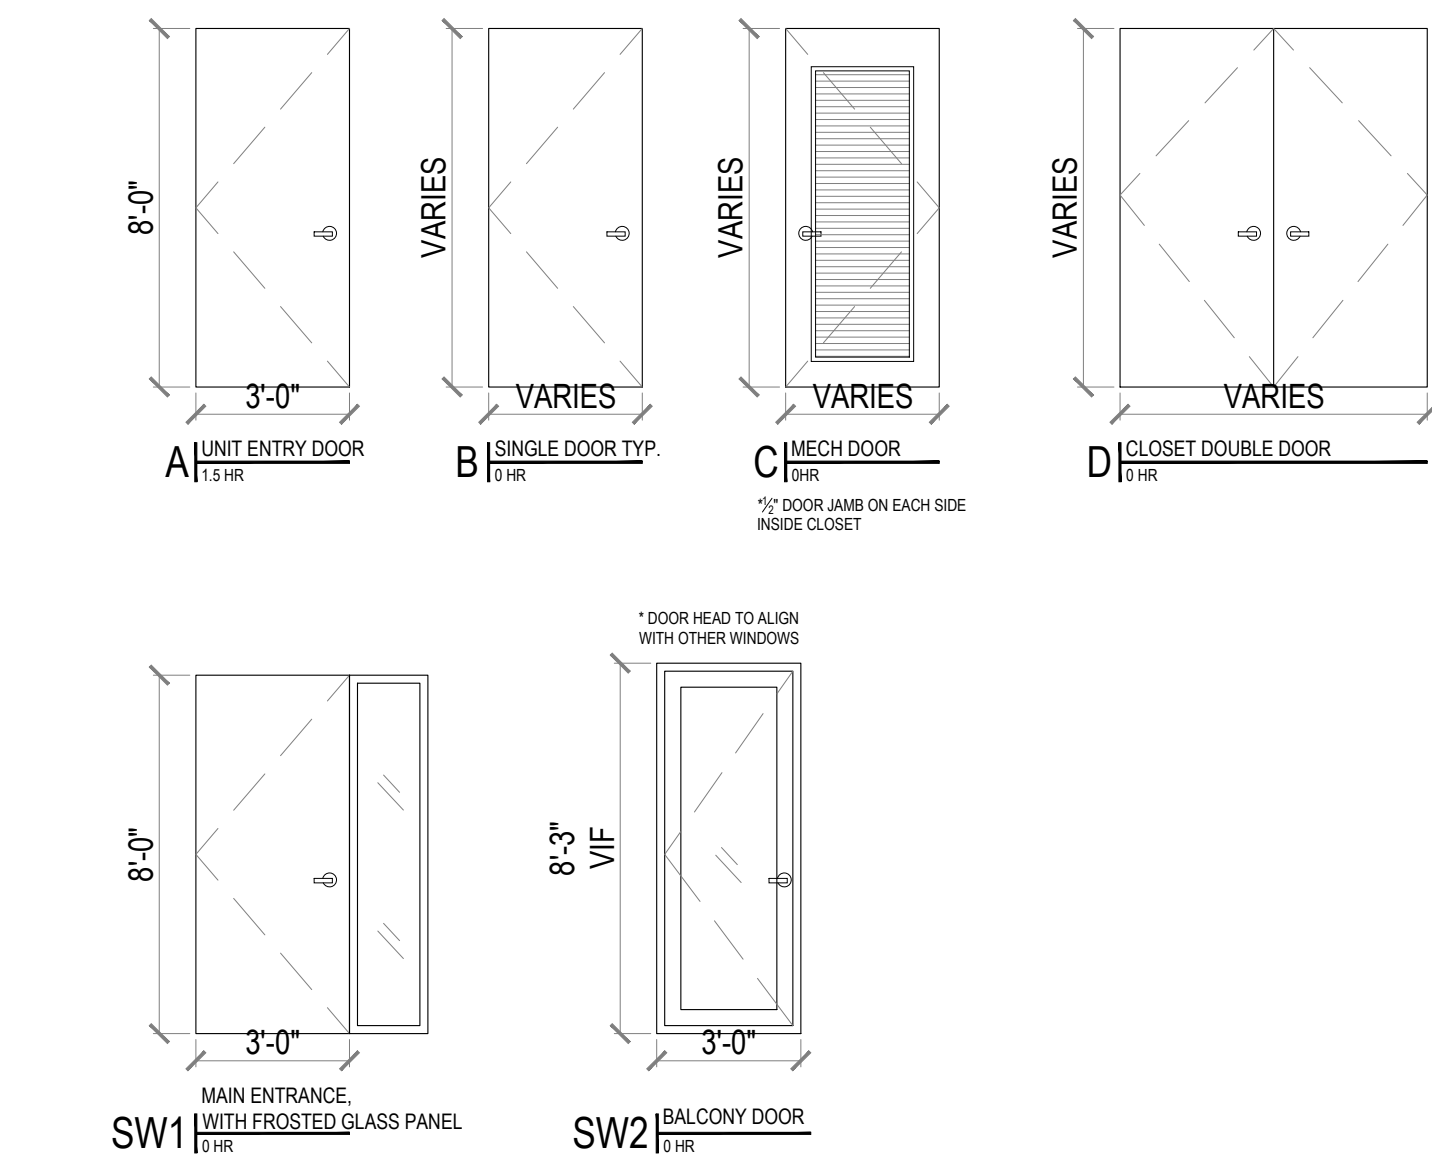

02 DOOR SCHEDULE

RTS

DOOR SCHEDULE - CELLAR										
TAG	ROOM NAME	DOOR				MATERIAL	DOOR TYPE	FIRE RATING	HARDWARE SET	REMARKS
		SIZE								
		WIDTH	HEIGHT	THK	JAMB					
CA	BEDROOM	3'-0"	6'-3"	1 3/4"	7 1/2"	WOOD	B	0hr	2	
CB	BATHROOM	3'-0"	6'-8"	1 3/4"	3 3/2"	WOOD	B	0hr	3	
CC	BEDROOM	3'-0"	6'-8"	1 3/4"	3 3/2"	WOOD	B	0hr	2	
CD	WALK-IN CLOSET	3'-0"	6'-8"	1 3/4"	3 3/2"	WOOD	B	0hr	4	
CE	DOUBLE DOOR CLOSET	5'-0"	6'-8"	1 3/4"	3 3/2"	WOOD	D	0hr	5	
CF	MEP CLOSET	2'-0"	6'-8"	1 3/4"	3 3/2"	WOOD	C	0hr	4	
CG	GAS METER CLOSET	3'-0"	6'-8"	1 3/4"	3 3/2"	WOOD	B	0hr	4	

DOOR SCHEDULE - 1ST FLOOR										
TAG	ROOM NAME	DOOR						FIRE RATING	HARDWARE SET	REMARKS
		SIZE				MATERIAL	DOOR TYPE			
		WIDTH	HEIGHT	THK	JAMB					
SW1	BLDG MAIN ENTRANCE	4'-10"	8'-0"	1 3/4"	-	EXTERIOR DOOR WITH SIDE GLAZING PANEL	SW1	0hr	-	INSULATED DOOR, U<0.36, AIR INFILTRATION = 0.1, DOOR CLOSER
1A	UNIT ENTRY DOOR	3'-0"	7'-0"	1 3/4"	6 1/2"	WOOD	A	0.75hr	1	DOOR CLOSER
1B	BEDROOM	3'-0"	7'-0"	1 3/4"	4 1/2"	WOOD	B	0hr	2	
1C	MASTER BEDROOM	3'-0"	7'-0"	1 3/4"	3 3/4"	WOOD	B	0hr	2	
1D	BATHROOM	3'-0"	7'-0"	1 3/4"	3 3/4"	WOOD	B	0hr	3	
1E	CLOSET	3'-0"	7'-0"	1 3/4"	3 3/4"	WOOD	B	0hr	4	

DOOR SCHEDULE - 2ND FLOOR										
TAG	ROOM NAME	DOOR				MATERIAL	DOOR TYPE	FIRE RATING	HARDWARE SET	REMARKS
		SIZE								
		WIDTH	HEIGHT	THK	JAMB					
2A	UNIT ENTRY DOOR	3'-0"	7'-0"	1 3⁄4"	6 1⁄2"	WOOD	A	0.75hr	1	DOOR CLOSER
2B	BEDROOM	3'-0"	7'-0"	1 3⁄4"	4 3⁄4"	WOOD	B	0hr	2	
2C	BEDROOM	3'-0"	7'-0"	1 3⁄4"	3 3⁄4"	WOOD	B	0hr	2	
2D	BATHROOM	3'-0"	7'-0"	1 3⁄4"	3 3⁄4"	WOOD	B	0hr	3	
2E	BATHROOM	3'-0"	7'-0"	1 3⁄4"	3 3⁄4"	WOOD	B	0hr	3	
2F	WID CLOSET	2'-0"	7'-0"	1 3⁄4"	3 3⁄4"	WOOD	C	0hr	4	
2G	CLOSET	2'-6"	7'-0"	1 3⁄4"	3 3⁄4"	WOOD	B	0hr	4	
2H	DOUBLE DOOR CLOSET	4'-4"	7'-0"	1 3⁄4"	3 3⁄4"	WOOD	D	0hr	5	
2I	MEP CLOSET	1'-10"	7'-0"	1 3⁄4"	4 3⁄4"	WOOD	C	0hr	4	

WINDOW SCHEDULE						
TAG	ROOM NAME	WINDOW			REMARKS	
		SIZE (VIF)				
		WIDTH	HEIGHT	JAMB		
EW1	BASEMENT REC SPACE WINDOW	2'-2"	3'-0"	VIF	VINYL	ANY TYPE IS OK. VIF
EW2	2ND FLOOR BEDROOM WINDOW	2'-8"	6'-0"	VIF	VINYL	DOUBLE HUNG. HEIGHT ADJUST WITH ADJACENT WINDOW. VIF

SET 1 - APARTMENT ENTRY DOOR
 (4) PAIR SPRING HINGE -- CAL NEWSH-140 4-1/2 X 4 1/2
 (3) SILENCERS -- CAL DSM21, FINISH RUBBER FINISH
 (1) MORTISE LOCK -- TBD
 (1) EDGE GUARD -- CAL BBDHG88, FINISH US1
 (1) FLOOR STOP -- ASSA ABLOY, DOOR STOP NO. 446
 (1) DOOR BOTTOM, AUTOMATIC, MORTISE -- PEM 441APKL36, FINISH A
 (1) DOOR VIEWER -- CAL DV90, FINISH US19
 (1) DOOR CLOSER -- ASSA ABLOY, MODEL 2701

SET 2 - BEDROOM DOOR
 (3) PAIR BUTT HINGES HAGER BB1279 4.5X4.5 (.134)
 (3) SILENCERS
 (1) SCHLAGE MATTE BLACK PASSAGE LEVER SET (MODEL: F40 G LAT 622, HOMEDOT SKU:1004655234)

SET 3 - BATHROOM DOOR
 (3) PAIR BUTT HINGES HAGER BB1279 4.5X4.5 (.134)
 (3) SILENCERS
 (1) SCHLAGE MATTE BLACK PRIVACY LEVER SET (MODEL: F40 G LAT 622, HOMEDOT SKU:1004655234)

SET 4 - CLOSET DOOR
 (3) PAIR BUTT HINGES HAGER BB1279 4.5X4.5 (.134)
 (3) SILENCERS
 (1) SCHLAGE MATTE BLACK PASSAGE LEVER SET (MODEL: F40 G LAT 622, HOMEDOT SKU:1004655234)

SET 5 - CLOSET DOUBLE DOOR
 (3) PAIR BUTT HINGES HAGER BB1279 4.5X4.5 (.134)
 (3) SILENCERS
 (1) SCHLAGE MATTE BLACK PASSAGE LEVER SET (MODEL: F40 G LAT 622, HOMEDOT SKU:1004655234)

SET 6 - MECHANICAL AND STORAGE ROOM
 (3) PAIR BUTT HINGES HAGER BB1279 4.5X4.5 (.134)
 (3) SILENCERS
 (2) SCHLAGE MATTE BLACK KEYED ENTRY LEVER SET (MODEL: F40 G LAT 622, HOMEDOT SKU:1004655234)

PROJECT 143

213 MAPLE STREET

213 MAPLE STREET, WEEHAWKEN, NEW JERSEY 07086

CONSULTANTS:

STRUCTURAL ENGINEER
 FLEX ENGINEERING GROUP LLC
 3133 CENTRAL AVE #202, UNION CITY, NJ 07087
 T: 201-974-9570
 E: flexengineer@yahoo.com

MECHANICAL ENGINEER
 FLEX ENGINEERING GROUP LLC
 3133 CENTRAL AVE #202, UNION CITY, NJ 07087
 T: 201-974-9570
 E: flexengineer@yahoo.com

GENERAL CONTRACTOR
 HOBOKEN KITCHEN & BATH
 2 14TH ST PH 32, HOBOKEN NJ, 07030
 T: 201-472-0425
 E: thestone@hobokenkitchenandbath.com

DATE DESCRIPTION

DOB STAMP AND SIGNATURE

SEAL AND SIGNATURE

CONTRACTORS SHALL ONLY UTILIZE WRITTEN DIMENSIONS. CONTRACTORS SHALL VERIFY AND BE RESPONSIBLE FOR ALL DIMENSIONS AND CONDITIONS ON THE JOB, AND OWNER MUST BE NOTIFIED OF ANY VARIATIONS FROM DIMENSIONS AND CONDITIONS SHOWN BY THESE DRAWINGS. ALL DIMENSIONS MUST BE SUBMITTED TO OWNER FOR APPROVAL, BEFORE PROCEEDING WITH ANY FABRICATION.


ALL DRAWINGS, SCHEDULES, SPECIFICATIONS ETC. DISTRIBUTED TO CONTRACTORS, BIDDERS, GOVERNMENTAL AGENCIES ETC., ARE NOT FOR GENERAL USE OR PUBLICATION BY OTHERS. ALL RIGHTS RESERVED. NONE OF THE IDEAS, ORIGINAL ARRANGEMENTS OR PLANS IN THIS DRAWING SHALL BE USED BY OR DISCLOSED TO ANY PERSONS, FIRM OR CORPORATION FOR ANY PURPOSE WITHOUT THE CURRENT AND WRITTEN PERMISSION OF OWNER.

DRAWING TITLE:


SCHEDULES

FOR CONSTRUCTION


A-010.00

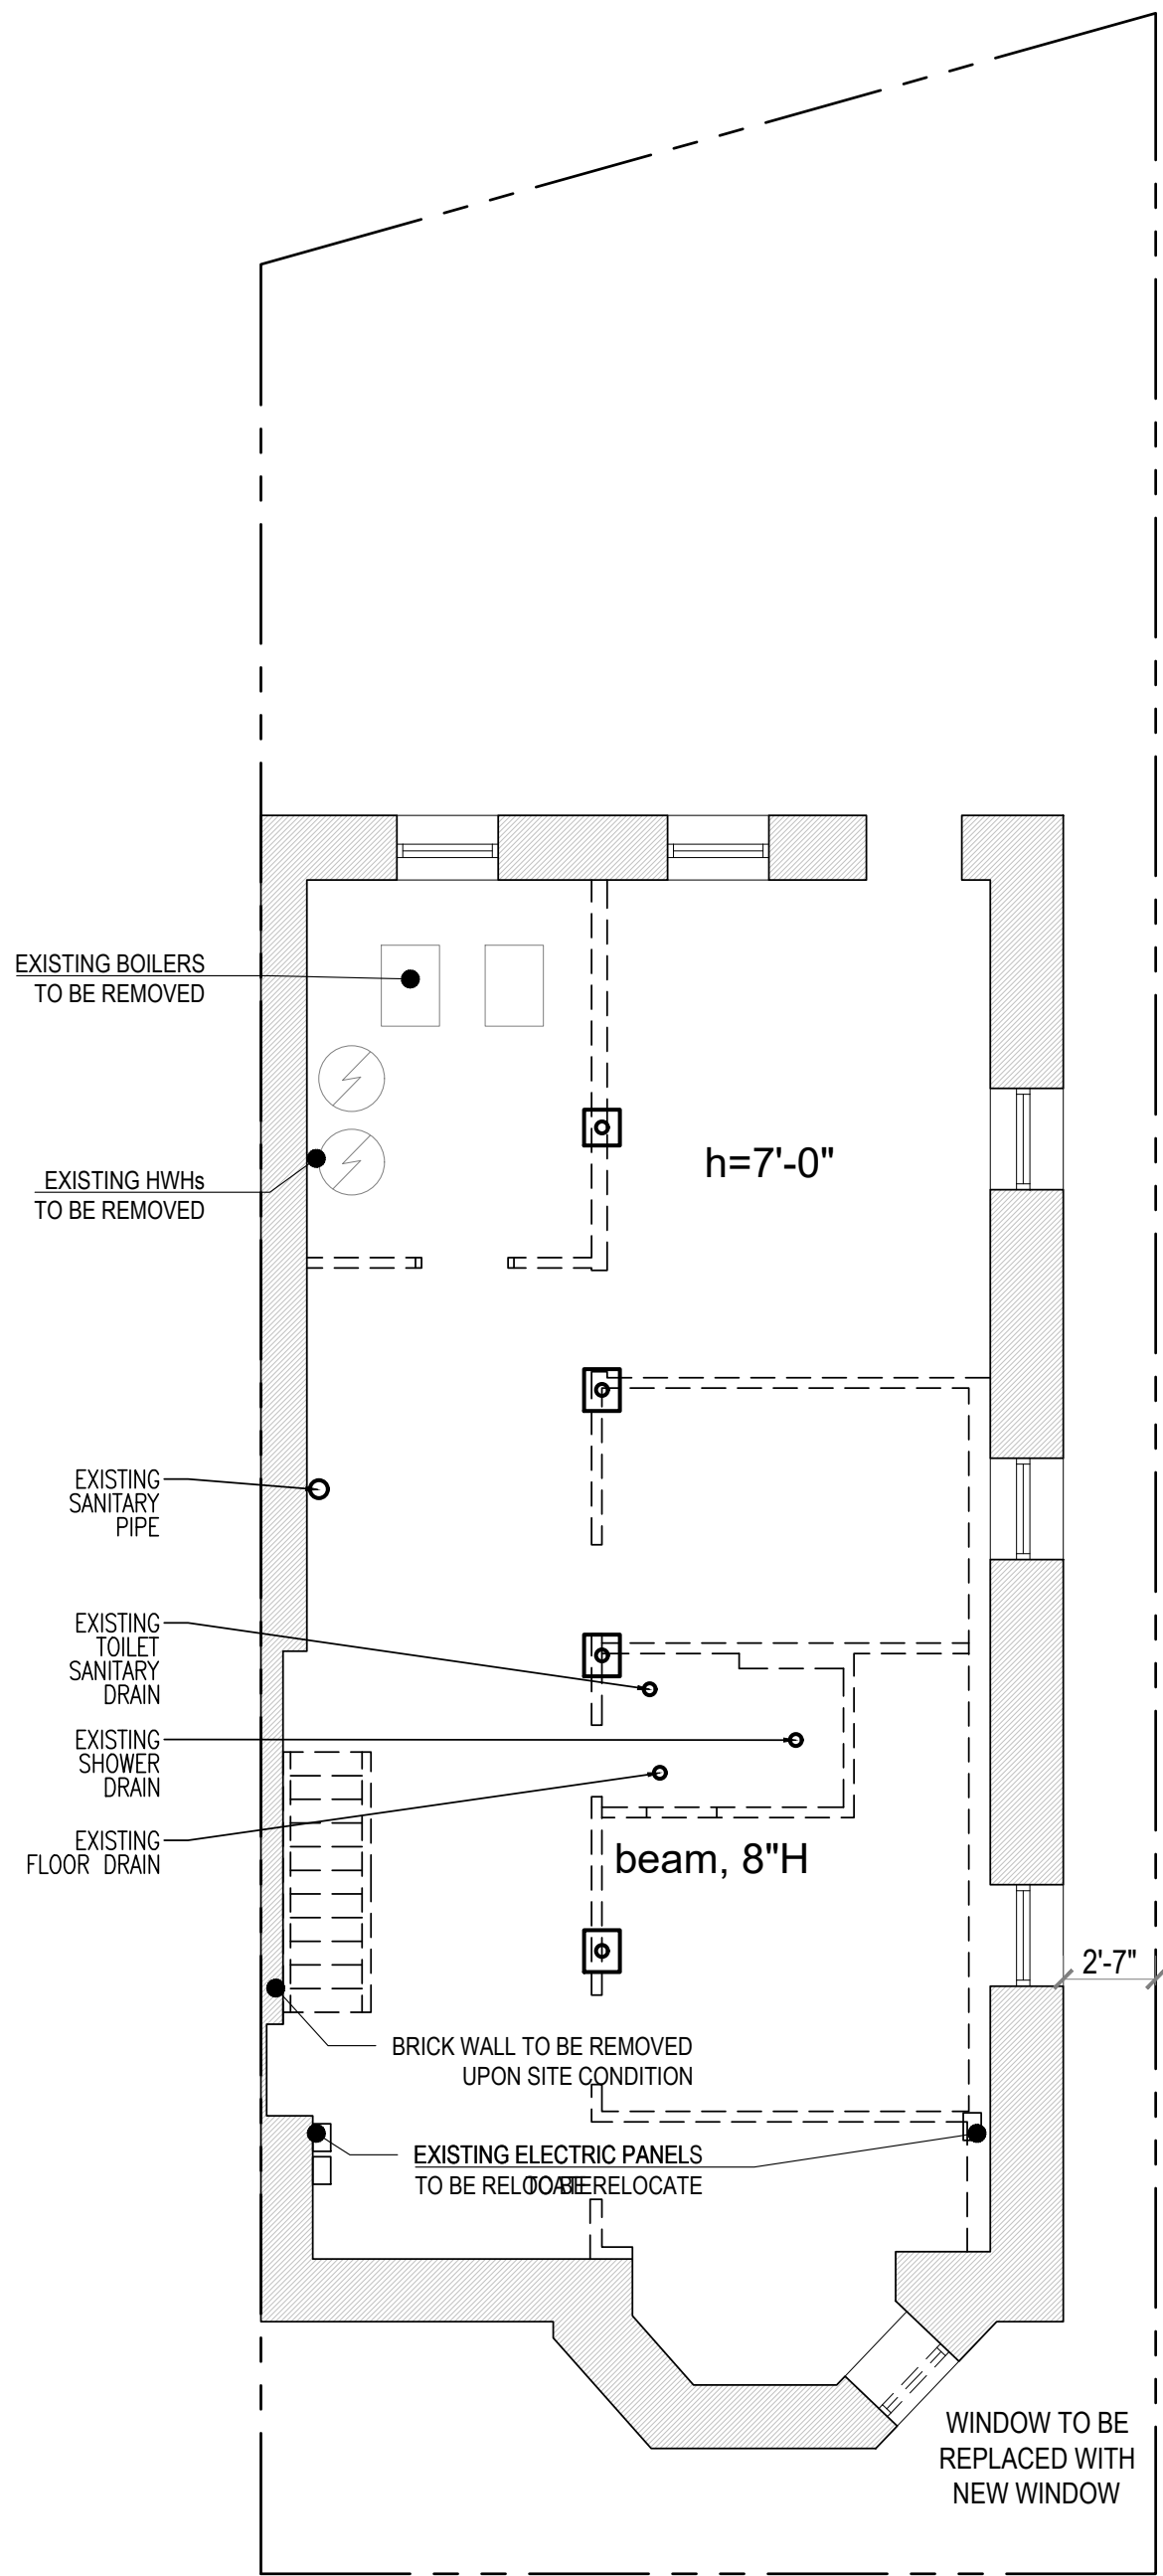


01 BASEMENT DEMO PLAN
3/16" = 1'

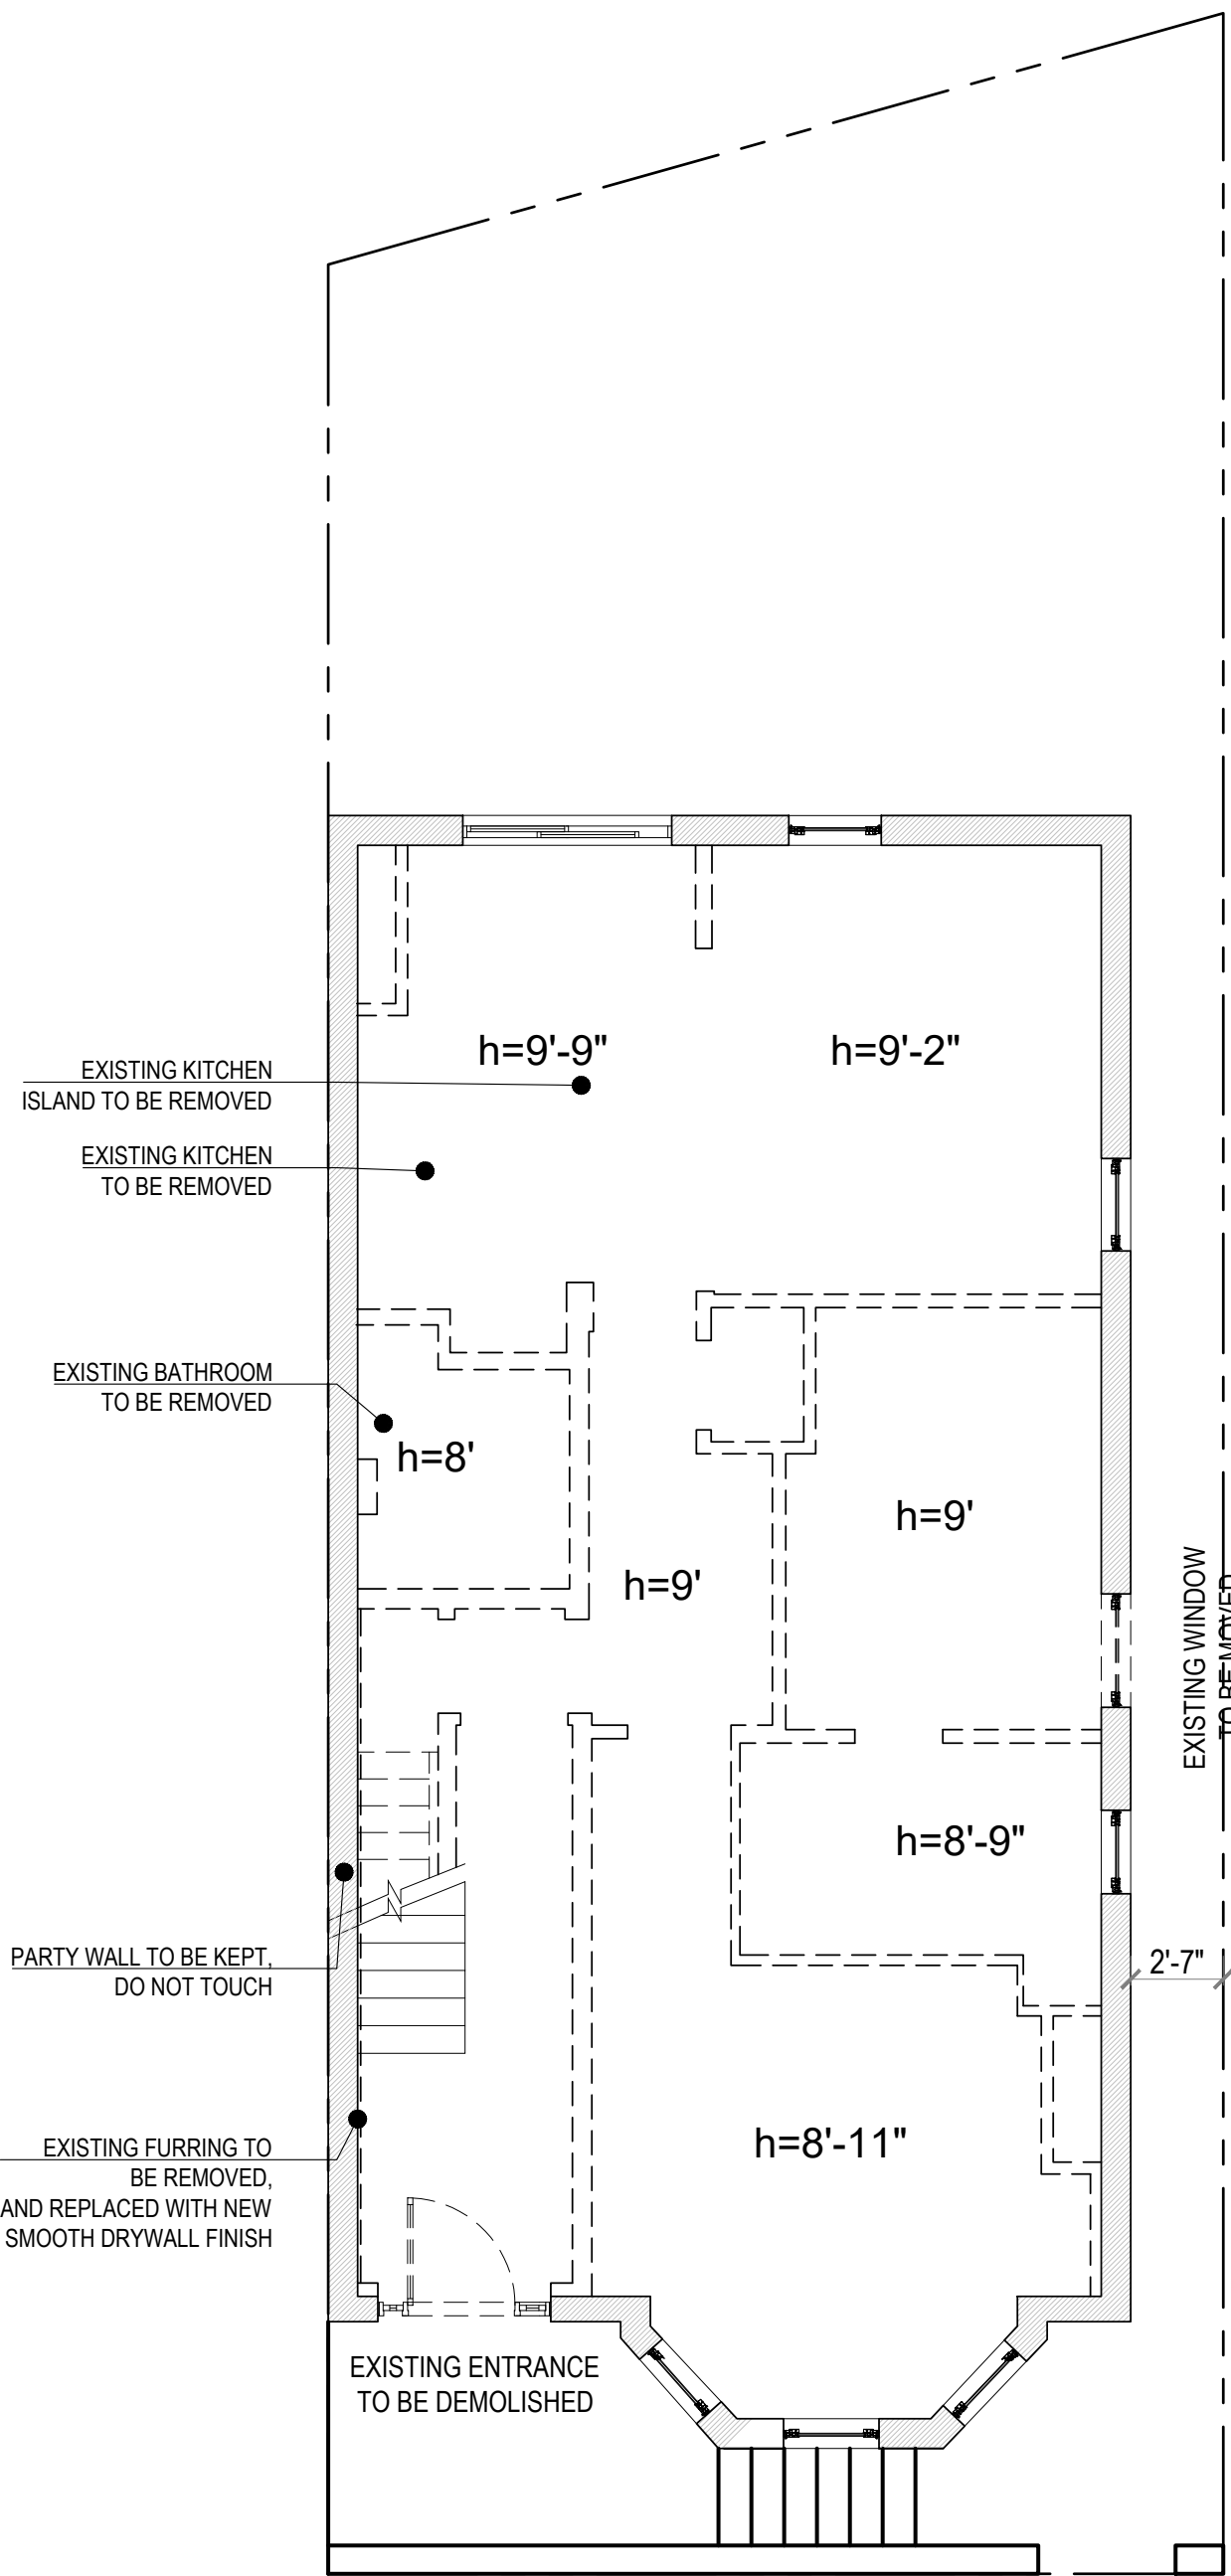

02 1ST FLOOR DEMO PLAN
3/16" = 1'

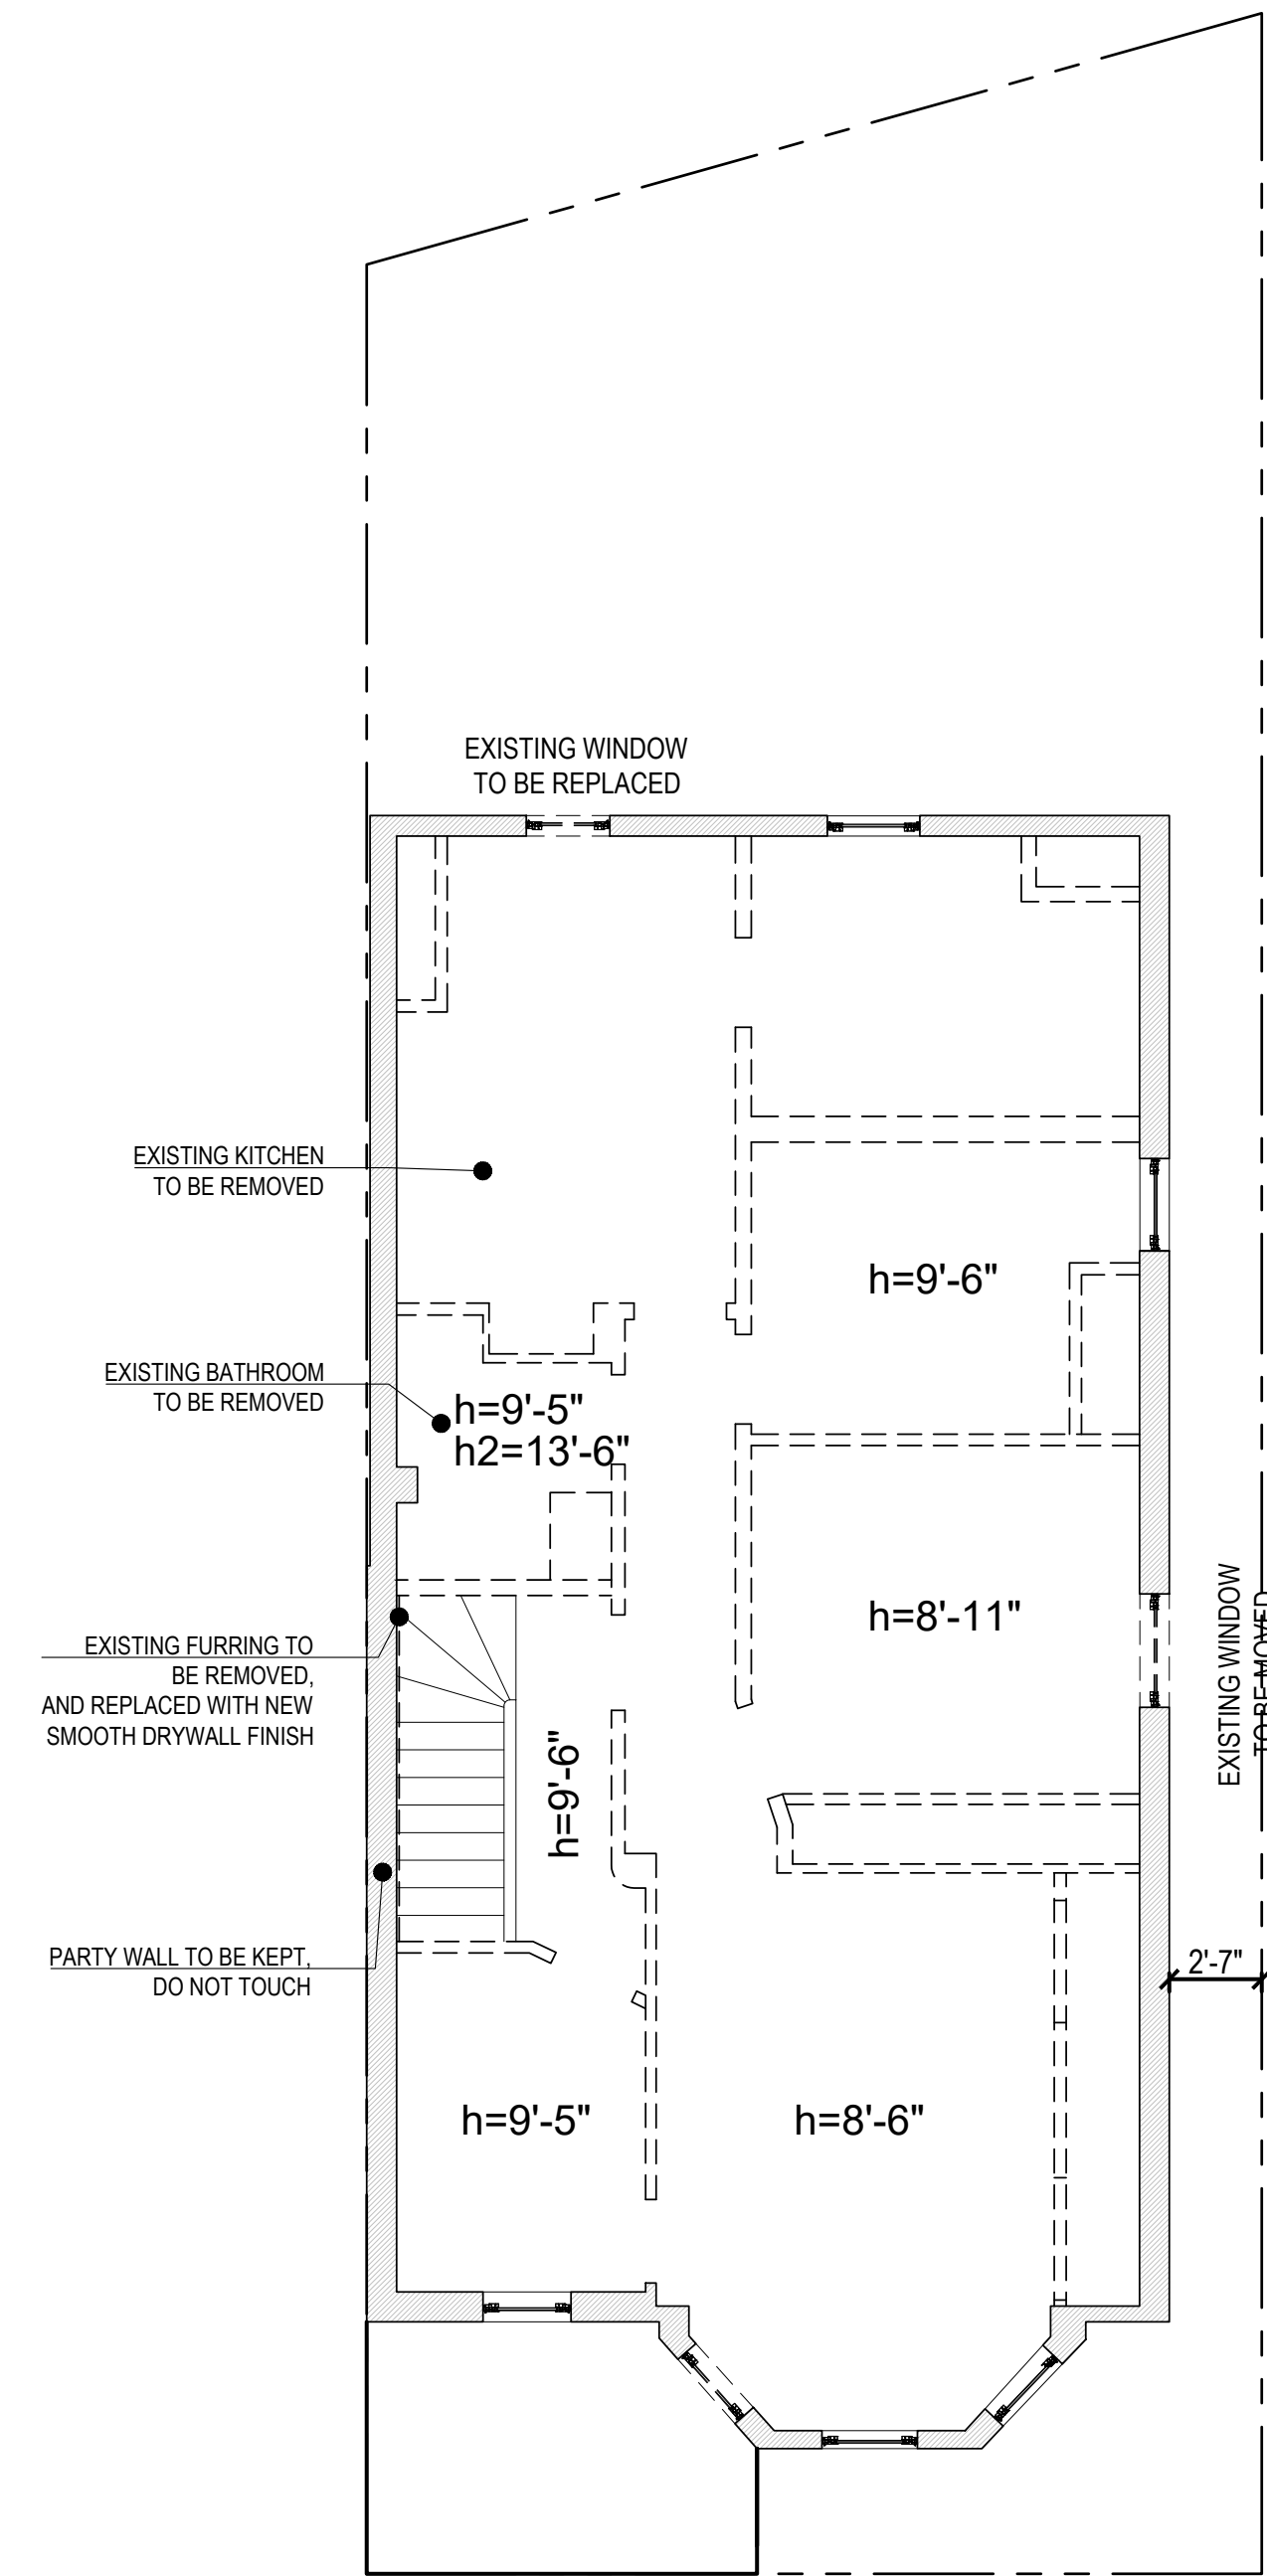

03 2ND FLOOR DEMO PLAN
3/16" = 1'

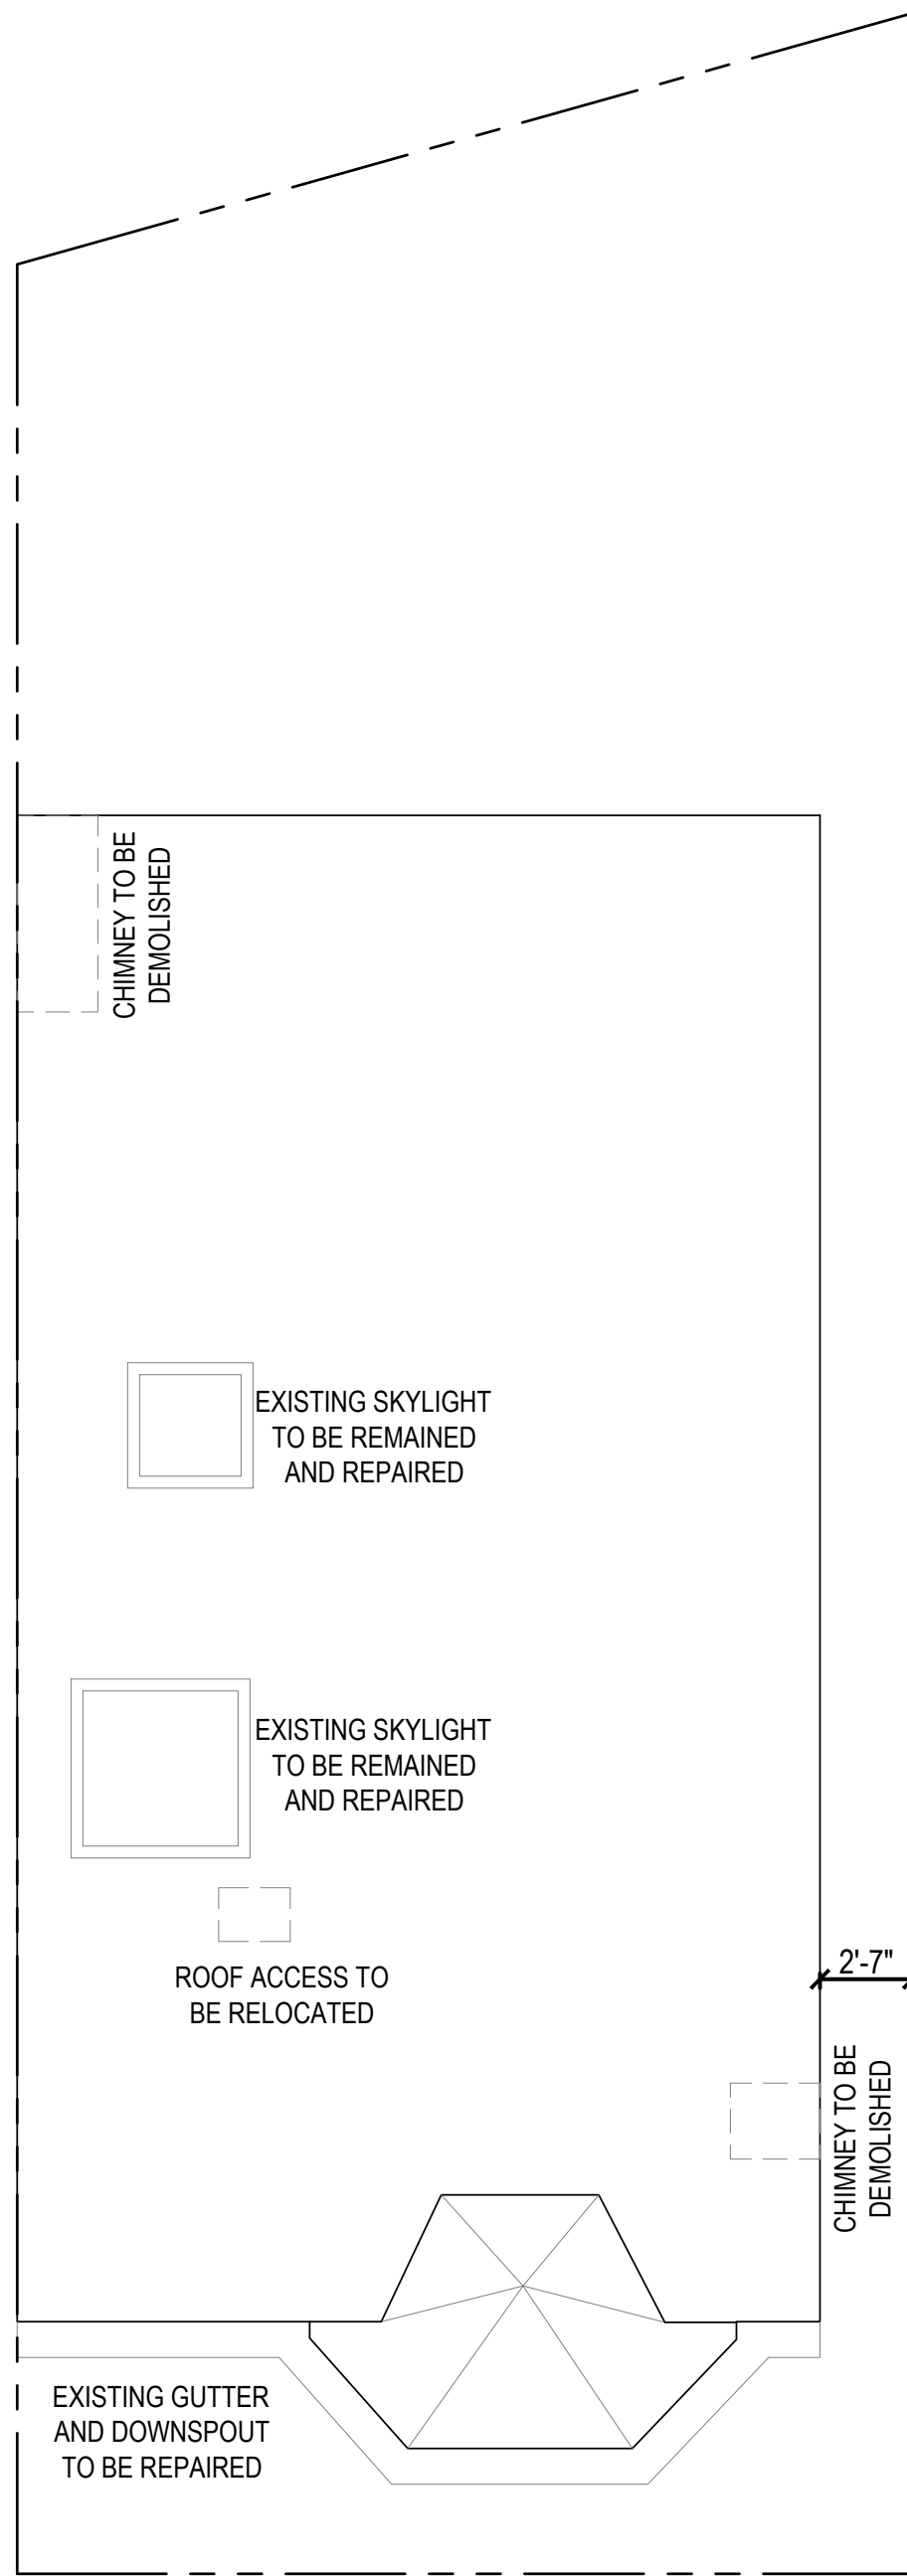

04 ROOF DEMO PLAN
3/16" = 1'

DEMOLITION SEQUENCE:

1. ALL SERVICES AFFECTED BY THE PROPOSED WORK SHALL BE DISCONNECTED AS NECESSARY PRIOR TO THE BEGINNING OF ANY REMOVAL AND/OR DEMOLITION FOR ANY WORK.
2. COVER AND REMOVE ALL PLUMBING FITTINGS INDICATED ON THE PLAN THROUGHOUT THE ENTIRE FLOOR.
3. REMOVE NON-STRUCTURAL PARTITIONS AND DOORS AS INDICATED ON DRAWING.
4. REMOVE EXISTING WINDOWS ON 2ND FLOOR AND ATTIC AS INDICATED ON PLAN.

NOTE: ONLY HAND HELD DEVICES ALLOWED FOR DEMOLITION.

TENANT PROTECTION PLAN

1. EGRESS: CONSTRUCTION OPERATION WILL NOT BLOCK HALLWAYS OR MEANS OF EGRESS FOR THE TENANTS OF THE BUILDING.
2. FIRE SAFETY: ALL EGRESS SHALL BE CLEAR ALL THE TIMES FOR FIRE FIGHTER RESPOND AND TENANT EXIT.
3. HEALTH REQUIREMENT: CONSTRUCTION WORK WILL BE CONFINED TO THE ITEMS AS INDICATED IN THE DRAWING, AND WILL NOT CREATE DUST, DIRT OR OTHER SUCH INCONVENIENCE TO THE OTHER TENANTS WITHIN THE BUILDING. ALL DUST AND DEBRIS SHALL BE CLEAN UP AT THE END OF EVERY SHIFT.
4. HOUSING STANDARDS: CONSTRUCTION OPERATION WILL NOT INVOLVE INTERRUPTION OF HEATING, WATER, OR OTHER ELECTRICAL SERVICES TO OTHER TENANTS OF THE BUILDING.
5. LEAD AND ASBESTOS: THIS IS "NOT AN LEAD AND ASBESTOS PROJECT".
6. STRUCTURAL INTEGRITY: IF ANY DISCREPANCY OR STRUCTURAL INTEGRITY QUESTIONABLE MUST CALL ENGINEER AND STOP ALL WORK UNLESS INSTRUCTED.
7. NOISE COMPLIANCE: CONSTRUCTION OPERATION WILL BE CONFINED TO NORMAL WORKING HOURS: 9:00 AM TO 4:00 PM MONDAYS THROUGH FRIDAYS, EXCEPT LEGAL HOLIDAYS.

GENERAL DEMOLITION NOTES:

1. DEMOLITION WORK SHALL COMPLY WITH ANSI A 10.6 SAFETY REQUIREMENTS FOR DEMOLITION.
2. THE CONTRACTOR SHALL VISIT THE SITE AND CAREFULLY EXAMINE THE WORK TO BE DONE SO AS THE BECOME FAMILIAR WITH THE EXIST. CONDITION AND NATURE OF THE SCOPE OF WORK. HE/SHE SHALL REPORT ANY POTENTIAL DIFFICULTIES TO THE OWNER AND ARCHITECT AS SOON AS POSSIBLE.
3. THE DEMOLITION DRAWINGS MAY NOT SHOW ALL REMOVALS REQUIRED. THE CONTRACT INCLUDES ALL WORK NECESSARY TO PRODUCE THE FINAL ARRANGEMENT AS SHOWN ON THE ARCHITECTURAL DRAWING.
4. PERFORM ALL CUTTING AND ROUGH PATCHING OF EXISTING WALLS PER PLANS. ALL CUTTING OF EXISTING MATERIALS SHALL BE HELD TO THE ABSOLUTE MINIMUM AS REQUIRED TO PROPERLY PERFORM THE WORK. ALL WORK SHALL BE CAREFULLY PERFORMED SO AS NOT TO DAMAGE OR ENDANGER EXISTING WORK TO REMAIN AS NEW WORK. THE GENERAL CONTRACTOR SHALL ASSUME COMPLETE RESPONSIBILITY AND LIABILITY FOR SAFETY AND STRUCTURAL INTEGRITY OF THE WORK TO REMAIN DURING DEMOLITION WORK.
5. REMOVE ALL EXISTING INTERIOR AND EXTERIOR DOORS, TRIM, HARDWARE AND BLOCKING AS INDICATED ON DRAWING.
6. THE CONTRACTOR SHALL PROVIDE AND MAINTAIN TEMPORARY PROTECTION OF WORK TO REMAIN WHERE DEMOLITION, REMOVAL, AND/ OR NEW WORK IS BEING DONE.
7. ALL DEMOLITION AND REMOVAL WORK SHALL BE BROUGHT TO NATURAL STOPPING POINT. ANY MATERIAL REMOVED BY MISTAKE OR IN EXCESS OF REQUIREMENTS SHALL BE REPLACED AT THE CONTRACTOR'S EXPENSE.
8. WHERE EXISTING PARTITIONS OR OTHER WORK AREA REMOVED, PROTUBERANCE OR DEPRESSIONS IN FLOORS, CEILINGS AND WALLS SHALL BE PROPERLY FILLED AND LEVELED FLUSH WITH THE ADJACENT SURFACES.
9. DISPOSAL: ALL MATERIALS, DEBRIS AND RUBBISH RESULTING FROM THE DEMOLITION, PREMISES AS THE WORK PROGRESSES AND LEGALLY DISPOSED OF OFF THE SITE IN ACCORDANCE WITH LOCAL AND BUILDING REGULATIONS.

PROJECT 143

213 MAPLE STREET

213 MAPLE STREET, WEEHAWKEN, NEW JERSEY, 07086

CONSULTANTS:

STRUCTURAL ENGINEER
FLEX ENGINEERING GROUP LLC
3133 CENTRAL AVE #202, UNION CITY, NJ 07087
T: 201-974-9570
E: flexengineer@yahoo.com

MECHANICAL ENGINEER
FLEX ENGINEERING GROUP LLC
3133 CENTRAL AVE #202, UNION CITY, NJ 07087
T: 201-974-9570
E: flexengineer@yahoo.com

GENERAL CONTRACTOR
HOBOKEN KITCHEN & BATH
2 14TH ST PH 32, HOBOKEN NJ, 07030
T: 201-472-0425
E: theodore@hobokenkitchenandbath.com

#	DATE	DESCRIPTION
---	------	-------------

DOB STAMP AND SIGNATURE

SEAL AND SIGNATURE

CONTRACTOR SHALL ONLY UTILIZE WRITTEN DIMENSIONS. CONTRACTOR SHALL VERIFY AND BE RESPONSIBLE FOR ALL DIMENSIONS AND CONDITIONS ON THE JOB. THE OWNER MUST BE NOTIFIED OF ANY VARIATIONS FROM DIMENSIONS AND CONDITIONS SHOWN BY THESE DRAWINGS. ALL DIMENSIONS MUST BE SUBMITTED TO OWNER FOR APPROVAL BEFORE PROCEEDING WITH ANY FABRICATION.

ALL DRAWINGS, SPECIFICATIONS, ETC. DISTRIBUTED TO CONTRACTORS, BIDDERS, GOVERNMENTAL AGENCIES ETC. ARE NOT FOR GENERAL USE OR PUBLICATION BY OTHERS. ALL RIGHTS RESERVED. NONE OF THE IDEAS OR INVENTIONS OR PLANS IN THIS DRAWING SHALL BE USED BY OR DISCLOSED TO ANY PERSONS FIRM OR CORPORATION FOR ANY PURPOSE WITHOUT THE CURRENT AND WRITTEN PERMISSION OF OWNER.

DRAWING TITLE:
DEMO PLANS


FOR CONSTRUCTION

A-080.00

STRUCTURAL ENGINEER
FLEX ENGINEERING GROUP LLC
3133 CENTRAL AVE #202, UNION CITY, NJ 07087
T: 201-974-9570
E: flexengineer@yahoo.com




MECHANICAL ENGINEER
FLEX ENGINEERING GROUP LLC
3133 CENTRAL AVE #202, UNION CITY, NJ 07087
T: 201-974-9570
E: flexengineer@yahoo.com

GENERAL CONTRACTOR
HOBOKEN KITCHEN & BATH
2 14TH ST PH 32, HOBOKEN ,NJ, 07030
T: 201-472-0425
E: theodore@hobokenkitchenandbath.com

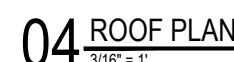

 PROPERTY LINE WALL TAG
 1HR RATED WALL  DOOR TAG
 2HR RATED WALL

A-100.00

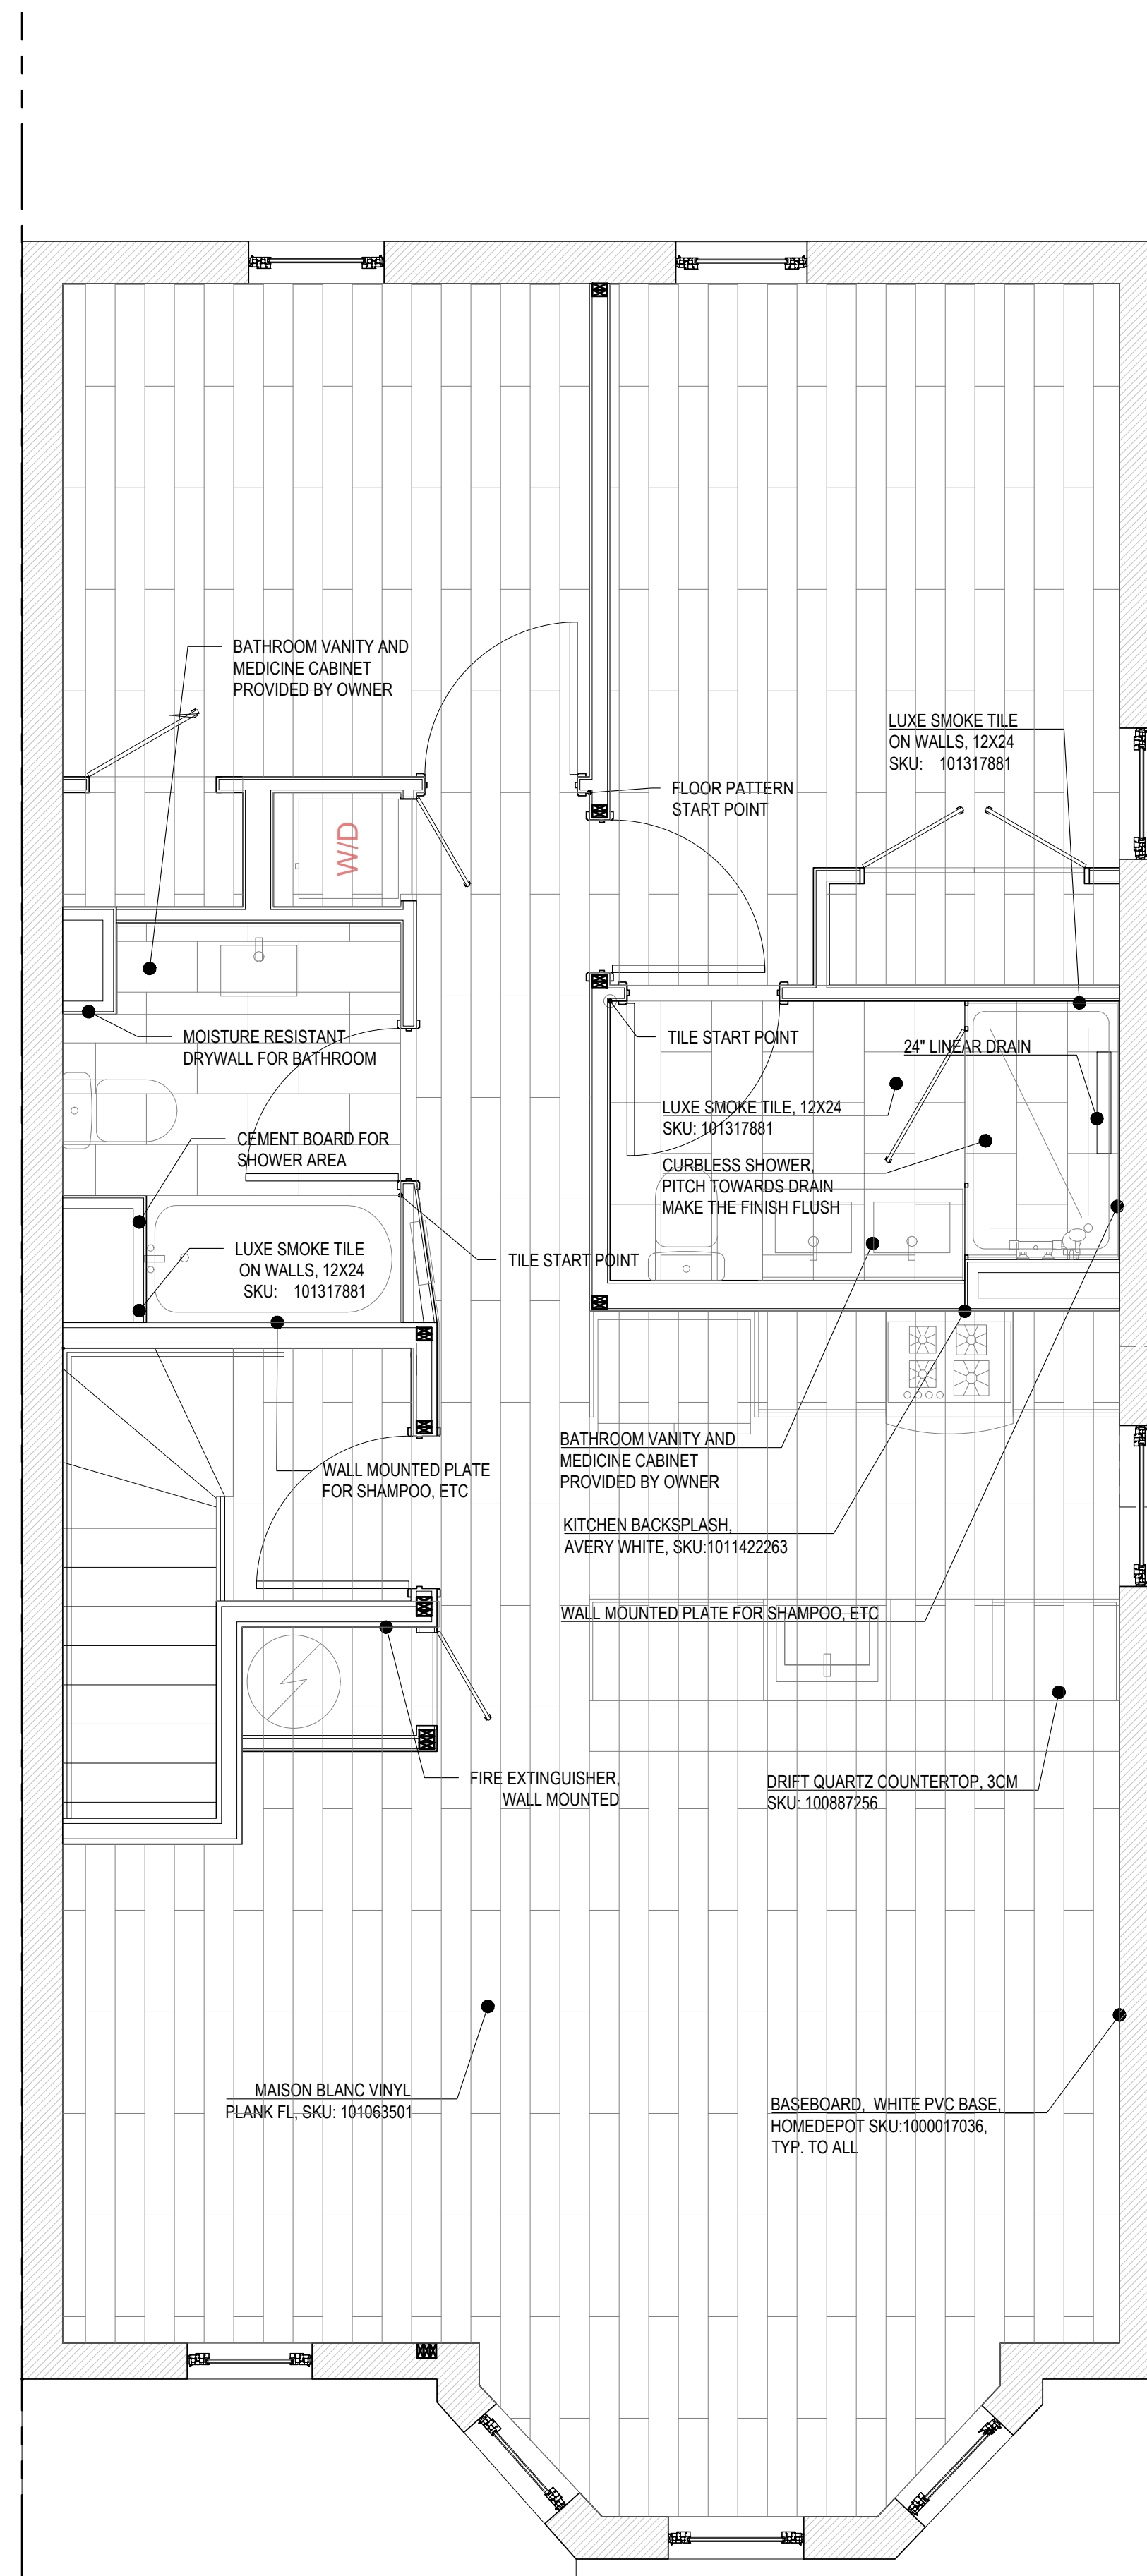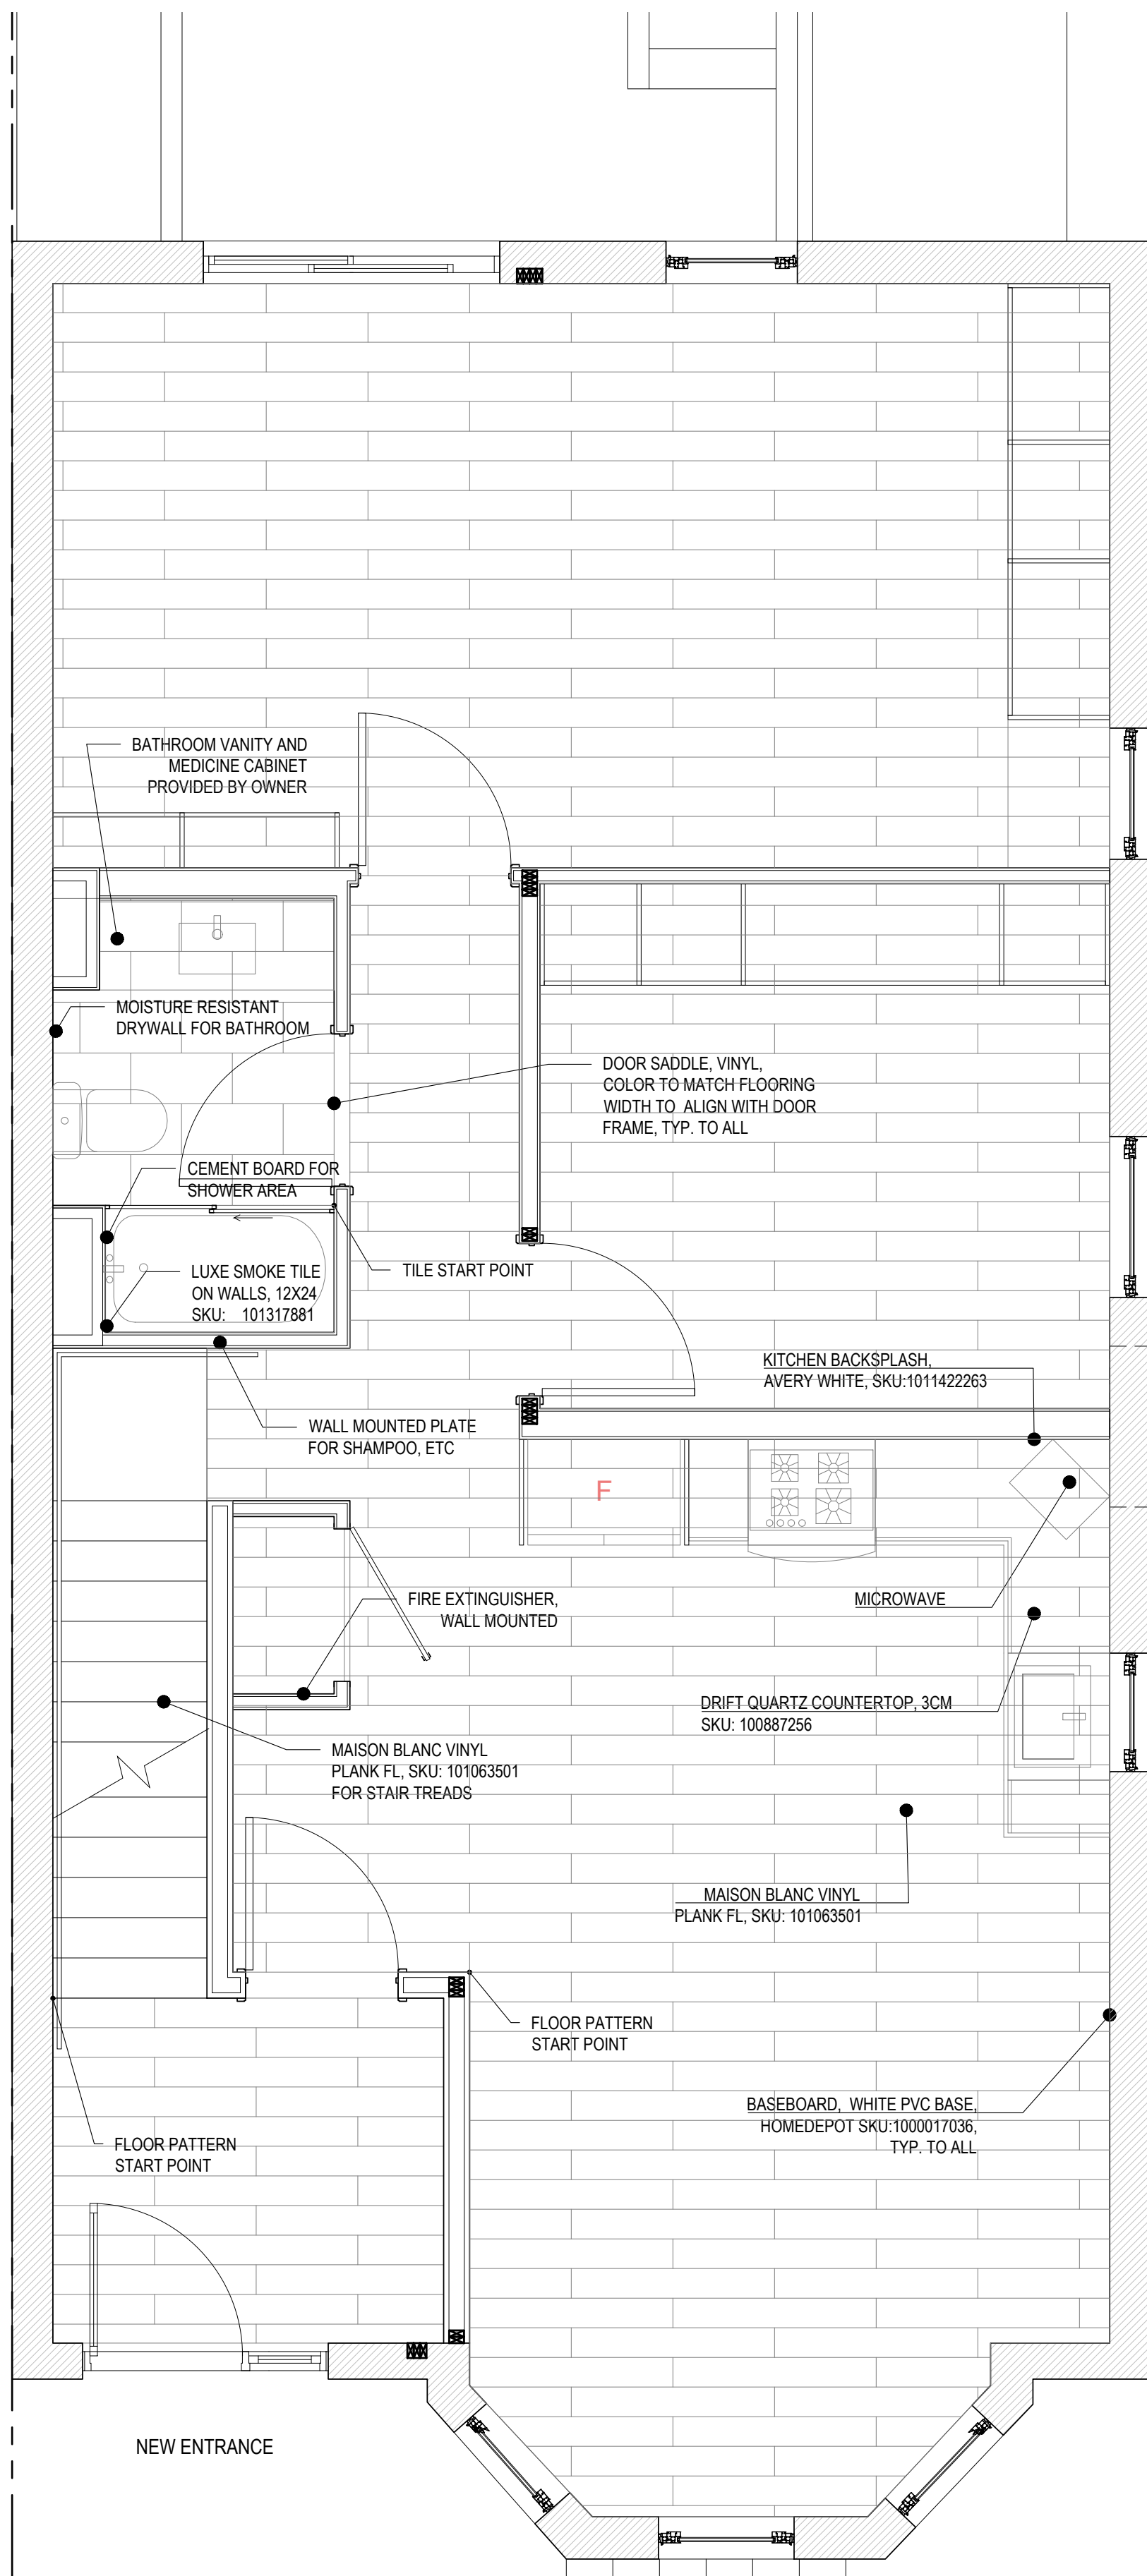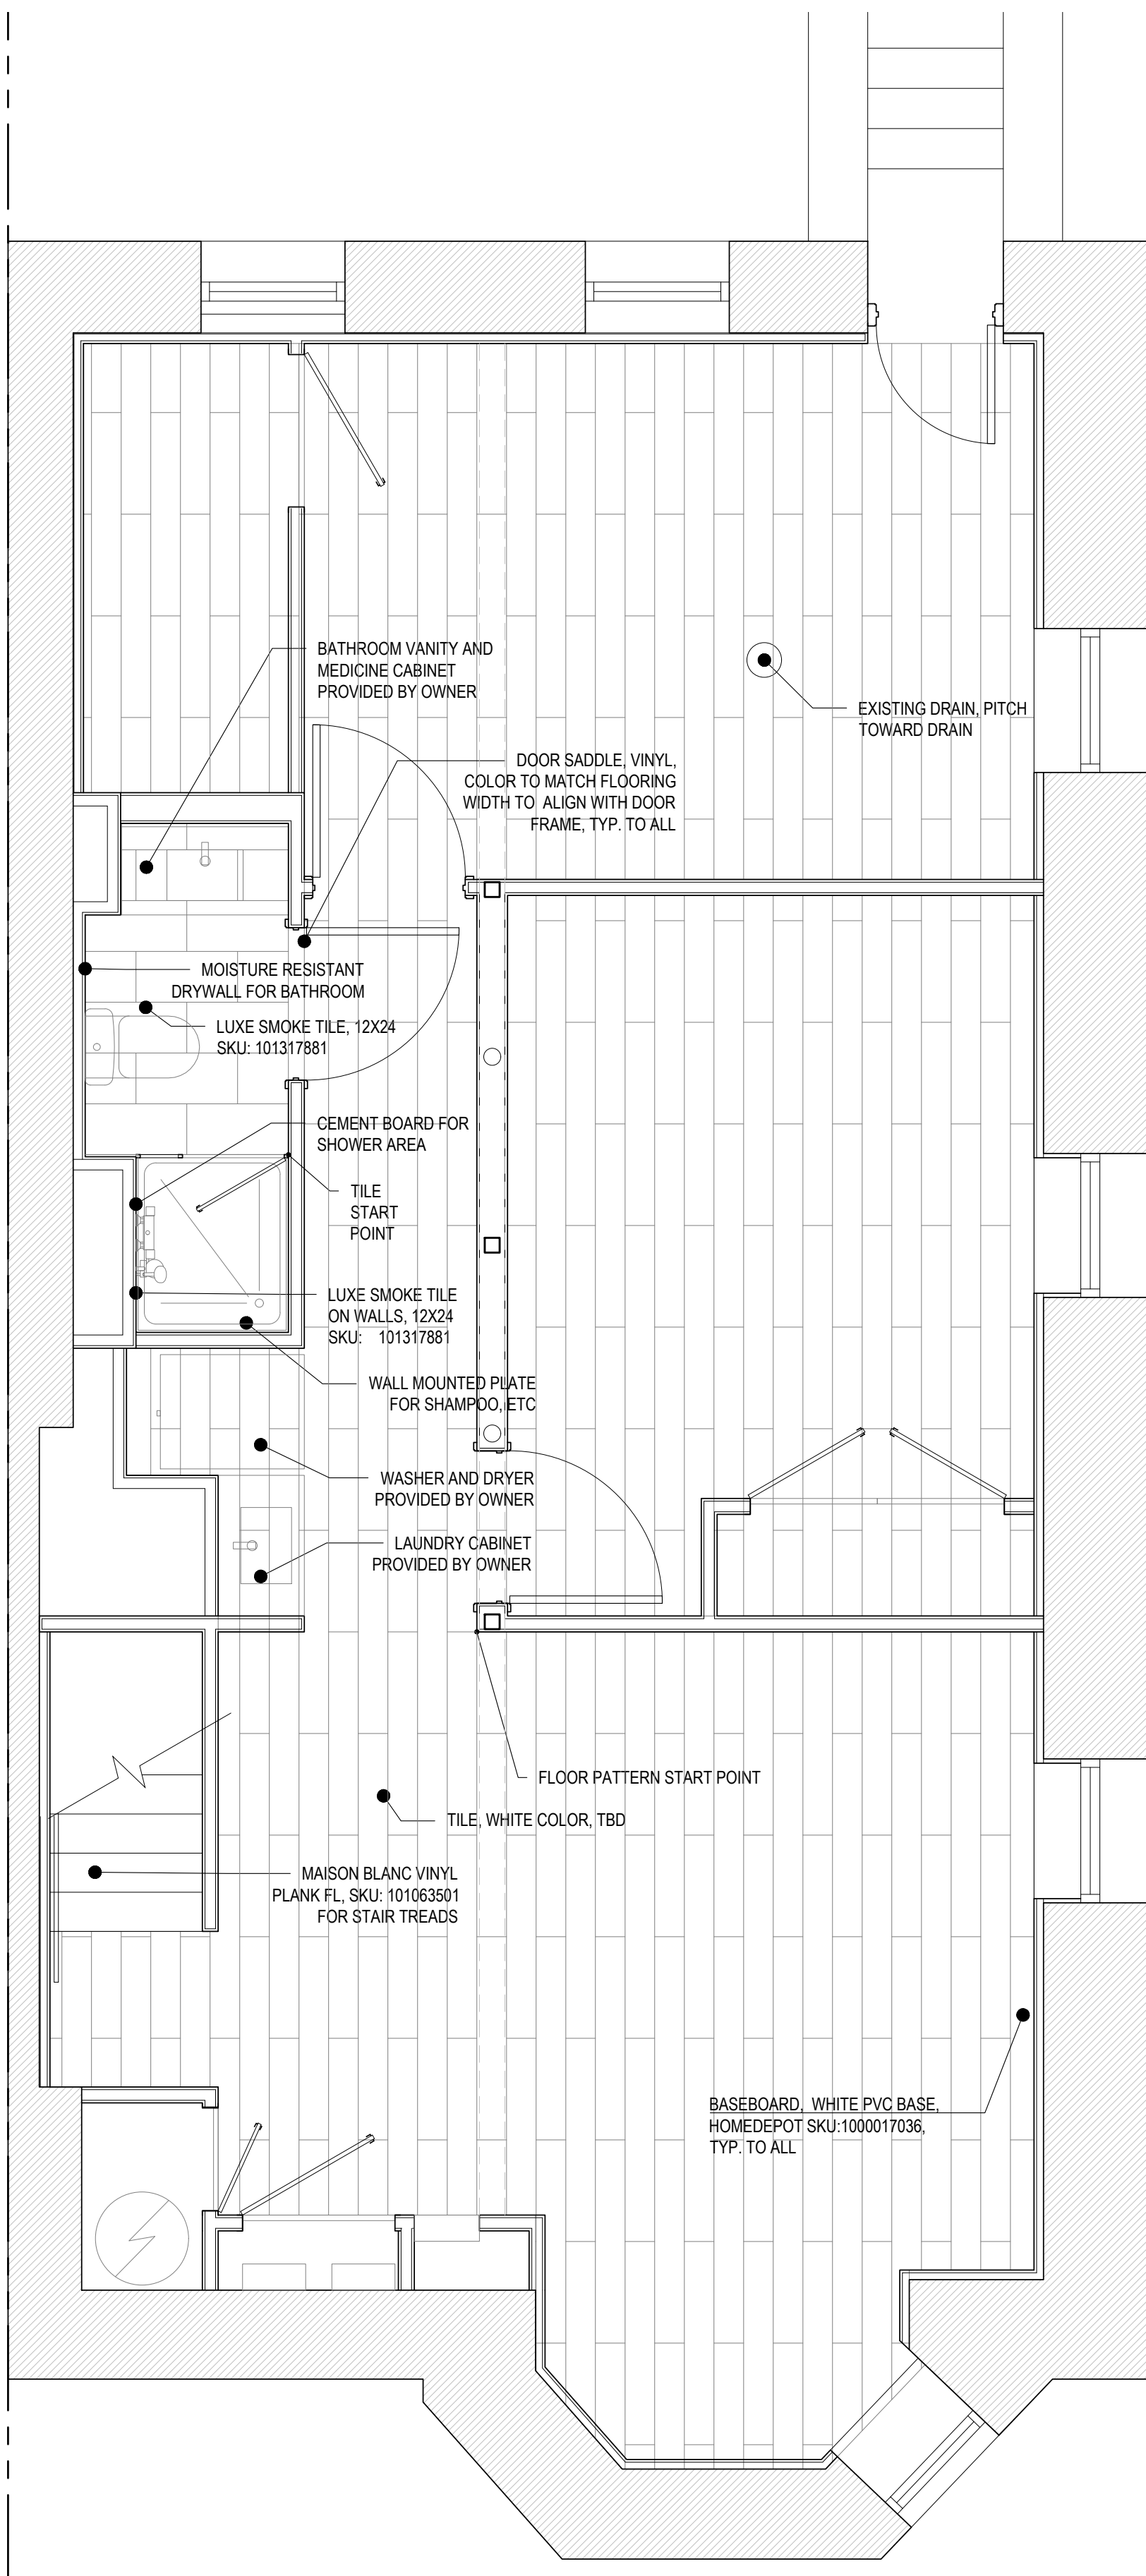

PROJECT 143
213 MAPLE STREET
213 MAPLE STREET, WEHAWKEN, NEW JERSEY, 07086

CONSULTANTS:
STRUCTURAL ENGINEER
FLEX ENGINEERING GROUP LLC
3133 CENTRAL AVE #202, UNION CITY, NJ 07087
T: 201-974-9570
E: flexengineer@yahoo.com

MECHANICAL ENGINEER
FLEX ENGINEERING GROUP LLC
3133 CENTRAL AVE #202, UNION CITY, NJ 07087
T: 201-974-9570
E: flexengineer@yahoo.com

GENERAL CONTRACTOR
HOBOKEN KITCHEN & BATH
2 14TH ST PH 32, HOBOKEN NJ, 07030
T: 201-472-0425
E: thestone@hobokenkitchenandbath.com

#	DATE	DESCRIPTION
---	------	-------------

DOB STAMP AND SIGNATURE

SEAL AND SIGNATURE

CONTRACTORS SHALL ONLY UTILIZE WRITTEN DIMENSIONS. CONTRACTORS SHALL VERIFY AND BE RESPONSIBLE FOR ALL DIMENSIONS AND CONDITIONS ON THE JOB. OWNER MUST BE NOTIFIED OF ANY VARIATIONS FROM DIMENSIONS AND CONDITIONS SHOWN BY THESE DRAWINGS. LOCAL SHOP DRAWINGS MUST BE SUBMITTED TO OWNER FOR APPROVAL, BEFORE PROCEEDING WITH ANY FABRICATION.

ALL DRAWINGS, SPECIFICATIONS, ETC. DISTRIBUTED TO CONTRACTORS, BIDDERS, GOVERNMENTAL AGENCIES, ETC., ARE NOT FOR GENERAL USE OR PUBLICATION BY OTHERS. ALL RIGHTS RESERVED. NONE OF THE IDEAS, DESIGN, ARRANGEMENTS OR PLANS IN THIS DRAWING SHALL BE USED BY OR DISCLOSED TO ANY PERSONS, FIRM OR CORPORATION FOR ANY PURPOSE WITHOUT THE WRITTEN PERMISSION OF OWNER.

DRAWING TITLE:
INTERIOR FLOOR PLANS

FOR CONSTRUCTION

A-101.00


POWER PLAN GENERAL NOTES
1. REFER TO ELECTRICAL DRAWINGS FOR CIRCUIT DETAILS
2. REFER TO INTERIOR ELEVATIONS FOR OUTLET HORIZONTAL AND VERTICAL DIMENSIONS

PROJECT 143
213 MAPLE STREET
213 MAPLE STREET, WEEHAWKEN, NEW JERSEY, 07086


CONSULTANTS:
STRUCTURAL ENGINEER
FLEX ENGINEERING GROUP LLC
3133 CENTRAL AVE #202, UNION CITY, NJ 07087
T: 201-974-9570
E: flexengineer@yahoo.com

MECHANICAL ENGINEER
FLEX ENGINEERING GROUP LLC
3133 CENTRAL AVE #202, UNION CITY, NJ 07087
T: 201-974-9570
E: flexengineer@yahoo.com


GENERAL CONTRACTOR
HOBOKEN KITCHEN & BATH
2 14TH ST PH 32, HOBOKEN NJ, 07030
T: 201-472-0425
E: thestone@hobokenkitchenandbath.com

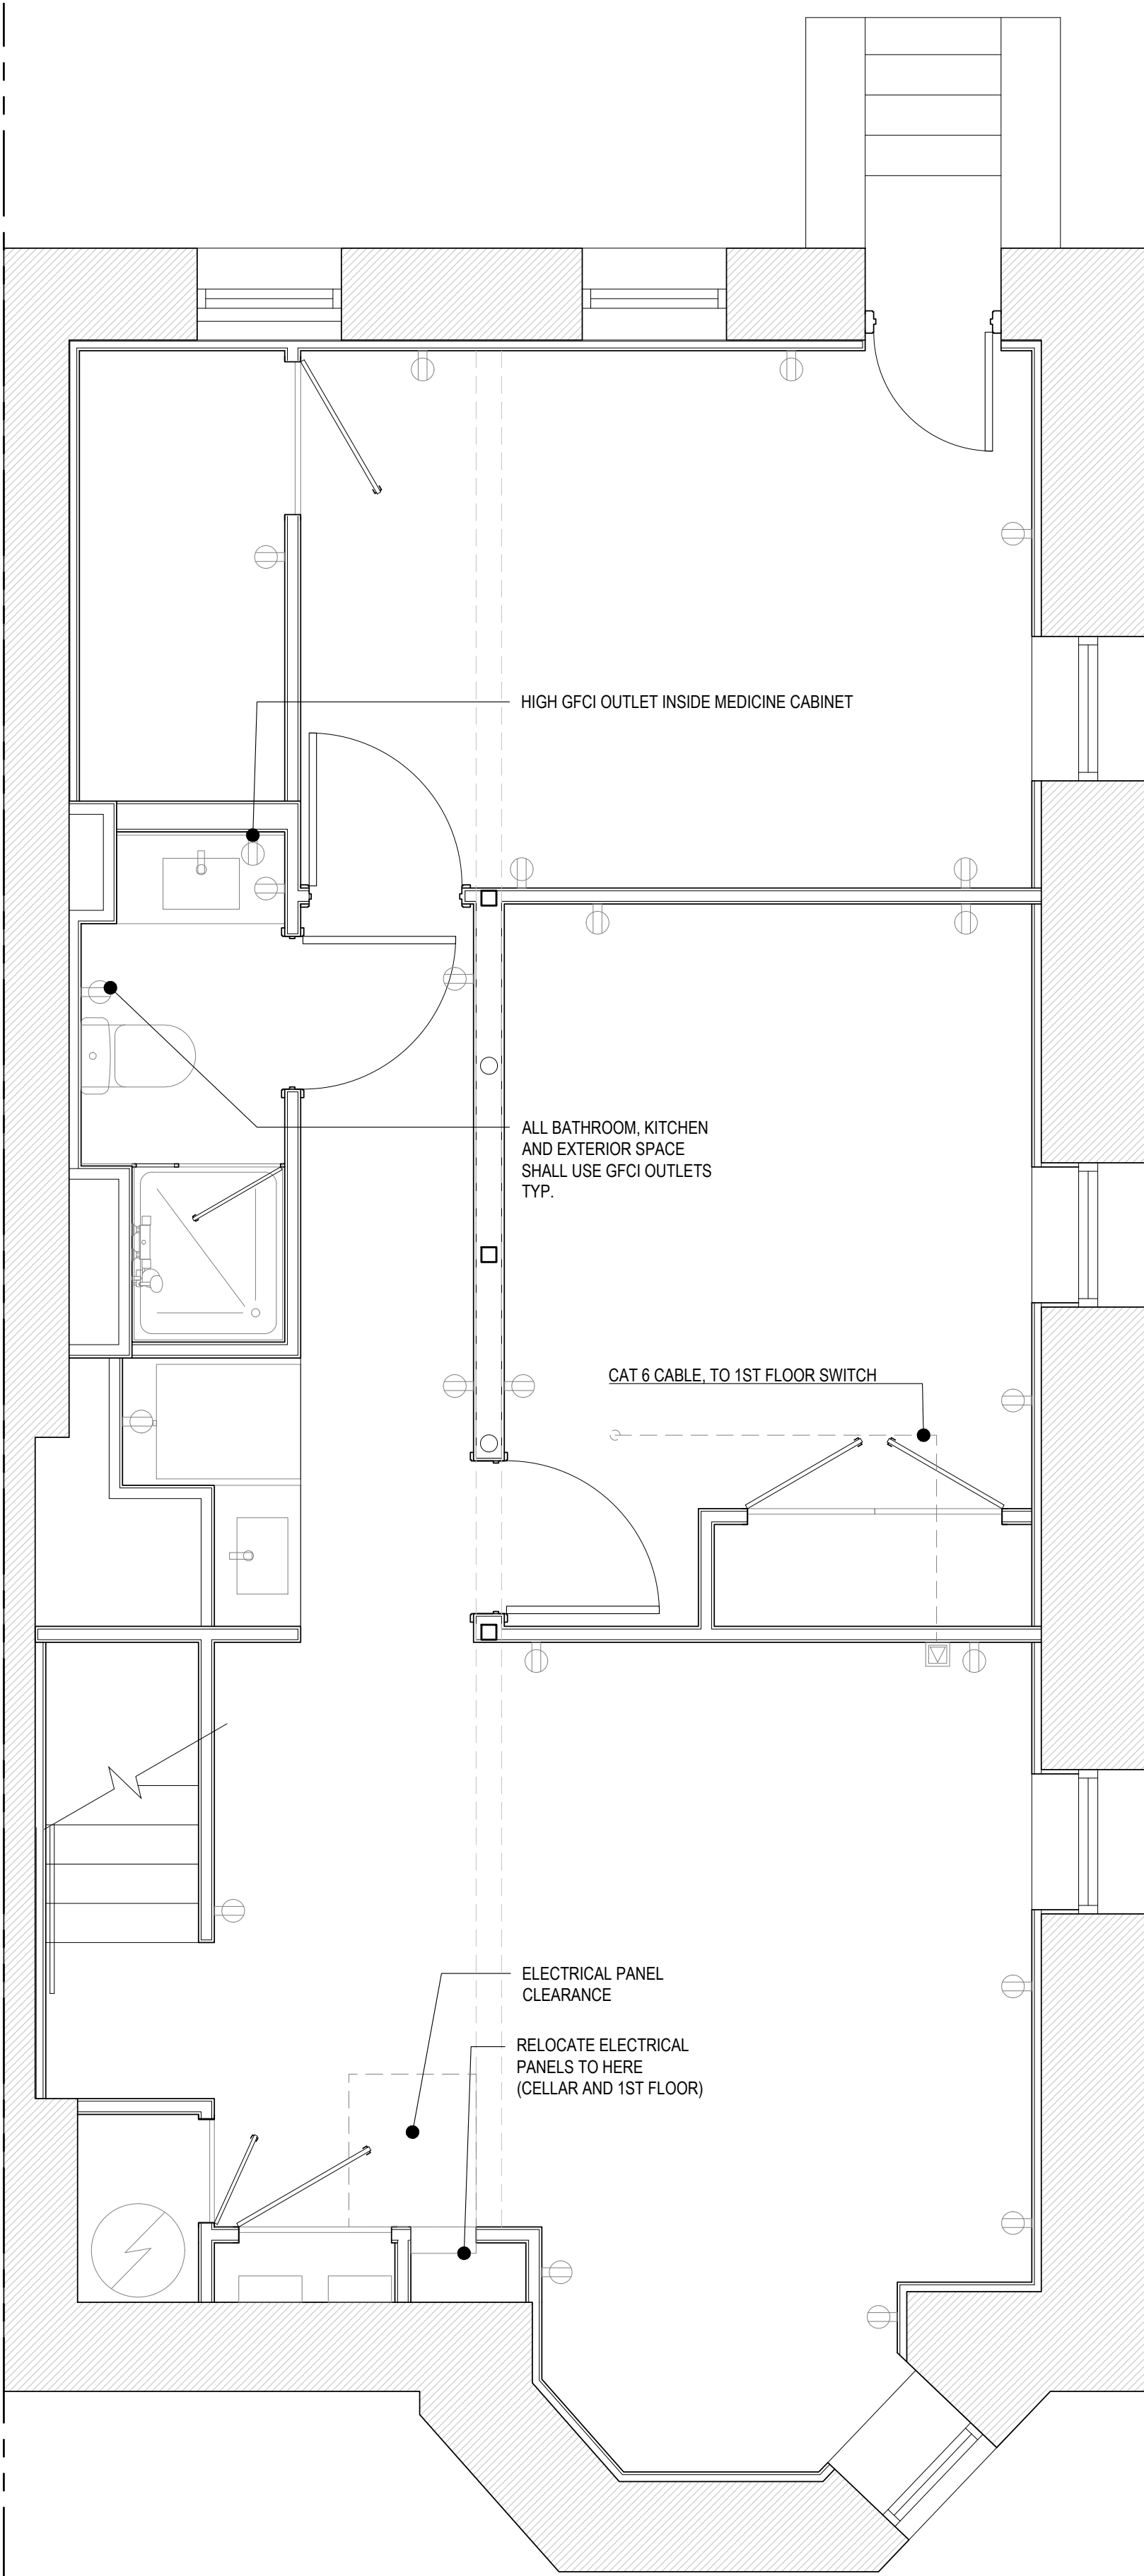

01 BASEMENT FLOOR - POWER PLAN
3/16" = 1'

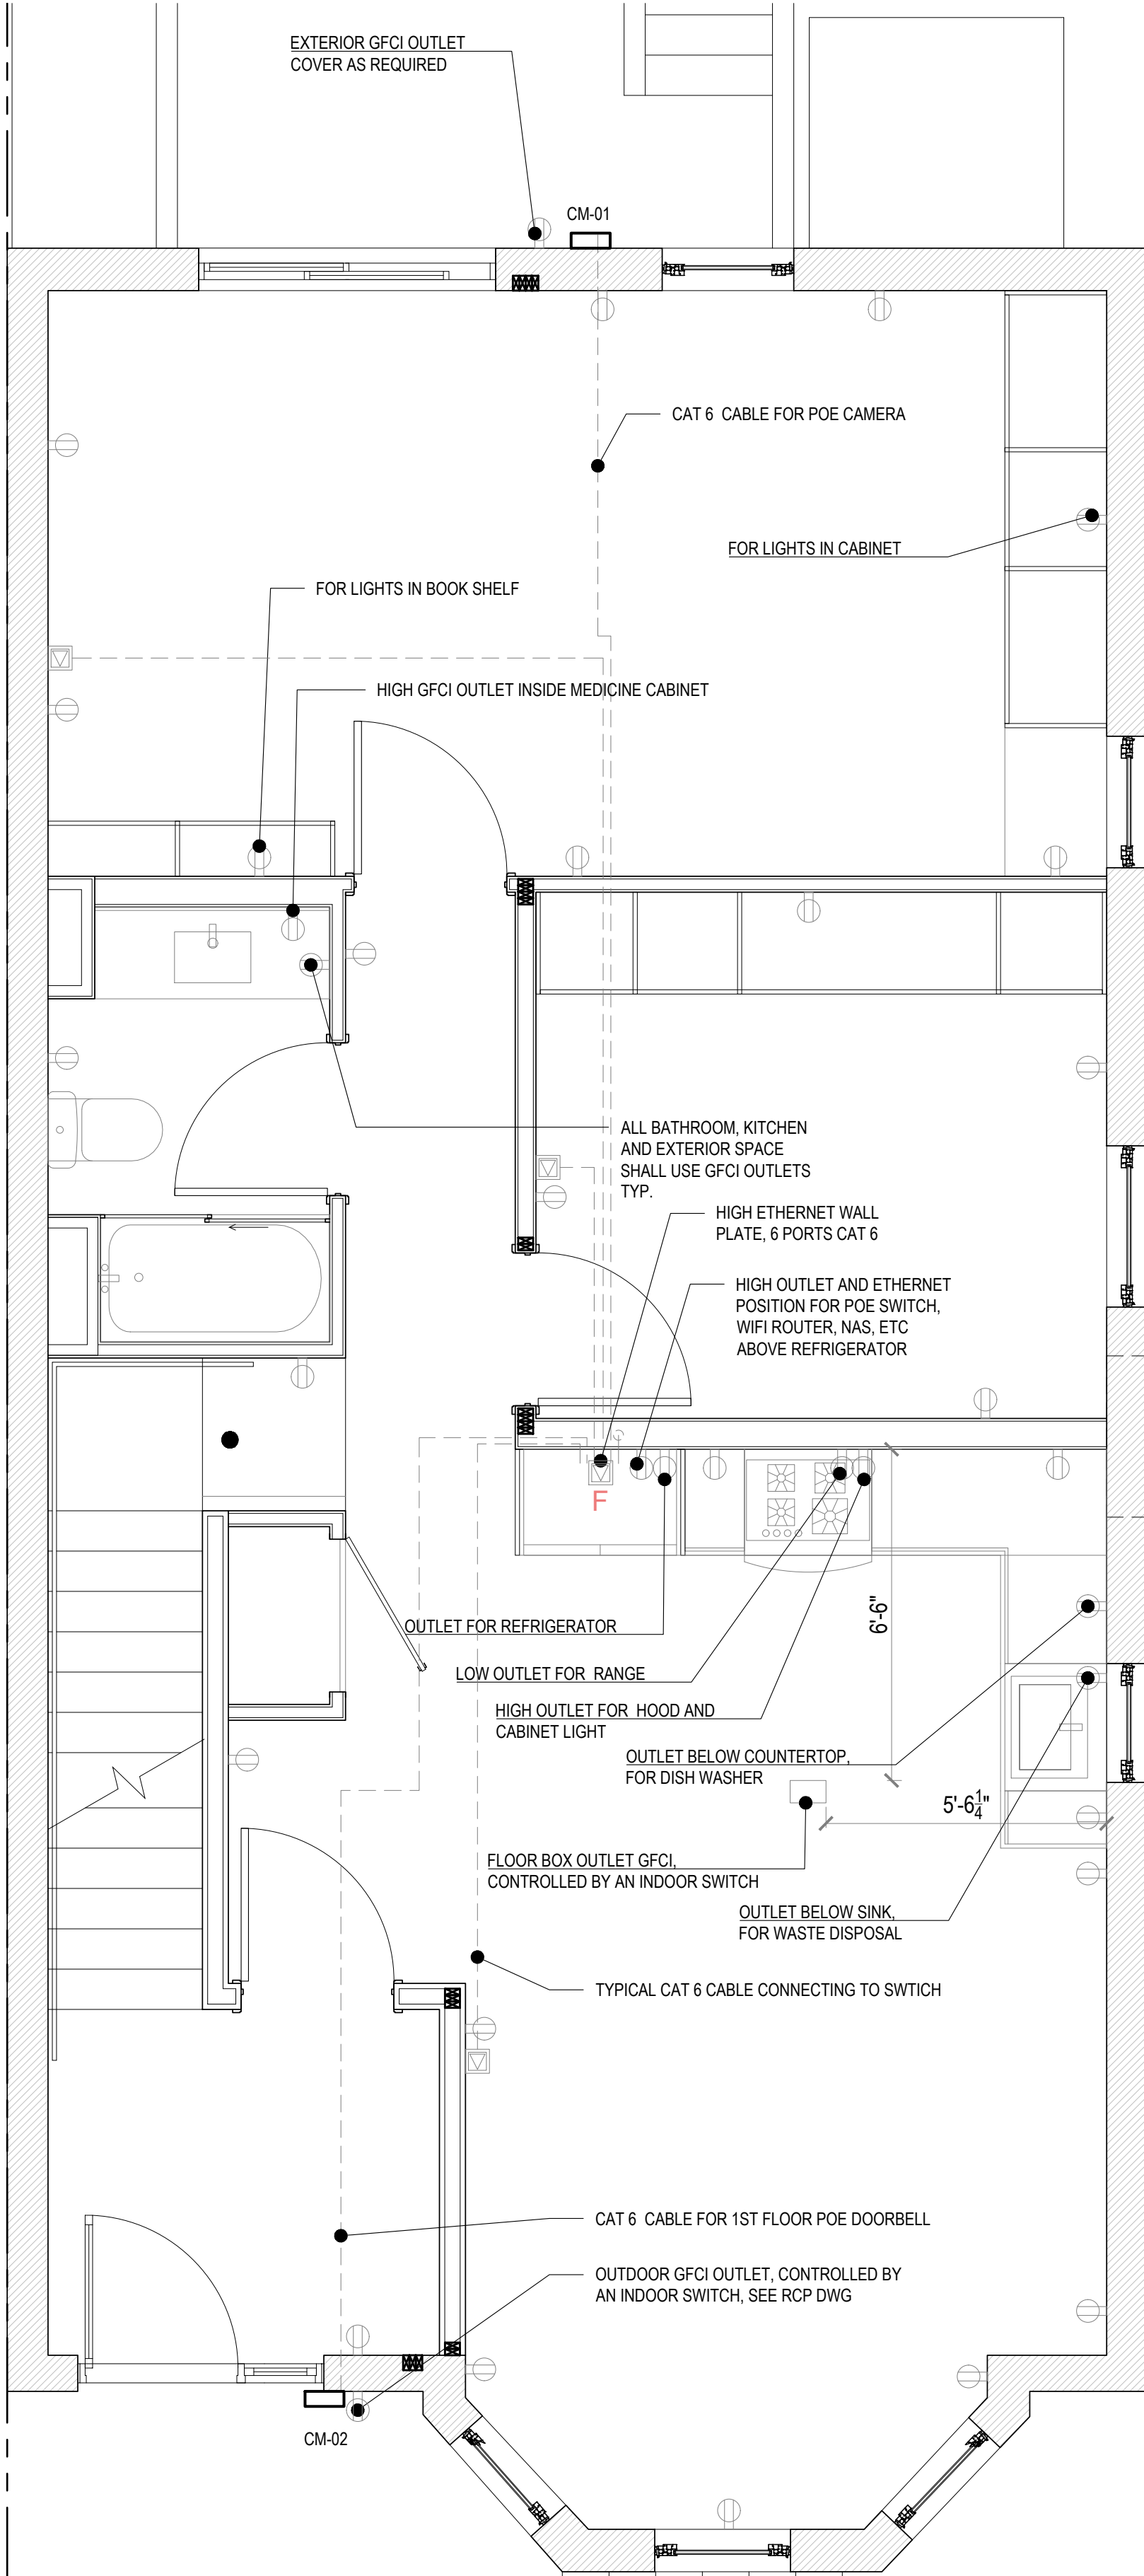

02 1ST FLOOR - POWER PLAN
3/16" = 1'

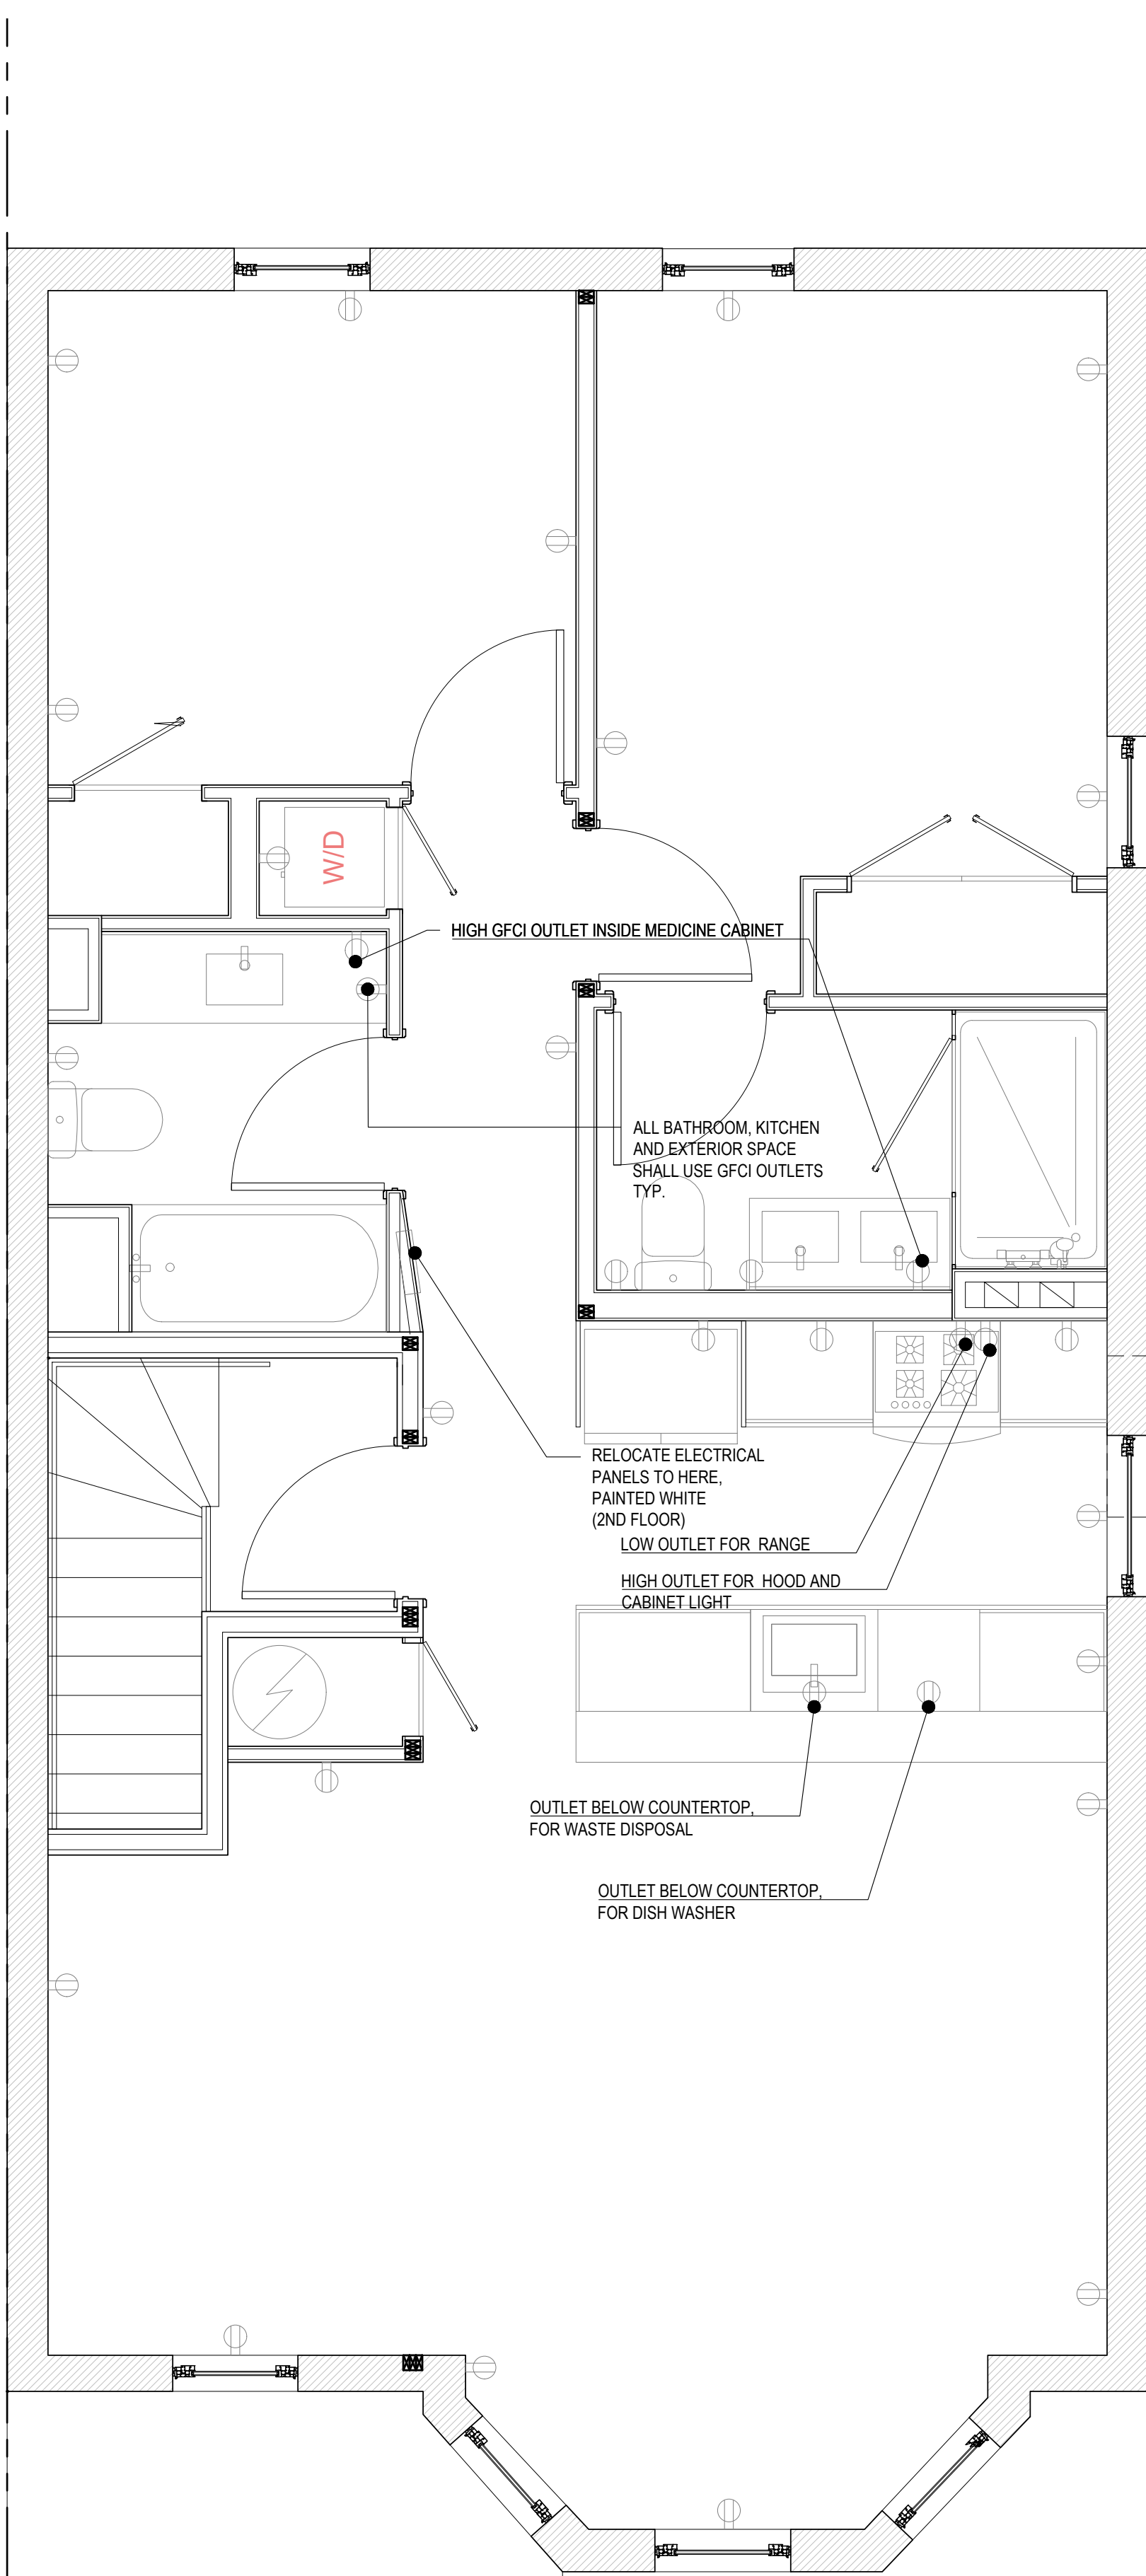

03 2ND FLOOR - POWER PLAN
3/16" = 1'

#	DATE	DESCRIPTION
---	------	-------------

DOB STAMP AND SIGNATURE

SEAL AND SIGNATURE

CONTRACTORS SHALL ONLY UTILIZE WRITTEN DIMENSIONS. CONTRACTORS SHALL VERIFY AND BE RESPONSIBLE FOR ALL DIMENSIONS AND CONDITIONS ON THE JOB. ANY OTHER MEASUREMENTS OR NOTICES OF ANY VARIATIONS FROM DIMENSIONS AND CONDITIONS SHOWN BY THESE DRAWINGS, INCLUDING SHOP DRAWINGS, MUST BE SUBMITTED TO OWNER FOR APPROVAL, BEFORE PROCEEDING WITH ANY FABRICATION.

ALL DRAWINGS, SPECIFICATIONS, ETC. DISTRIBUTED TO CONTRACTORS, BOARDS, GOVERNMENTAL AGENCIES, ETC., ARE NOT FOR GENERAL USE OR PUBLICATION BY OTHERS. ALL RIGHTS RESERVED. NONE OF THE IDEAS, DESIGN, ARRANGEMENTS OR PLANS IN THIS DRAWING SHALL BE USED BY OR DISCLOSED TO ANY PERSONS, FIRM OR CORPORATION FOR ANY PURPOSE WITHOUT THE WRITTEN PERMISSION OF OWNER.

DRAWING TITLE:
POWER PLANS


FOR CONSTRUCTION

A-102.00


POWER PLAN GENERAL NOTES
1. REFER TO ELECTRICAL DRAWINGS FOR CIRCUIT DETAILS
2. REFER TO INTERIOR ELEVATIONS FOR OUTLET HORIZONTAL AND VERTICAL DIMENSIONS

PROJECT 103
213 MAPLE STREET
213 MAPLE STREET, WEHAWKEN, NEW JERSEY, 07086


CONSULTANTS:
STRUCTURAL ENGINEER
FLEX ENGINEERING GROUP LLC
3133 CENTRAL AVE #202, UNION CITY, NJ 07087
T: 201-974-9570
E: flexengineer@yahoo.com
MECHANICAL ENGINEER
FLEX ENGINEERING GROUP LLC
3133 CENTRAL AVE #202, UNION CITY, NJ 07087
T: 201-974-9570
E: flexengineer@yahoo.com
GENERAL CONTRACTOR
HOBOKEN KITCHEN & BATH
2 14TH ST PH 32, HOBOKEN NJ, 07030
T: 201-472-0425
E: thestone@hobokenkitchenandbath.com

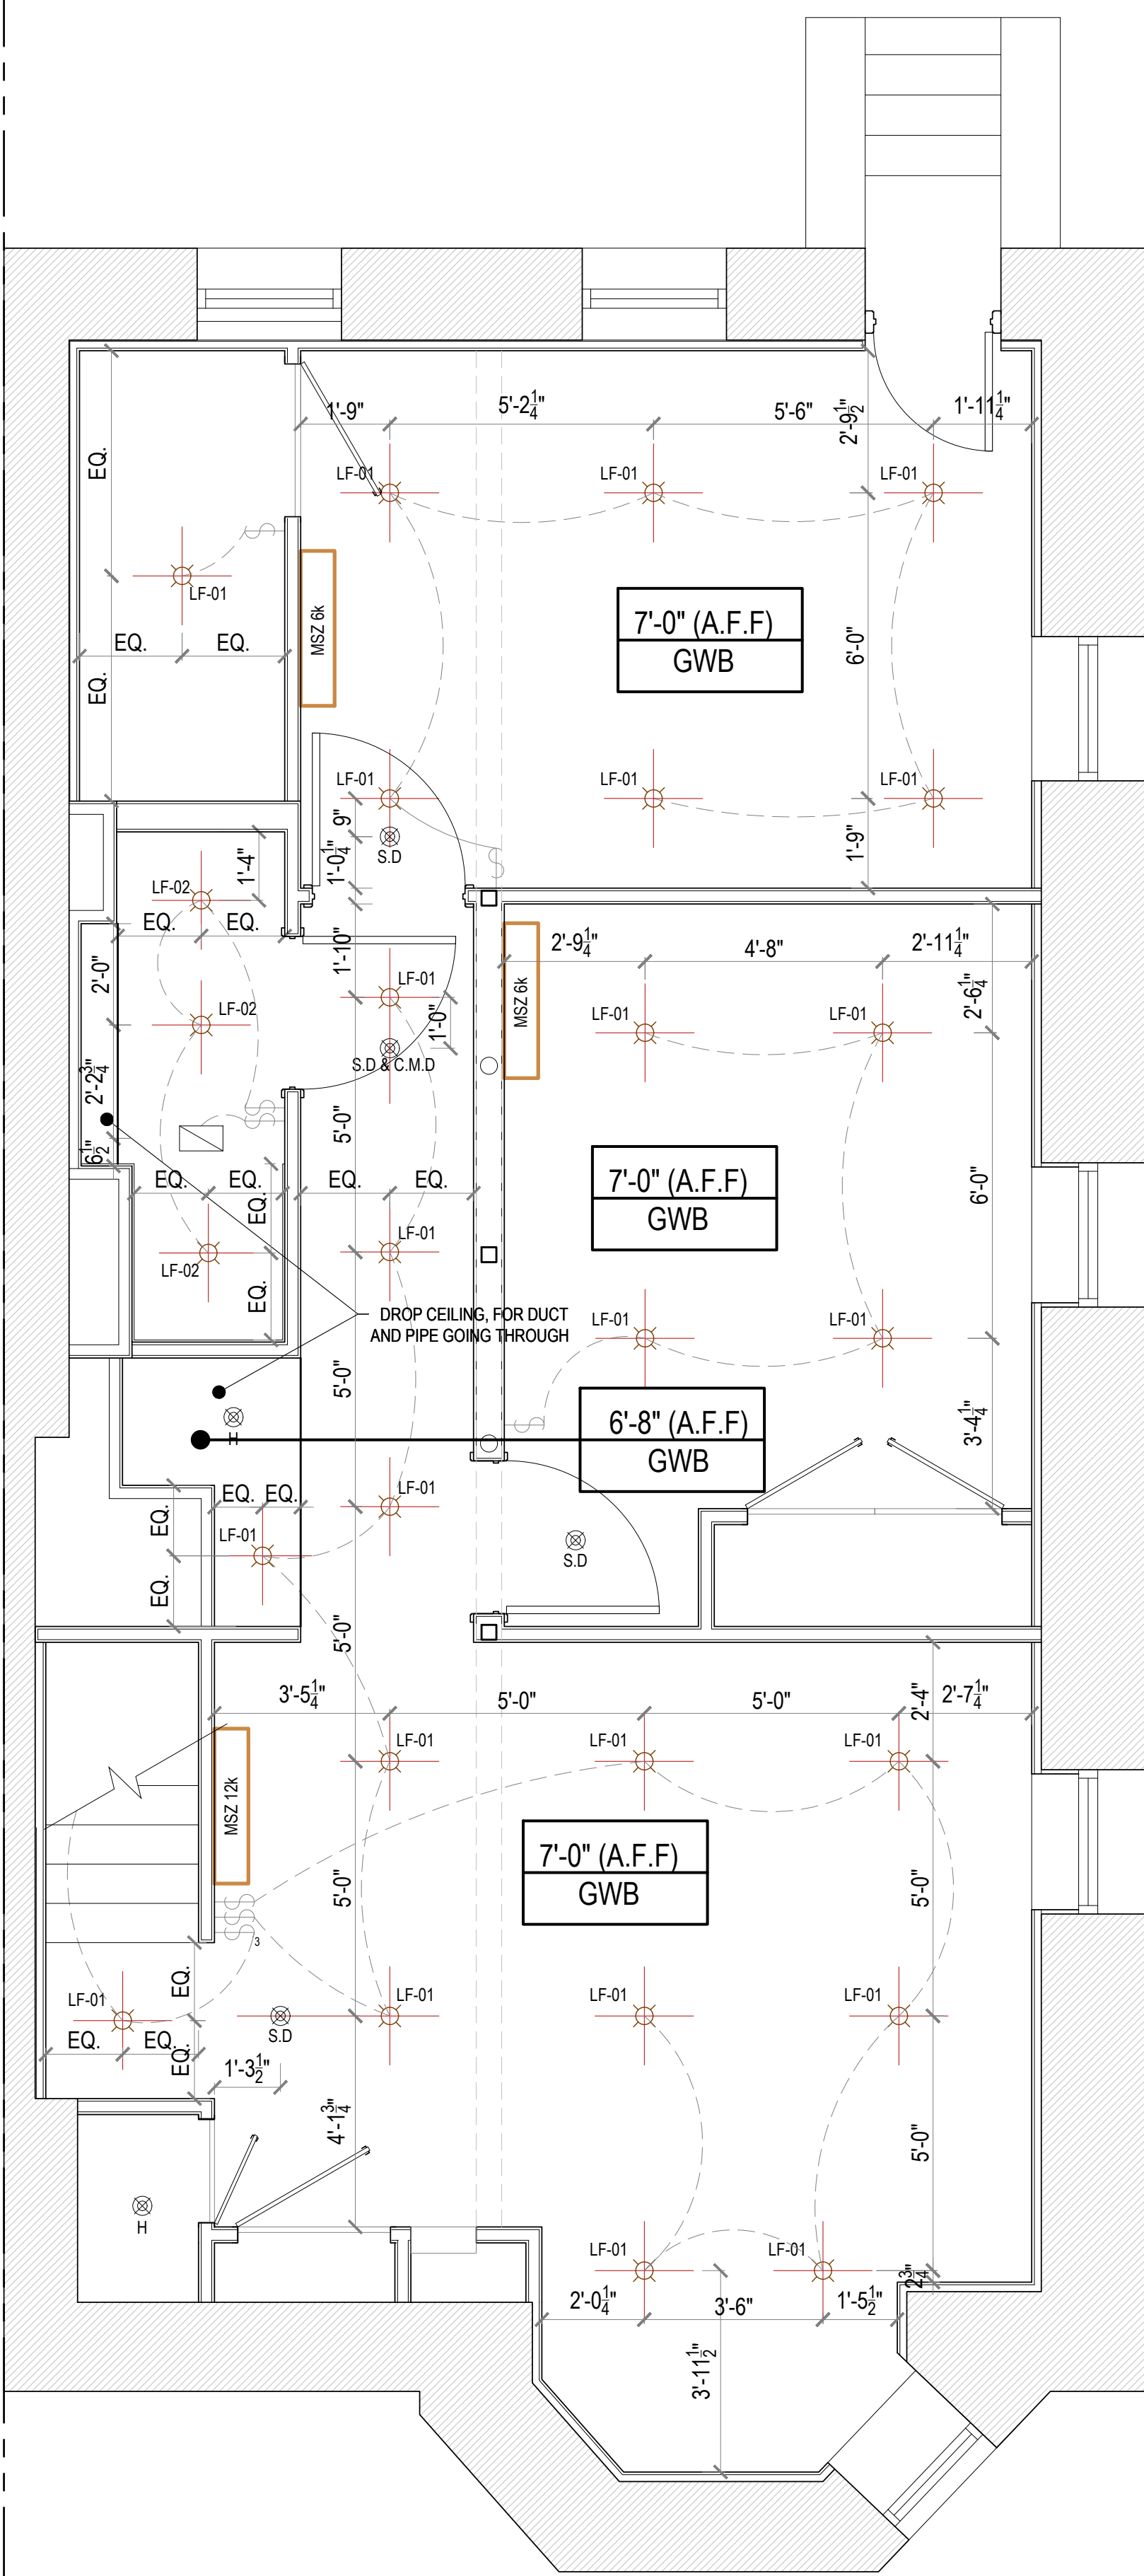

01 BASEMENT - RCP

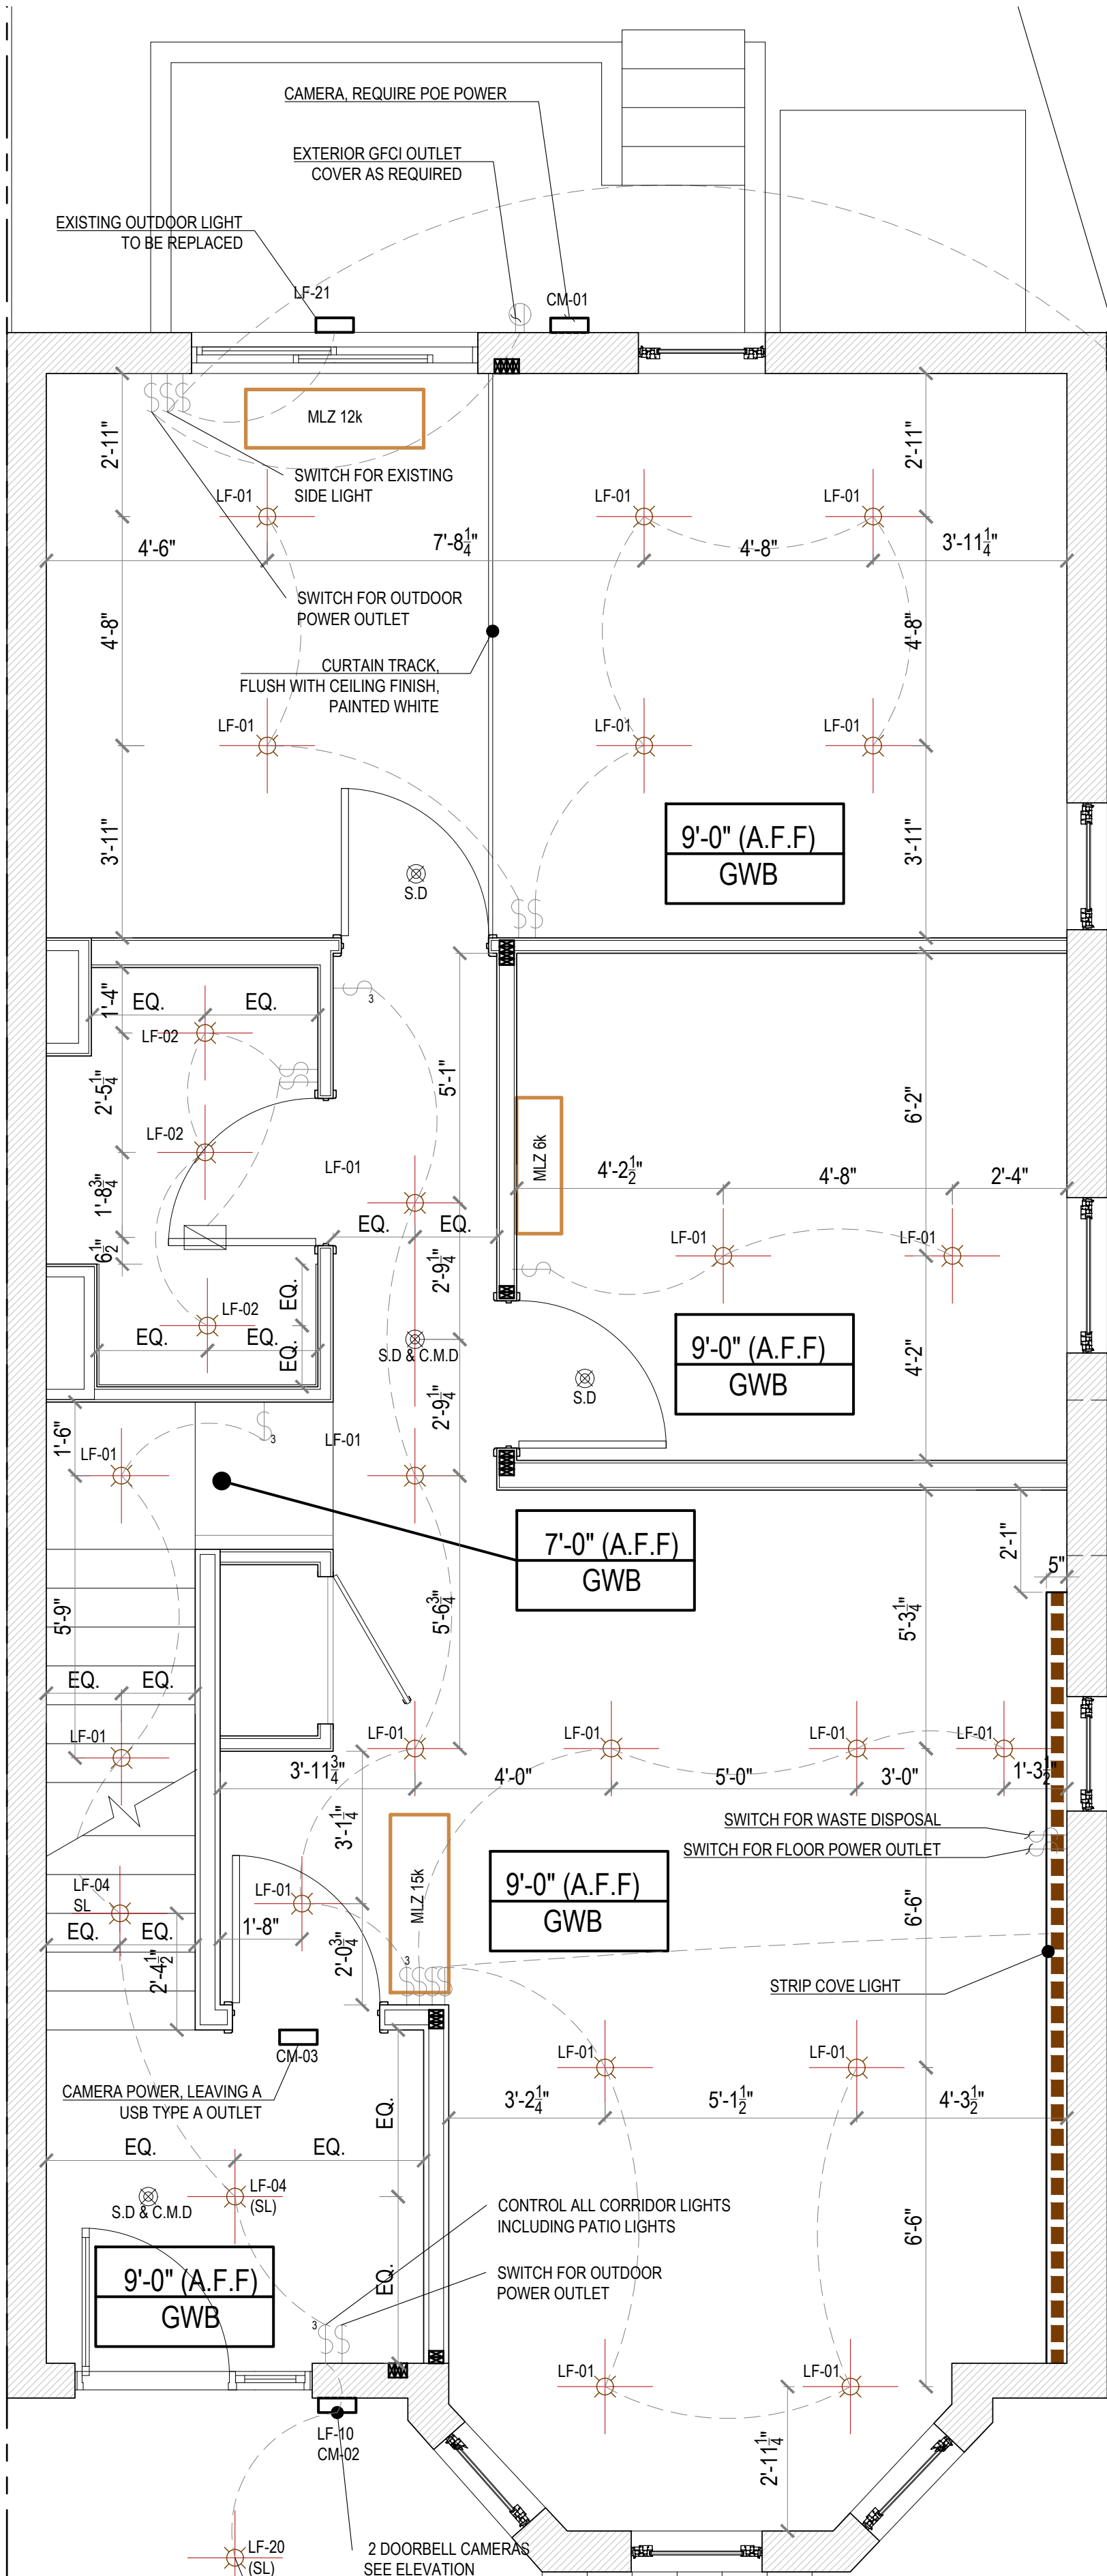

02 1ST FLOOR - RCP

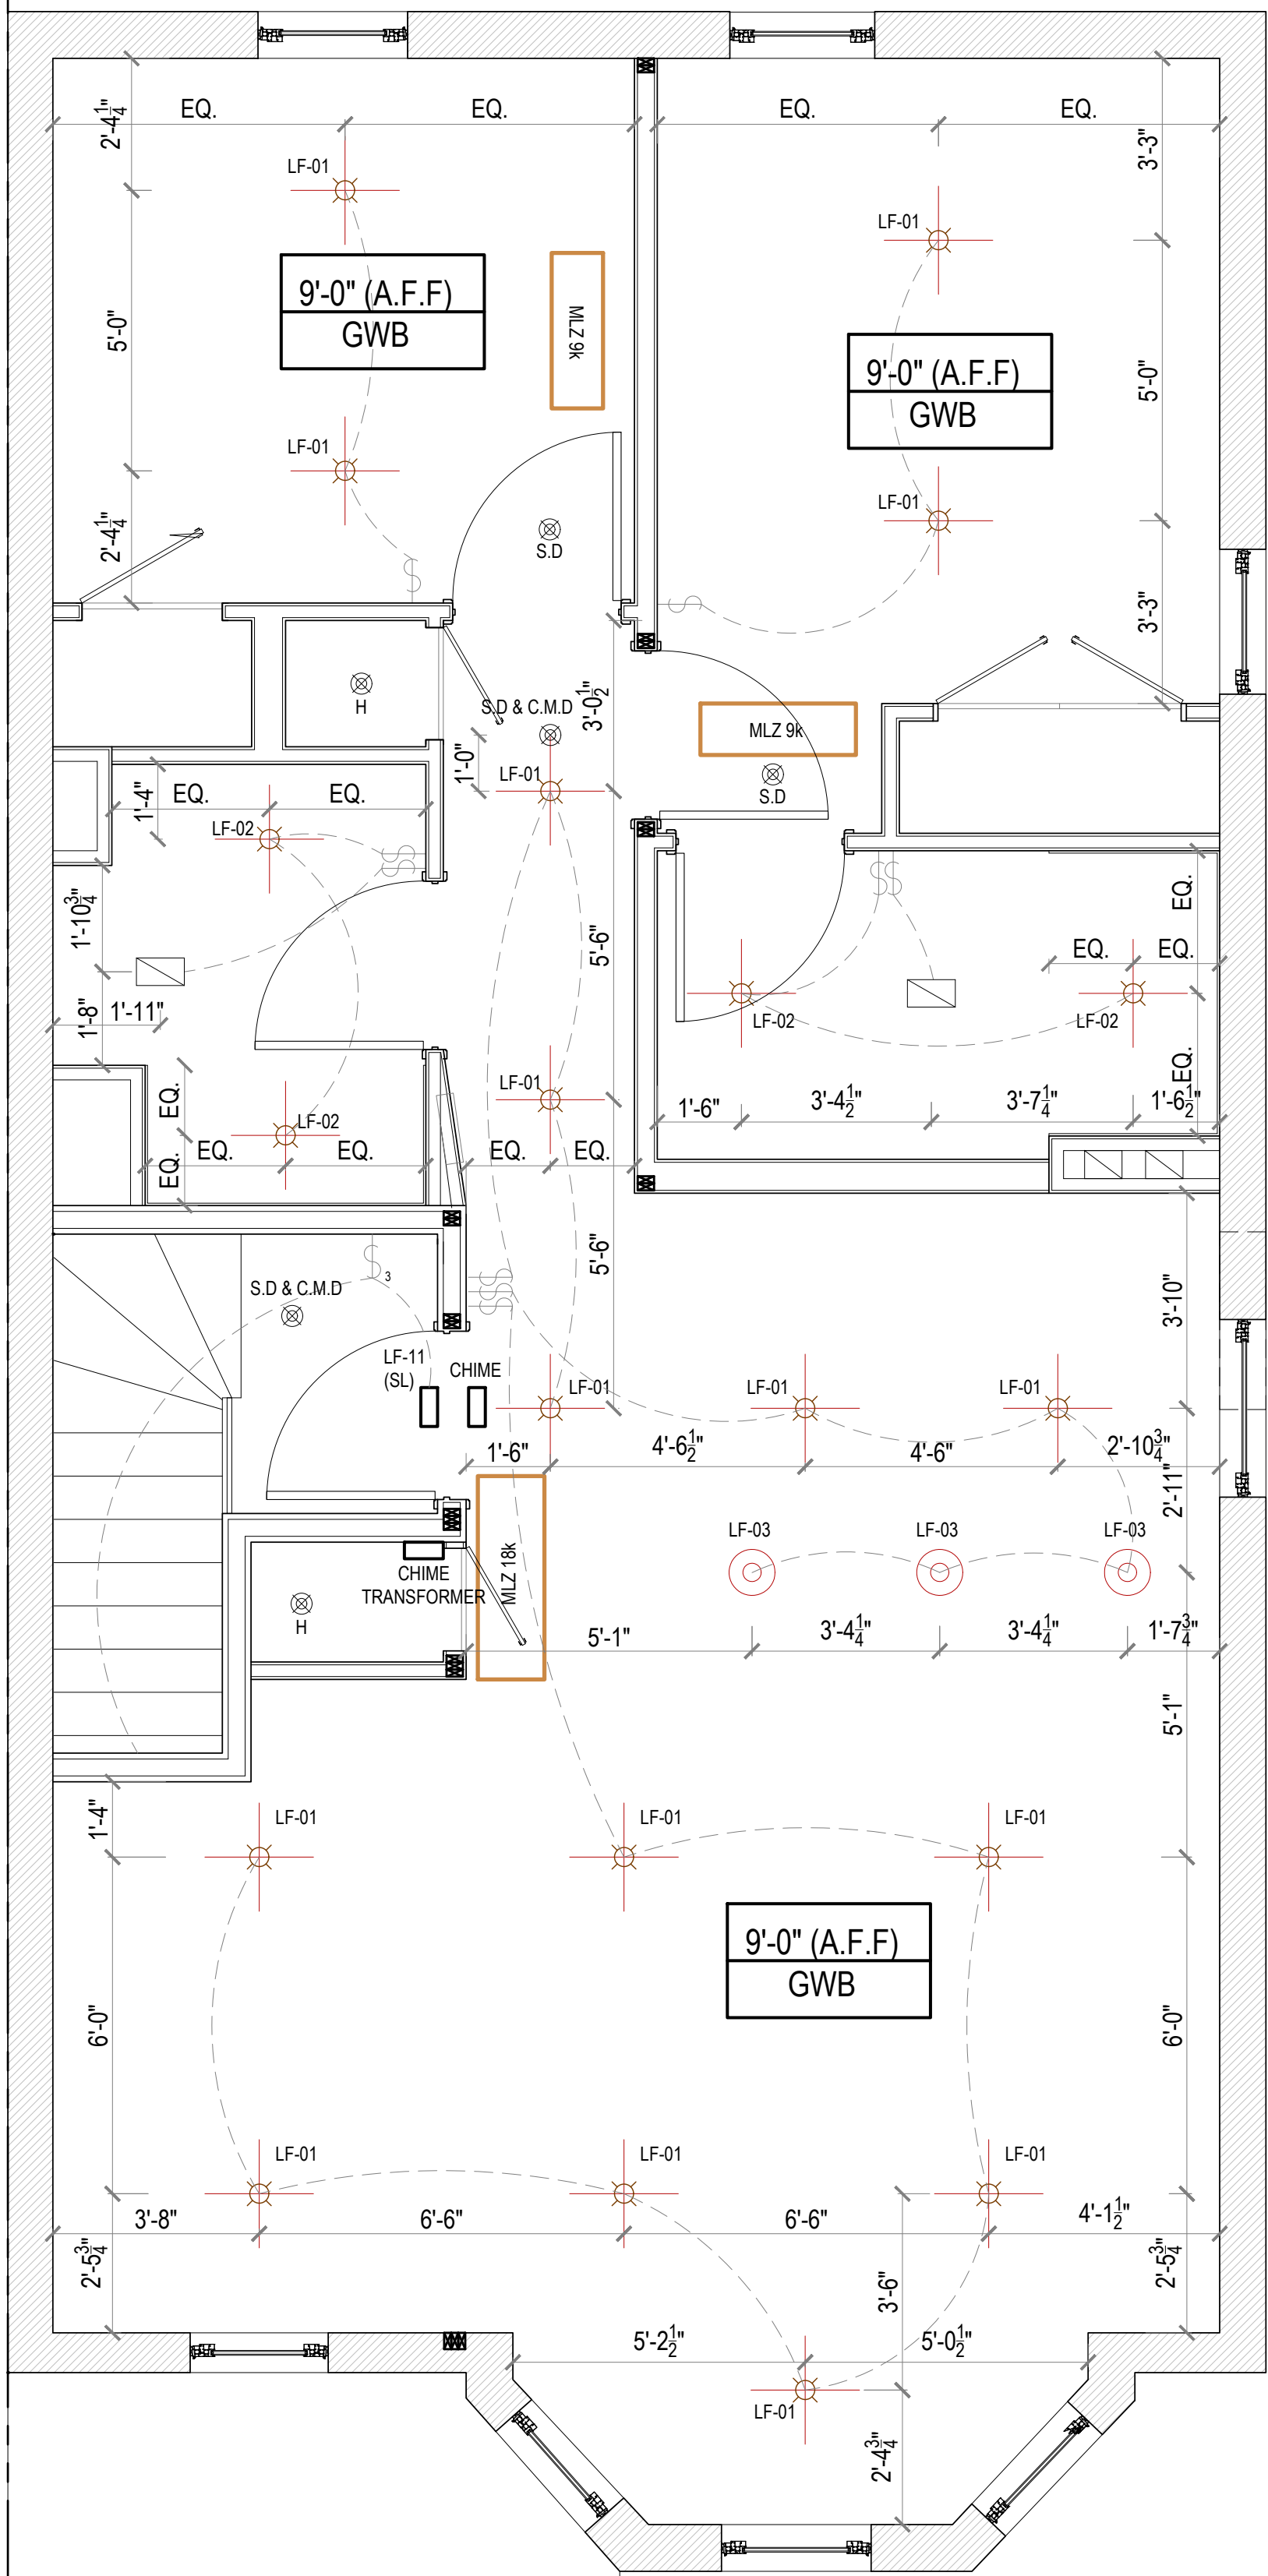

03 2ND FLOOR - RCP

DATE DESCRIPTION

DOB STAMP AND SIGNATURE




SEAL AND SIGNATURE

CONTRACTOR SHALL ONLY UTILIZE WRITTEN DIMENSIONS. CONTRACTOR SHALL VERIFY AND BE RESPONSIBLE FOR ALL DIMENSIONS AND CONDITIONS ON THE JOB. OWNER MUST BE NOTIFIED OF ANY VARIATIONS FROM DIMENSIONS AND CONDITIONS SHOWN BY THESE DIMENSIONS. ALL SHOP DRAWINGS MUST BE SUBMITTED TO OWNER FOR APPROVAL, BEFORE PROCEEDING WITH ANY FABRICATION.

DRAWING TITLE:
RCP

FOR CONSTRUCTION

A-103.00

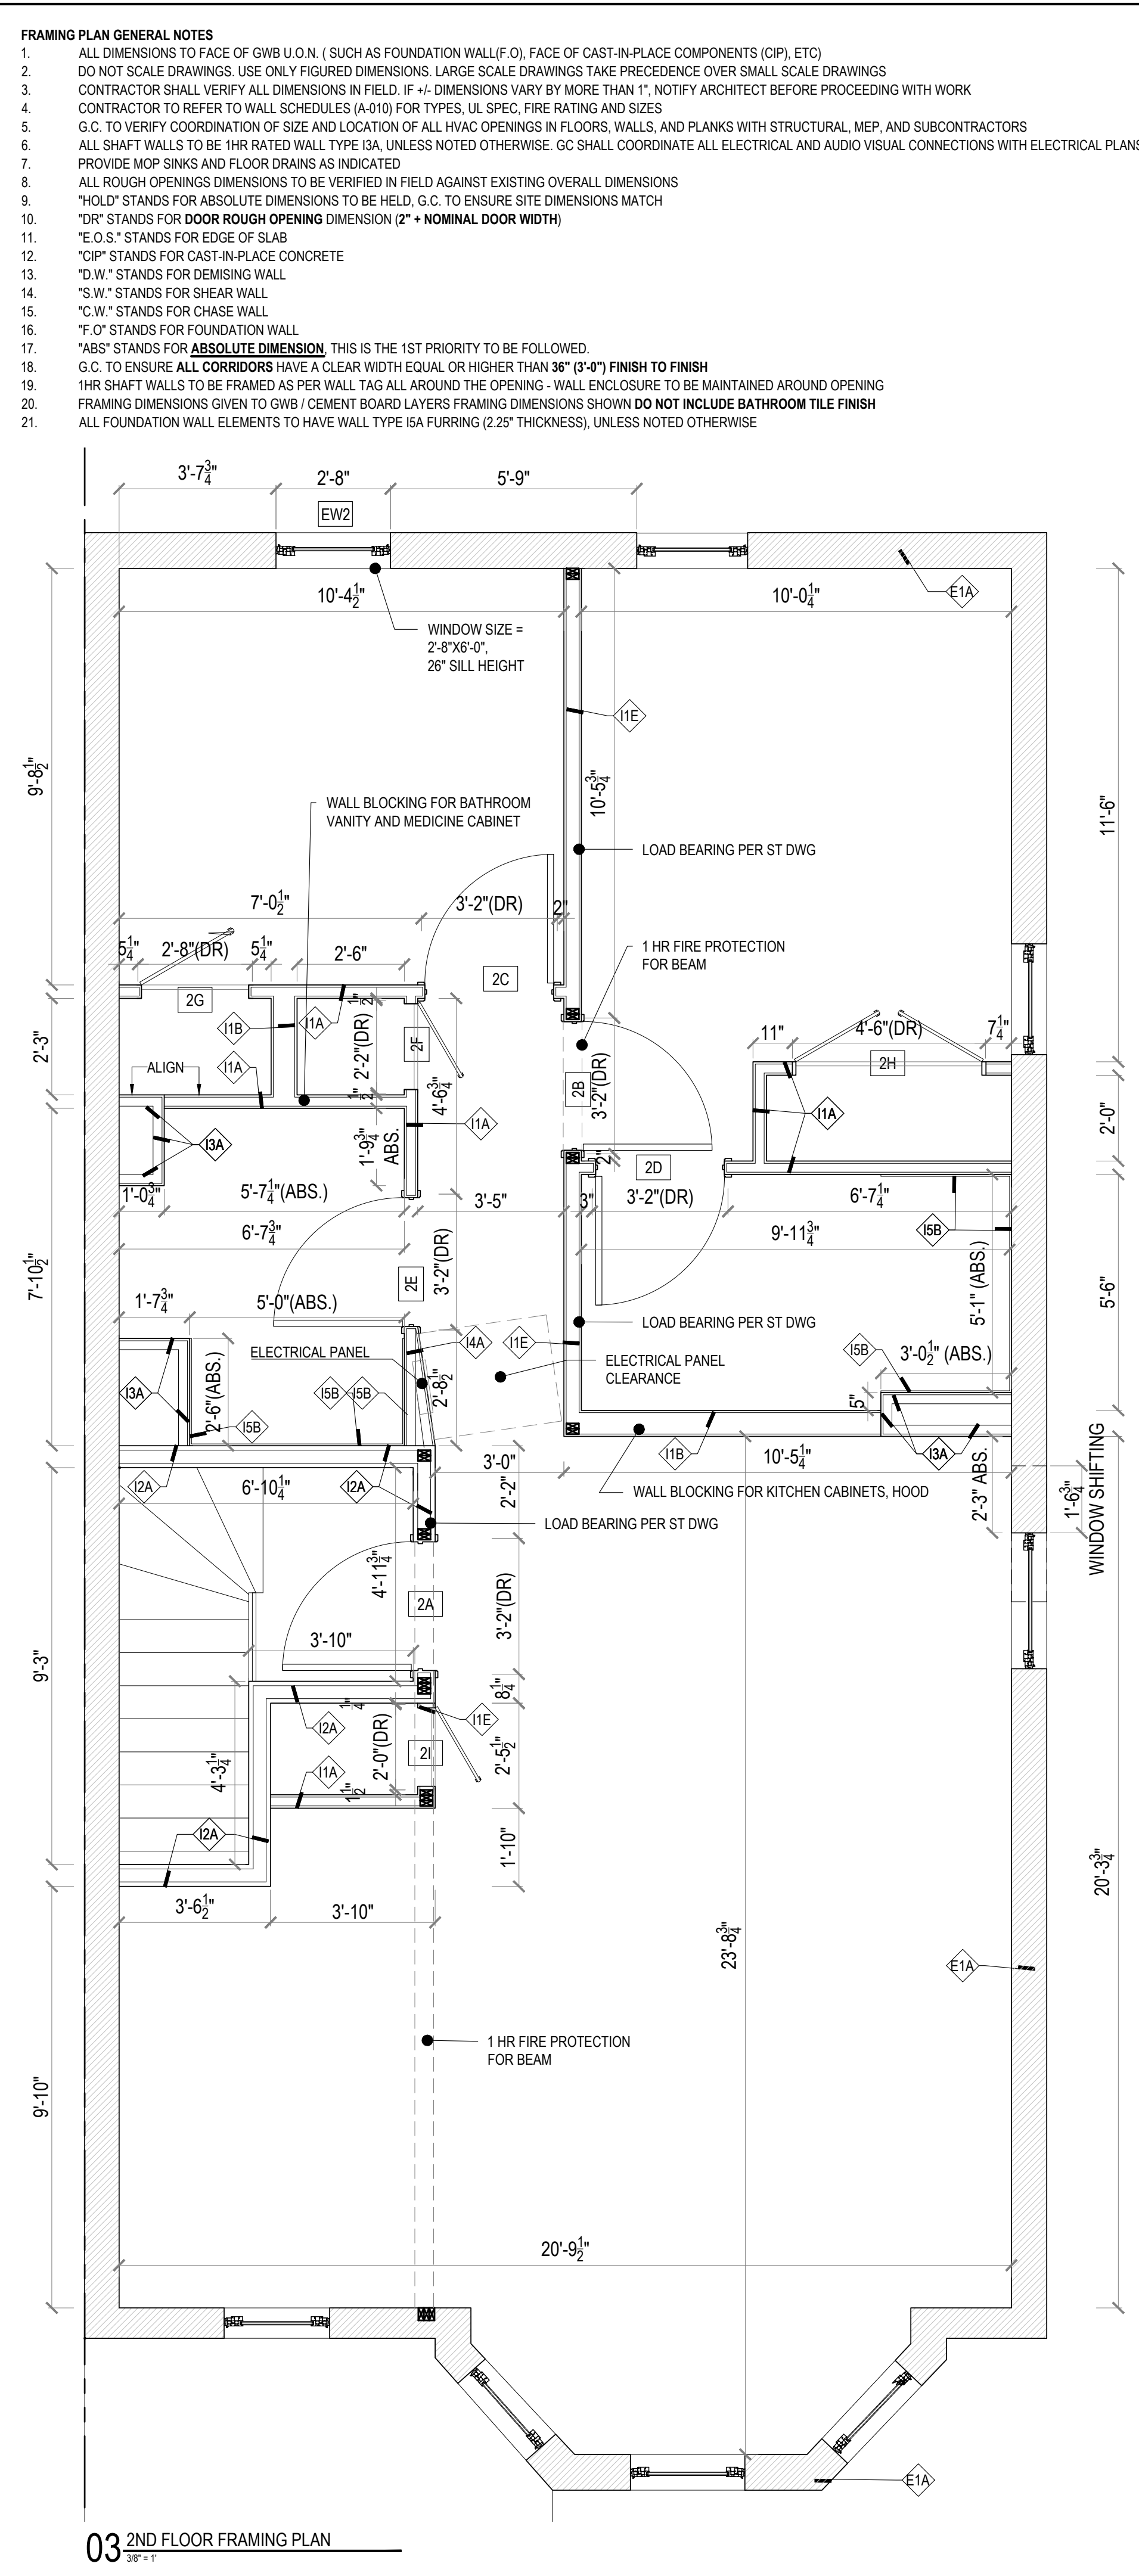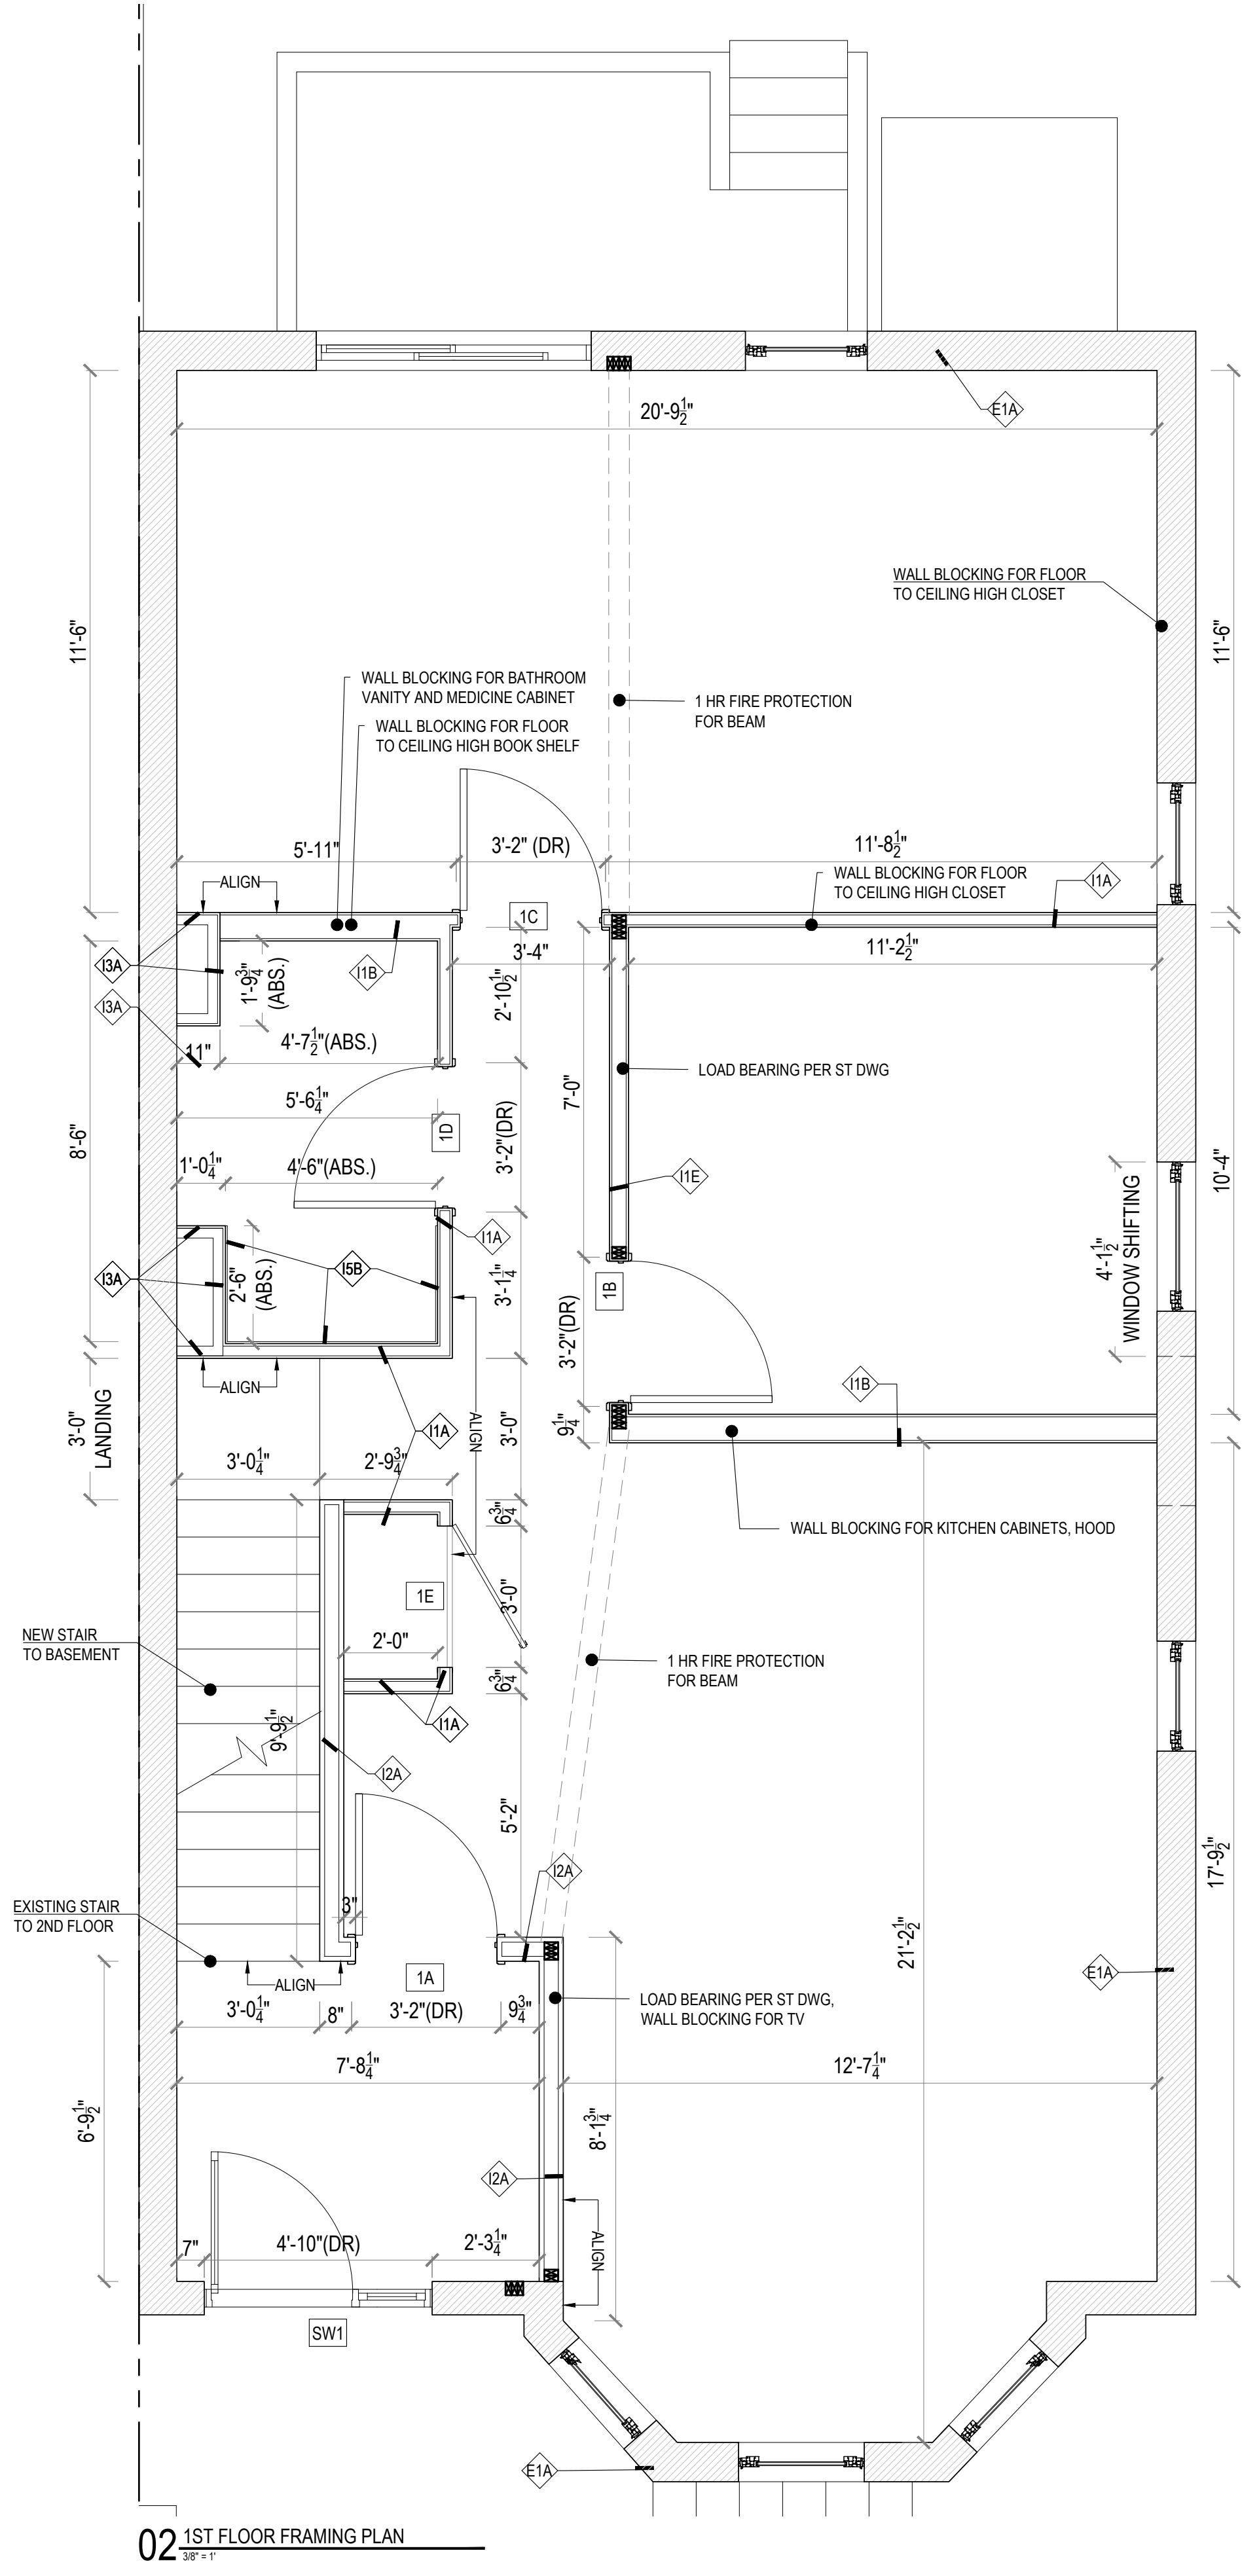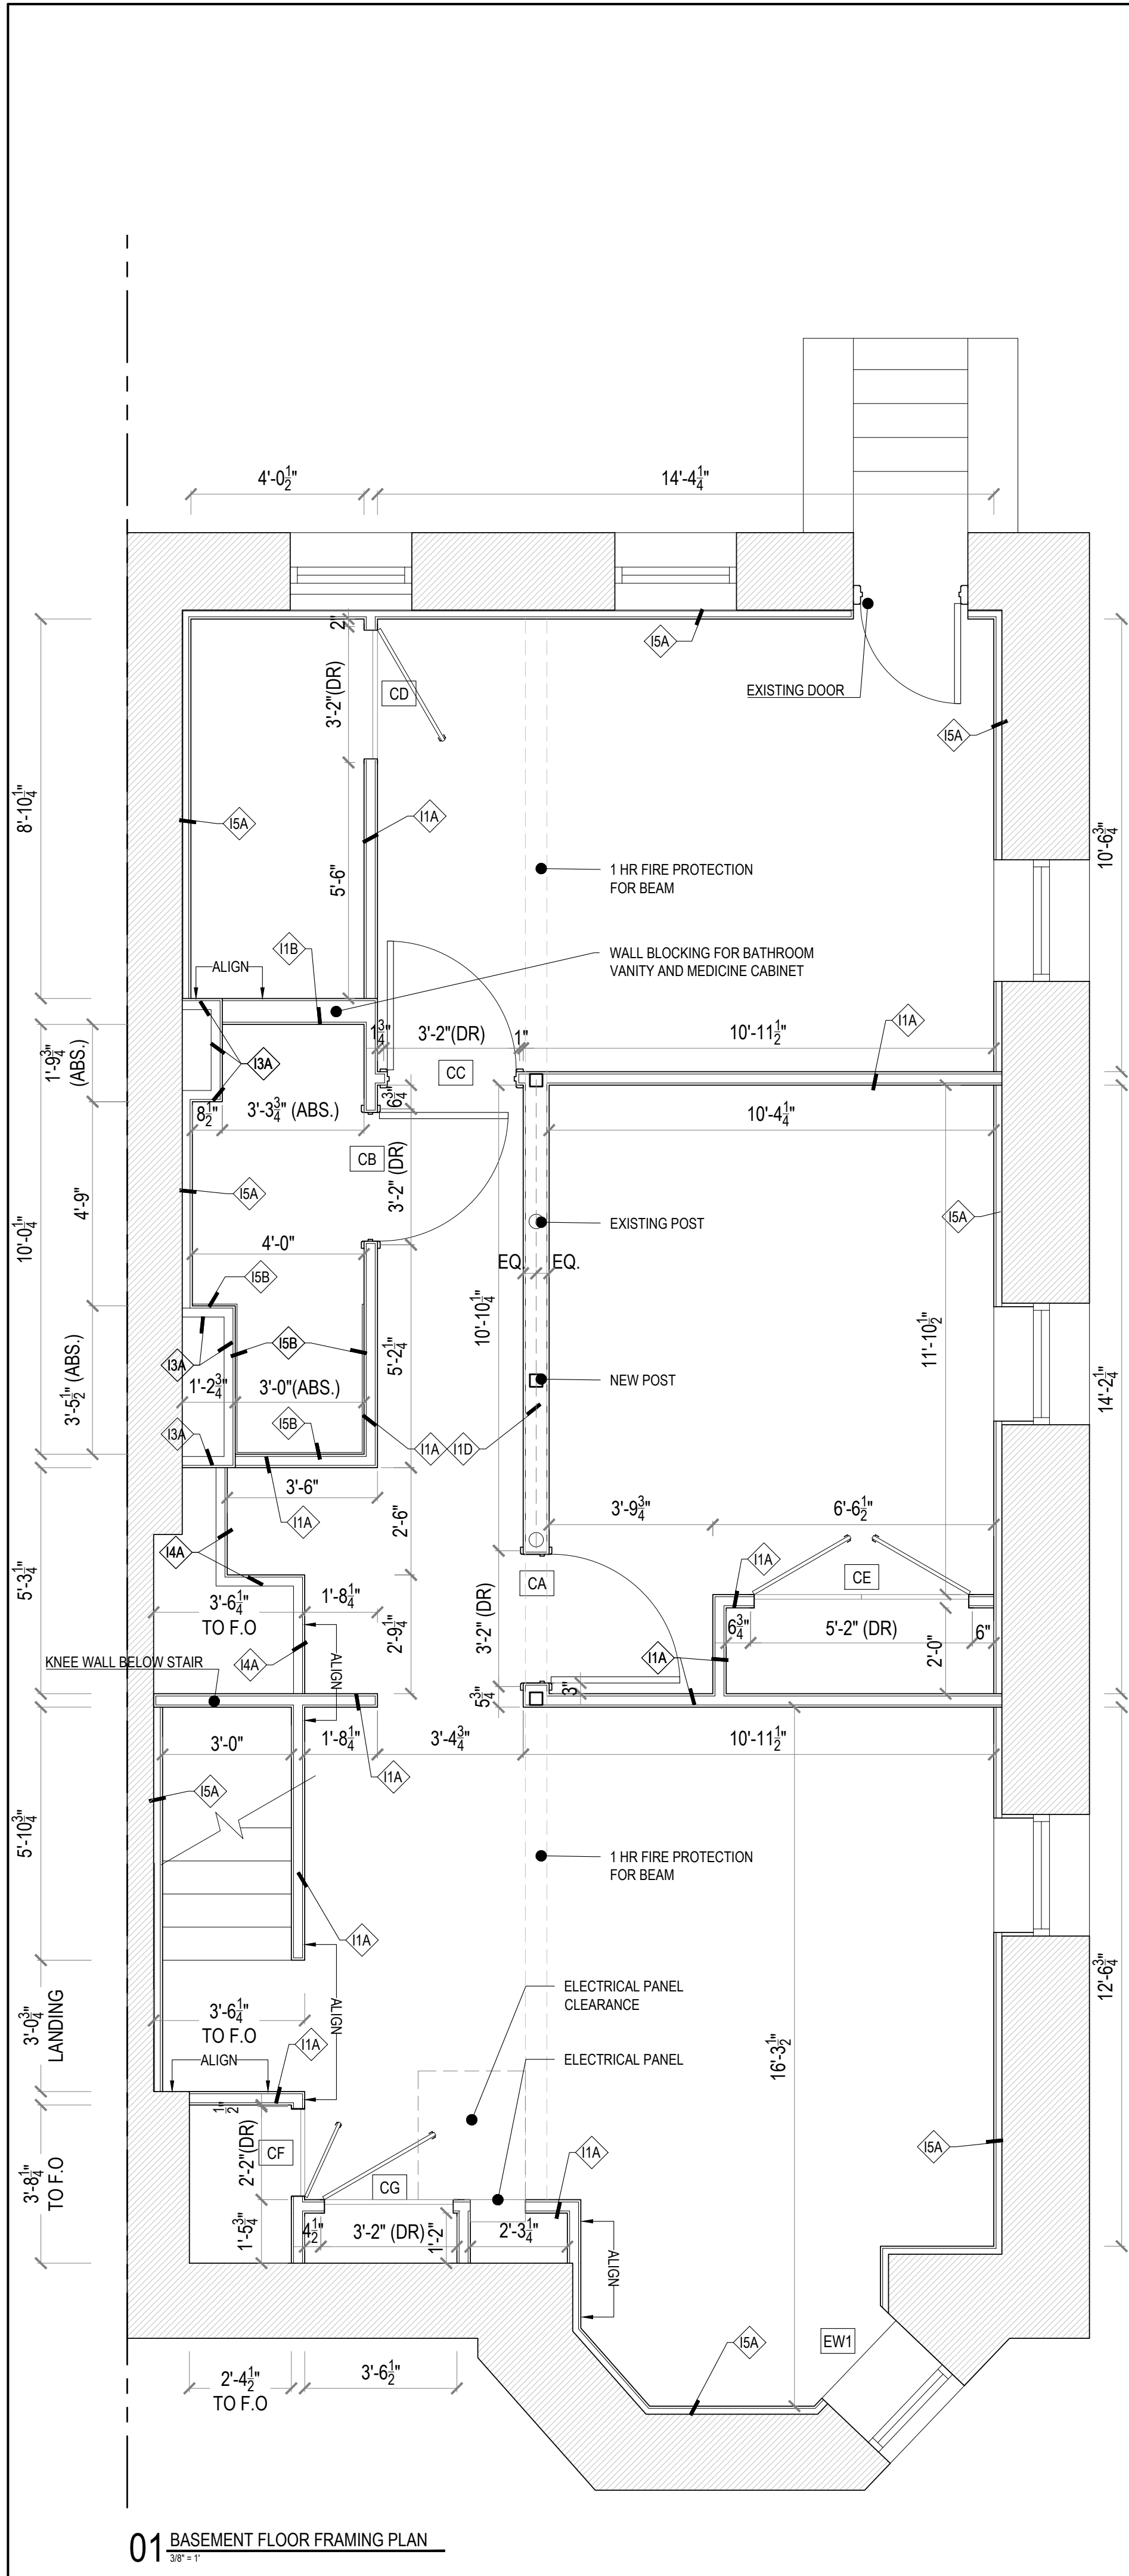

- FRAMING PLAN GENERAL NOTES
- ALL DIMENSIONS TO FACE OF GWB U.O.N. (SUCH AS FOUNDATION WALL(F.O), FACE OF CAST-IN-PLACE COMPONENTS (CIP), ETC)
 - DO NOT SCALE DRAWINGS. USE ONLY FIGURED DIMENSIONS. LARGE SCALE DRAWINGS TAKE PRECEDENCE OVER SMALL SCALE DRAWINGS
 - CONTRACTOR SHALL VERIFY ALL DIMENSIONS IN FIELD IF +/- DIMENSIONS VARY BY MORE THAN 1". NOTIFY ARCHITECT BEFORE PROCEEDING WITH WORK
 - CONTRACTOR TO REFER TO WALL SCHEDULES (A-010) FOR TYPES, UL SPEC, FIRE RATING AND SIZES
 - G.C. TO VERIFY COORDINATION OF SIZE AND LOCATION OF ALL HVAC OPENINGS IN FLOORS, WALLS, AND PLANKS WITH STRUCTURAL, MEP, AND SUBCONTRACTORS
 - ALL SHAFT WALLS TO BE 1HR RATED WALL TYPE I3A, UNLESS NOTED OTHERWISE. GC SHALL COORDINATE ALL ELECTRICAL AND AUDIO VISUAL CONNECTIONS WITH ELECTRICAL PLANS
 - PROVIDE MOP SINKS AND FLOOR DRAINS AS INDICATED
 - ALL ROUGH OPENINGS DIMENSIONS TO BE VERIFIED IN FIELD AGAINST EXISTING OVERALL DIMENSIONS
 - "HOLD" STANDS FOR ABSOLUTE DIMENSIONS TO BE HELD, G.C. TO ENSURE SITE DIMENSIONS MATCH
 - "DR" STANDS FOR DOOR ROUGH OPENING DIMENSION (2" + NOMINAL DOOR WIDTH)
 - "E.O.S." STANDS FOR EDGE OF SLAB
 - "CIP" STANDS FOR CAST-IN-PLACE CONCRETE
 - "D.W." STANDS FOR DEMISING WALL
 - "S.W." STANDS FOR SHEAR WALL
 - "C.W." STANDS FOR CHASE WALL
 - "F.O." STANDS FOR FOUNDATION WALL
 - "ABS" STANDS FOR ABSOLUTE DIMENSION. THIS IS THE 1ST PRIORITY TO BE FOLLOWED.
 - G.C. TO ENSURE ALL CORRIDORS HAVE A CLEAR WIDTH EQUAL OR HIGHER THAN 36" (3'-0") FINISH TO FINISH
 - 1HR SHAFT WALLS TO BE FRAMED AS PER WALL TAG ALL AROUND THE OPENING - WALL ENCLOSURE TO BE MAINTAINED AROUND OPENING
 - FRAMING DIMENSIONS GIVEN TO GWB / CEMENT BOARD LAYERS FRAMING DIMENSIONS SHOWN DO NOT INCLUDE BATHROOM TILE FINISH
 - ALL FOUNDATION WALL ELEMENTS TO HAVE WALL TYPE I5A FURRING (2.25" THICKNESS), UNLESS NOTED OTHERWISE

PROJECT 143

213 MAPLE STREET

213 MAPLE STREET, WEEHAWKEN, NEW JERSEY 07086

CONSULTANTS:

STRUCTURAL ENGINEER
FLEX ENGINEERING GROUP LLC
3133 CENTRAL AVE #202, UNION CITY, NJ 07087
T: 201-974-9570
E: flexengineer@yahoo.com

MECHANICAL ENGINEER
FLEX ENGINEERING GROUP LLC
3133 CENTRAL AVE #202, UNION CITY, NJ 07087
T: 201-974-9570
E: flexengineer@yahoo.com

GENERAL CONTRACTOR
HOBOKEN KITCHEN & BATH
2 14TH ST PH 32, HOBOKEN NJ, 07030
T: 201-472-0425
E: hkbath@hobokenkitchenandbath.com

#	DATE	DESCRIPTION
---	------	-------------

DOB STAMP AND SIGNATURE

SEAL AND SIGNATURE

CONTRACTORS SHALL ONLY UTILIZE WRITTEN DIMENSIONS. CONTRACTORS SHALL VERIFY AND BE RESPONSIBLE FOR ALL DIMENSIONS AND CONDITIONS ON THE JOB. OWNER MUST BE NOTIFIED OF ANY VARIATIONS FROM DIMENSIONS AND CONDITIONS SHOWN BY THESE DRAWINGS. ALL SHOP DRAWINGS MUST BE SUBMITTED TO OWNER FOR APPROVAL BEFORE PROCEEDING WITH ANY FABRICATION.



ALL DRAWINGS, SPECIFICATIONS, ETC. DISTRIBUTED TO CONTRACTORS, BOODERS, GOVERNMENTAL AGENCIES ETC. ARE NOT FOR GENERAL USE OR PUBLICATION BY OTHERS. ALL RIGHTS RESERVED. NONE OF THE IDEAS, DESIGN, INFORMATION OR PLANS IN THIS DRAWING SHALL BE USED BY OR DISCLOSED TO ANY PERSONS, FIRM OR CORPORATION FOR ANY PURPOSE WITHOUT THE WRITTEN PERMISSION OF OWNER.

DRAWING TITLE:
FRAMING PLANS

FOR CONSTRUCTION


A-104.00

GENERAL CONTRACTOR
HOBOKEN KITCHEN & BATH
2 14TH ST PH 32, HOBOKEN, NJ, 07030
T: 201-472-0425
E: thodore@hobokenkitchenandbath.com

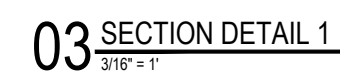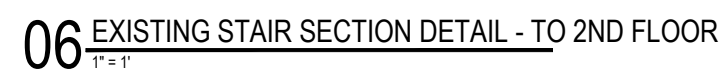


A-110.00


ALL MILLWORK CABINETRY MATERIAL AND INSTALLATION BY OWNER
IN WALL WOOD BLOCKING FOR ALL CABINETY BY HKB

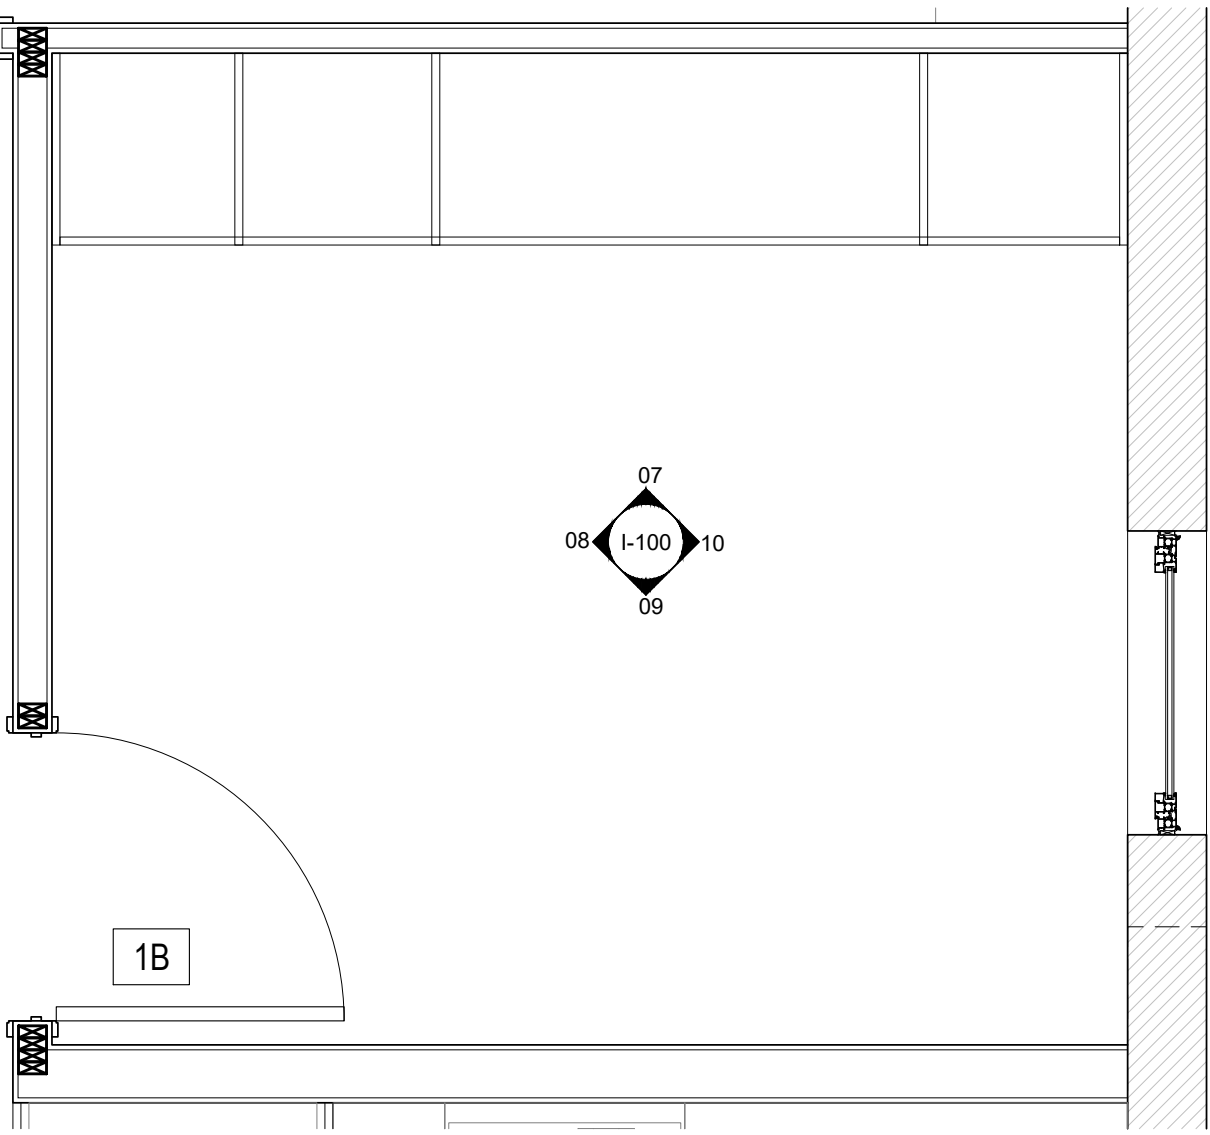


06 FIRST FLOOR GUEST BEDROOM ENLARGED PLAN
1/2" = 1'

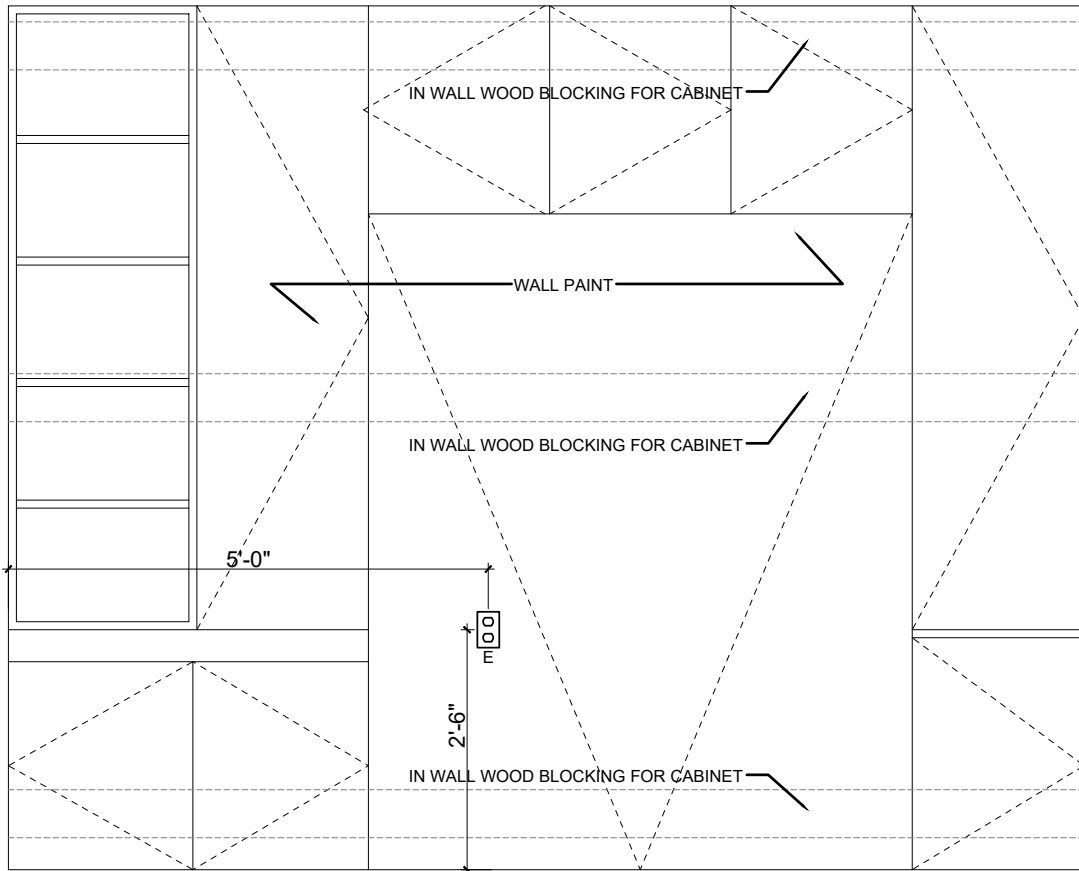


07 FIRST FLOOR GUEST BEDROOM SOUTH ELEVATION
1/2" = 1'

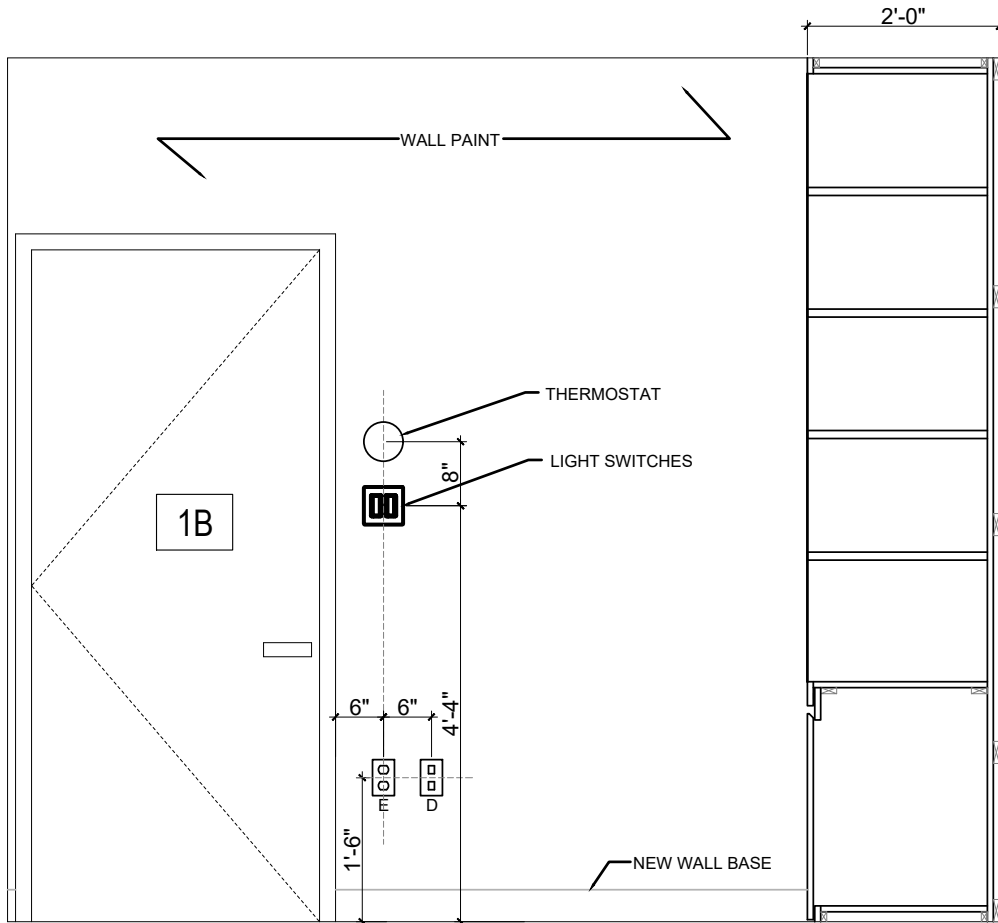


08 FIRST FLOOR GUEST BEDROOM EAST ELEVATION
1/2" = 1'

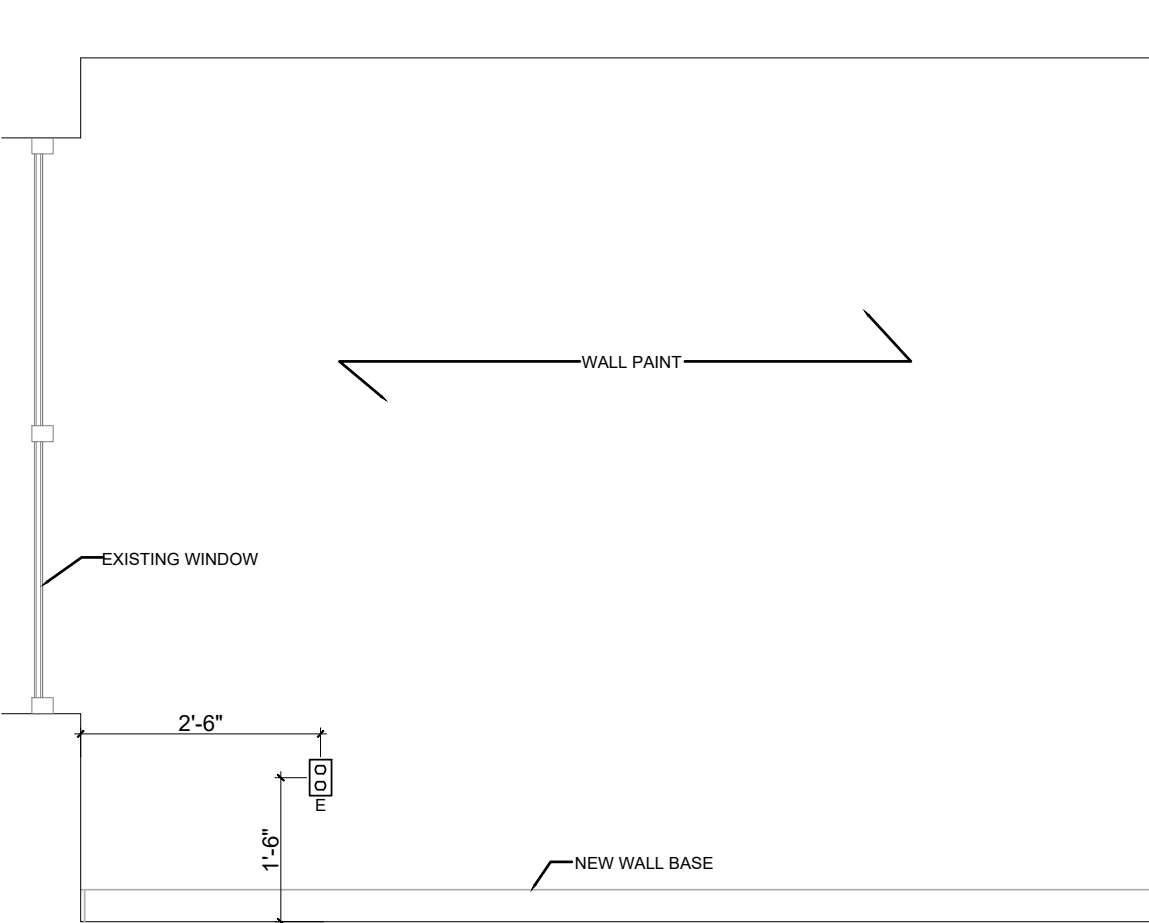


09 FIRST FLOOR GUEST BEDROOM NORTH ELEVATION
1/2" = 1'

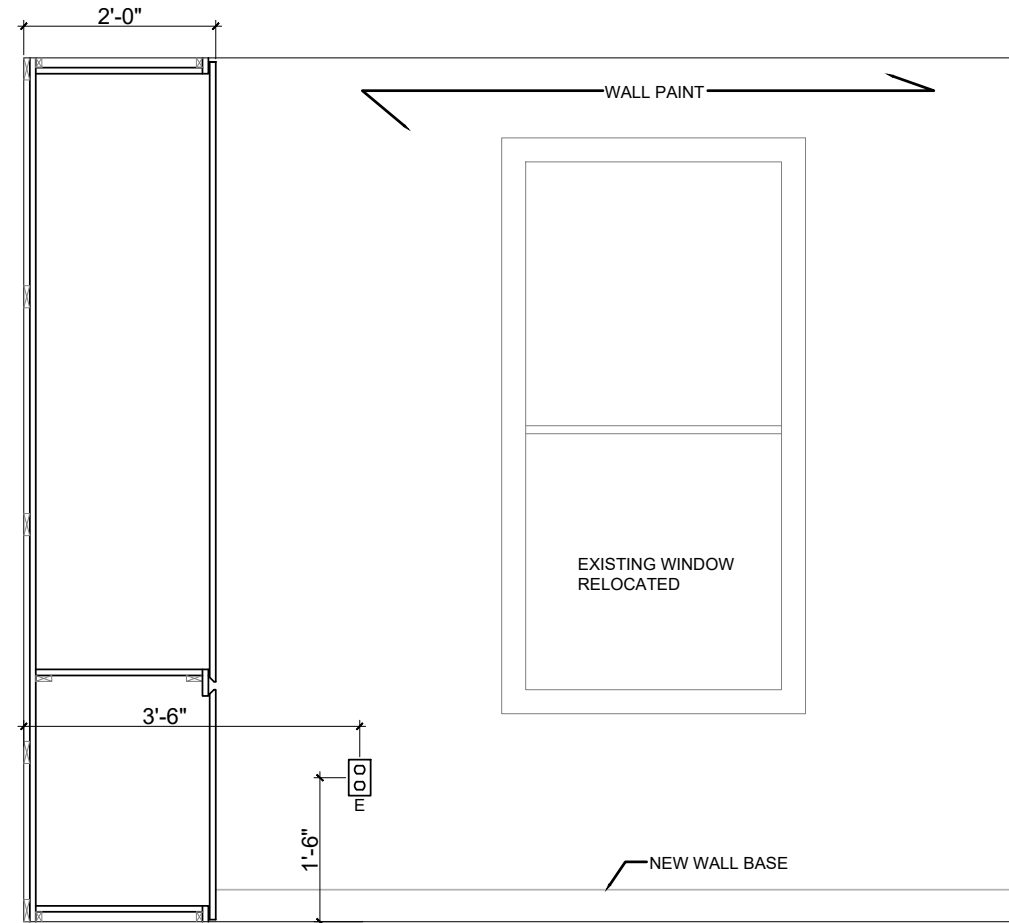


10 FIRST FLOOR GUEST BEDROOM WEST ELEVATION
1/2" = 1'

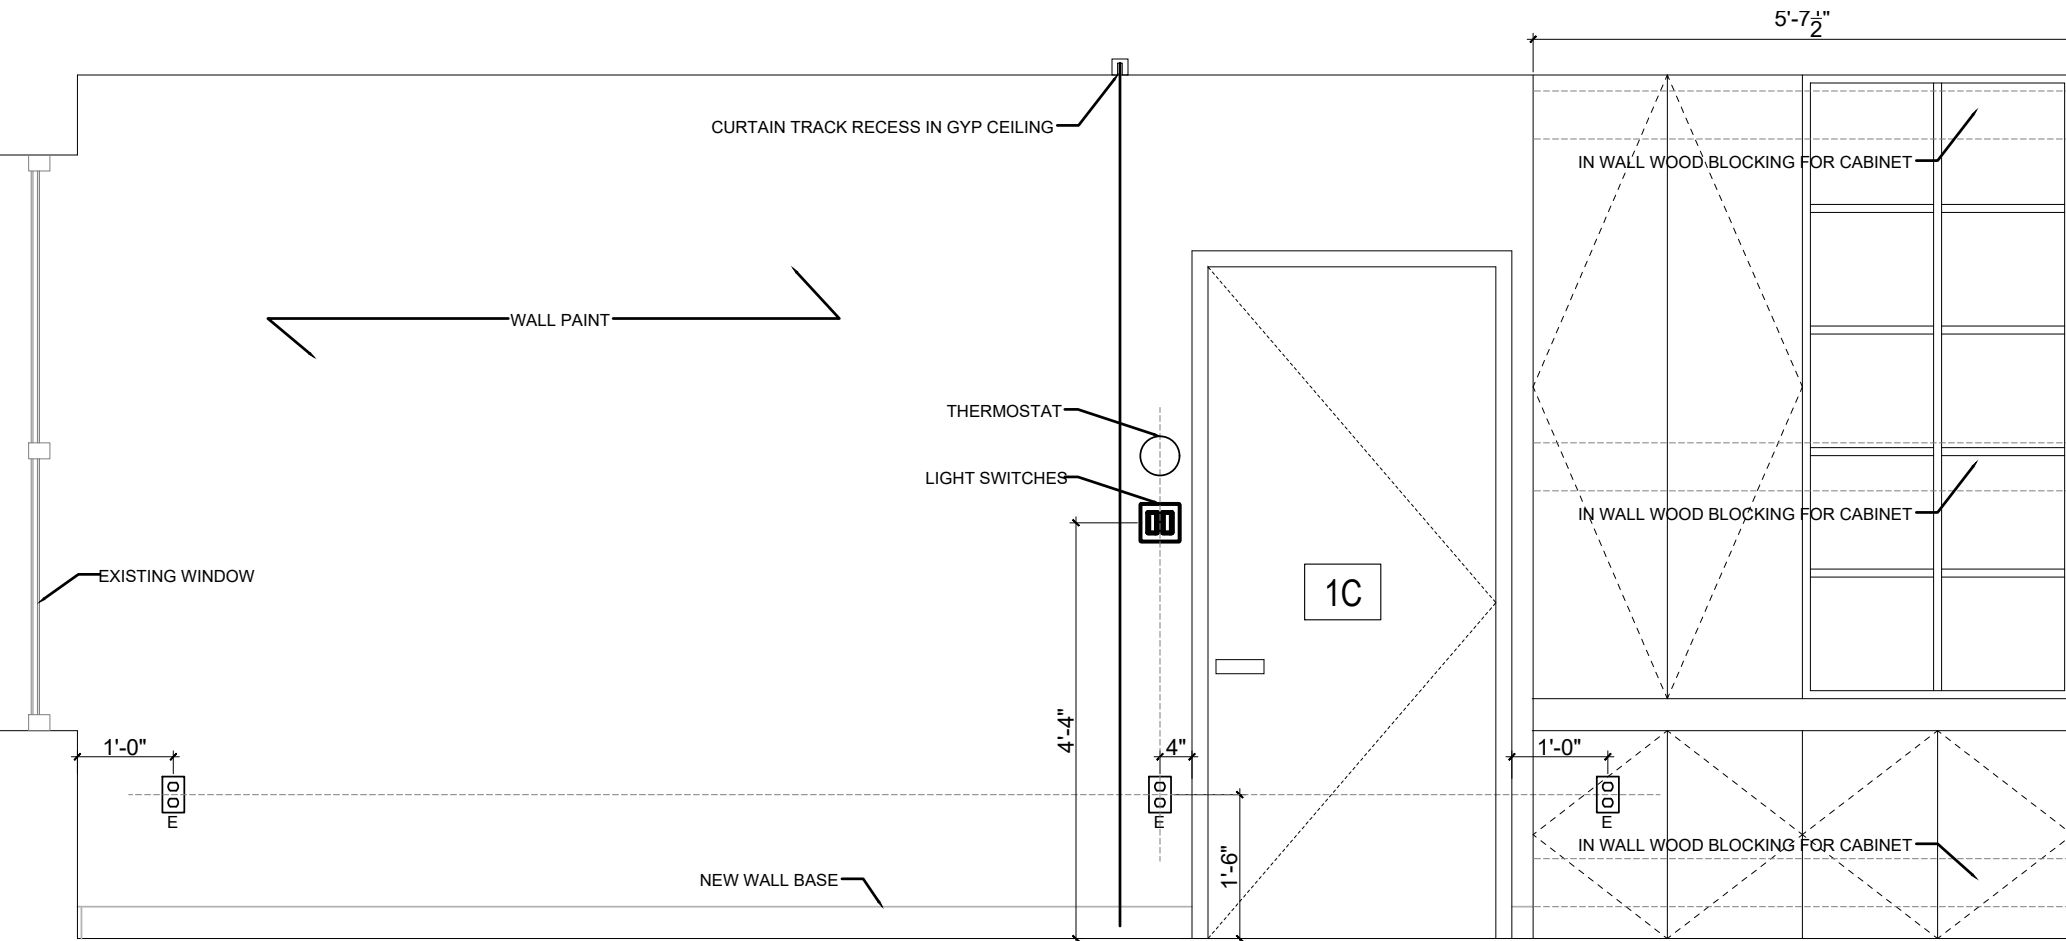


04 FIRST FLOOR MASTER BEDROOM NORTH ELEVATION
1/2" = 1'

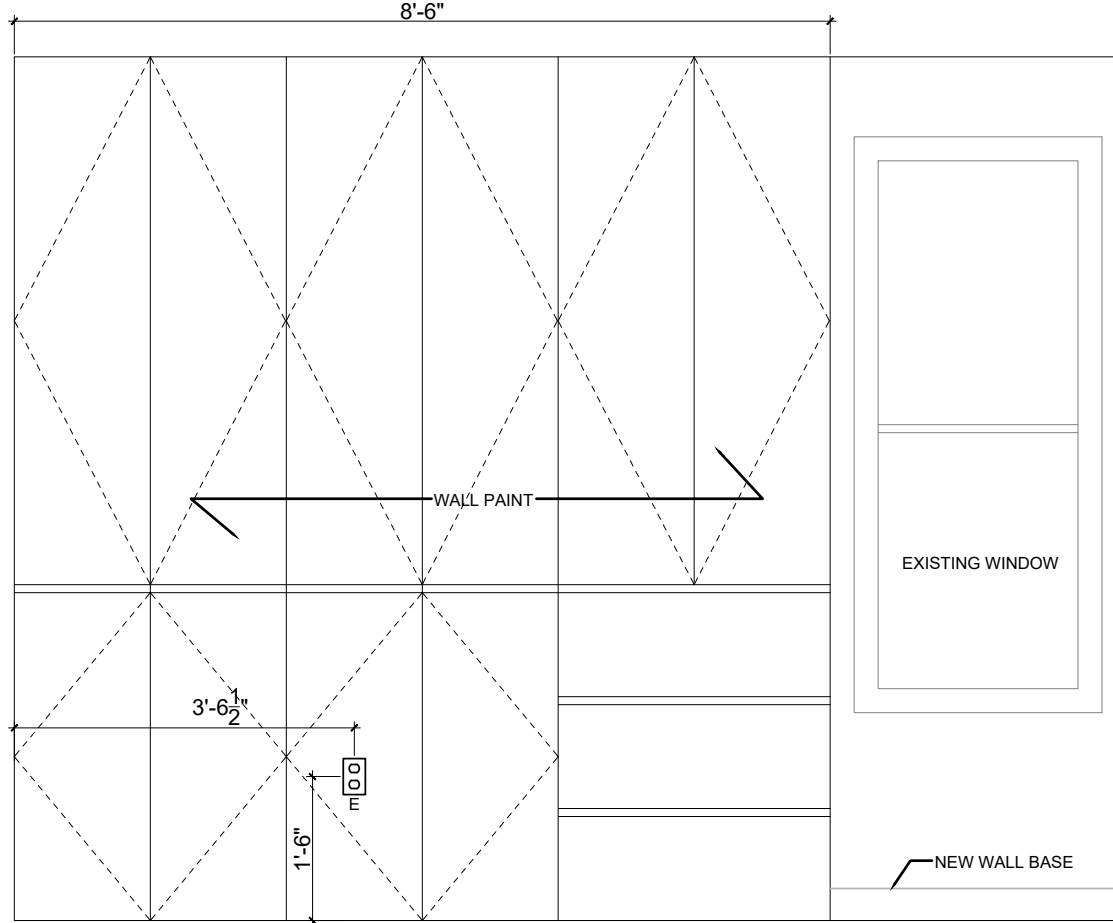


05 FIRST FLOOR MASTER BEDROOM WEST ELEVATION
1/2" = 1'

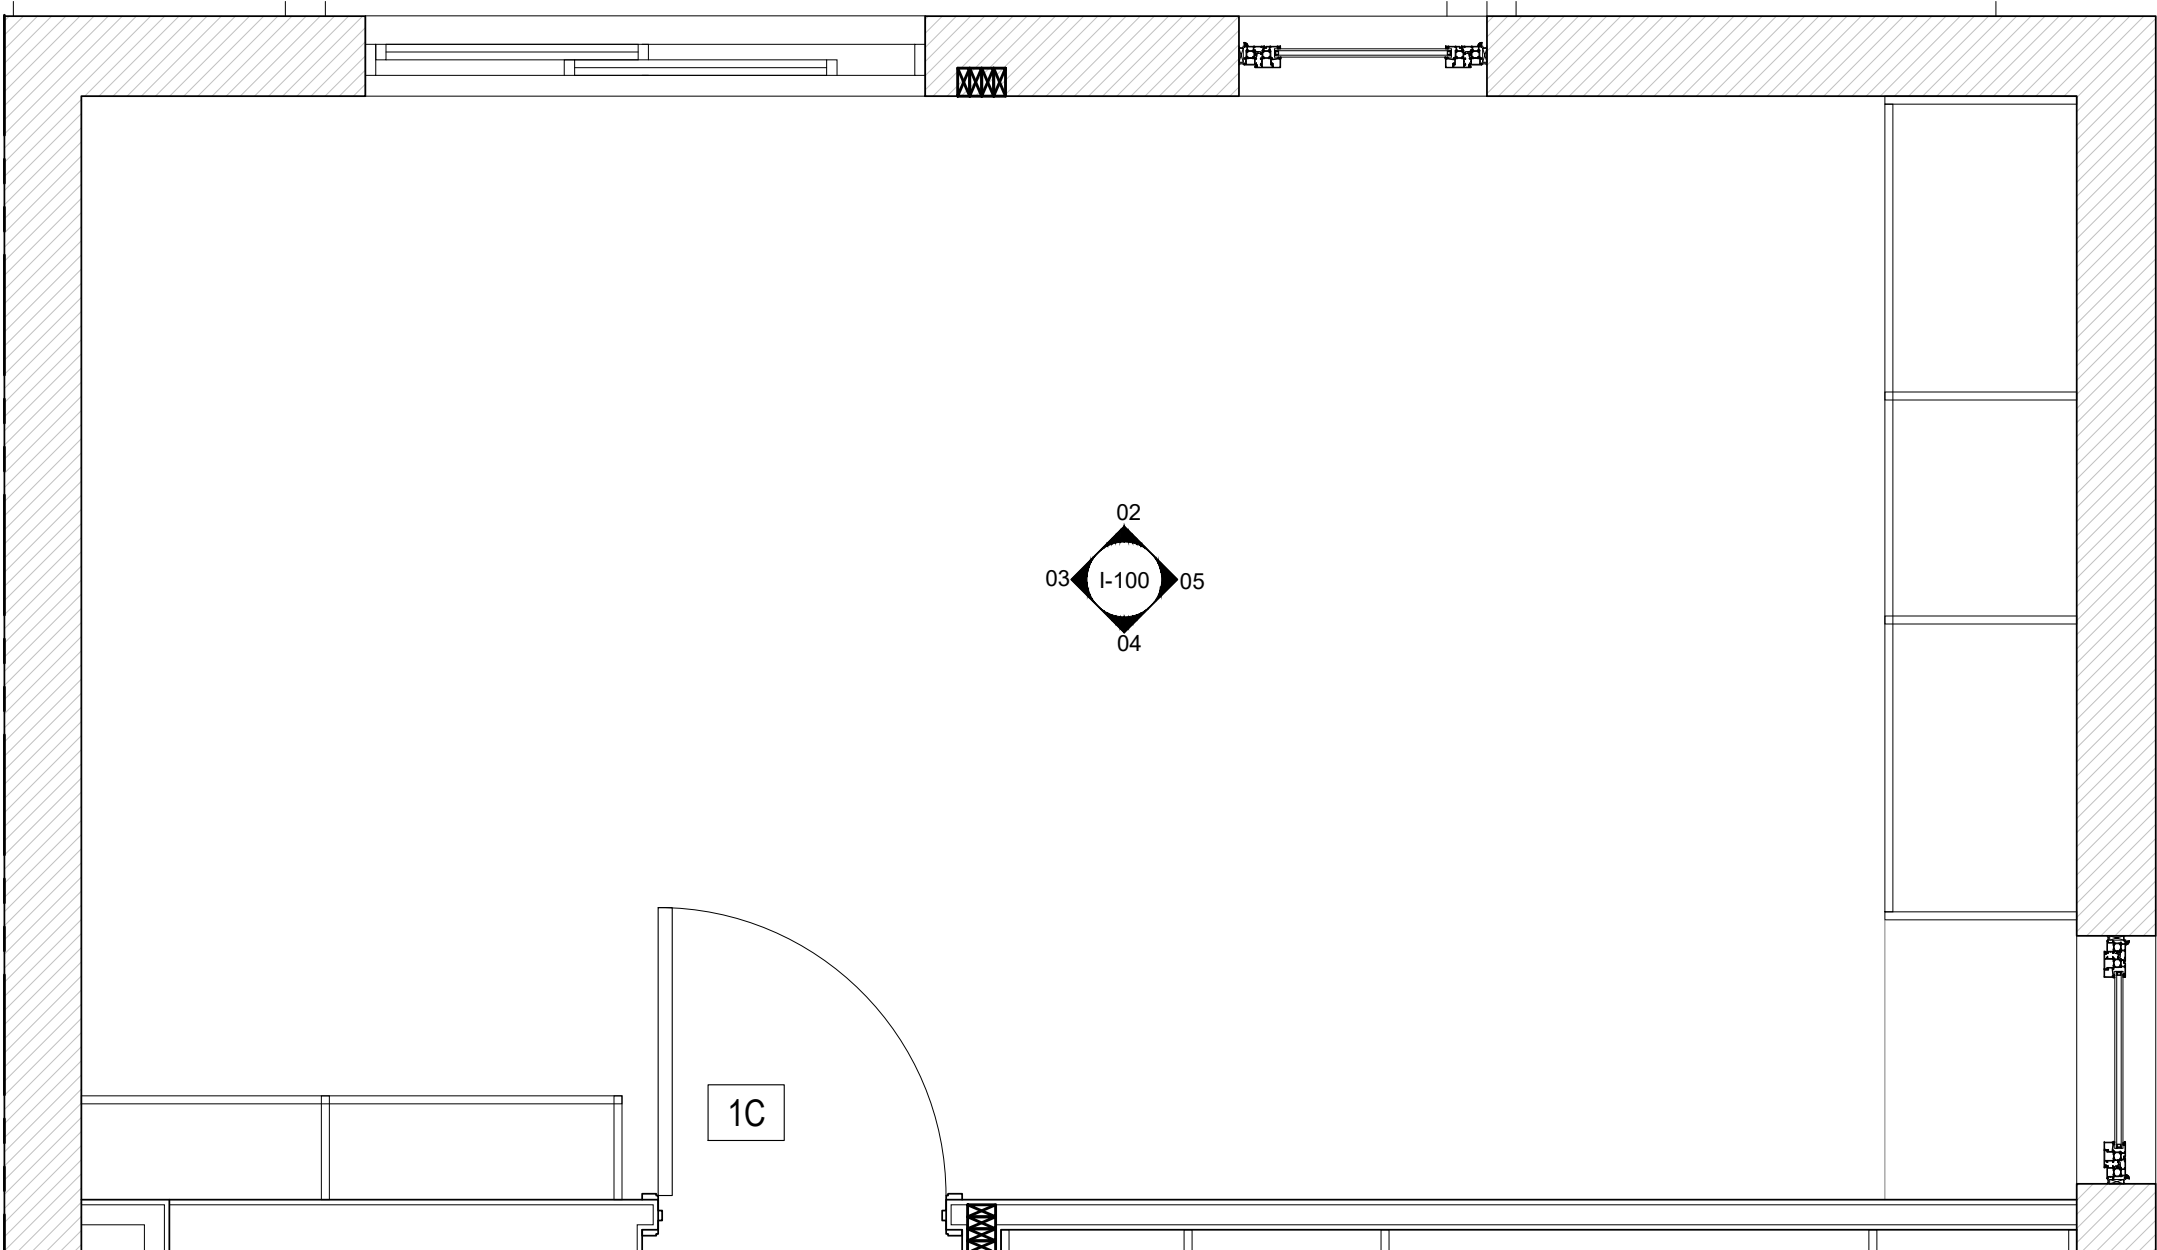

01 FIRST FLOOR MASTER BEDROOM ENLARGED PLAN
1/2" = 1'

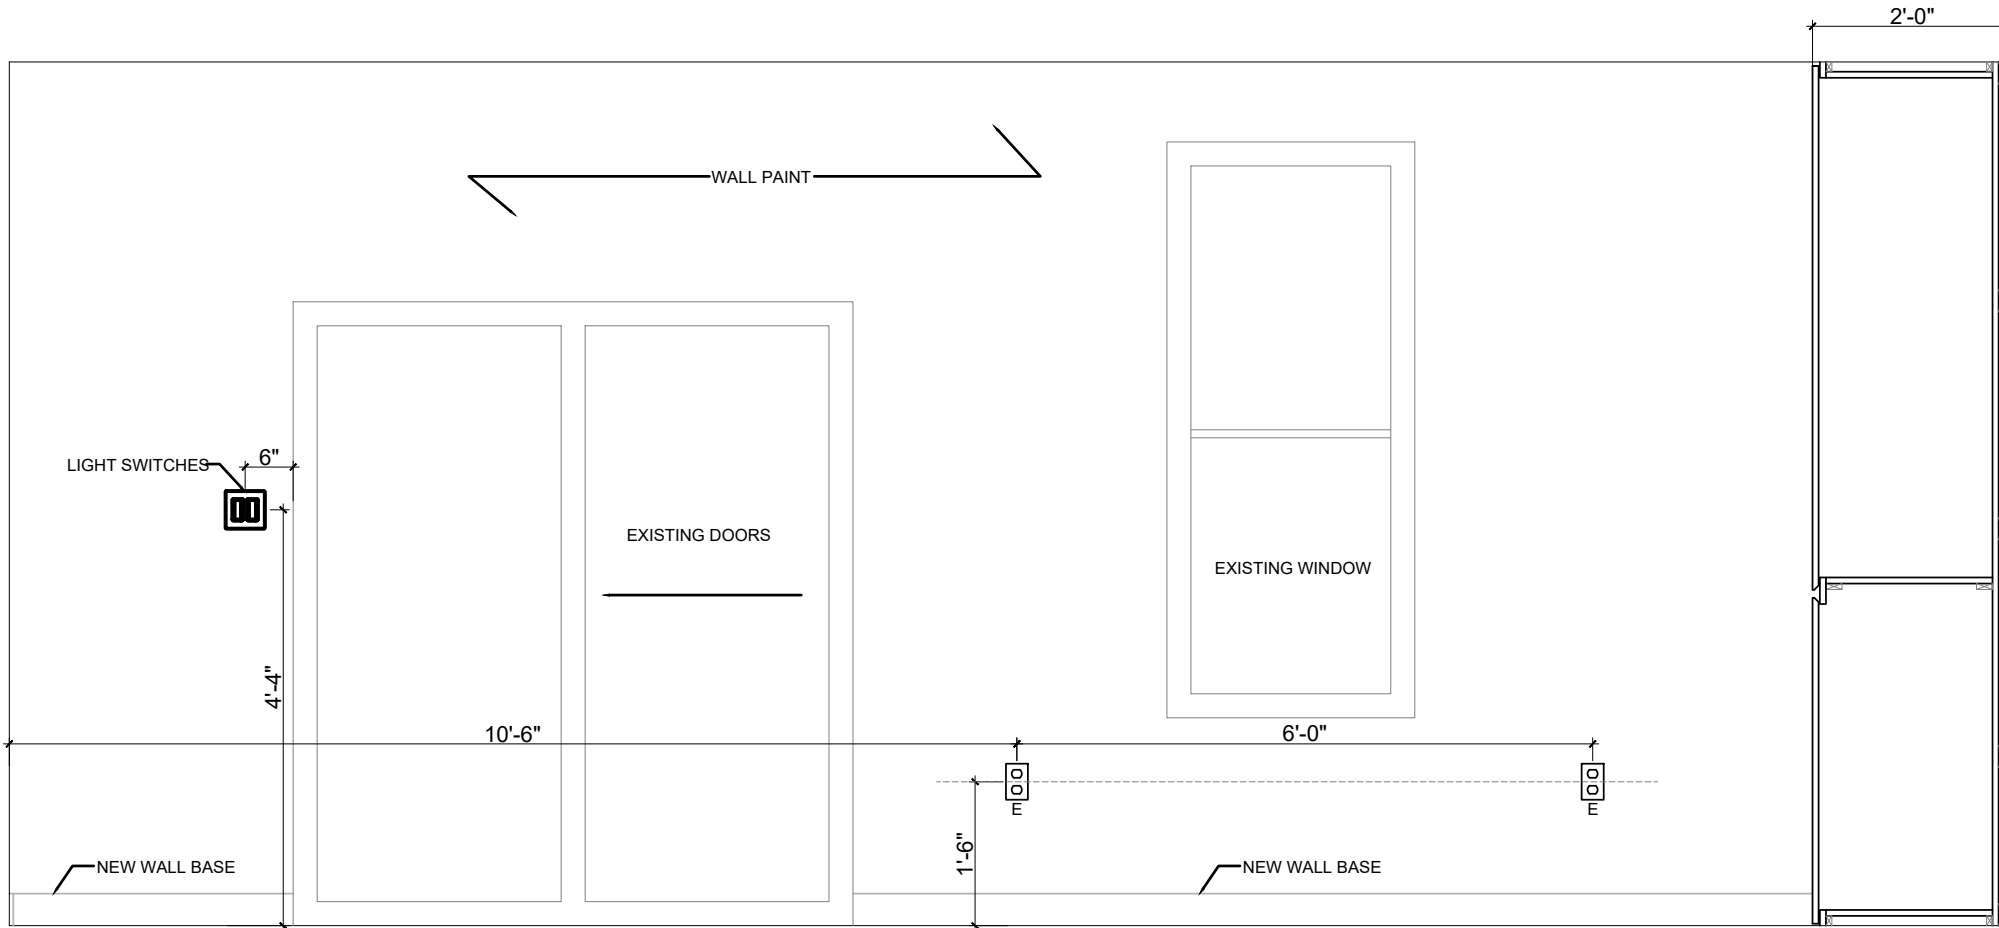

02 FIRST FLOOR MASTER BEDROOM SOUTH ELEVATION
1/2" = 1'

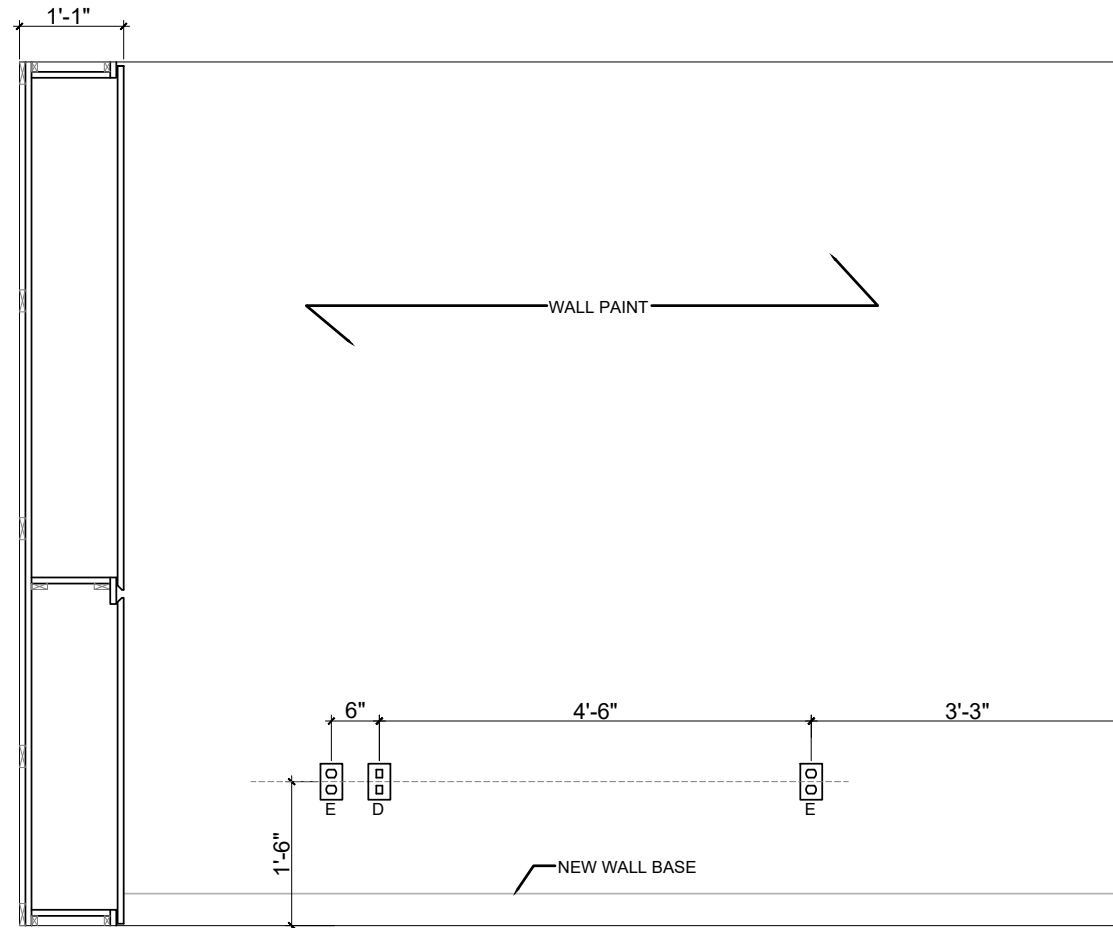

03 FIRST FLOOR MASTER BEDROOM EAST ELEVATION
1/2" = 1'

PROJECT 103

213 MAPLE STREET

213 MAPLE STREET, WEHAWKEN, NEW JERSEY, 07086

CONSULTANTS:

STRUCTURAL ENGINEER
FLEX ENGINEERING GROUP LLC
3133 CENTRAL AVE #202, UNION CITY, NJ 07087
T: 201-974-9570
E: flexengr@flexengr.com

MECHANICAL ENGINEER
FLEX ENGINEERING GROUP LLC
3133 CENTRAL AVE #202, UNION CITY, NJ 07087
T: 201-974-9570
E: flexengr@flexengr.com

GENERAL CONTRACTOR
HOBOKEN KITCHEN & BATH
2 14TH ST PH 32, HOBOKEN NJ, 07030
T: 201-472-9425
E: hkb@hobokenkitchenandbath.com

DATE DESCRIPTION

DOB STAMP AND SIGNATURE

SEAL AND SIGNATURE

CONTRACTOR SHALL ONLY UTILIZE WRITTEN DIMENSIONS. CONTRACTOR SHALL VERIFY AND BE RESPONSIBLE FOR ALL DIMENSIONS AND CONDITIONS ON THE JOB, AND OWNER MUST BE NOTIFIED OF ANY VARIATIONS FROM DIMENSIONS AND CONDITIONS SHOWN BY THESE DRAWINGS. SCALED SHOP DRAWINGS MUST BE SUBMITTED TO OWNER FOR APPROVAL BEFORE PROCEEDING WITH ANY FABRICATION.


ALL DRAWINGS, SPECIFICATIONS, ETC. CONTRIBUTED TO CONTRACTORS, BIDDERS, GOVERNMENT AGENCIES, ETC. ARE NOT FOR GENERAL USE OR PUBLICATION BY OTHERS. ALL RIGHTS RESERVED. NONE OF THE DESIGN, ARRANGEMENTS OR PLANS IN THESE DRAWINGS SHALL BE USED BY OR DISCLOSED TO ANY PERSONS, FIRM OR CORPORATION FOR ANY PURPOSE WITHOUT THE WRITTEN PERMISSION OF OWNER.

DRAWING TITLE:


I-100
INTERIOR ELEVATION -
FIRST FLOOR

FOR CONSTRUCTION


ALL MILLWORK CABINETRY MATERIAL AND INSTALLATION BY OWNER
IN WALL WOOD BLOCKING FOR ALL CABINETRY BY HKB

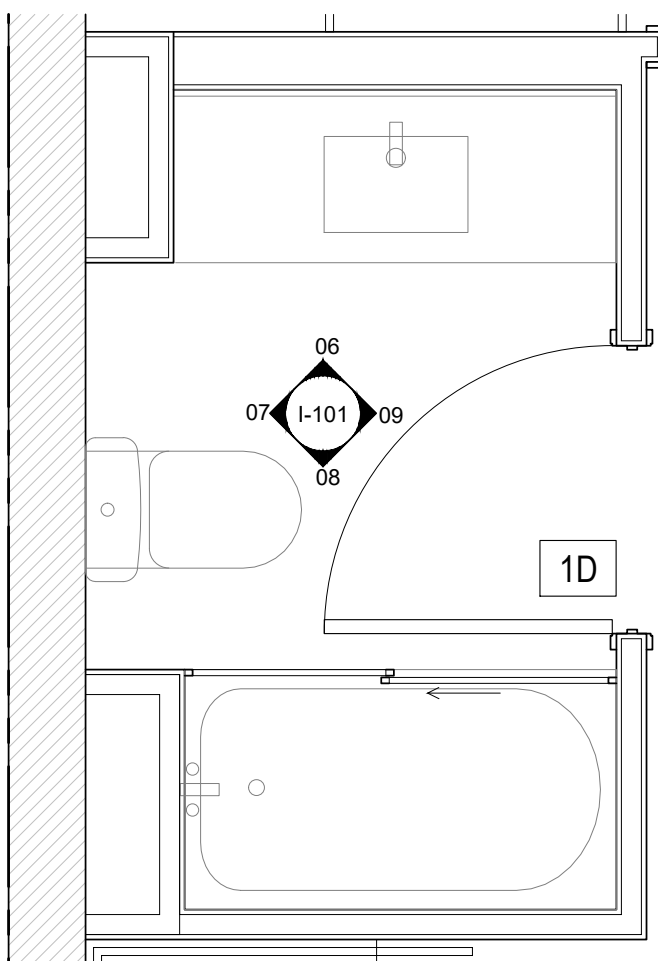


05 FIRST FLOOR TOILET ENLARGED PLAN
1/12" = 1'

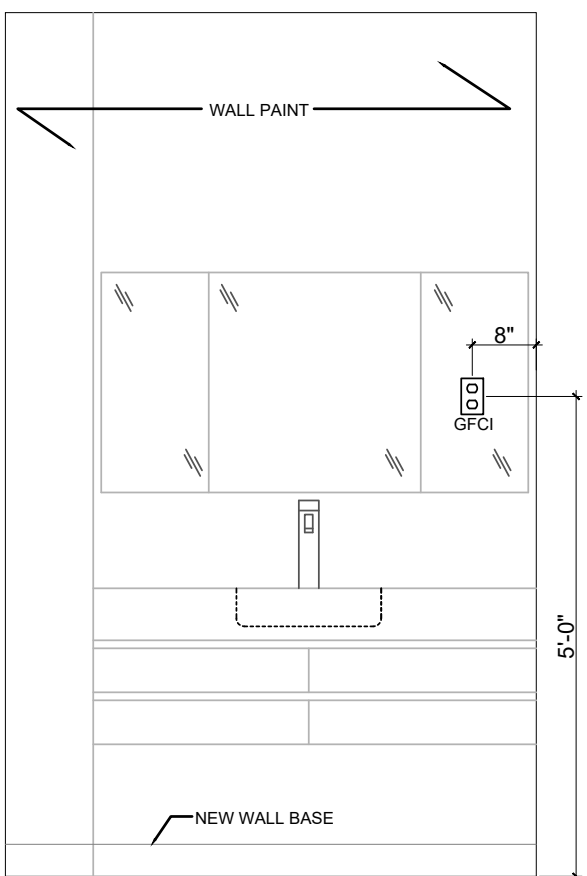


06 FIRST FLOOR TOILET SOUTH ELEVATION
1/12" = 1'

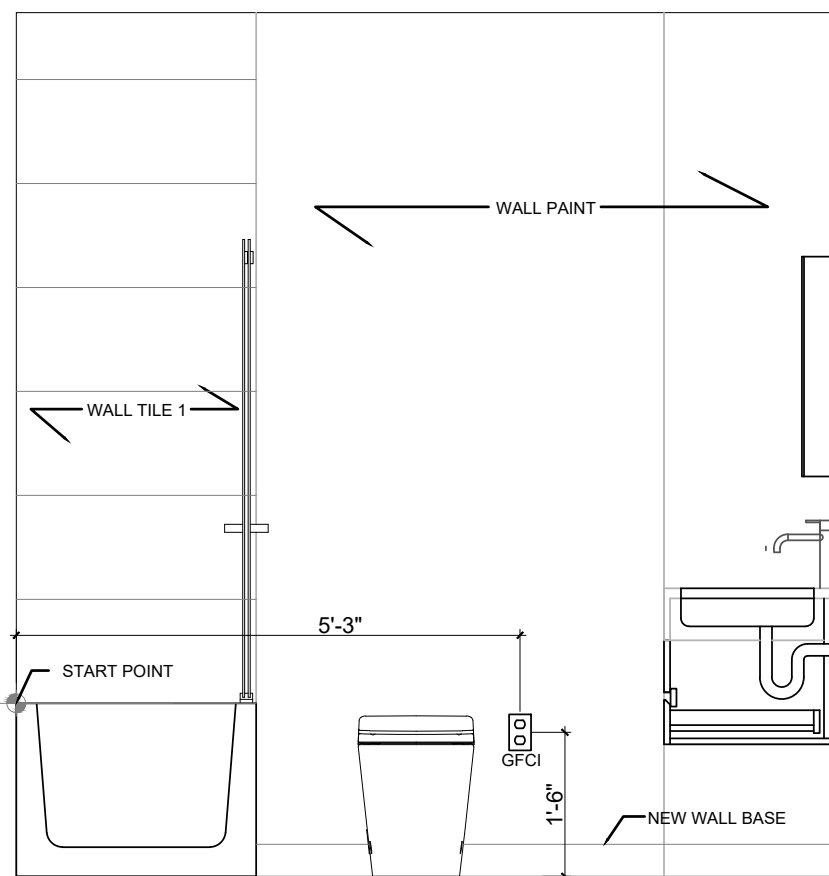


07 FIRST FLOOR TOILET EAST ELEVATION
1/12" = 1'

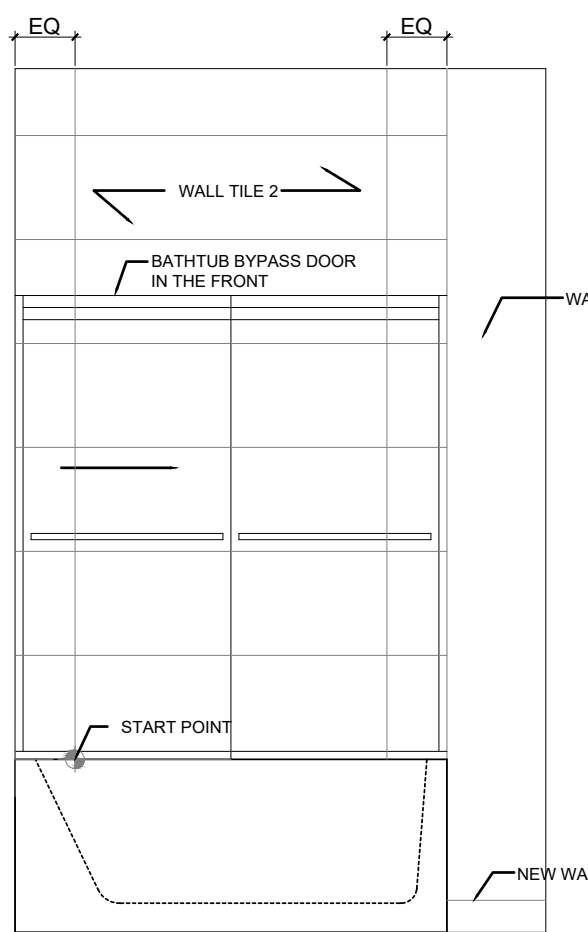


08 FIRST FLOOR TOILET NORTH ELEVATION
1/12" = 1'

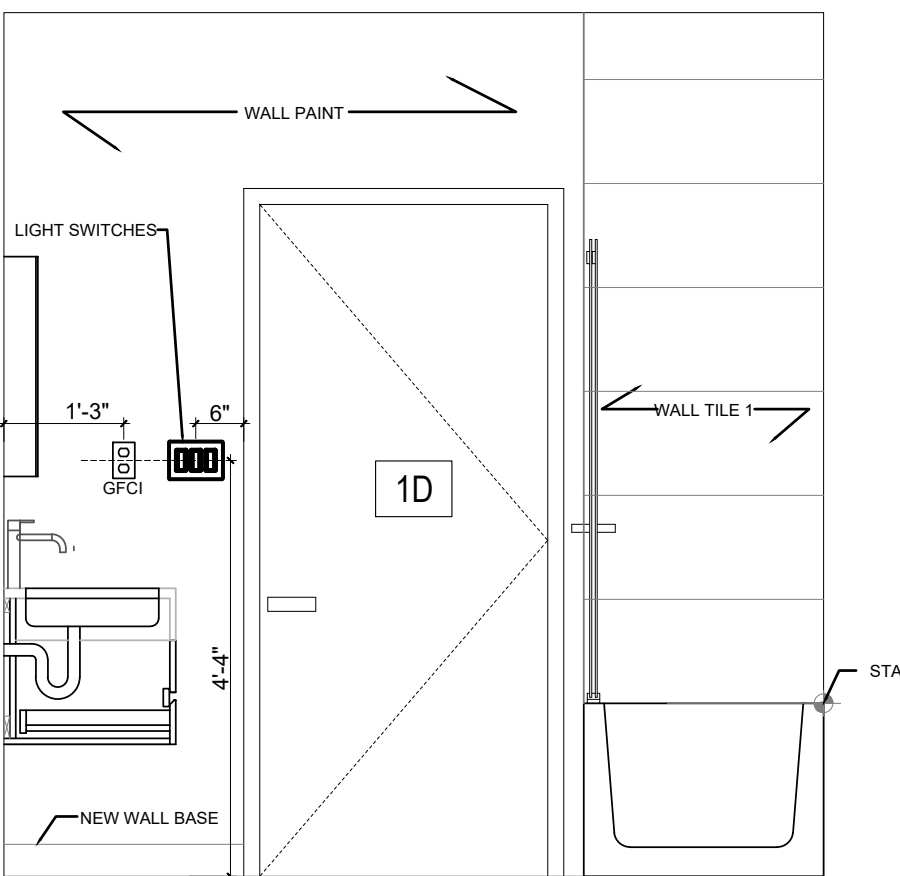


09 FIRST FLOOR TOILET EAST ELEVATION
1/12" = 1'

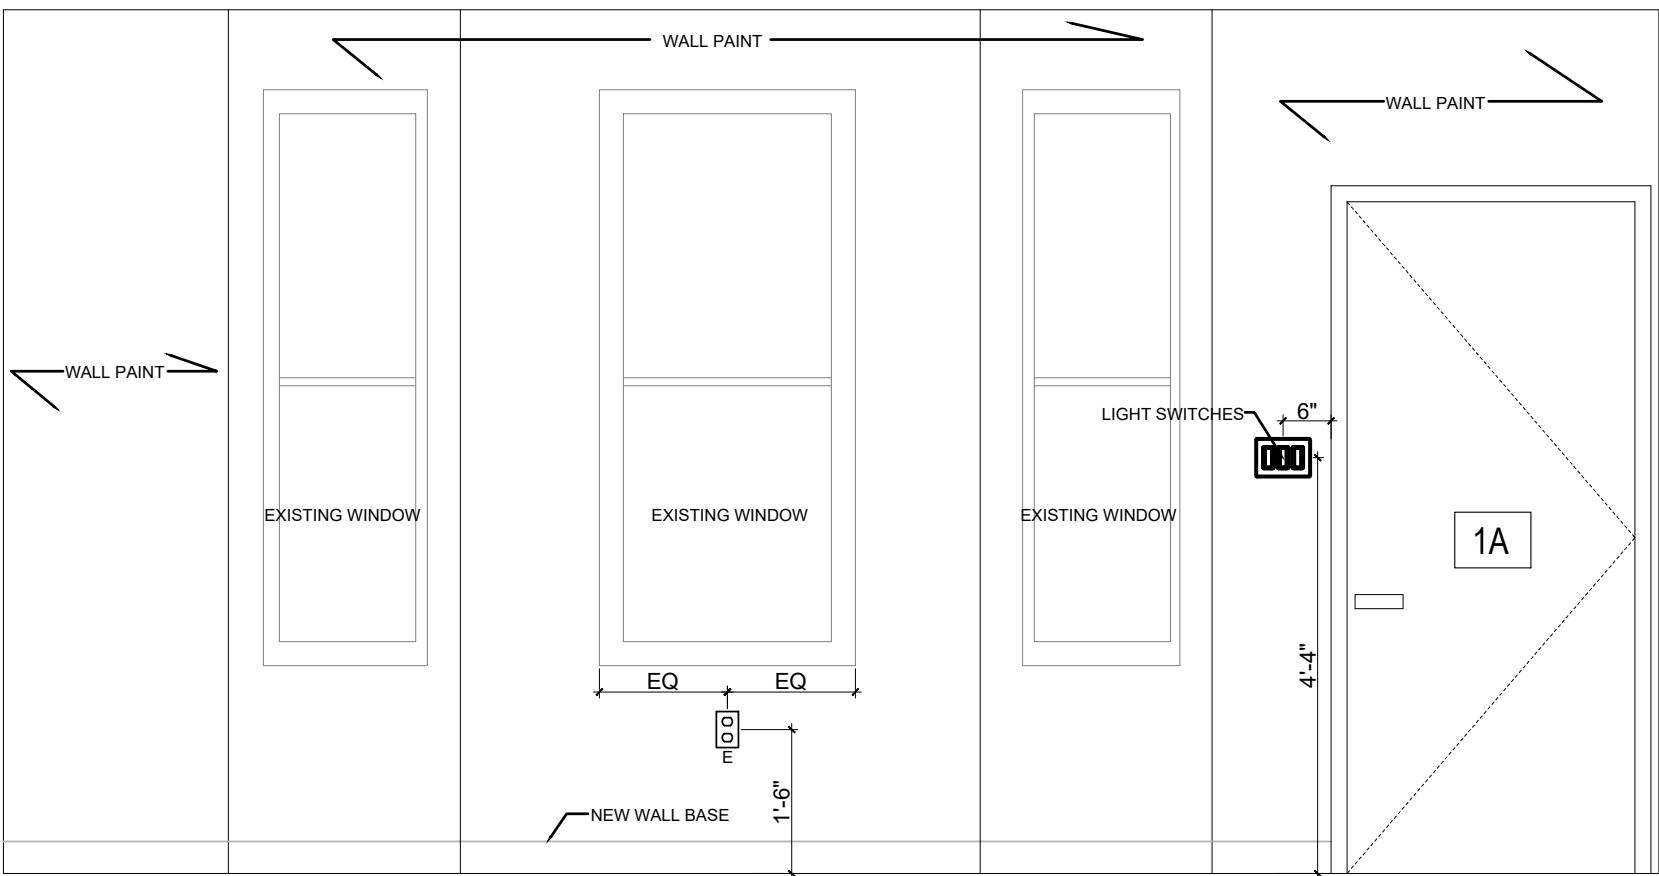


03 FIRST FLOOR LIVING ROOM & KITCHEN NORTH ELEVATION
1/12" = 1'

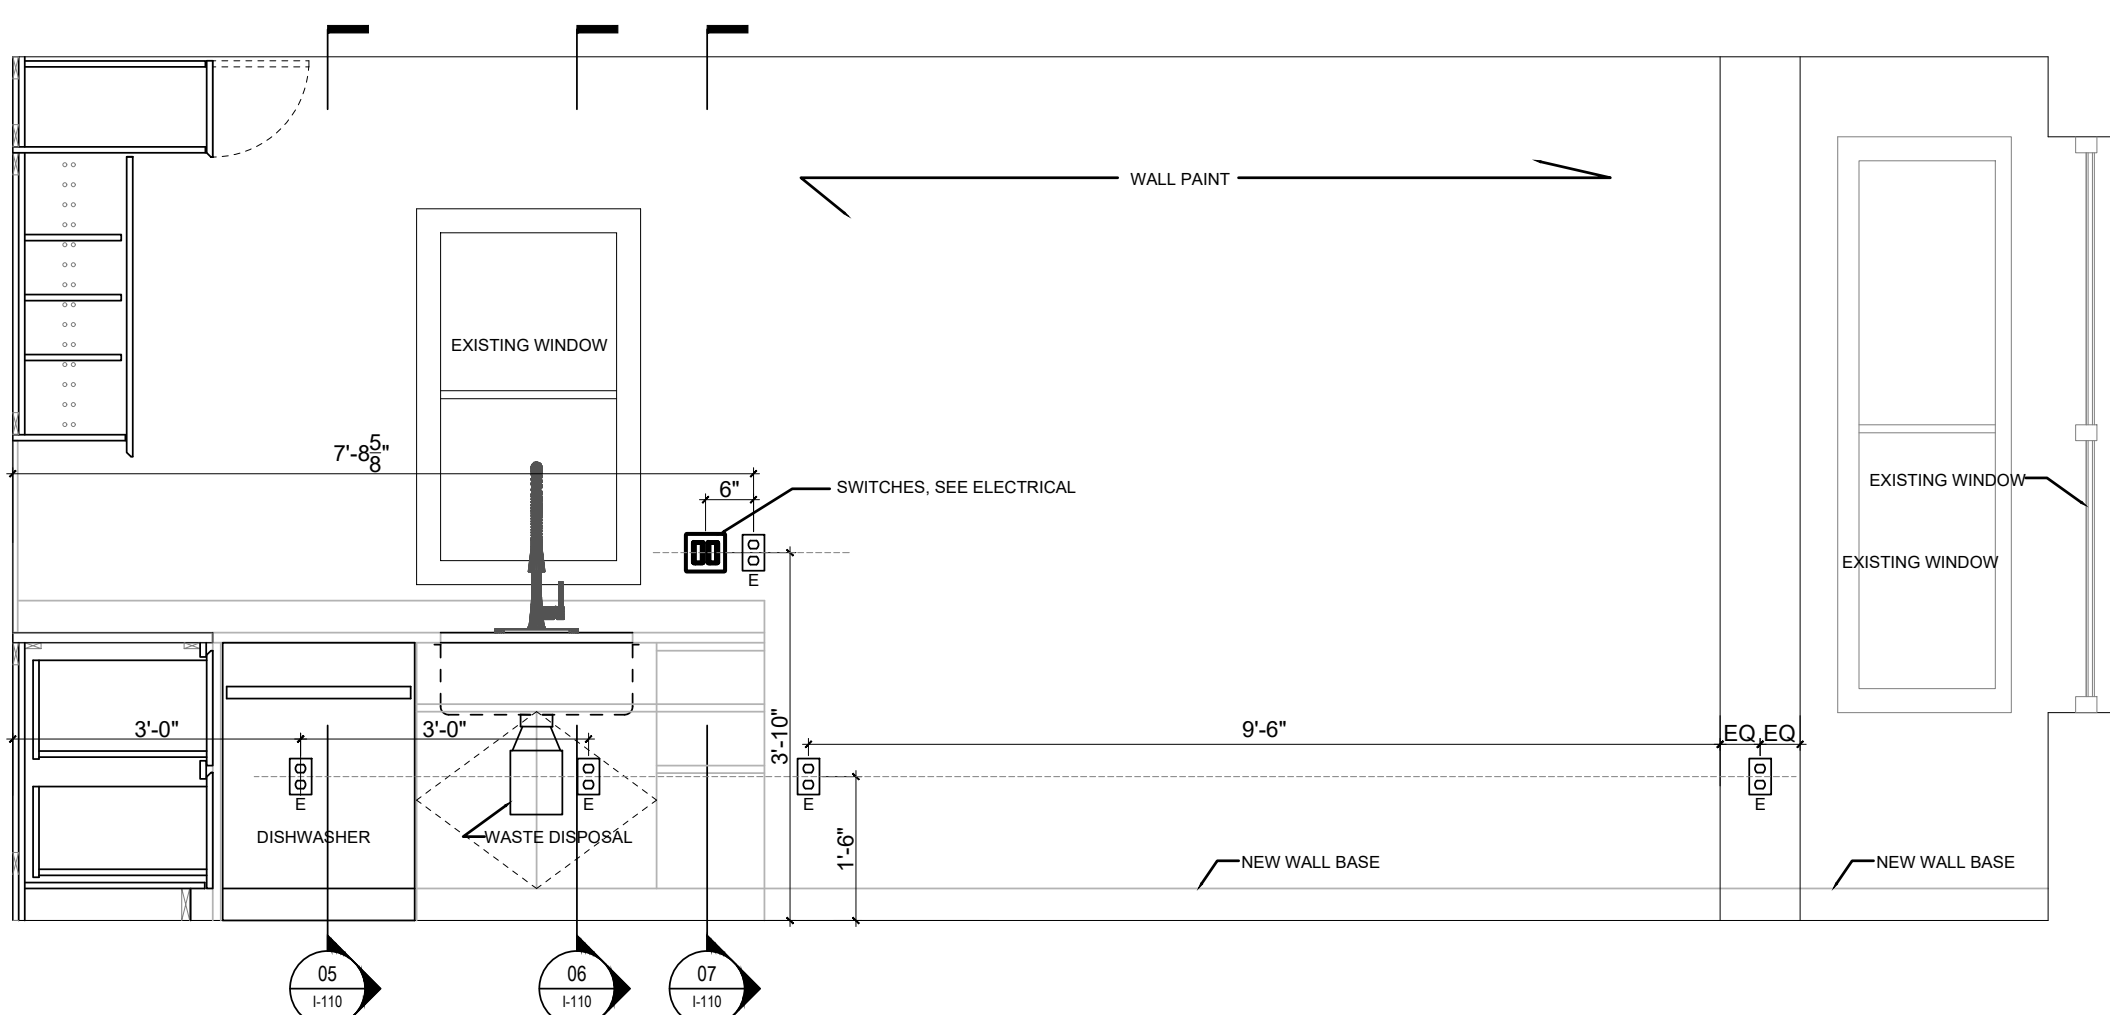

04 FIRST FLOOR LIVING ROOM & KITCHEN WEST ELEVATION
1/12" = 1'

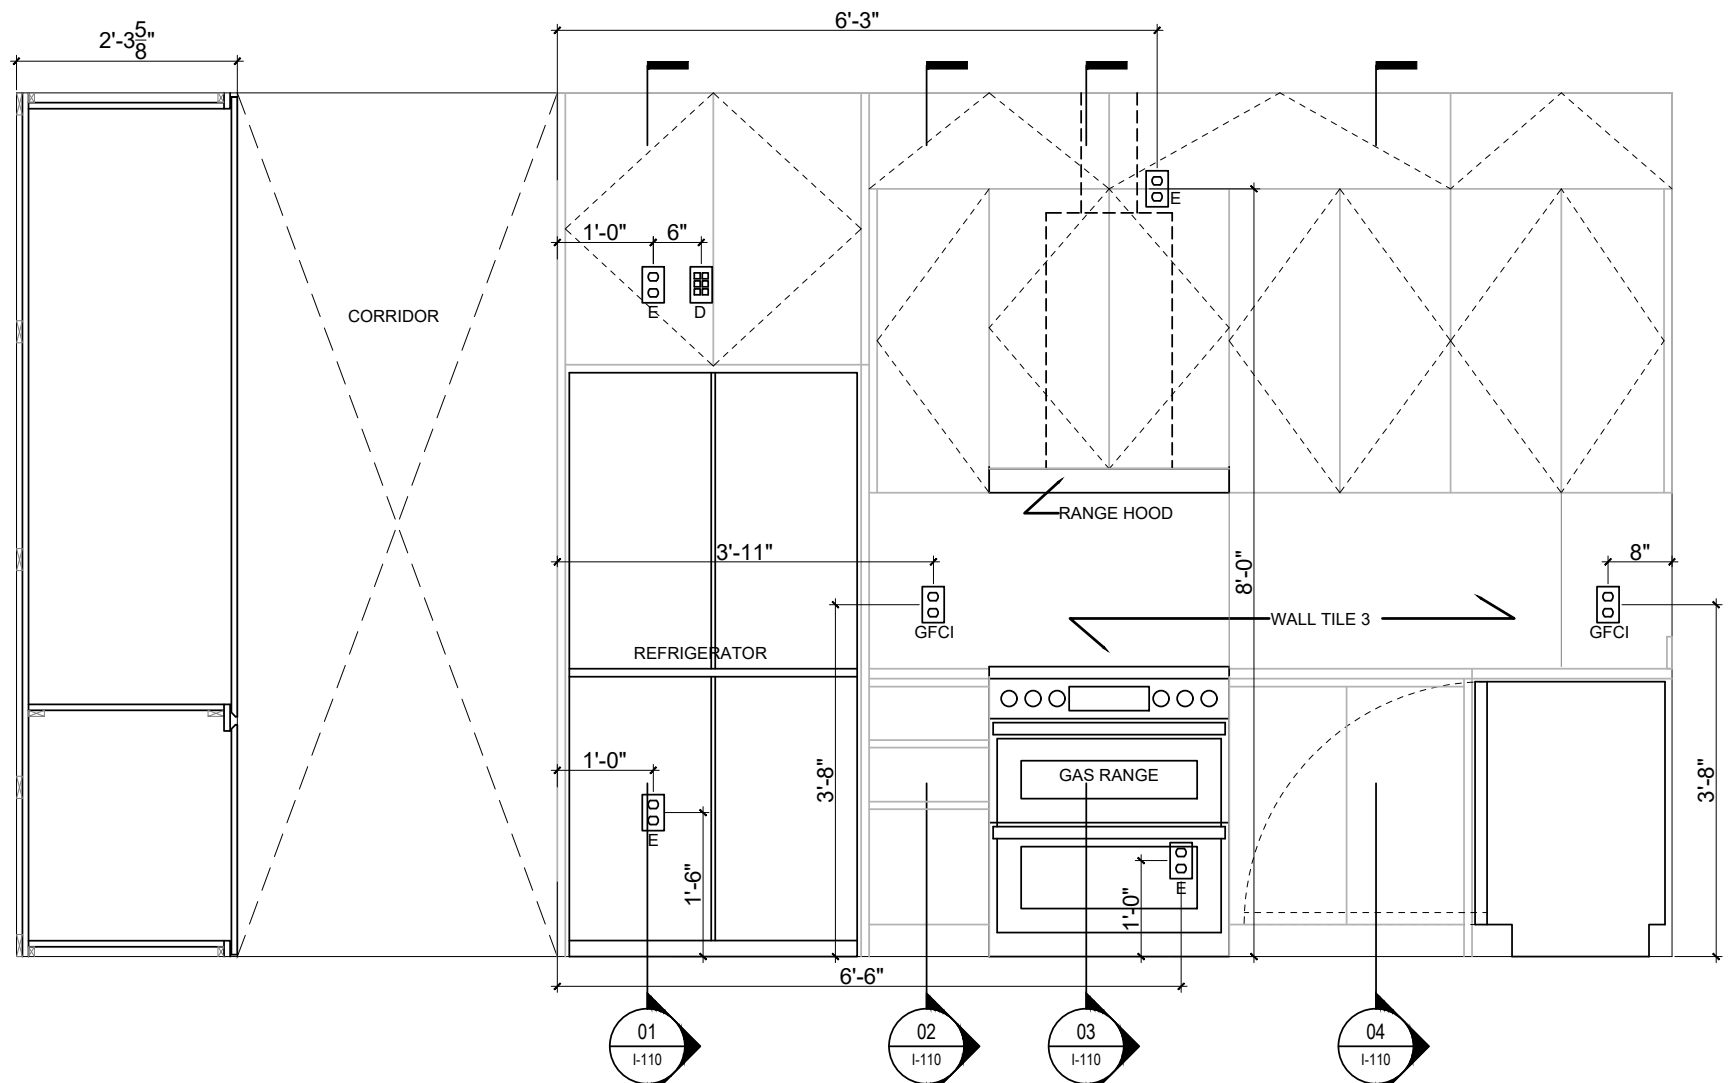

01 FIRST FLOOR LIVING ROOM & KITCHEN SOUTH ELEVATION
1/12" = 1'

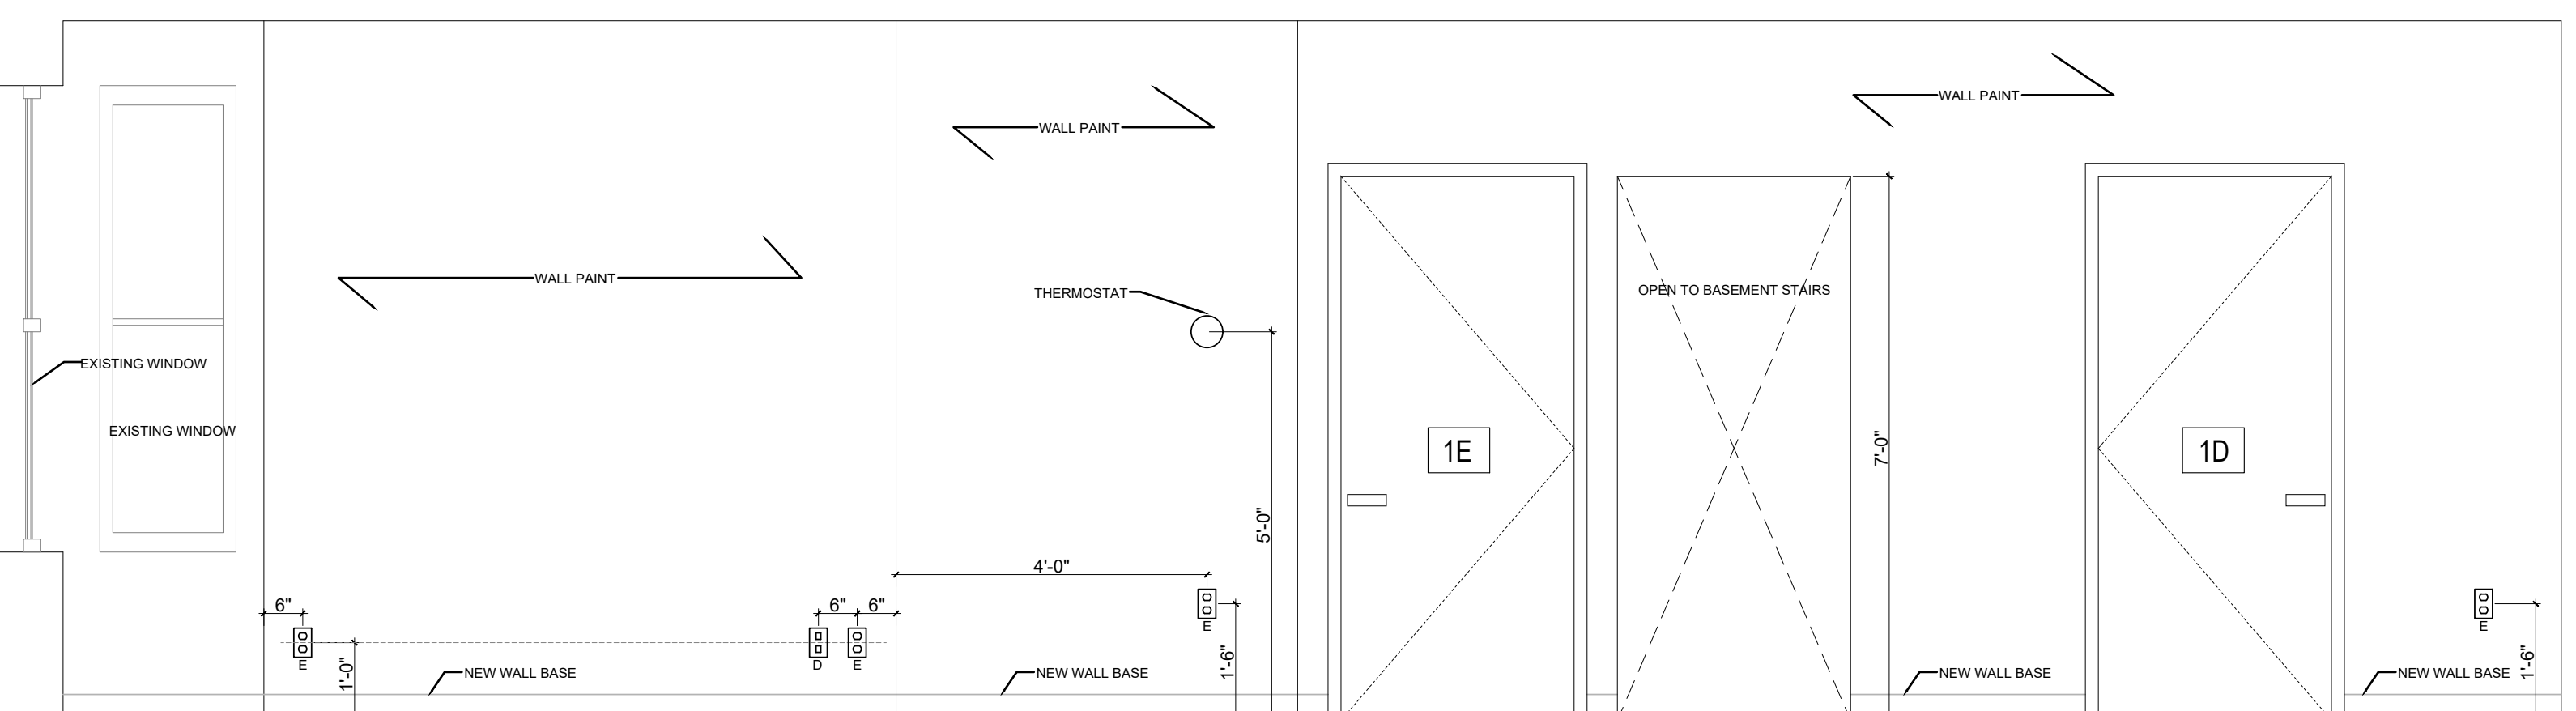

02 FIRST FLOOR LIVING ROOM & KITCHEN EAST ELEVATION
1/12" = 1'

PROJECT 103
213 MAPLE STREET
213 MAPLE STREET, WEEHAWKEN, NEW JERSEY, 07086

CONSULTANTS:
STRUCTURAL ENGINEER
FLEX ENGINEERING GROUP LLC
3133 CENTRAL AVE #202, UNION CITY, NJ 07087
T: 201-974-9570
E: flexengineer@yahoo.com

MECHANICAL ENGINEER
FLEX ENGINEERING GROUP LLC
3133 CENTRAL AVE #202, UNION CITY, NJ 07087
T: 201-974-9570
E: flexengineer@yahoo.com

GENERAL CONTRACTOR
HOBOKEN KITCHEN & BATH
2 14TH ST PH 32, HOBOKEN NJ, 07030
T: 201-472-0425
E: thodons@hobokenkitchenandbath.com

#	DATE	DESCRIPTION
---	------	-------------

DOB STAMP AND SIGNATURE

SEAL AND SIGNATURE


CONTRACTOR SHALL ONLY UTILIZE WRITTEN DIMENSIONS. CONTRACTOR SHALL VERIFY AND BE RESPONSIBLE FOR ALL DIMENSIONS AND CONDITIONS ON THE JOB. OWNER MUST BE NOTIFIED OF ANY VARIATIONS FROM DIMENSIONS AND CONDITIONS SHOWN BY THESE DRAWINGS. SCALED SHOP DRAWINGS MUST BE SUBMITTED TO OWNER FOR APPROVAL, BEFORE PROCEEDING WITH ANY FABRICATION.

ALL DRAWINGS, SPECIFICATIONS, ETC. CONTRIBUTED TO CONTRACTORS, BIDDERS, GOVERNMENT AGENCIES, ETC. ARE NOT FOR GENERAL USE OR PUBLICATION BY OTHERS. ALL RIGHTS RESERVED. NONE OF THE IDEAS, DESIGN, ARRANGEMENTS OR PLANS IN THESE DRAWINGS SHALL BE USED BY OR DISCLOSED TO ANY PERSONS, FIRM OR CORPORATION FOR ANY PURPOSE WITHOUT THE CURRENT AND WRITTEN PERMISSION OF OWNER.


DRAWING TITLE:
I-101
INTERIOR ELEVATION -
FIRST FLOOR

FOR CONSTRUCTION


ALL MILLWORK CABINETRY MATERIAL AND INSTALLATION BY OWNER
IN WALL WOOD BLOCKING FOR ALL CABINETRY BY HKB

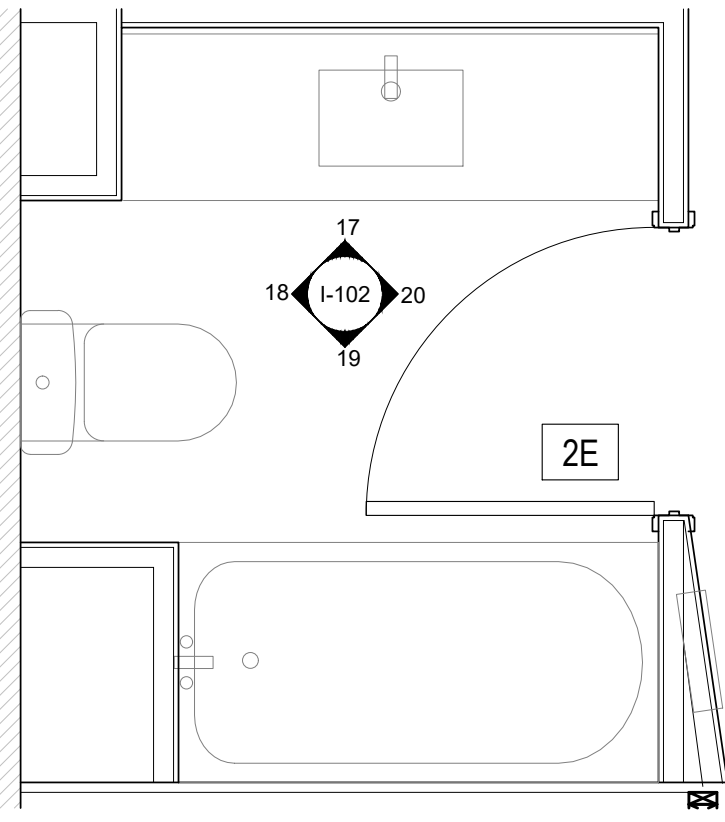


15 SECOND FLOOR GUEST TOILET ENLARGED PLAN
1/2" = 1'

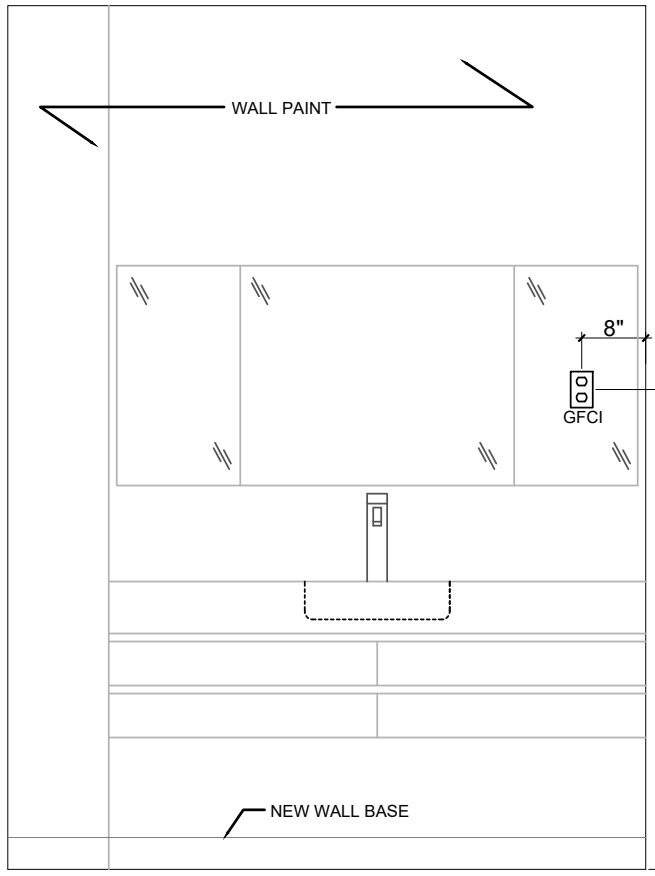


16 SECOND FLOOR GUEST TOILET SOUTH ELEVATION
1/2" = 1'

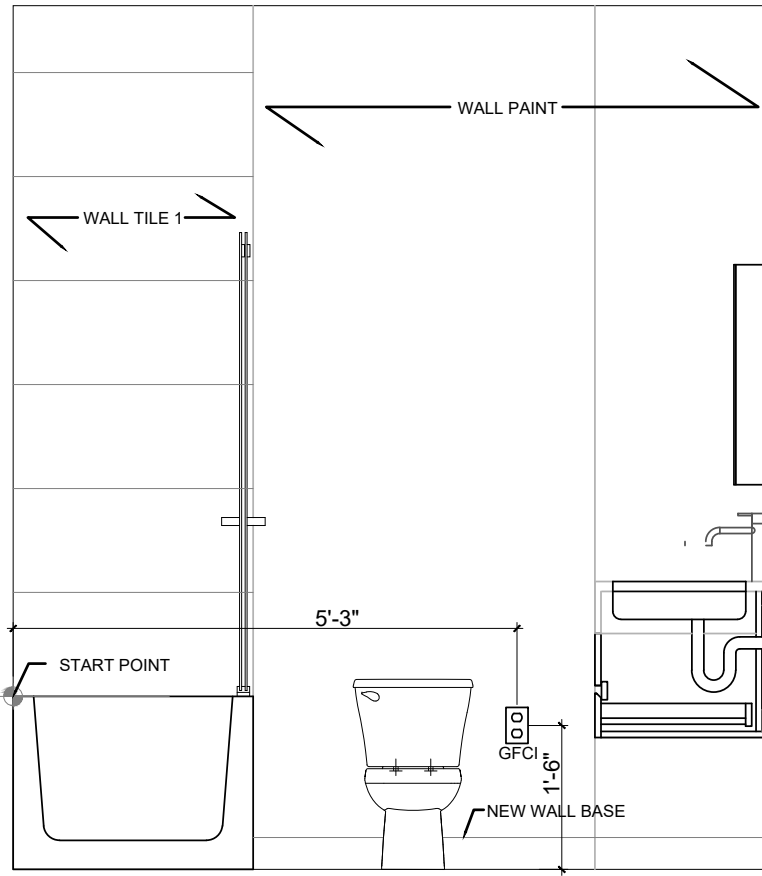


17 SECOND FLOOR GUEST TOILET EAST ELEVATION
1/2" = 1'

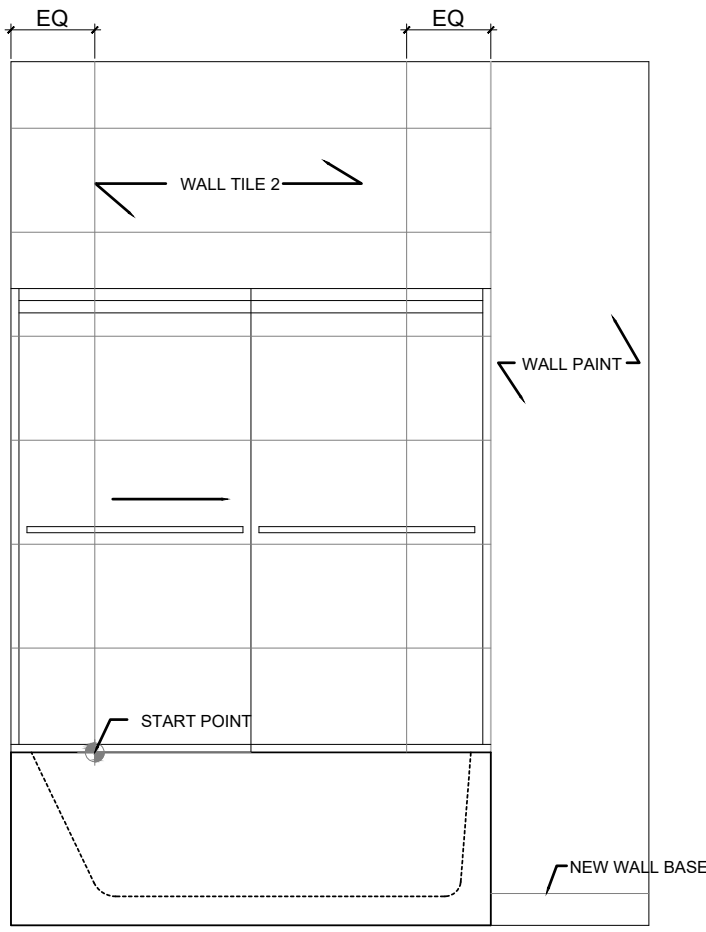


18 SECOND FLOOR GUEST TOILET NORTH ELEVATION
1/2" = 1'

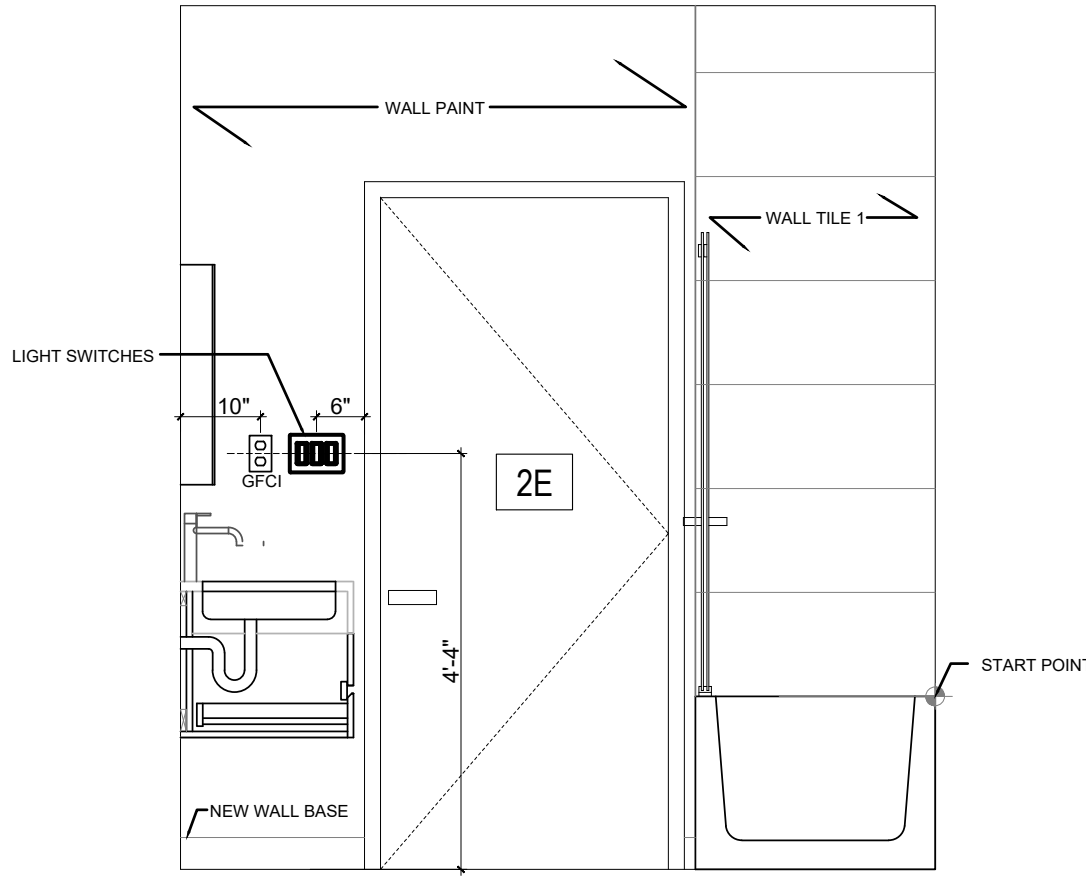


19 SECOND FLOOR GUEST TOILET WEST ELEVATION
1/2" = 1'

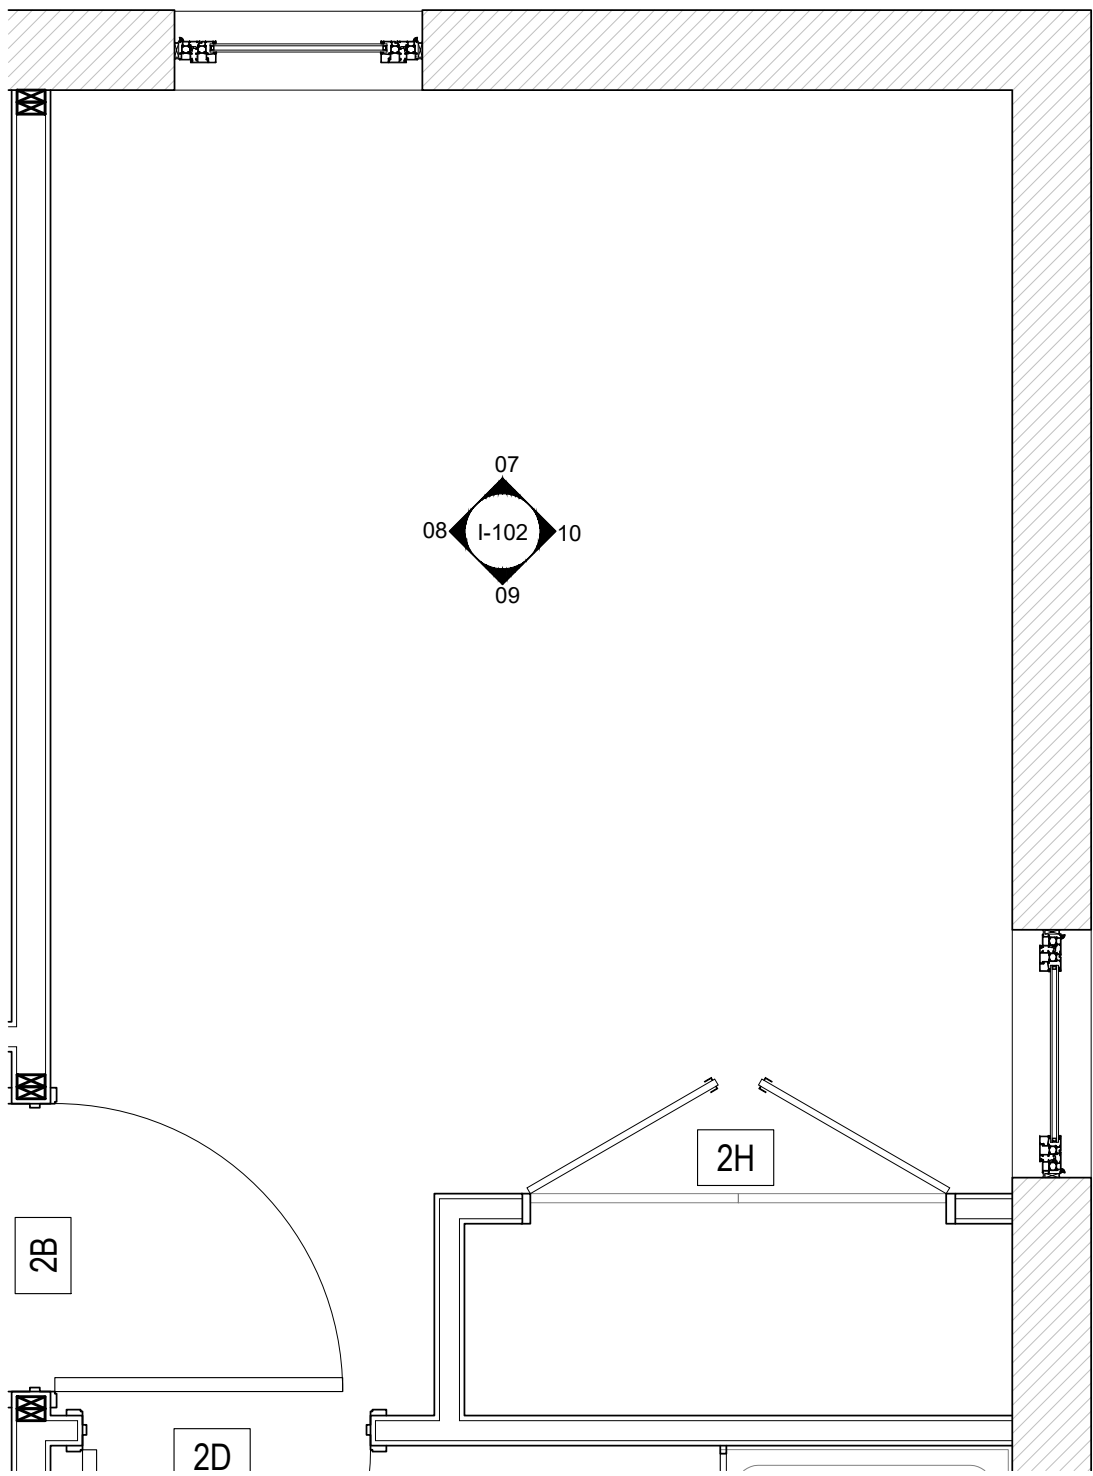


06 SECOND FLOOR MASTER BEDROOM ENLARGED PLAN
1/2" = 1'

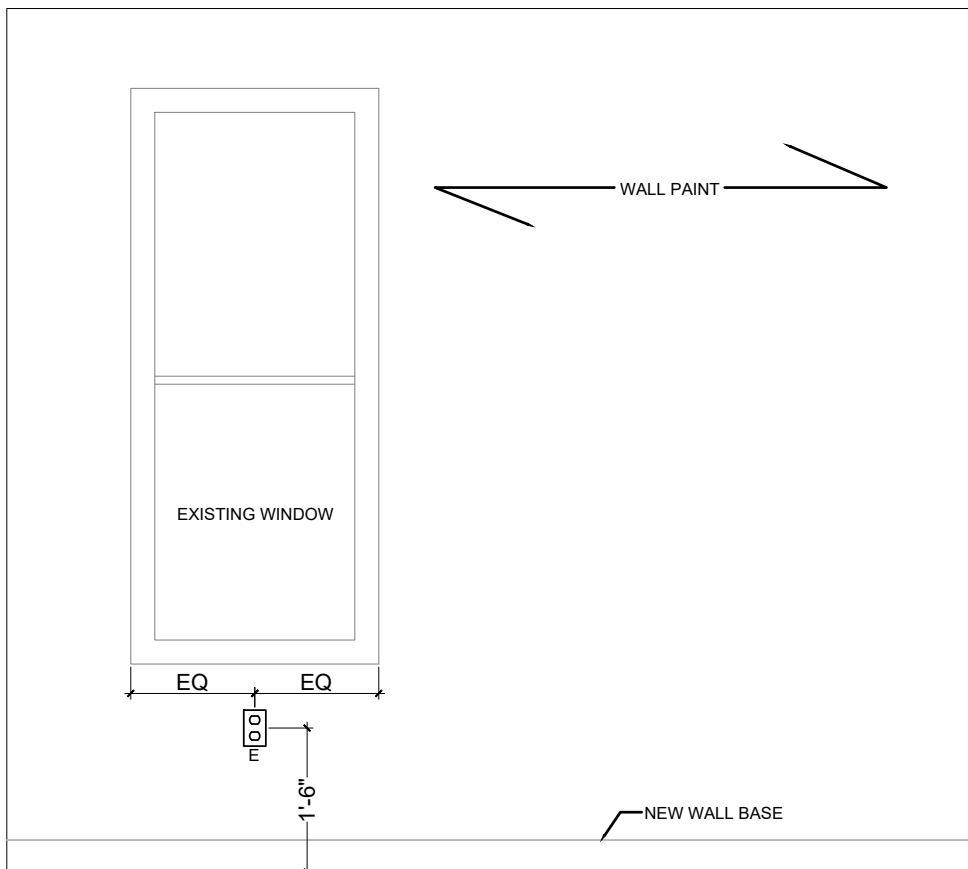


07 SECOND FLOOR MASTER BEDROOM SOUTH ELEVATION
1/2" = 1'

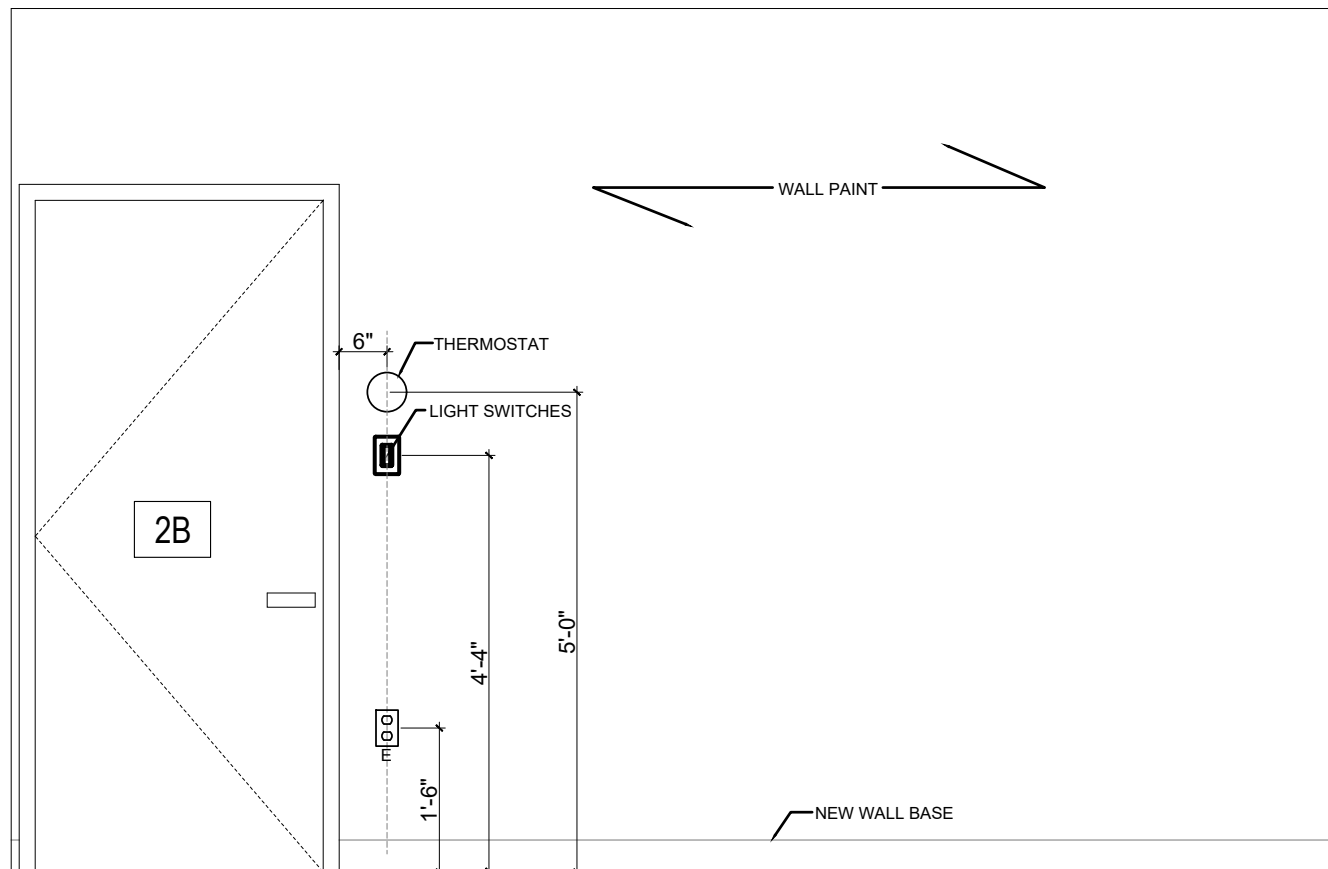


08 SECOND FLOOR MASTER BEDROOM EAST ELEVATION
1/2" = 1'

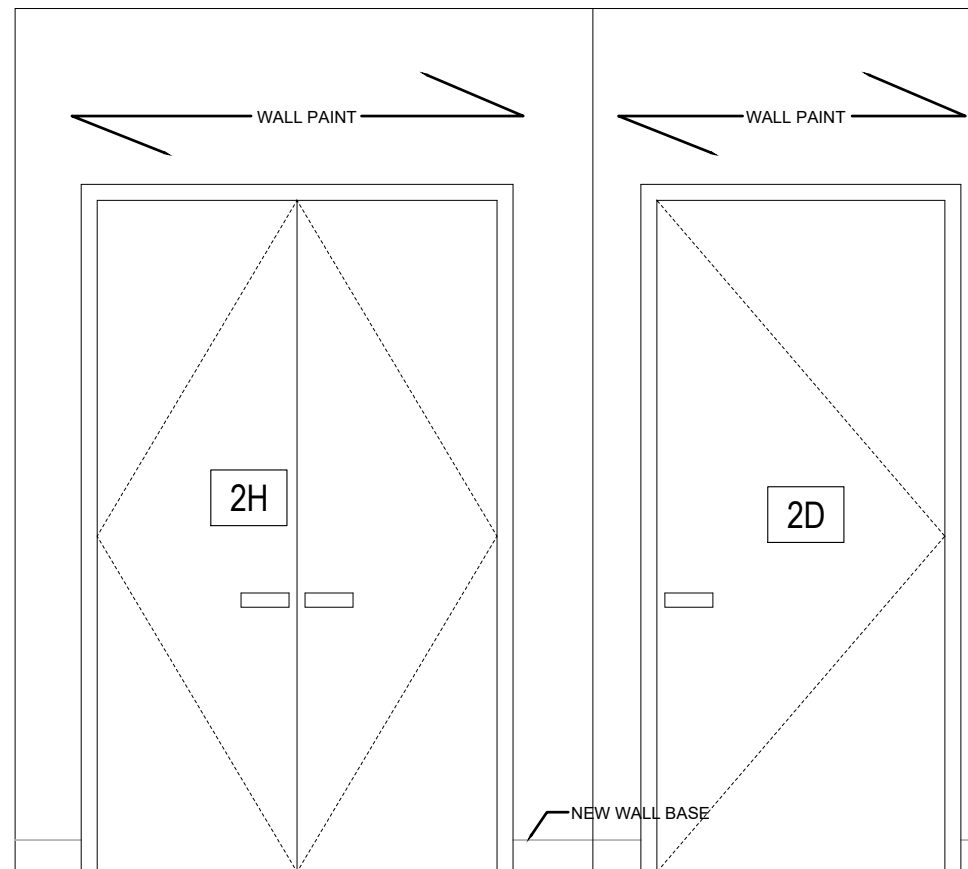


09 SECOND FLOOR MASTER BEDROOM NORTH ELEVATION
1/2" = 1'

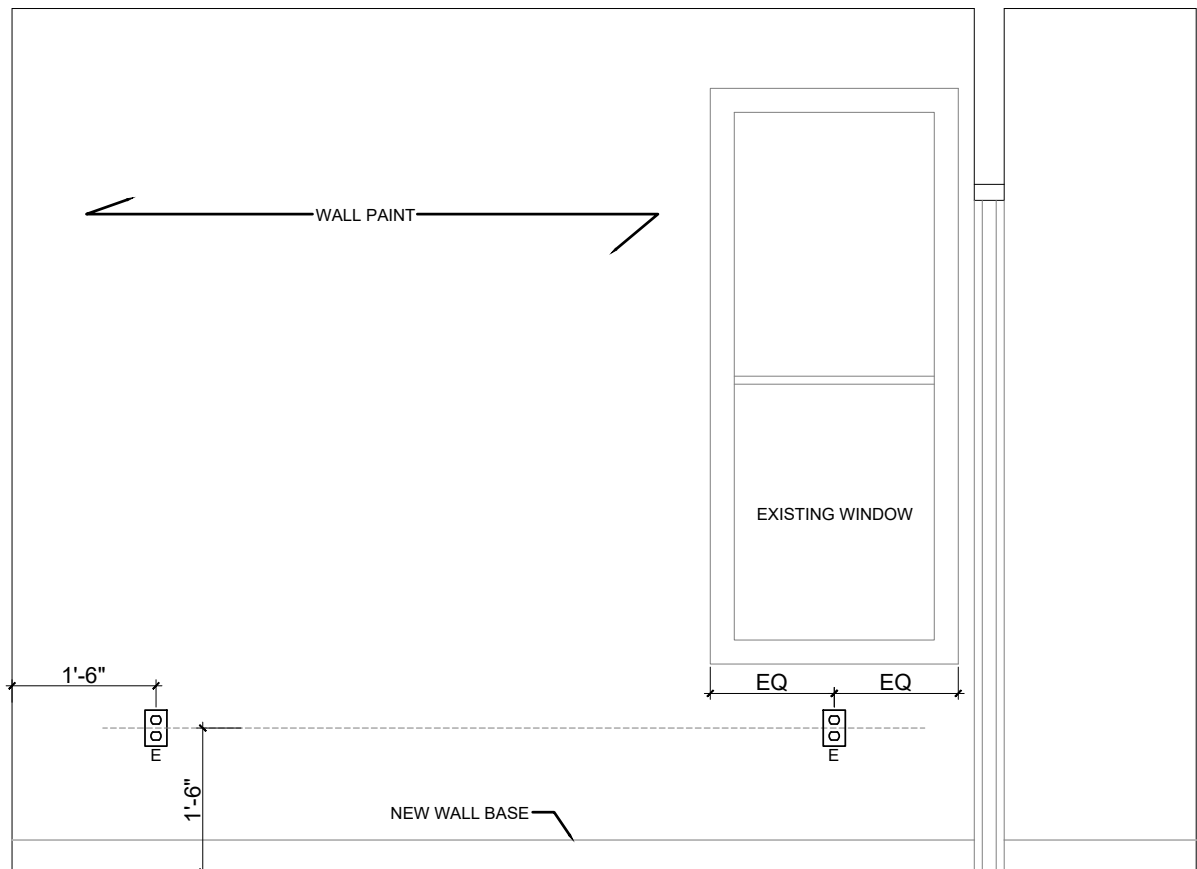


10 SECOND FLOOR MASTER BEDROOM WEST ELEVATION
1/2" = 1'

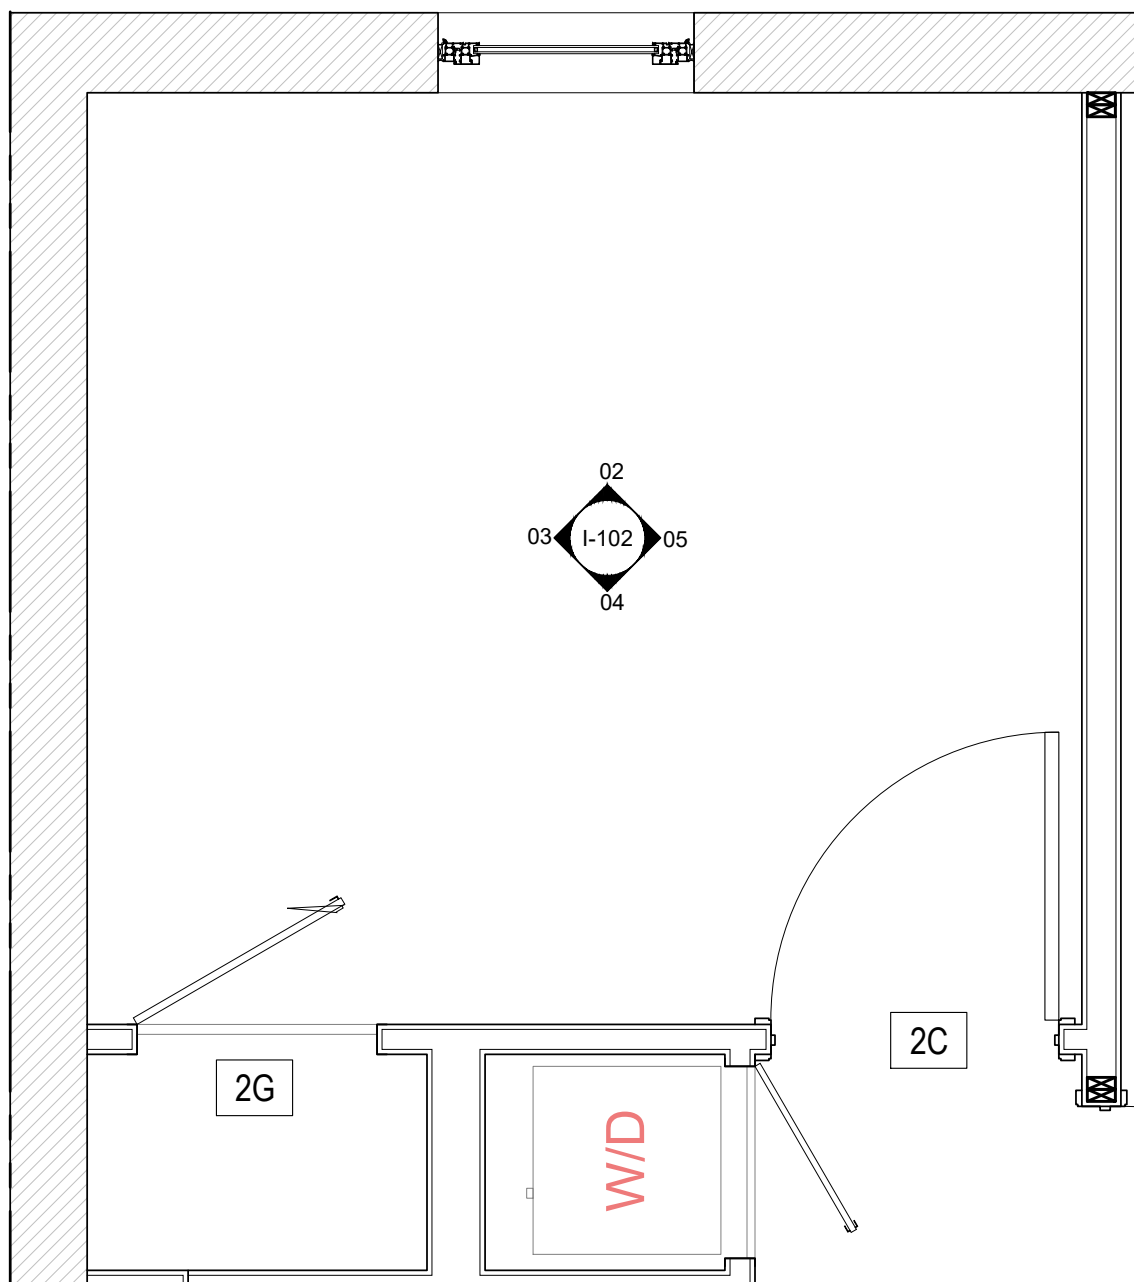


01 SECOND FLOOR GUEST BEDROOM ENLARGED PLAN
1/2" = 1'

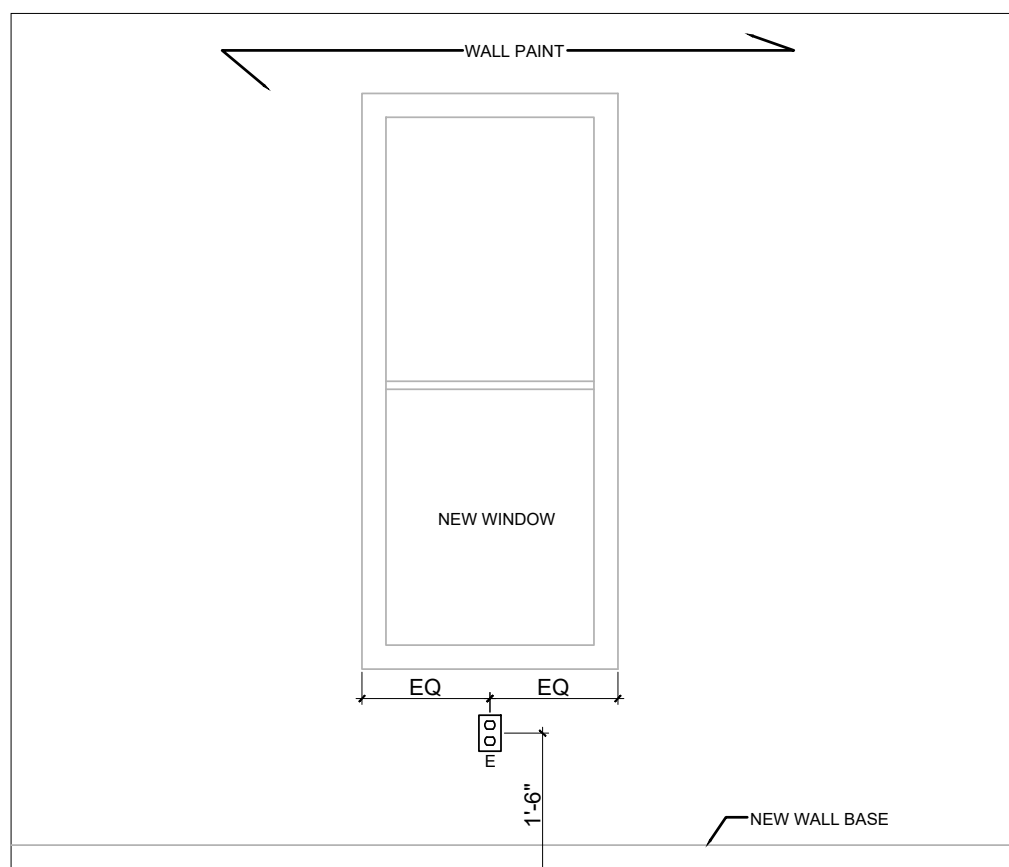


02 SECOND FLOOR GUEST BEDROOM SOUTH ELEVATION
1/2" = 1'

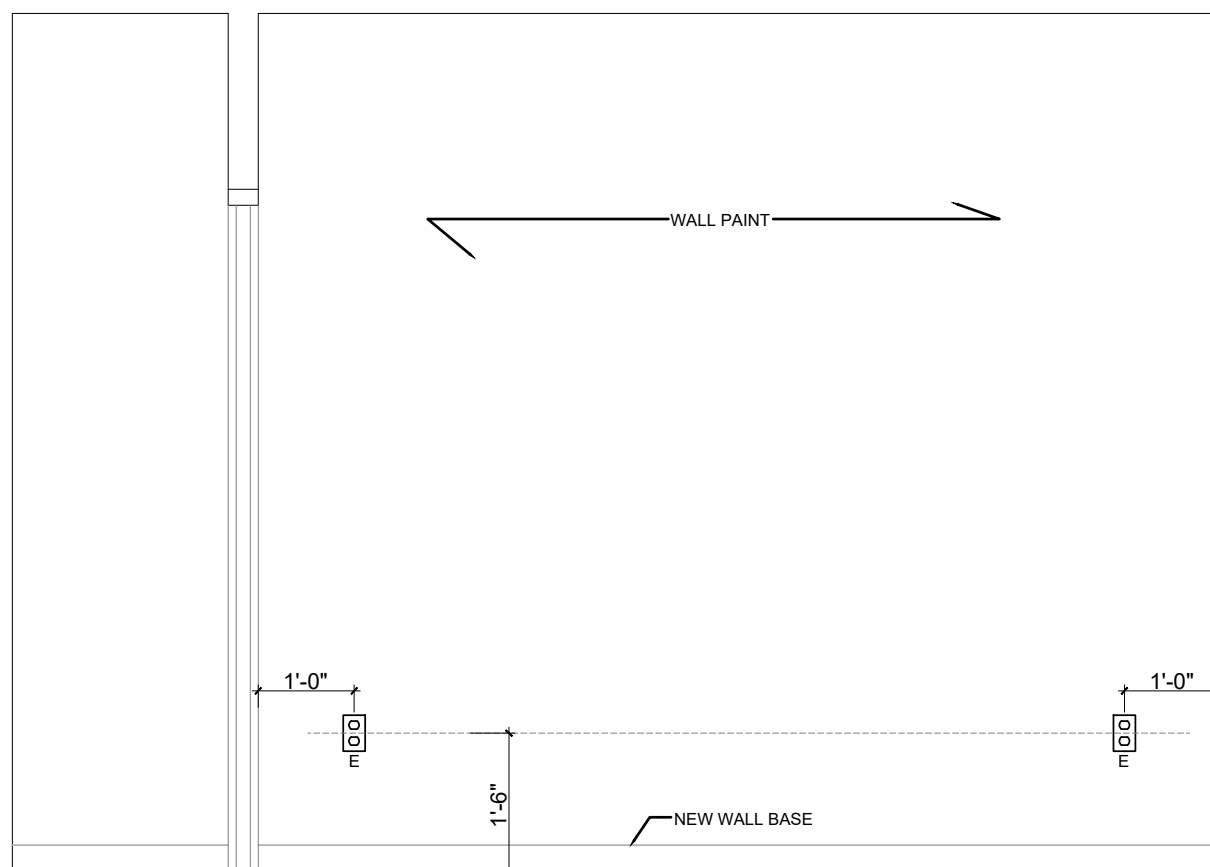

03 SECOND FLOOR GUEST BEDROOM EAST ELEVATION
1/2" = 1'

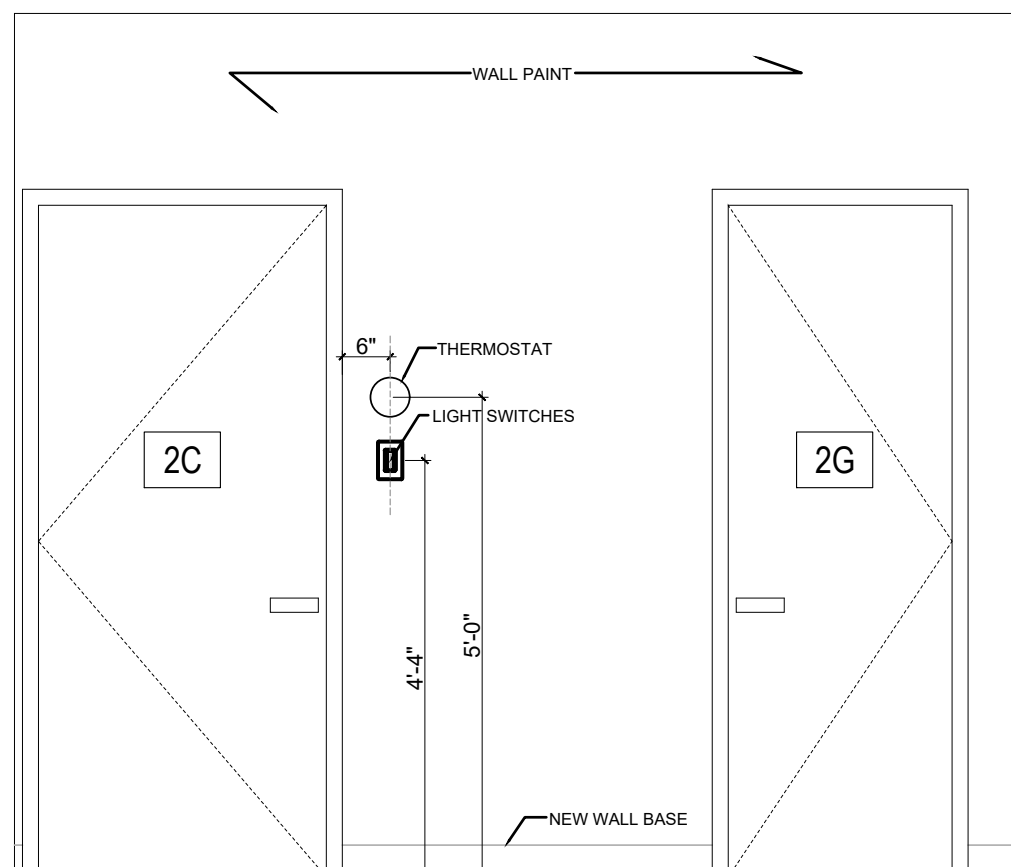

04 SECOND FLOOR GUEST BEDROOM NORTH ELEVATION
1/2" = 1'

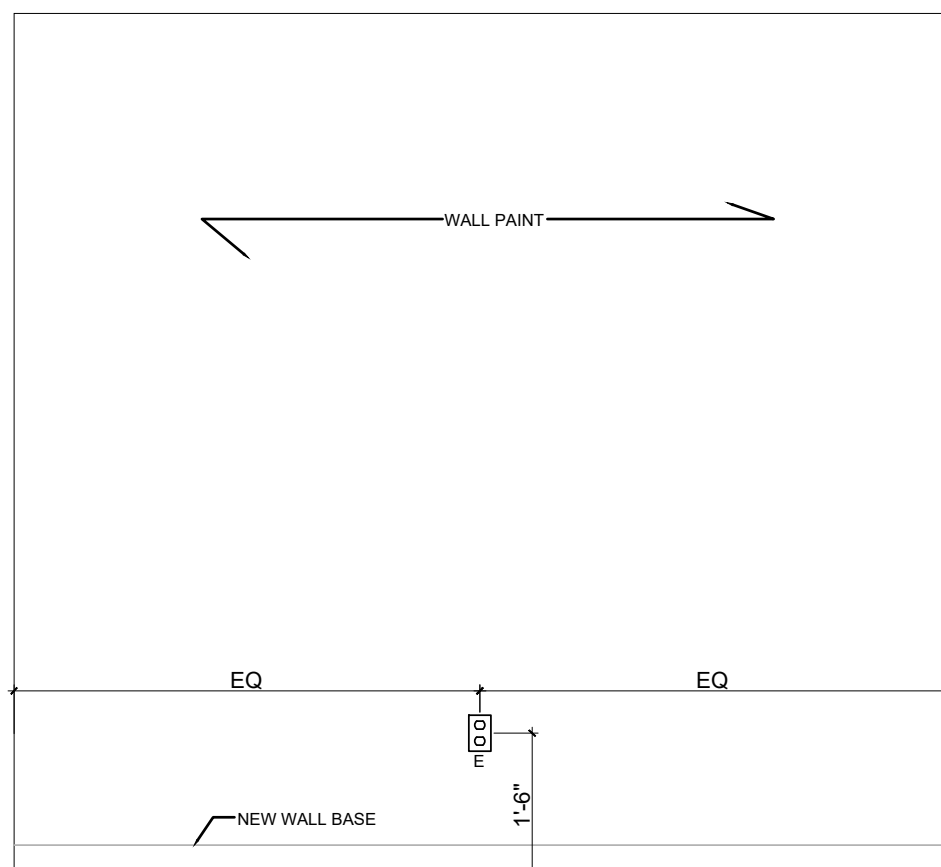

05 SECOND FLOOR GUEST BEDROOM WEST ELEVATION
1/2" = 1'

PROJECT 103

213 MAPLE STREET

213 MAPLE STREET, WEEHAWKEN, NEW JERSEY, 07086

CONSULTANTS:

STRUCTURAL ENGINEER
FLEX ENGINEERING GROUP LLC
3133 CENTRAL AVE #202, UNION CITY, NJ 07087
T: 201-974-9570
E: flexengr@yahoo.com

MECHANICAL ENGINEER
FLEX ENGINEERING GROUP LLC
3133 CENTRAL AVE #202, UNION CITY, NJ 07087
T: 201-974-9570
E: flexengr@yahoo.com

GENERAL CONTRACTOR
HOBOKEN KITCHEN & BATH
2 14TH ST PH 32, HOBOKEN, NJ 07030
T: 201-472-0425
E: theodore@hobokenkitchenandbath.com

DATE DESCRIPTION

DOB STAMP AND SIGNATURE

SEAL AND SIGNATURE

CONTRACTOR SHALL ONLY UTILIZE WRITTEN DIMENSIONS. CONTRACTOR SHALL VERIFY AND BE RESPONSIBLE FOR ALL DIMENSIONS AND CONDITIONS ON THE JOB. AND OWNER MUST BE NOTIFIED OF ANY VARIATIONS FROM DIMENSIONS AND CONDITIONS SHOWN BY THESE DRAWINGS. SCALED SHOP DRAWINGS MUST BE SUBMITTED TO OWNER FOR APPROVAL, BEFORE PROCEEDING WITH ANY FABRICATION.


ALL DRAWINGS, SPECIFICATIONS, ETC. CONTRIBUTED TO CONTRACTORS, BIDDERS, GOVERNMENTAL AGENCIES, ETC. ARE NOT FOR GENERAL USE OR PUBLICATION BY OTHERS. ALL RIGHTS RESERVED. NONE OF THE DRAWING, SPECIFICATIONS, ETC. SHALL BE USED BY OR DISCLOSED TO ANY PERSONS, FIRM OR CORPORATION FOR ANY PURPOSE WITHOUT THE WRITTEN PERMISSION OF OWNER.

DRAWING TITLE:


I-102
INTERIOR ELEVATION -
SECOND FLOOR

FOR CONSTRUCTION


ALL MILLWORK CABINETRY MATERIAL AND INSTALLATION BY OWNER
IN WALL WOOD BLOCKING FOR ALL CABINETRY BY HKB

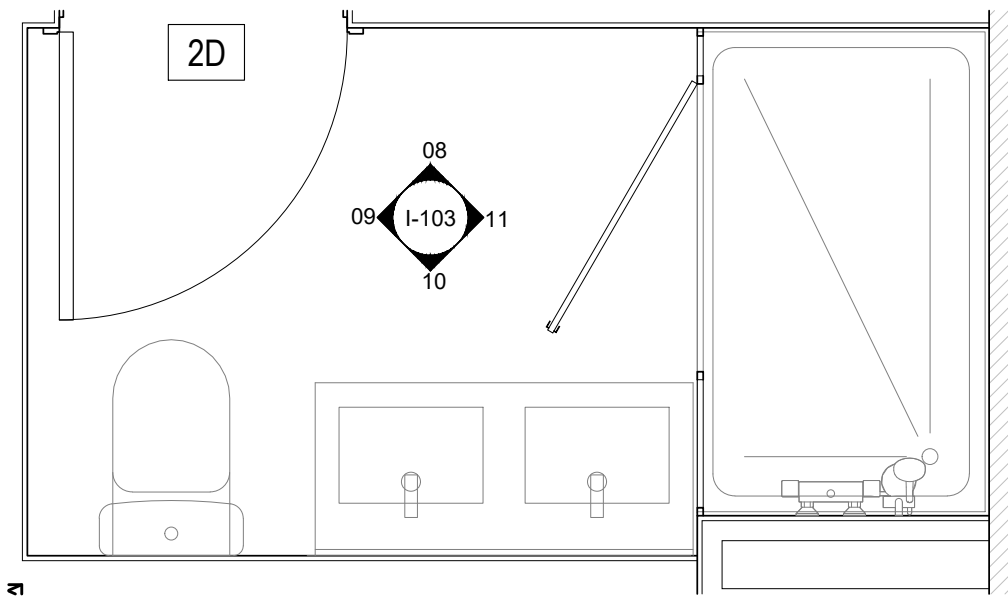


07 SECOND FLOOR MASTER TOILET ENLARGED PLAN
1/2" = 1'

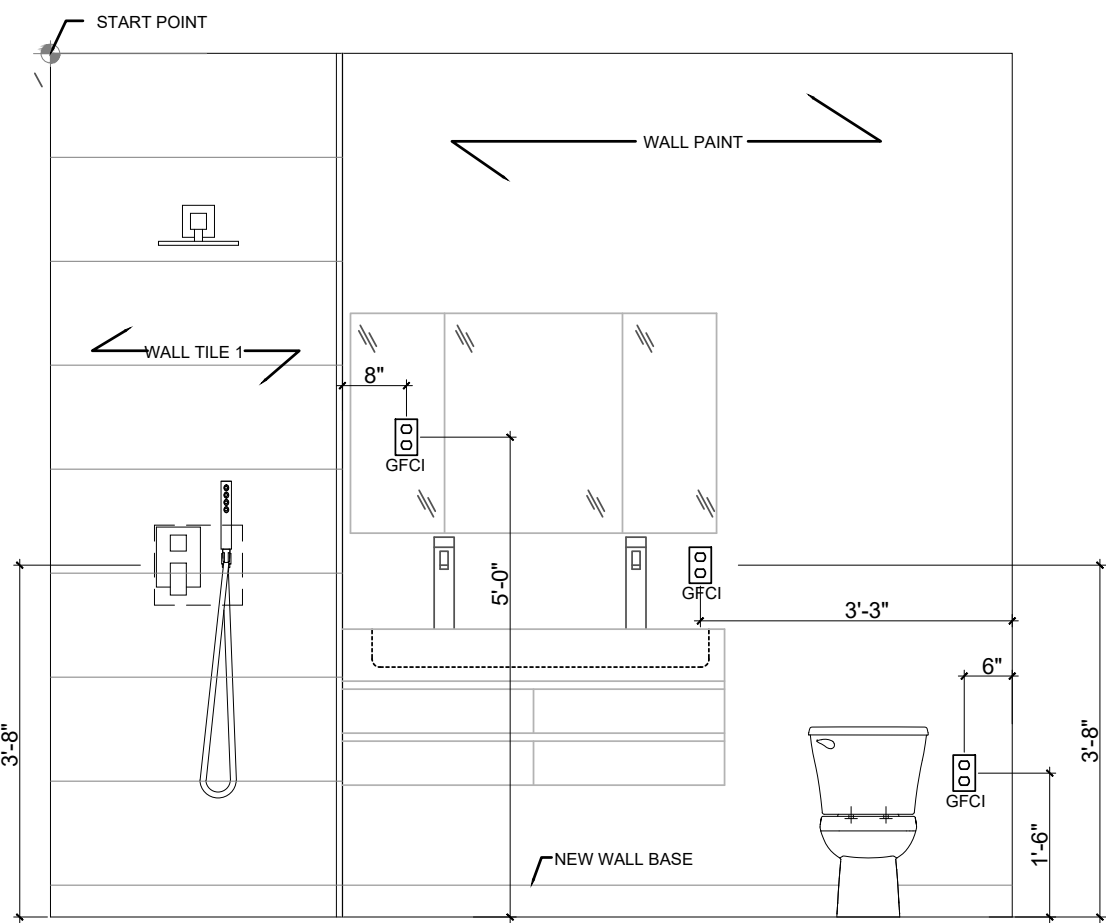


10 SECOND FLOOR MASTER TOILET NORTH ELEVATION
1/2" = 1'

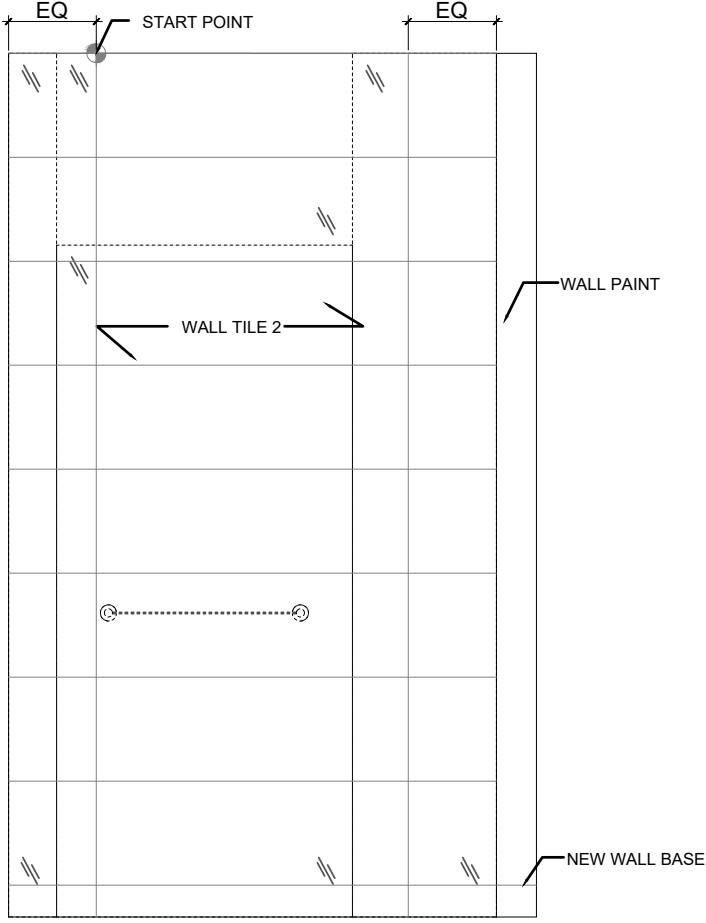


11 SECOND FLOOR MASTER TOILET WEST ELEVATION
1/2" = 1'

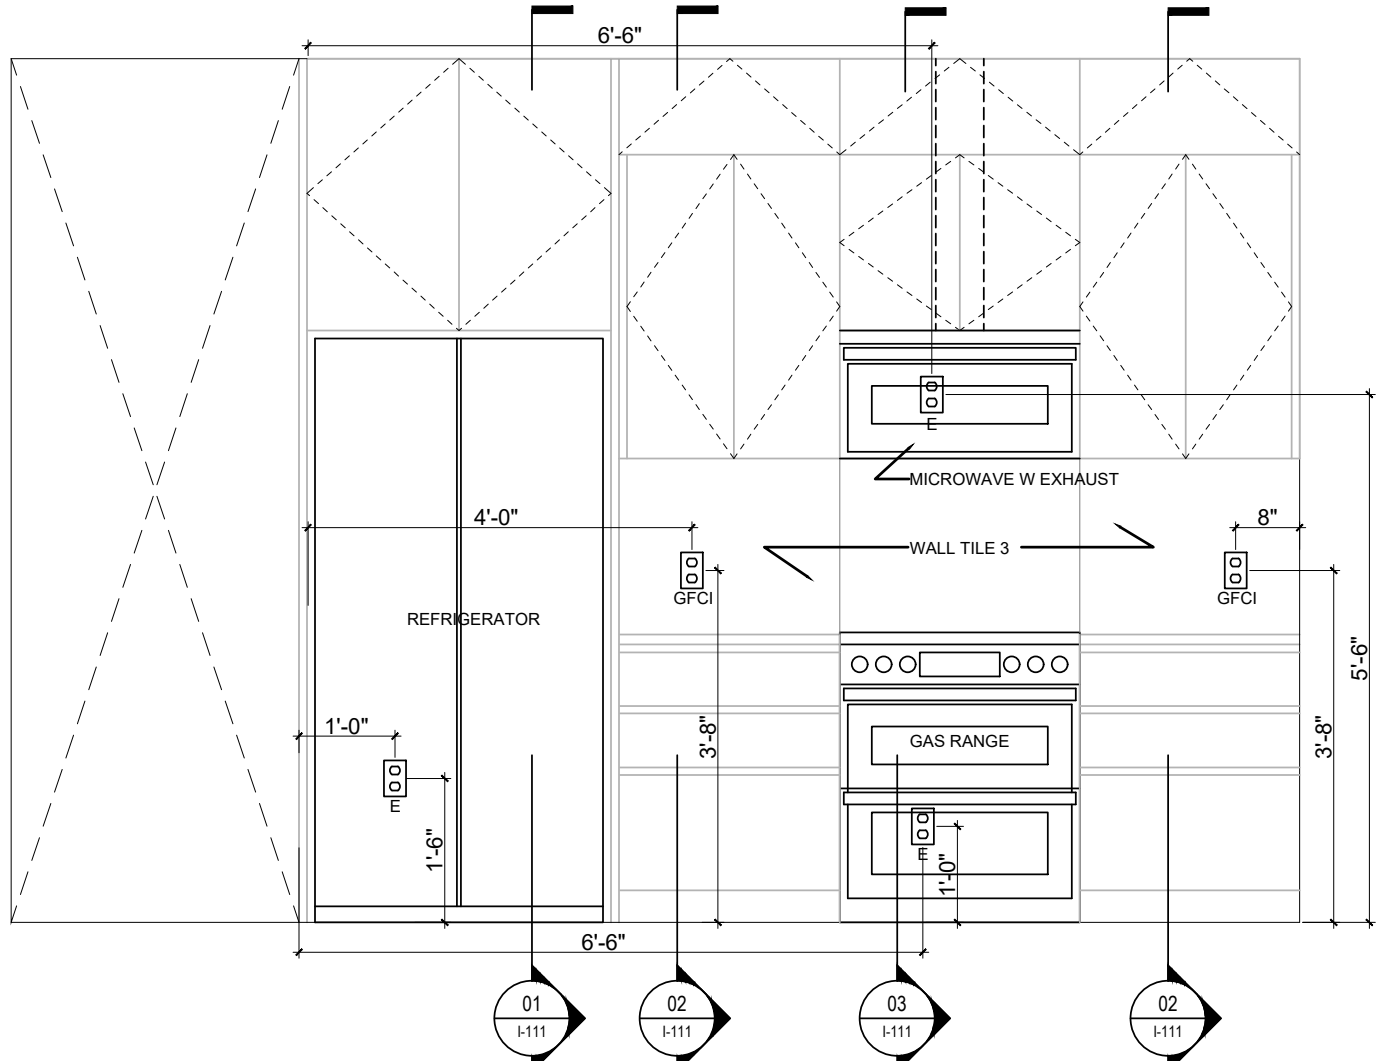


05 SECOND FLOOR KITCHEN SOUTH ELEVATION
1/2" = 1'

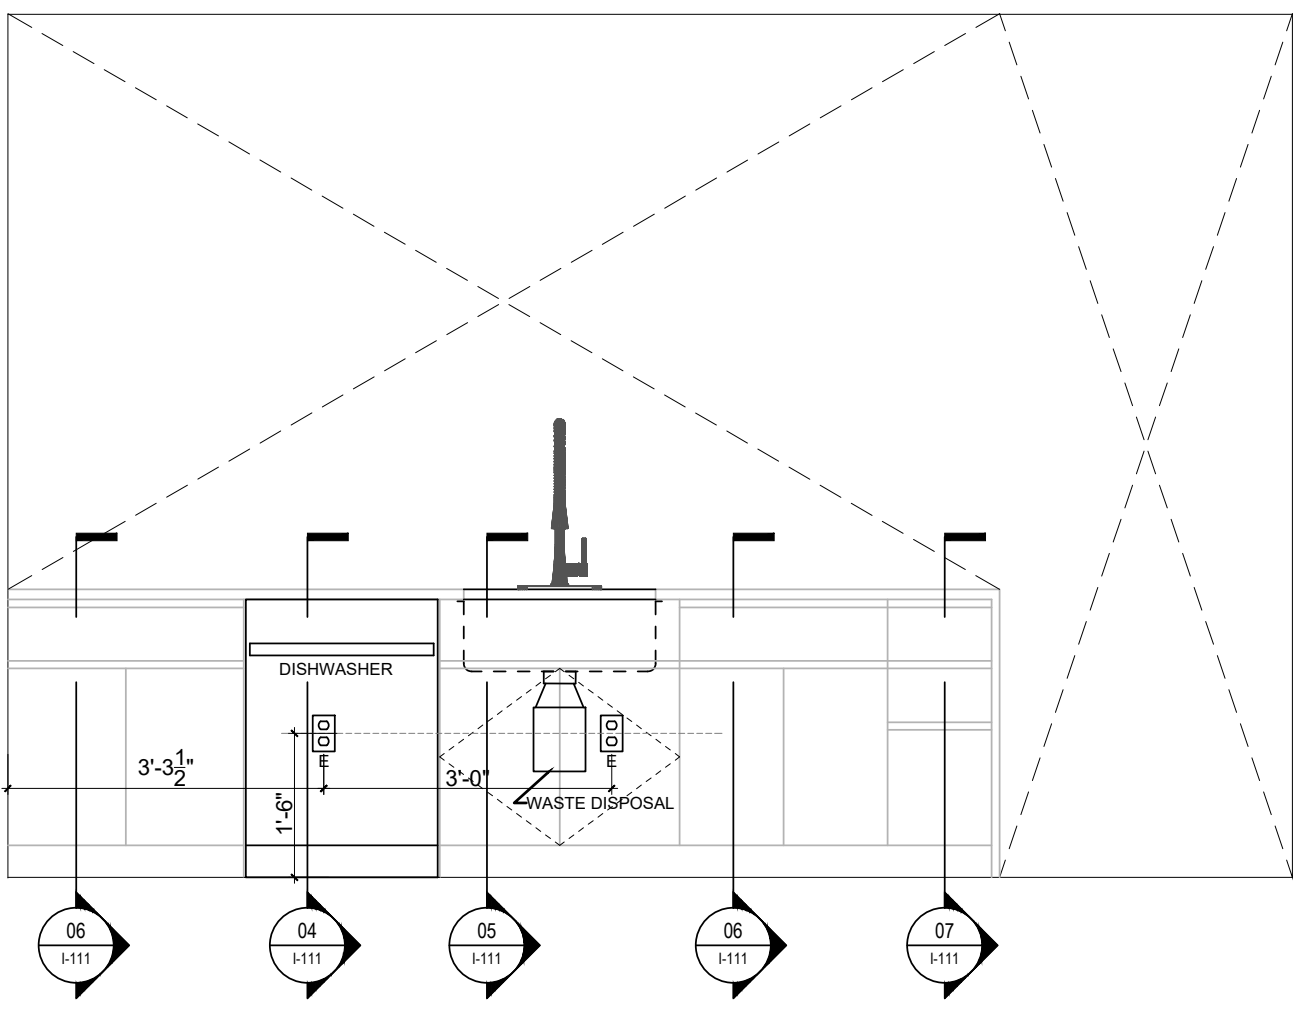


06 SECOND FLOOR KITCHEN NORTH ELEVATION
1/2" = 1'

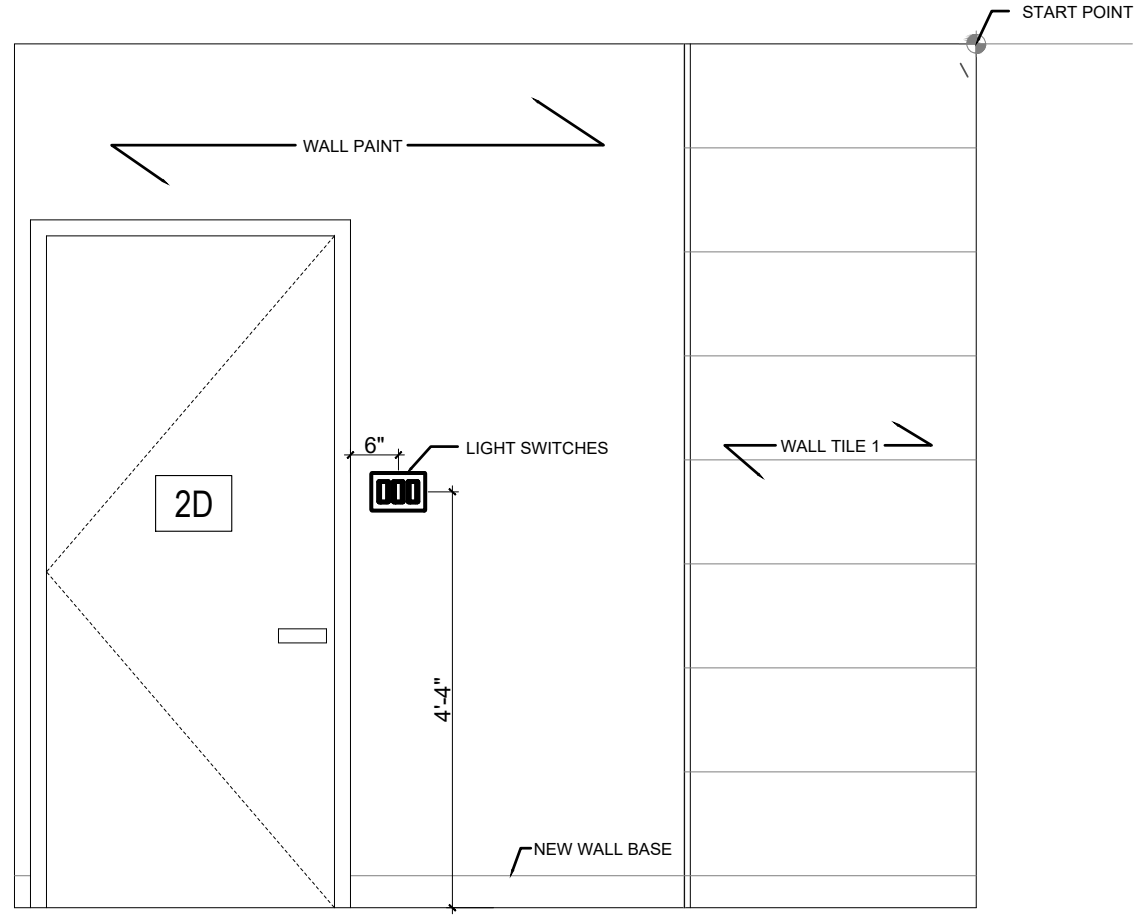


08 SECOND FLOOR MASTER TOILET SOUTH ELEVATION
1/2" = 1'

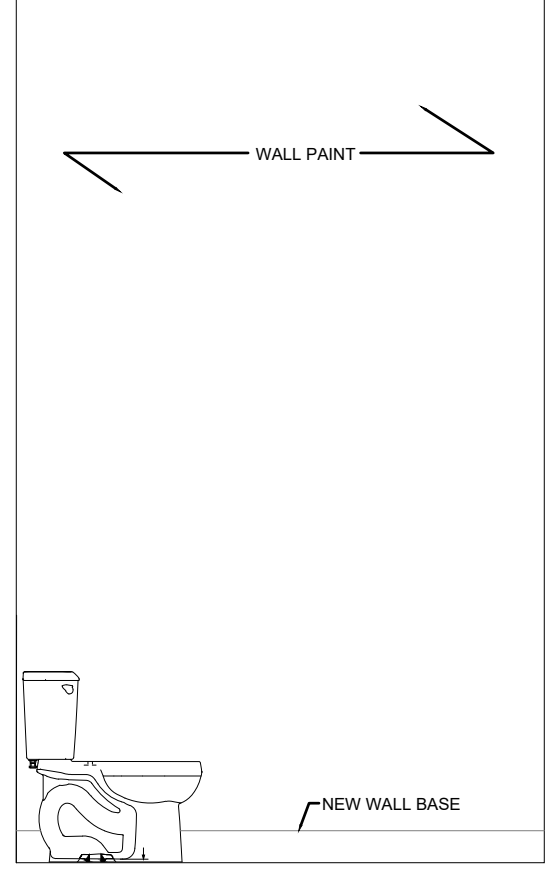


09 SECOND FLOOR MASTER TOILET EAST ELEVATION
1/2" = 1'

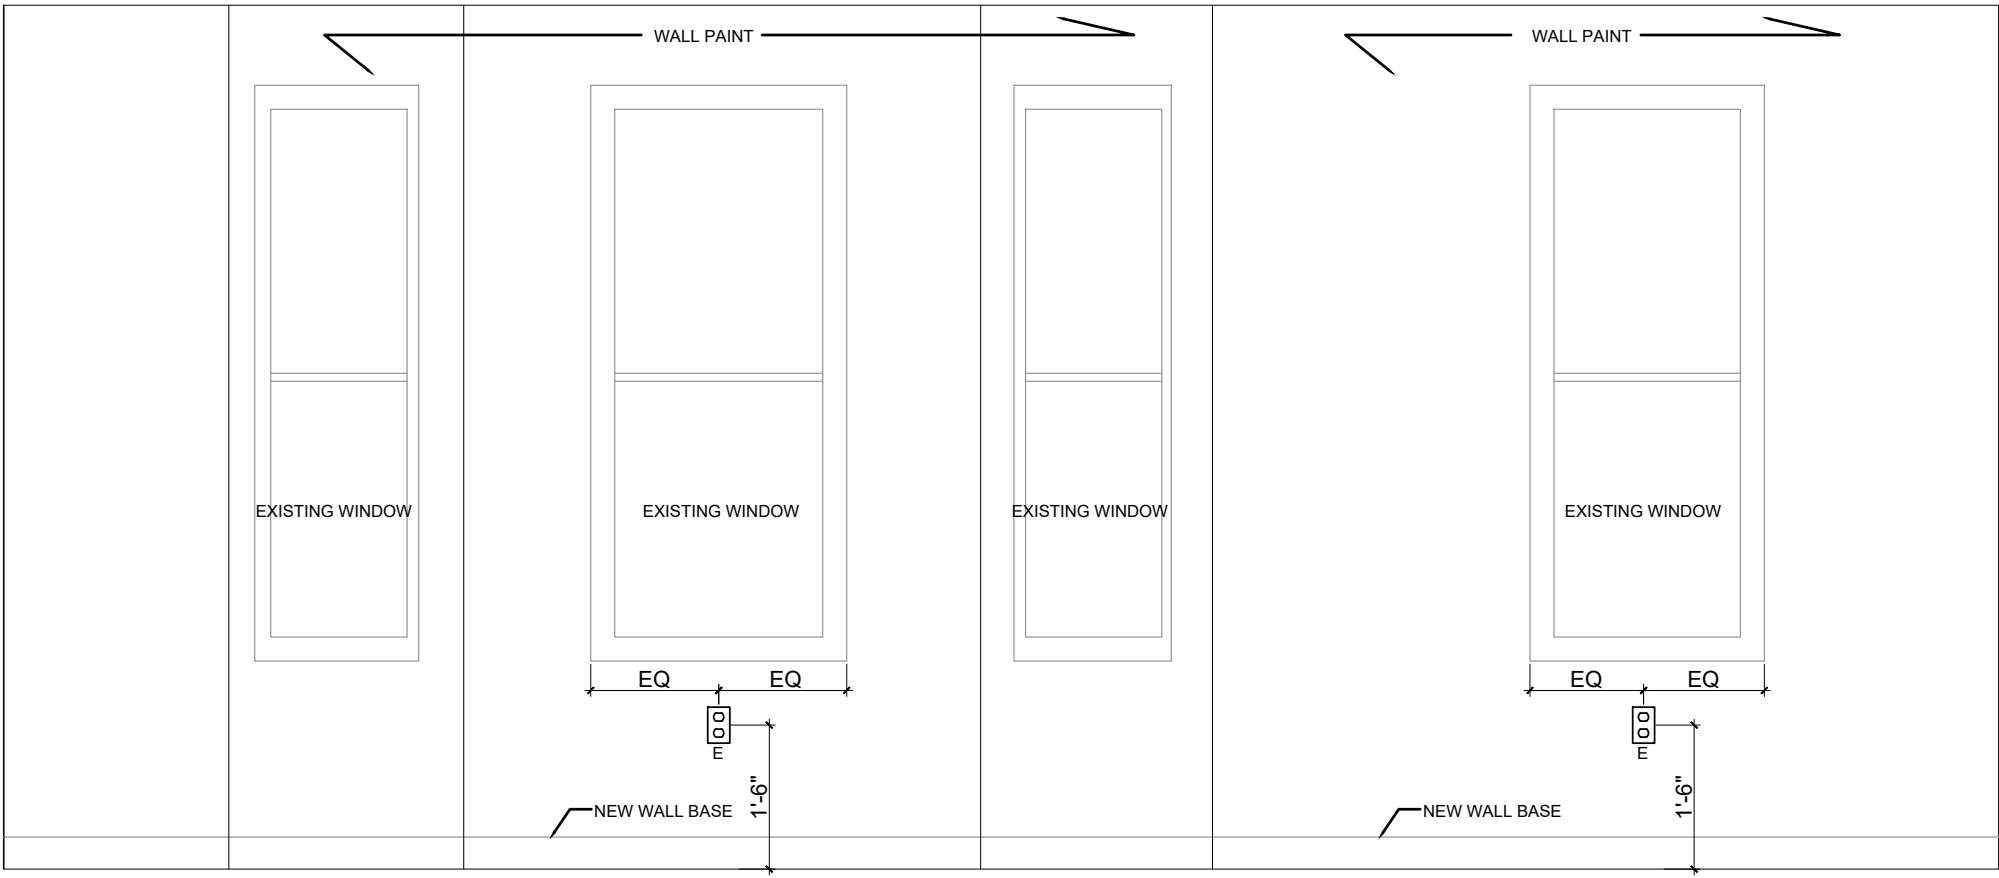


03 SECOND FLOOR LIVING ROOM NORTH ELEVATION
1/2" = 1'

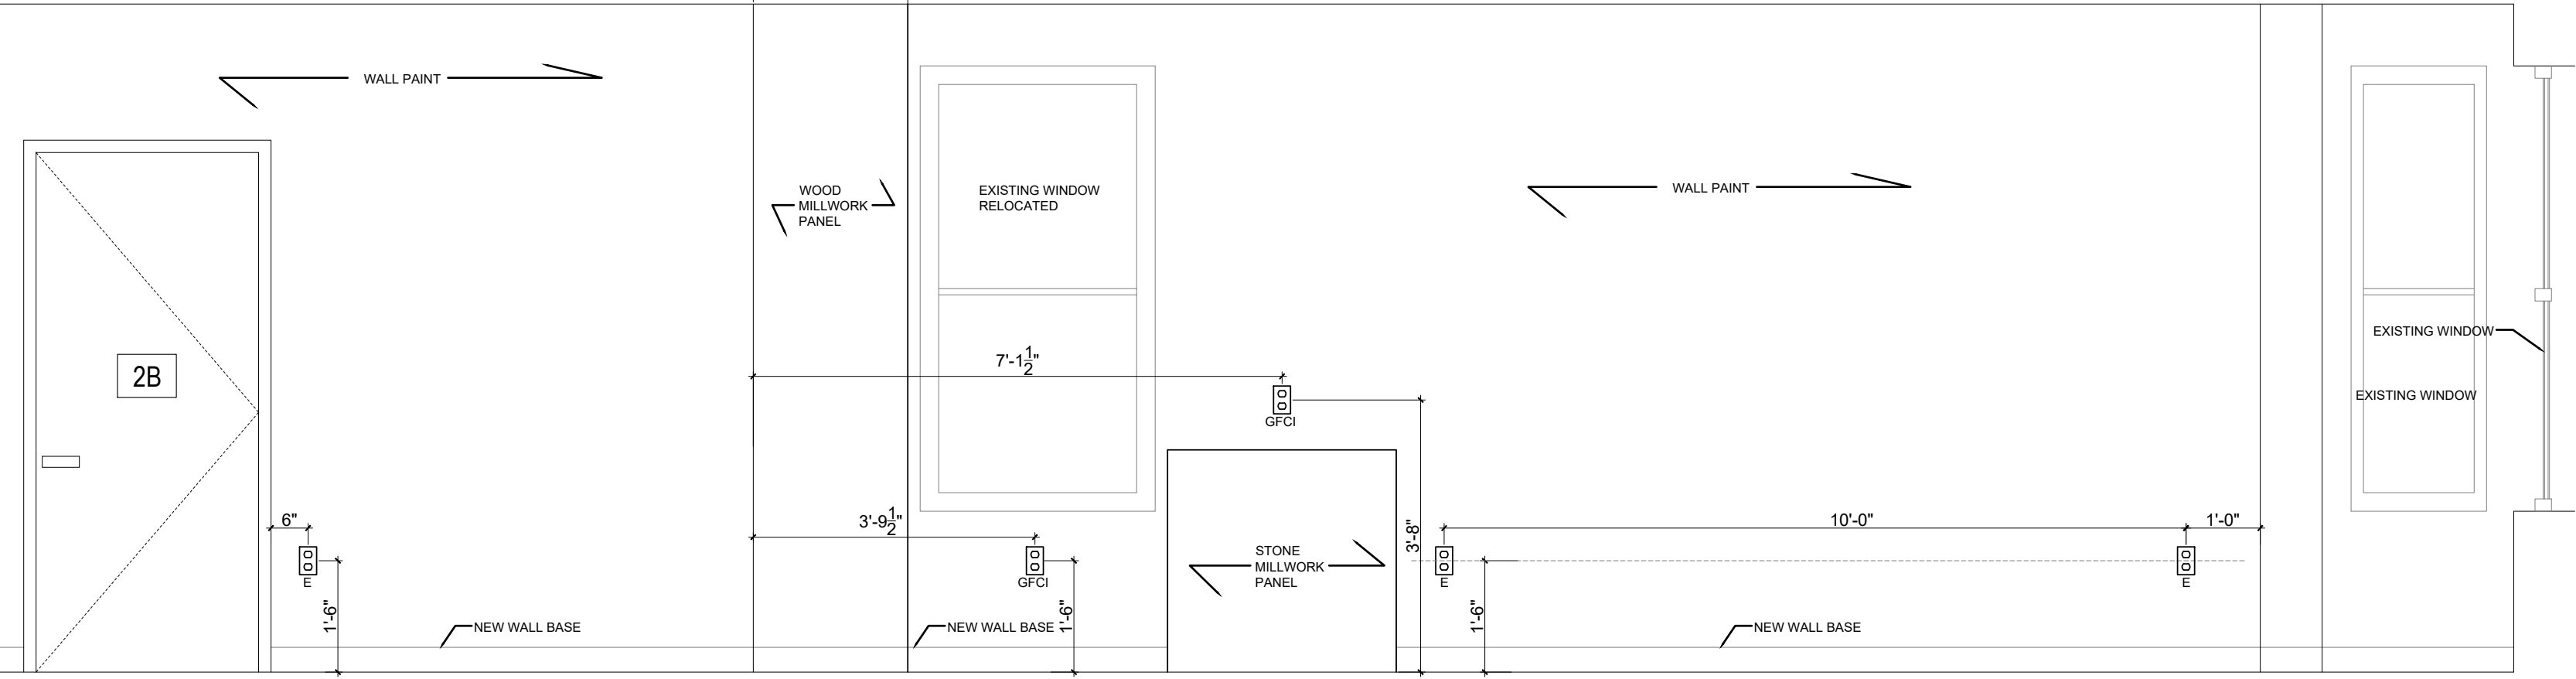

04 SECOND FLOOR LIVING ROOM & CORRIDOR WEST ELEVATION
1/2" = 1'

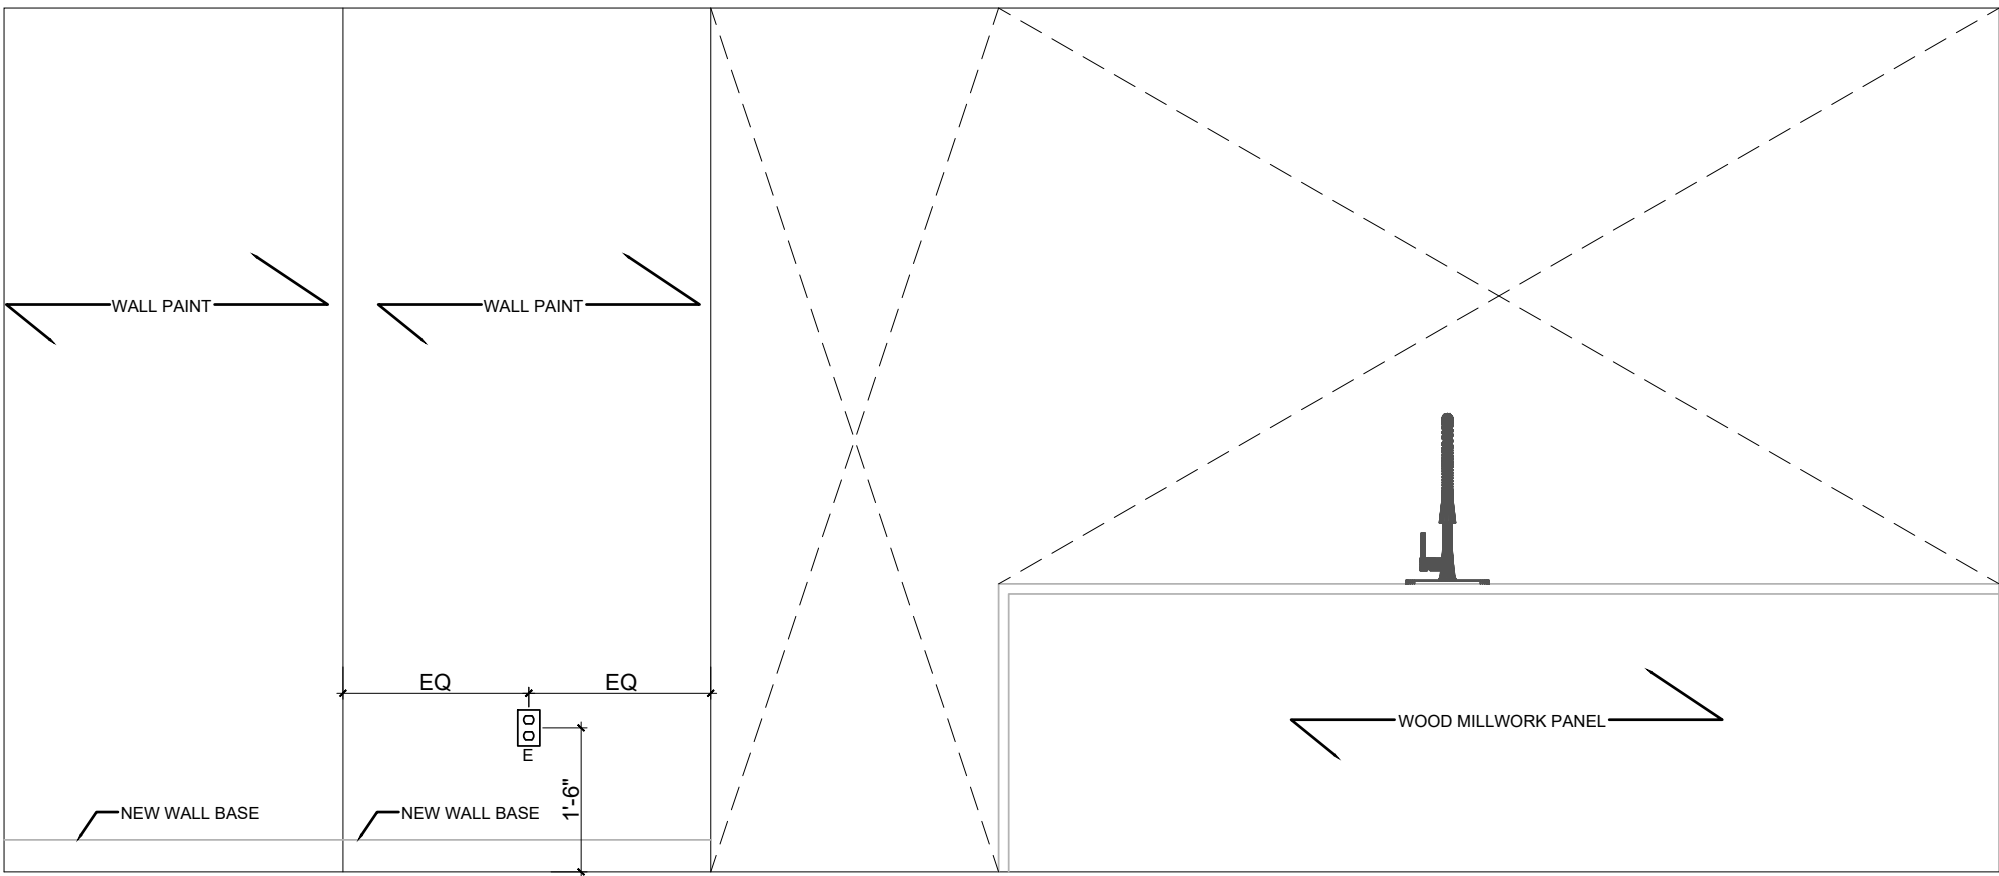

01 SECOND FLOOR LIVING ROOM SOUTH ELEVATION
1/2" = 1'

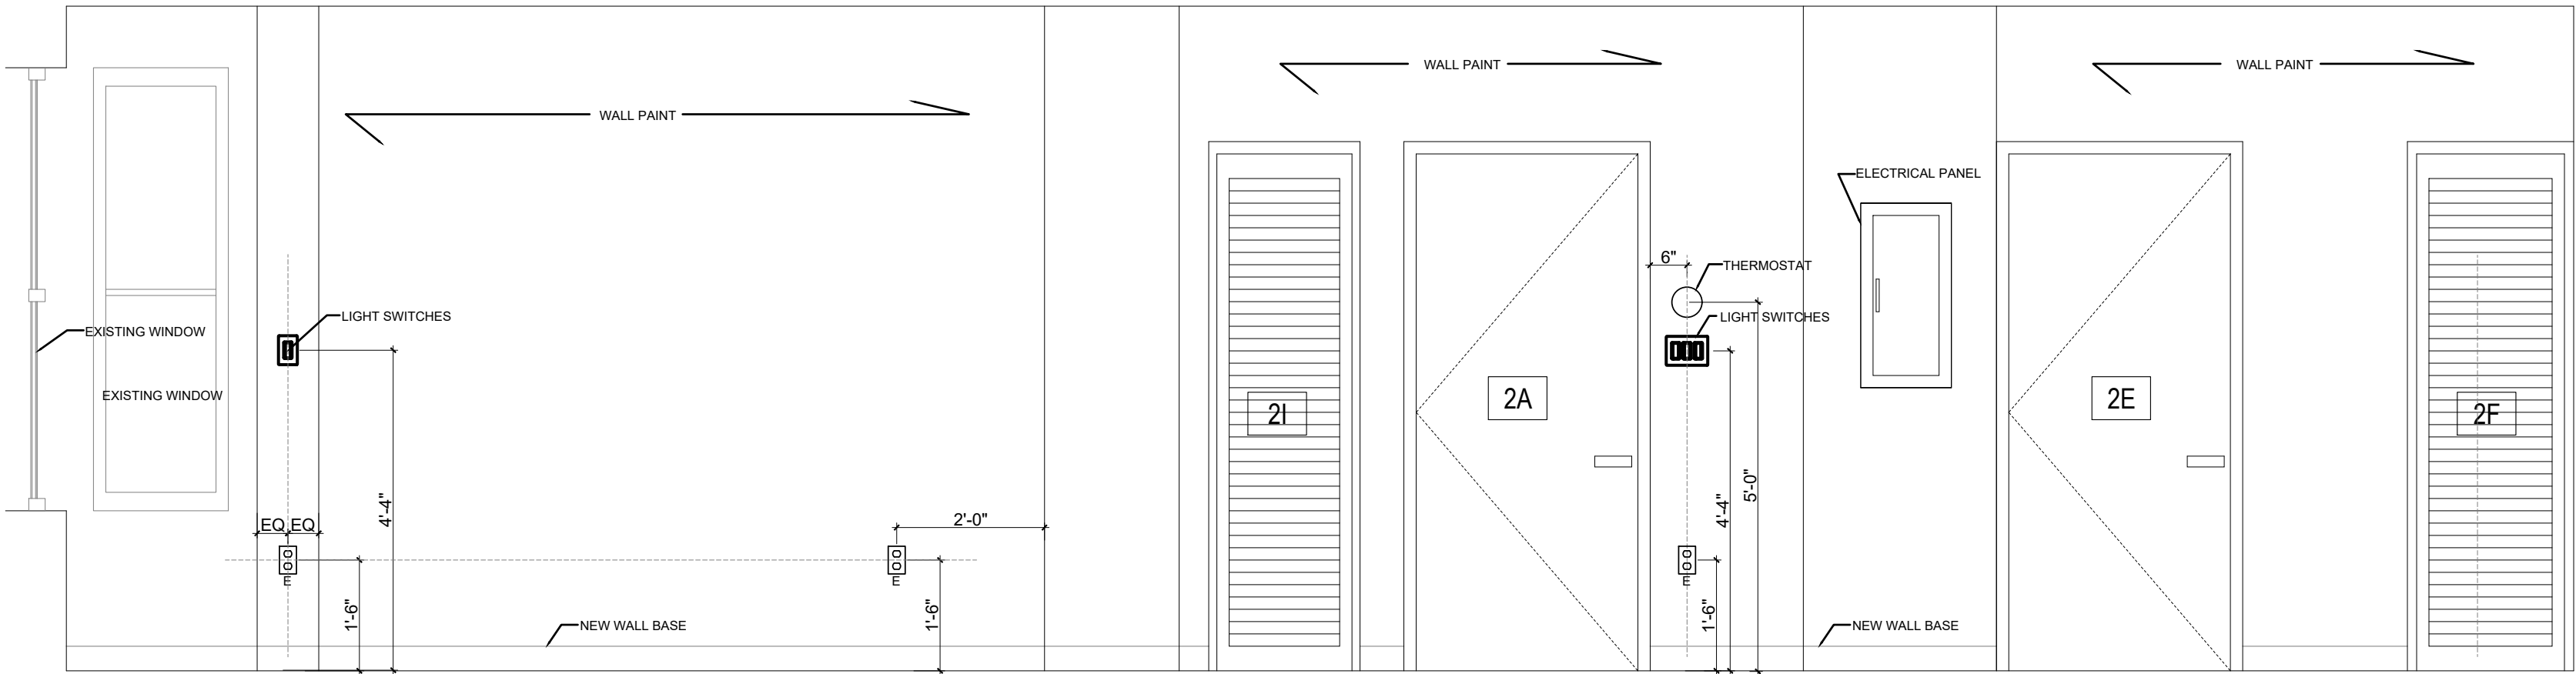

02 SECOND FLOOR LIVING ROOM & CORRIDOR EAST ELEVATION
1/2" = 1'

PROJECT 103
213 MAPLE STREET
213 MAPLE STREET, WEEHAWKEN, NEW JERSEY, 07086

CONSULTANTS:
STRUCTURAL ENGINEER
FLEX ENGINEERING GROUP LLC
3133 CENTRAL AVE #202, UNION CITY, NJ 07087
T: 201-974-9570
E: flexengineer@yahoo.com

MECHANICAL ENGINEER
FLEX ENGINEERING GROUP LLC
3133 CENTRAL AVE #202, UNION CITY, NJ 07087
T: 201-974-9570
E: flexengineer@yahoo.com

GENERAL CONTRACTOR
HOBOKEN KITCHEN & BATH
2 14TH ST PH 32, HOBOKEN NJ, 07030
T: 201-472-0425
E: theodore@hobokenkitchenandbath.com

#	DATE	DESCRIPTION
---	------	-------------

DOB STAMP AND SIGNATURE

SEAL AND SIGNATURE


CONTRACTOR SHALL ONLY UTILIZE WRITTEN DIMENSIONS. CONTRACTOR SHALL VERIFY AND BE RESPONSIBLE FOR ALL MEASUREMENTS AND CONDITIONS ON THE JOB. AND OWNER MUST BE NOTIFIED OF ANY VARIATIONS FROM DIMENSIONS AND CONDITIONS SHOWN BY THESE DRAWINGS. SCALED SHOP DRAWINGS MUST BE SUBMITTED TO OWNER FOR APPROVAL, BEFORE PROCEEDING WITH ANY FABRICATION.

ALL DRAWINGS, SPECIFICATIONS, ETC. CONTRIBUTED TO CONTRACTORS, BIDDERS, GOVERNMENTAL AGENCIES, ETC. ARE NOT FOR GENERAL USE OR PUBLICATION BY OTHERS. ALL RIGHTS RESERVED. NONE OF THE IDEAS, DESIGN, ARRANGEMENTS OR PLANS IN THESE DRAWINGS SHALL BE USED BY OR DISCLOSED TO ANY PERSONS, FIRM OR CORPORATION FOR ANY PURPOSE WITHOUT THE WRITTEN PERMISSION OF OWNER.


DRAWING TITLE:
I-103
INTERIOR ELEVATION -
SECOND FLOOR

FOR CONSTRUCTION


ALL MILLWORK CABINETRY MATERIAL AND INSTALLATION BY OWNER
IN WALL WOOD BLOCKING FOR ALL CABINETRY BY HKB

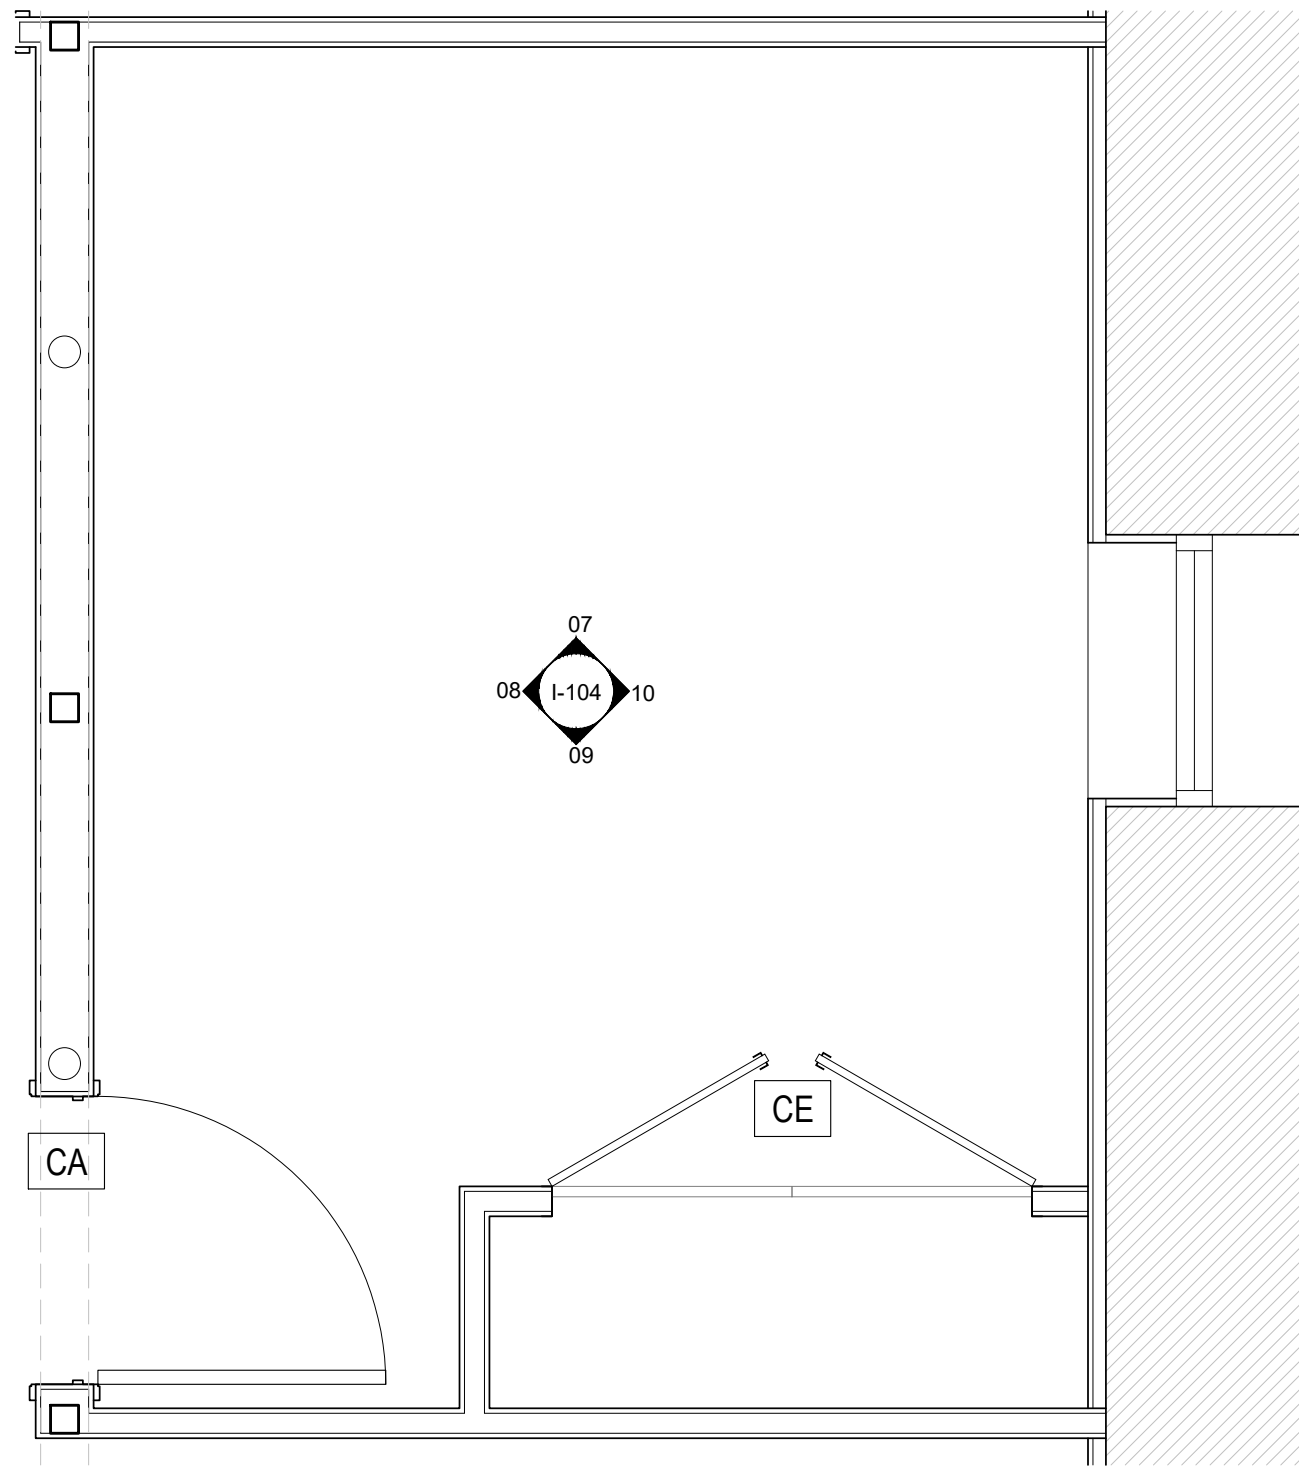


06 CELLAR SMALL STORAGE ROOM ENLARGED PLAN
1/2" = 1'

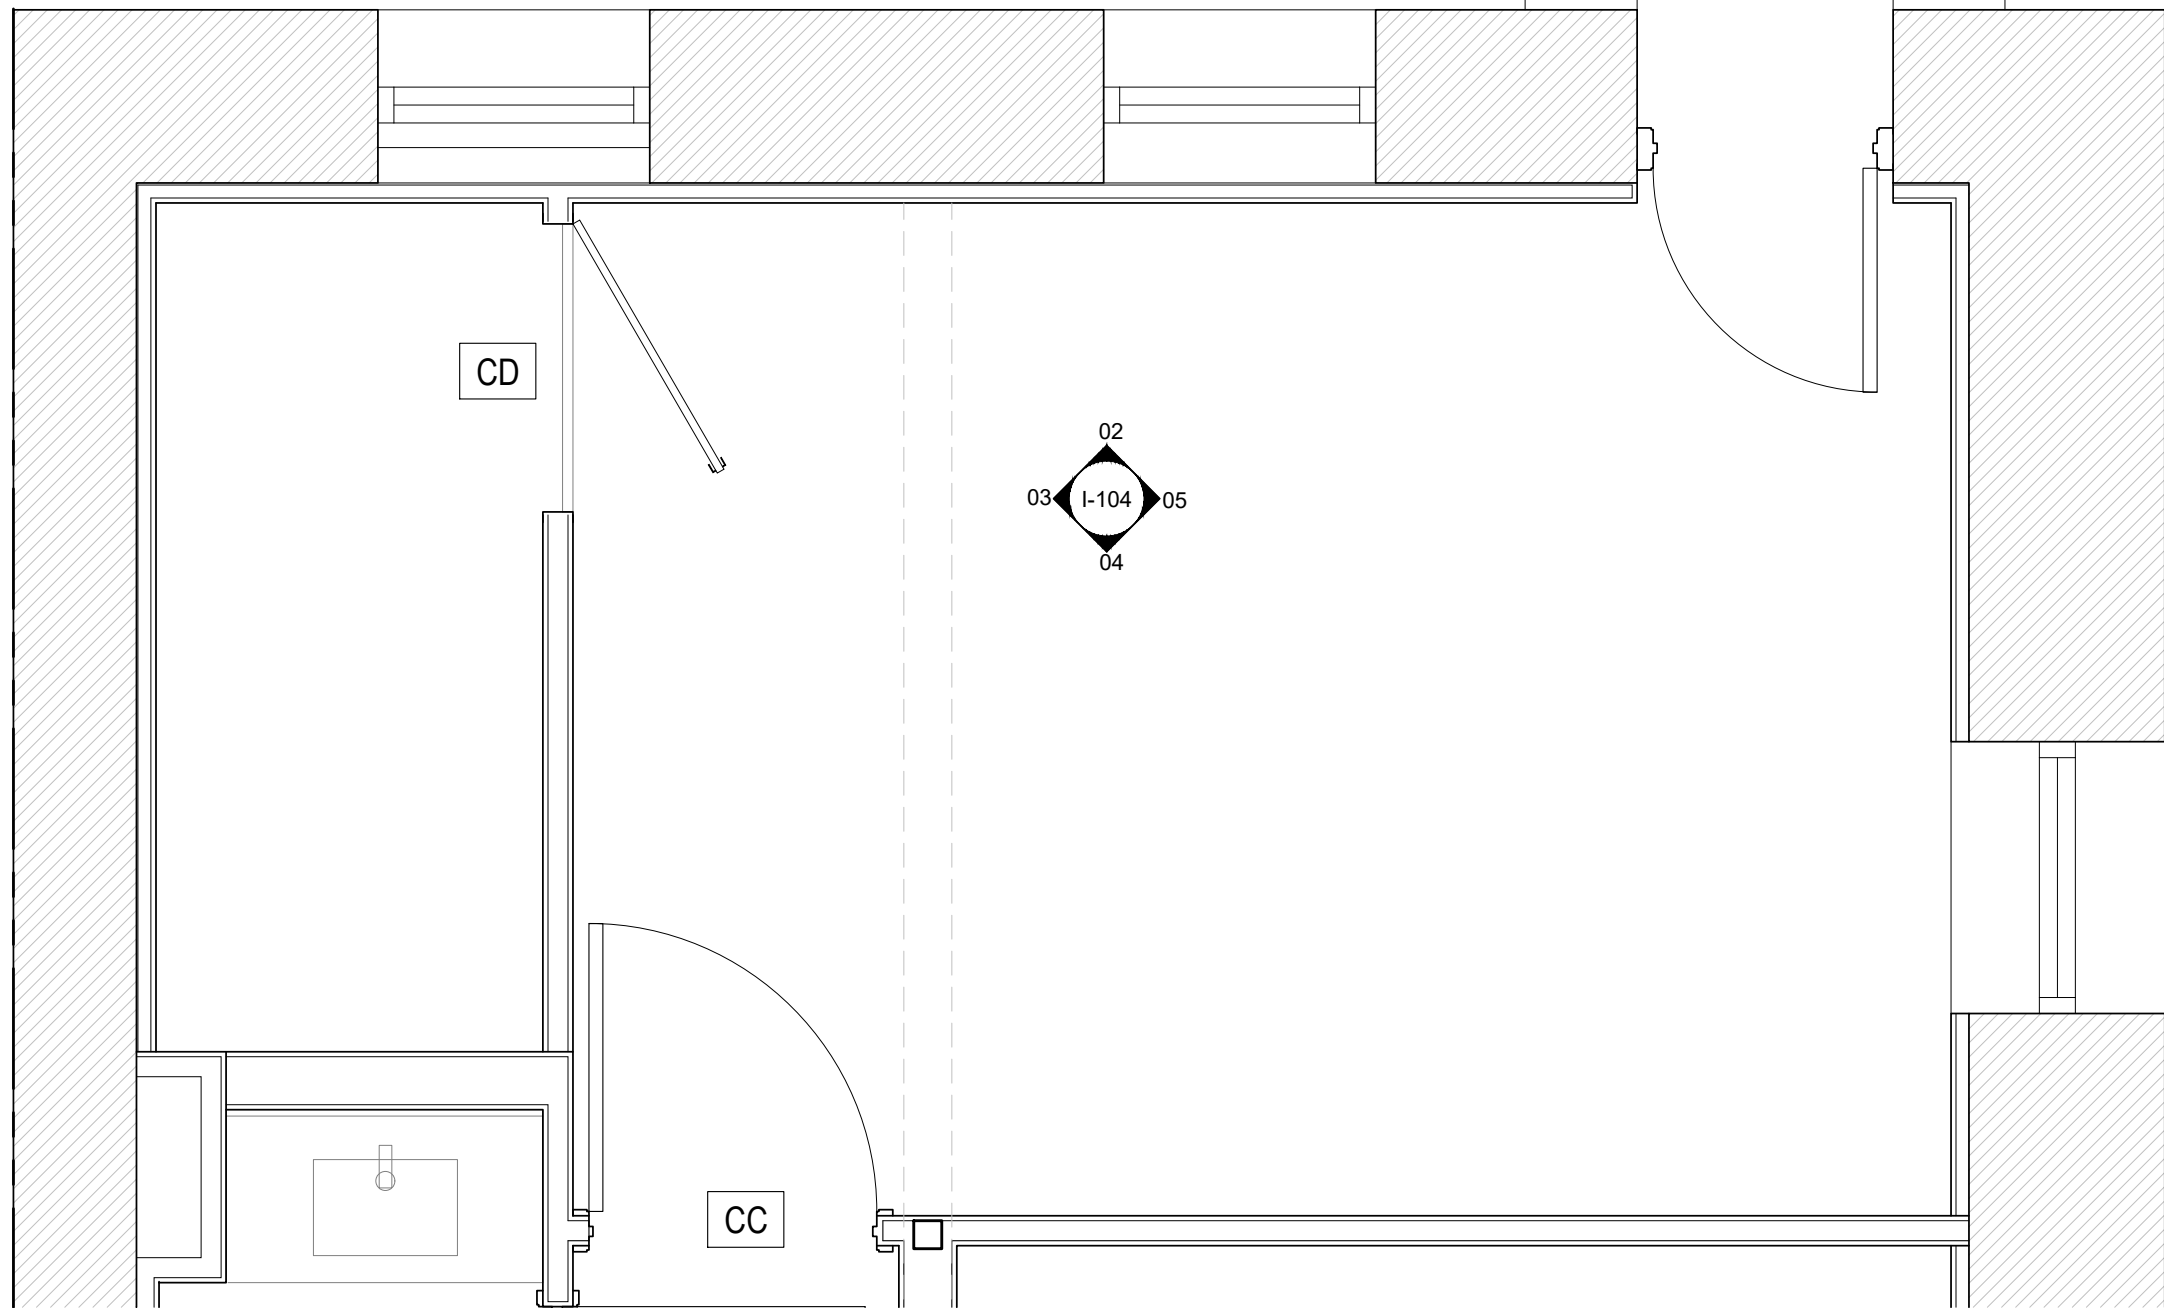


01 CELLAR LARGE STORAGE ROOM ENLARGED PLAN
1/2" = 1'

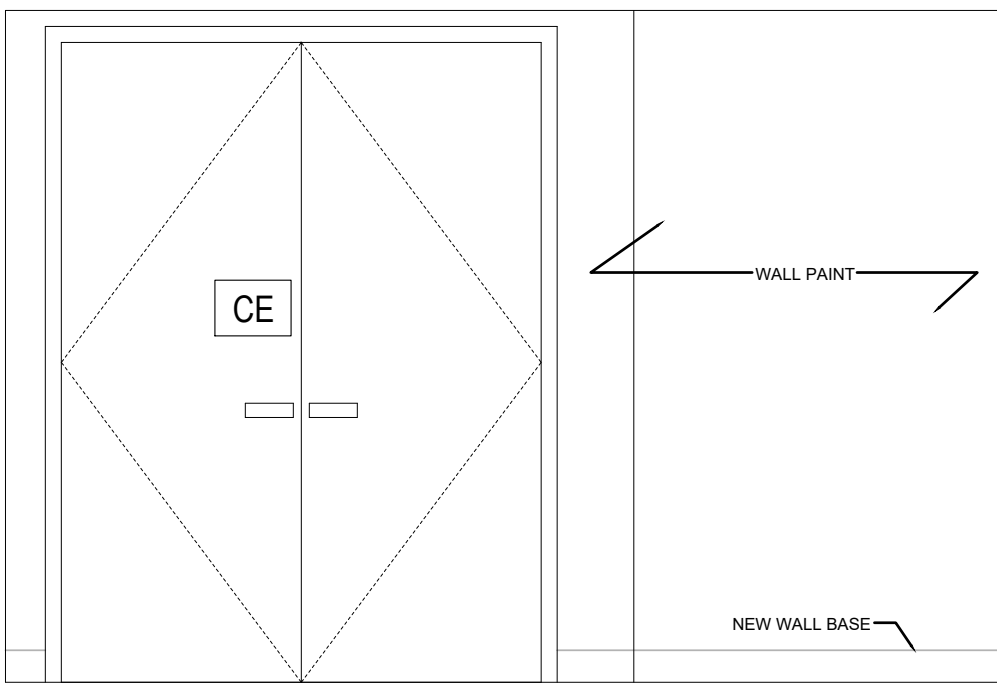


09 CELLAR SMALL STORAGE ROOM NORTH ELEVATION
1/2" = 1'

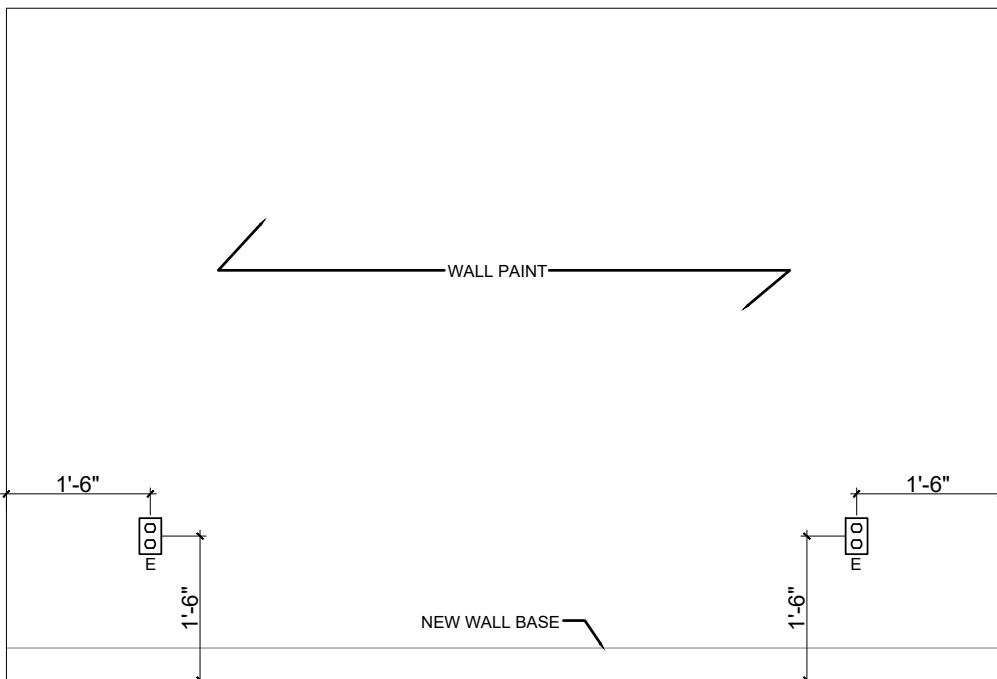


07 CELLAR SMALL STORAGE ROOM SOUTH ELEVATION
1/2" = 1'

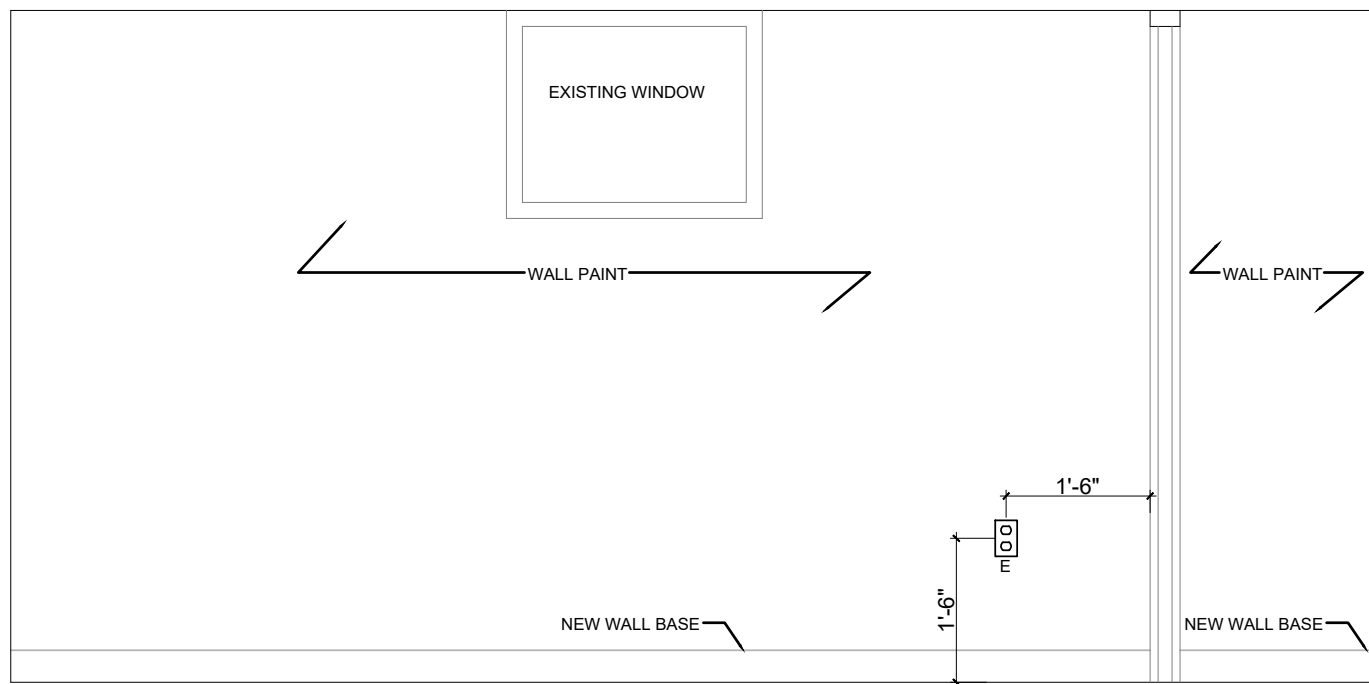


10 CELLAR SMALL STORAGE ROOM WEST ELEVATION
1/2" = 1'

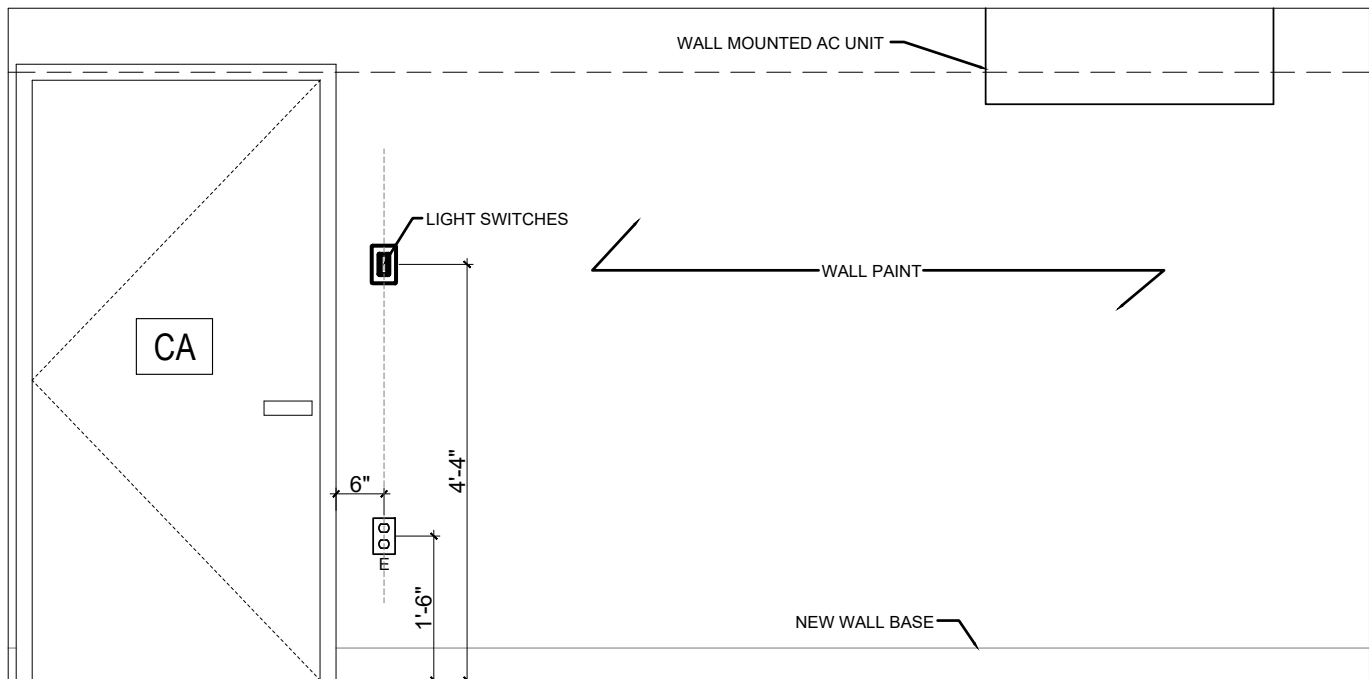


08 CELLAR SMALL STORAGE ROOM EAST ELEVATION
1/2" = 1'

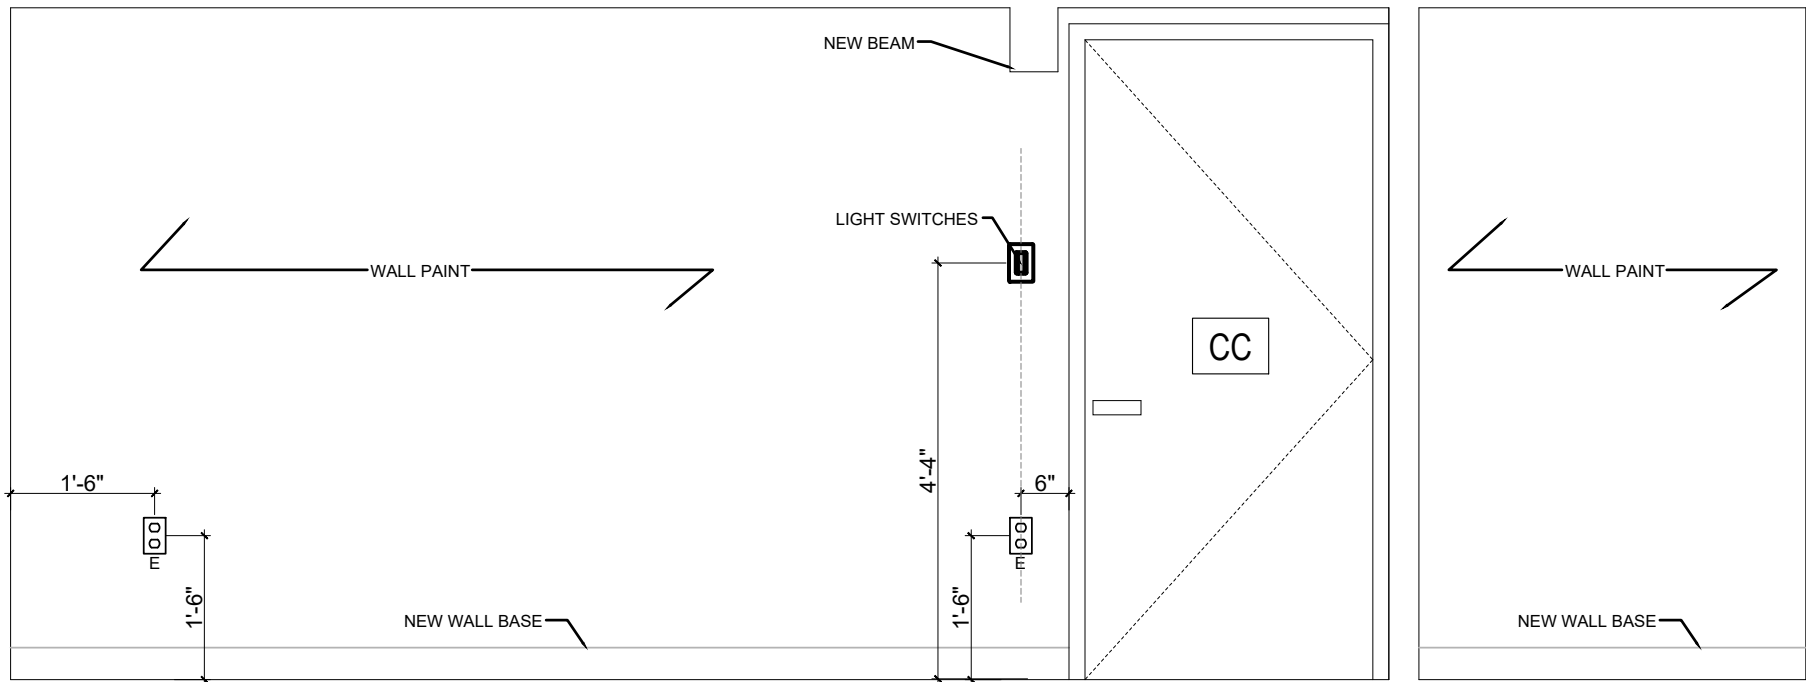


04 CELLAR LARGE STORAGE ROOM NORTH ELEVATION
1/2" = 1'

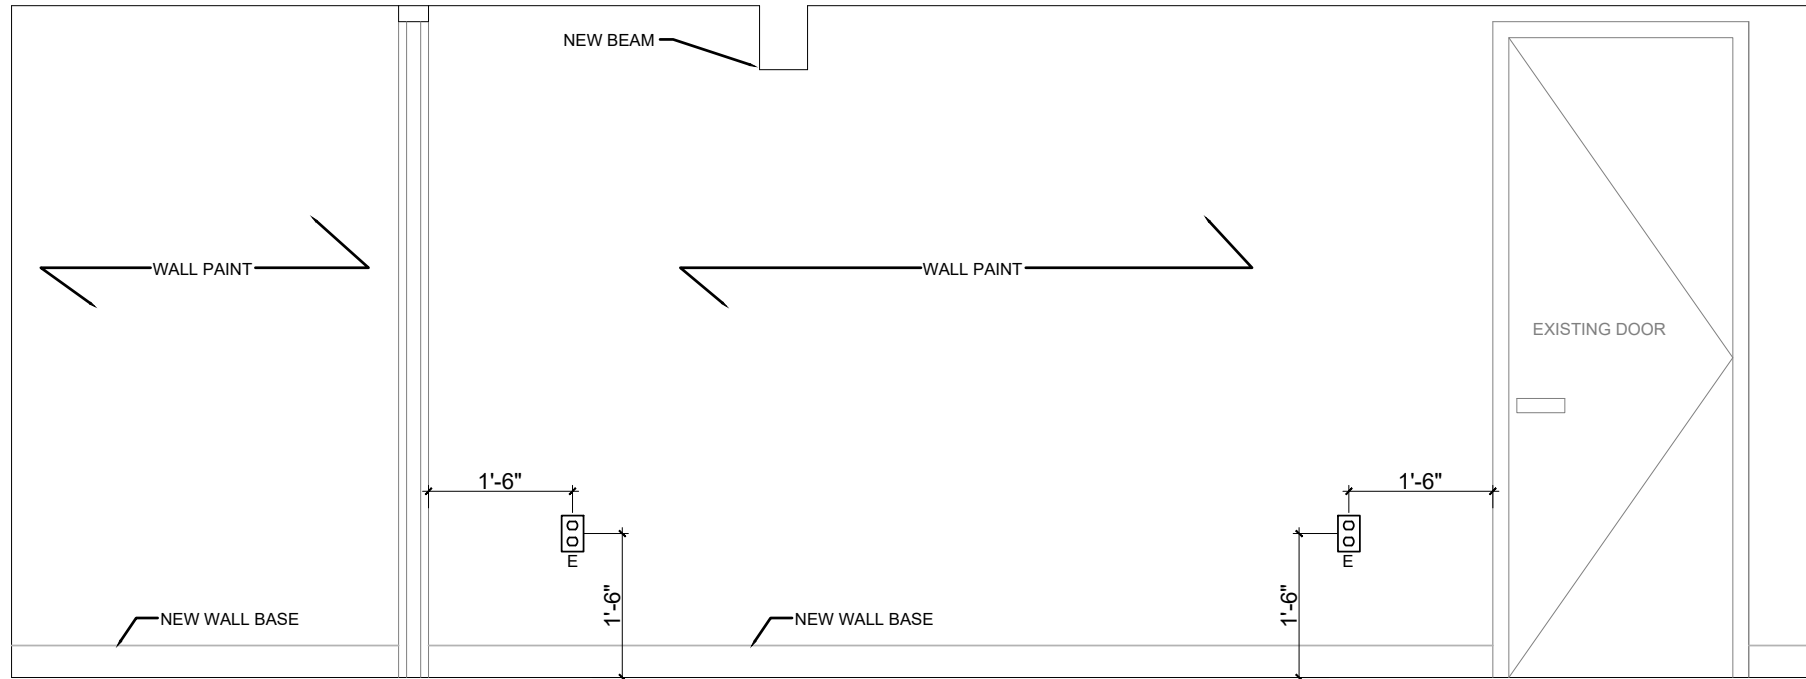

02 CELLAR LARGE STORAGE ROOM SOUTH ELEVATION
1/2" = 1'

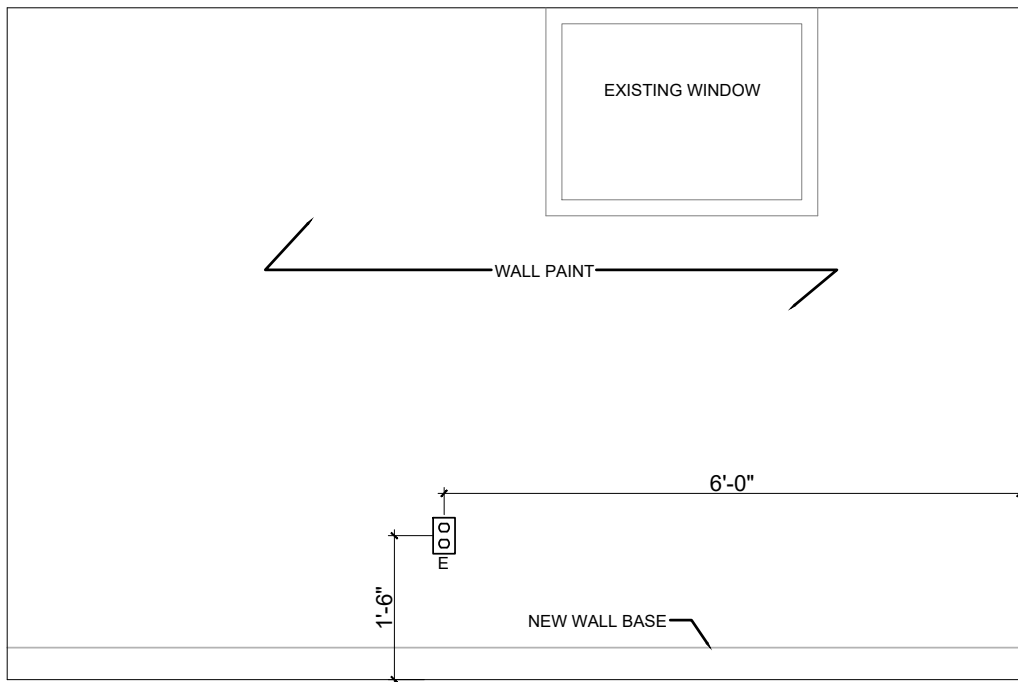

05 CELLAR LARGE STORAGE ROOM WEST ELEVATION
1/2" = 1'

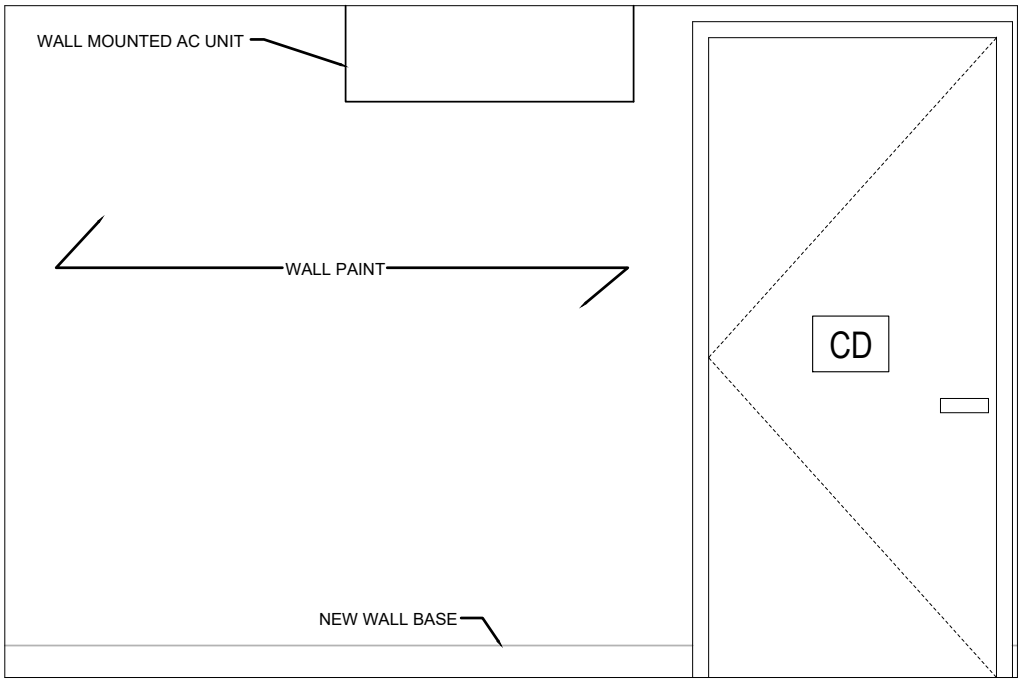

03 CELLAR LARGE STORAGE ROOM EAST ELEVATION
1/2" = 1'

PROJECT 103

213 MAPLE STREET

213 MAPLE STREET, WEEHAWKEN, NEW JERSEY, 07086

CONSULTANTS:

STRUCTURAL ENGINEER
FLEX ENGINEERING GROUP LLC
3133 CENTRAL AVE #202, UNION CITY, NJ 07087
T: 201-974-9570
E: flexengineer@yahoo.com

MECHANICAL ENGINEER
FLEX ENGINEERING GROUP LLC
3133 CENTRAL AVE #202, UNION CITY, NJ 07087
T: 201-974-9570
E: flexengineer@yahoo.com

GENERAL CONTRACTOR
HOBOKEN KITCHEN & BATH
2 14TH ST PH 32, HOBOKEN NJ, 07030
T: 201-472-0425
E: theodore@hobokenkitchenandbath.com

DATE DESCRIPTION

DOB STAMP AND SIGNATURE

SEAL AND SIGNATURE

CONTRACTORS SHALL ONLY UTILIZE WRITTEN DIMENSIONS. CONTRACTORS SHALL VERIFY AND BE RESPONSIBLE FOR ALL DIMENSIONS AND CONDITIONS ON THE JOB, AND DIMENSIONS MUST BE NOTIFIED OF ANY VARIATIONS FROM DIMENSIONS AND CONDITIONS SHOWN BY THESE DRAWINGS. SCALED SHOP DRAWINGS MUST BE SUBMITTED TO OWNER FOR APPROVAL, BEFORE PROCEEDING WITH ANY FABRICATION.

ALL DRAWINGS, SPECIFICATIONS, ETC. CONTRIBUTED TO CONTRACTORS, BIDDERS, GOVERNMENTAL AGENCIES, ETC. ARE NOT FOR GENERAL USE OR PUBLICATION BY OTHERS. ALL RIGHTS RESERVED. NONE OF THE IDEAS, DESIGN, ARRANGEMENTS OR PLANS IN THESE DRAWINGS SHALL BE USED BY OR DISCLOSED TO ANY PERSONS, FIRM OR CORPORATION FOR ANY PURPOSE WITHOUT THE CURRENT AND WRITTEN PERMISSION OF OWNER.

DRAWING TITLE:

I-104

INTERIOR ELEVATION -
CELLAR

FOR CONSTRUCTION


ALL MILLWORK CABINETRY MATERIAL AND INSTALLATION BY OWNER
IN WALL WOOD BLOCKING FOR ALL CABINETRY BY HKB

PROJECT 103
213 MAPLE STREET
213 MAPLE STREET, WEEHAWKEN, NEW JERSEY, 07086


CONSULTANTS:
STRUCTURAL ENGINEER
FLEX ENGINEERING GROUP LLC
3133 CENTRAL AVE #202, UNION CITY, NJ 07087
T: 201-974-9570
E: flexengineer@yahoo.com

MECHANICAL ENGINEER
FLEX ENGINEERING GROUP LLC
3133 CENTRAL AVE #202, UNION CITY, NJ 07087
T: 201-974-9570
E: flexengineer@yahoo.com


GENERAL CONTRACTOR
HOBOKEN KITCHEN & BATH
2 14TH ST PH 32, HOBOKEN NJ, 07030
T: 201-472-0425
E: theodore@hobokenkitchenandbath.com

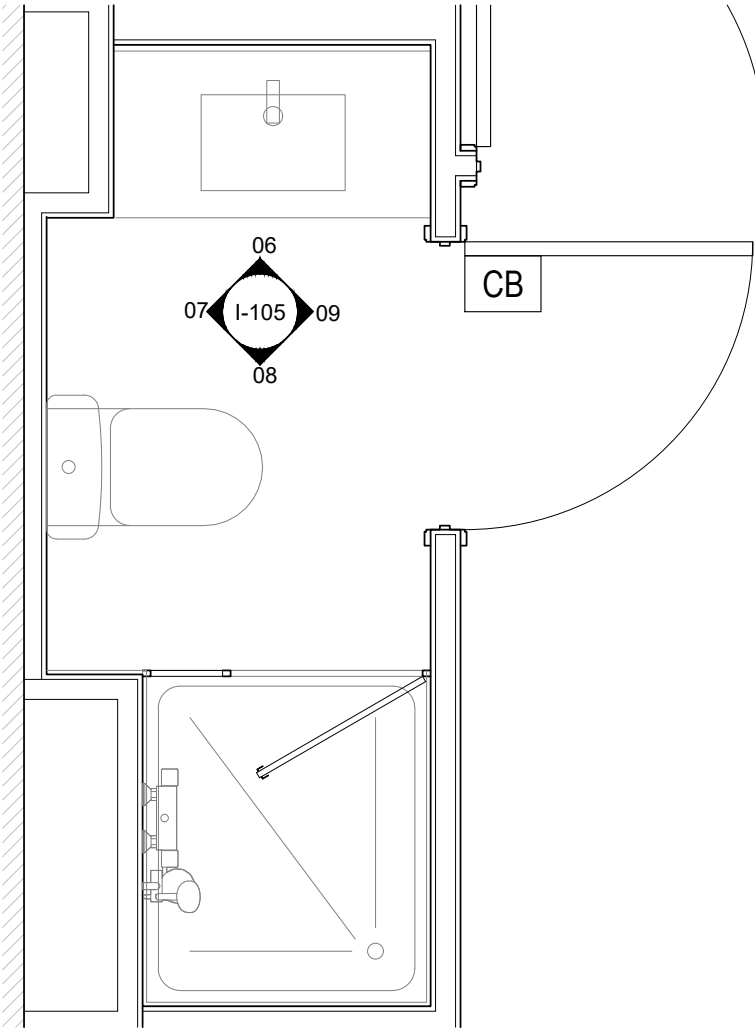


05 CELLAR TOILET ENLARGED PLAN
1/2" = 1'

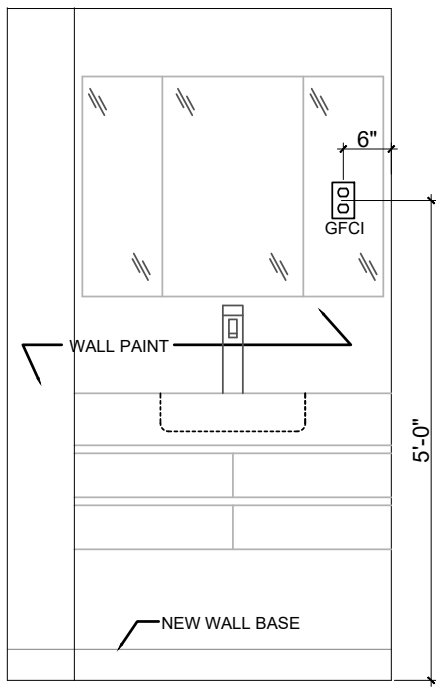


06 CELLAR TOILET SOUTH ELEVATION
1/2" = 1'

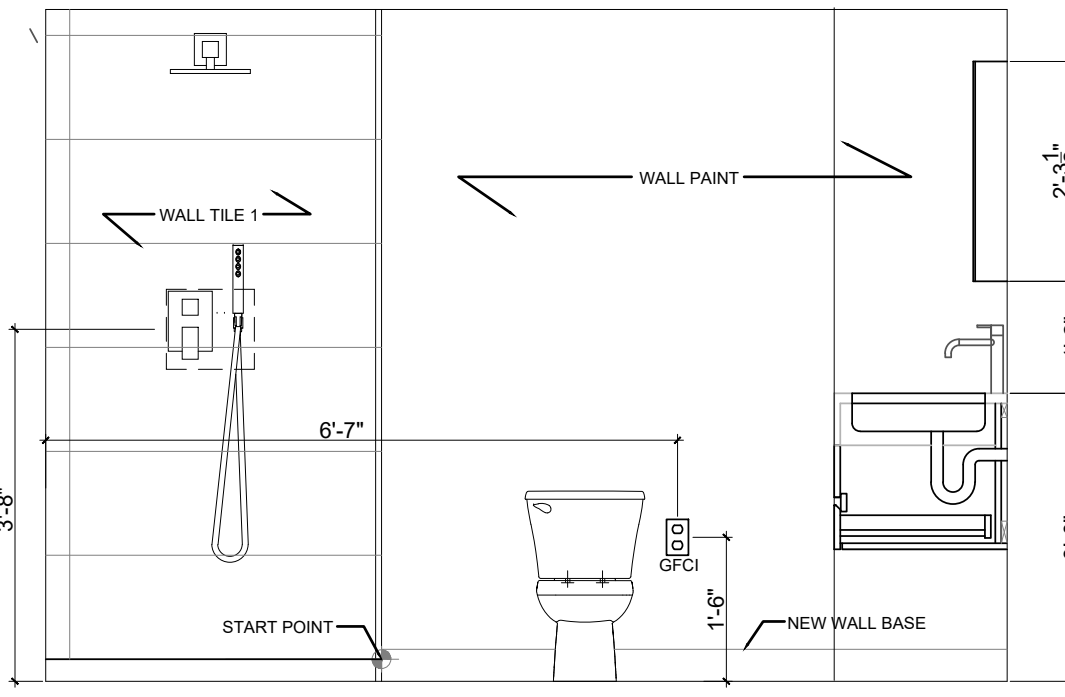


07 CELLAR TOILET EAST ELEVATION
1/2" = 1'

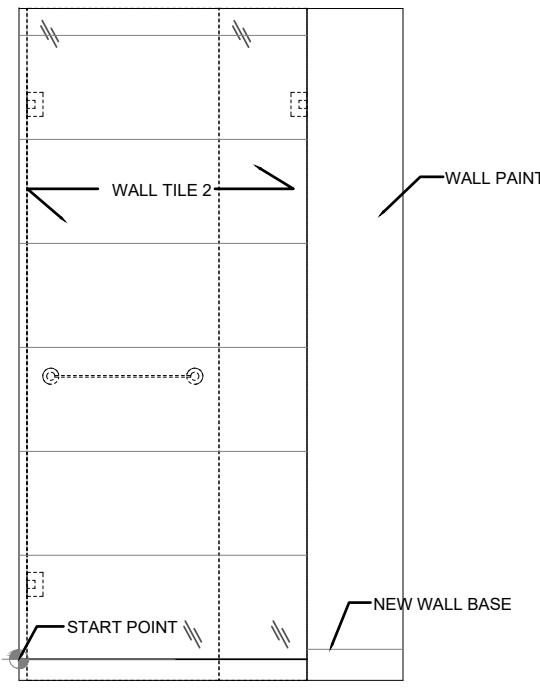


08 CELLAR TOILET NORTH ELEVATION
1/2" = 1'

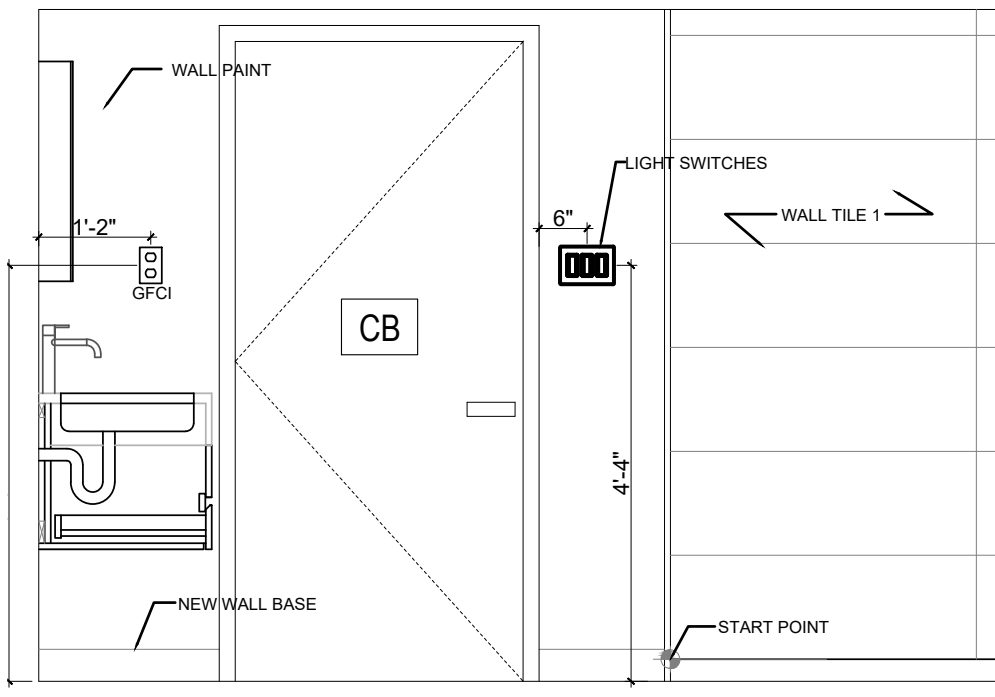


09 CELLAR TOILET WEST ELEVATION
1/2" = 1'

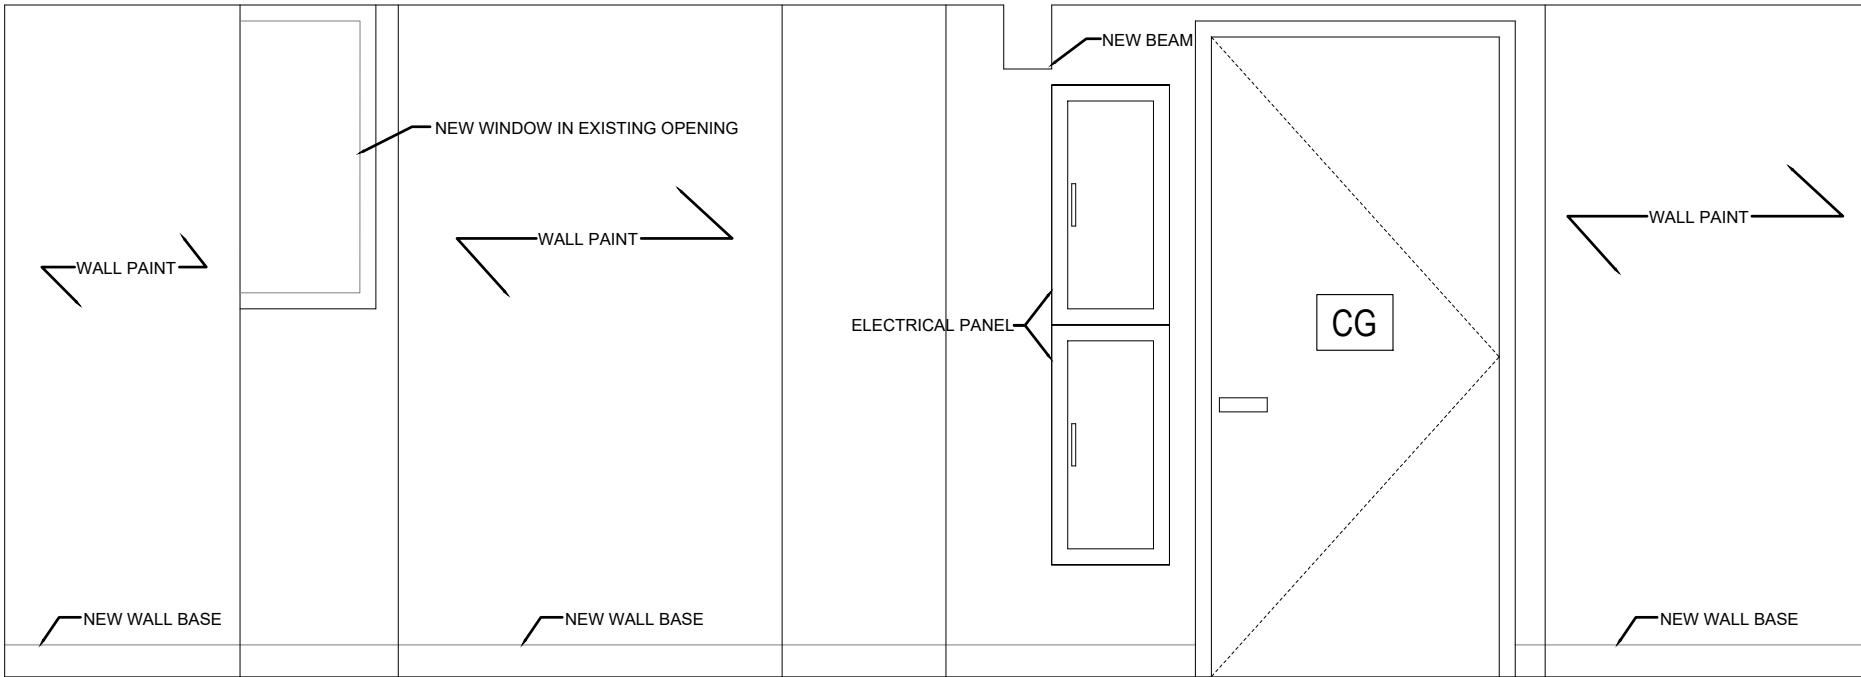


03 SECOND FLOOR LIVING ROOM NORTH ELEVATION
1/2" = 1'

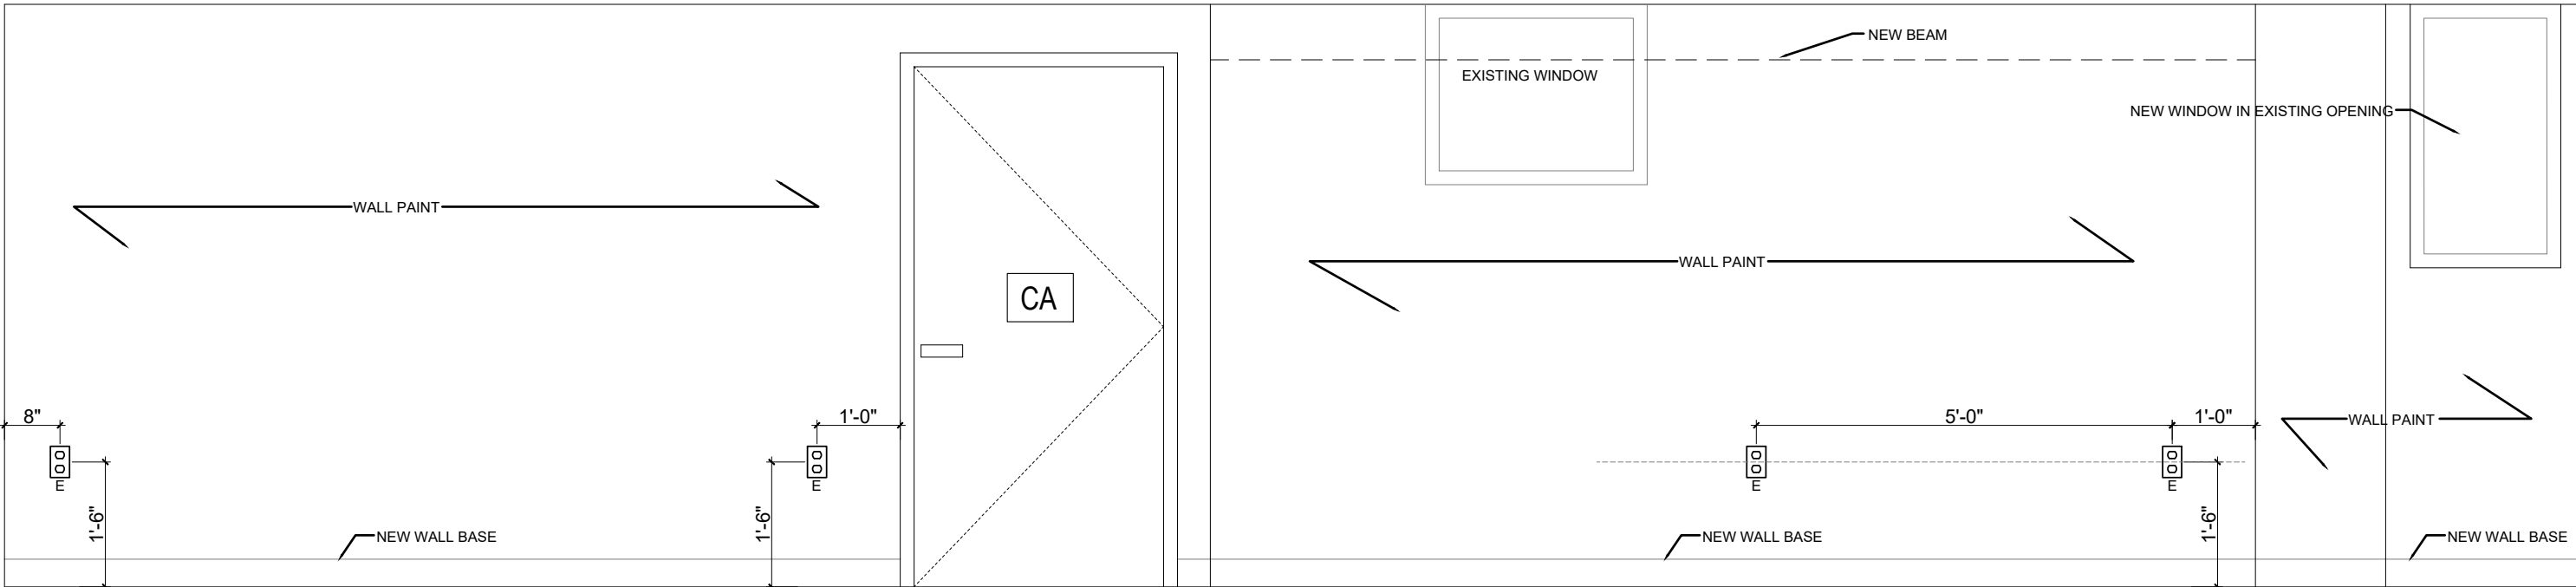

04 SECOND FLOOR LIVING ROOM & CORRIDOR WEST ELEVATION
1/2" = 1'

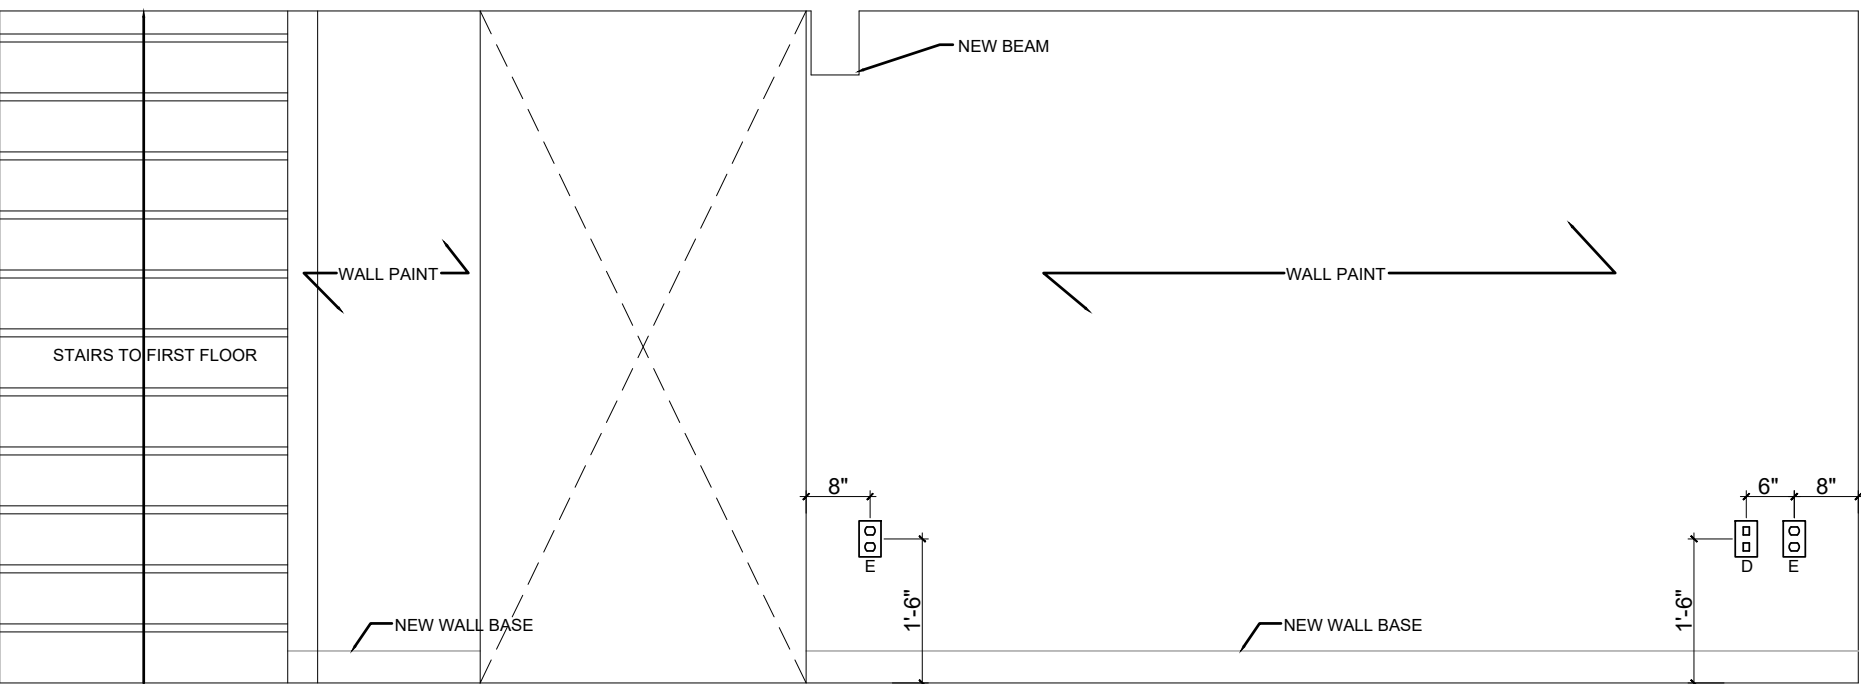

01 CELLAR RECREATION SPACE SOUTH ELEVATION
1/2" = 1'

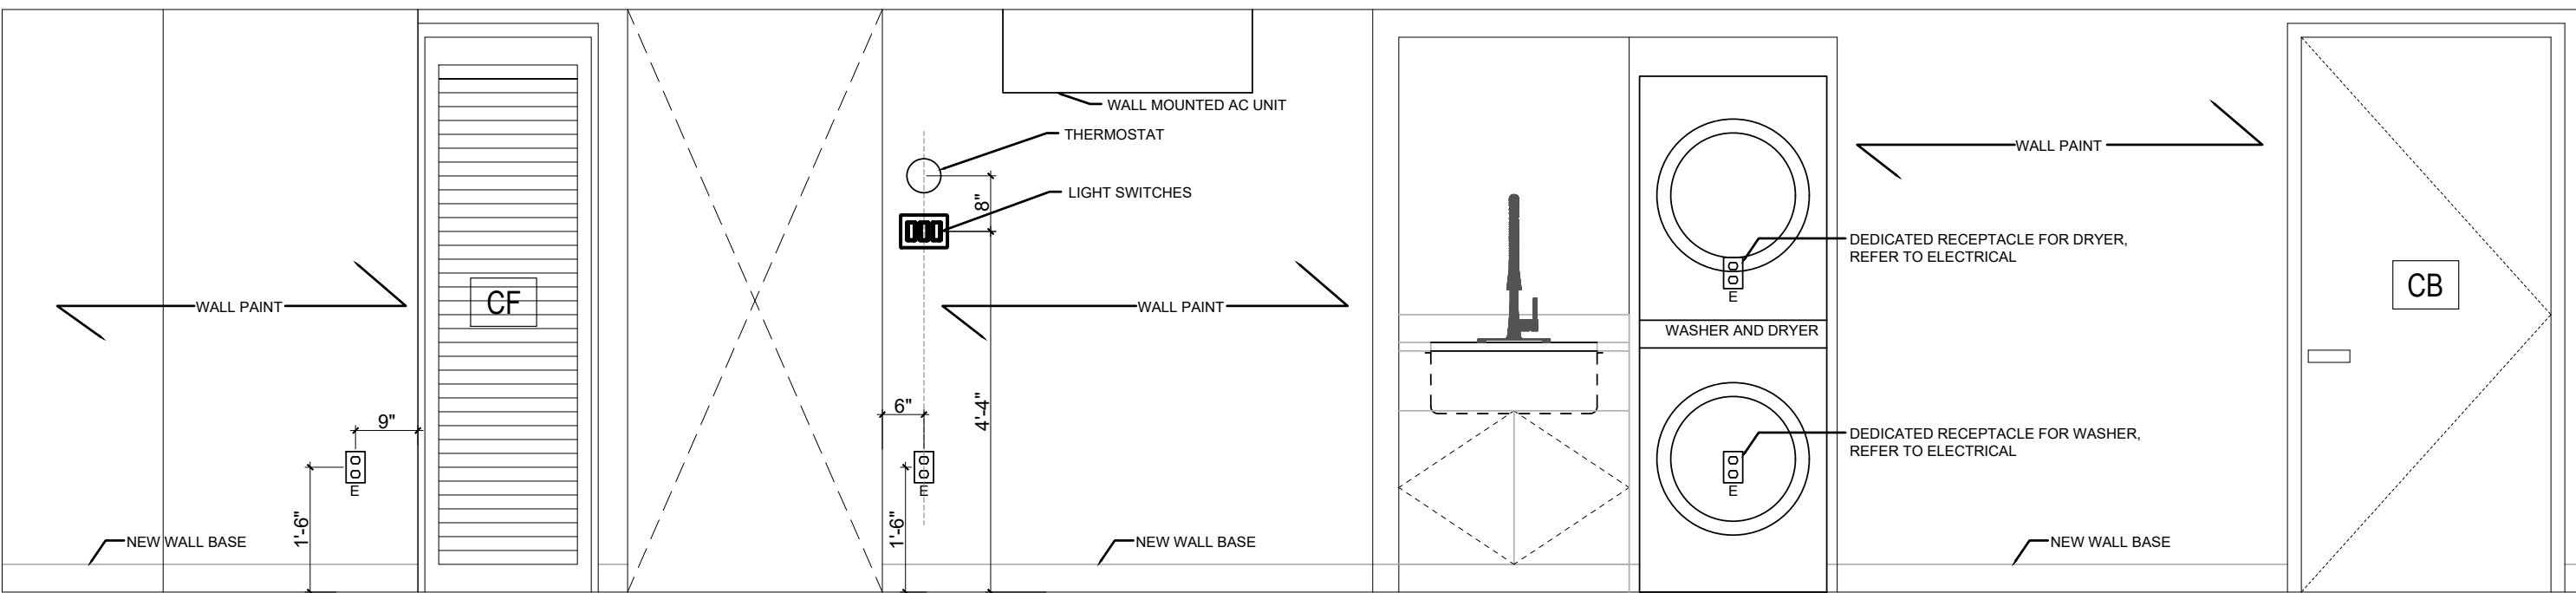

02 CELLAR RECREATION SPACE EAST ELEVATION
1/2" = 1'

#	DATE	DESCRIPTION
DOB STAMP AND SIGNATURE		
SEAL AND SIGNATURE		
DRAWING TITLE: I-105 INTERIOR ELEVATION - CELLAR FOR CONSTRUCTION		








ALL MILLWORK CABINETRY MATERIAL AND INSTALLATION BY OWNER
IN WALL WOOD BLOCKING FOR ALL CABINETRY BY HKB

PROJECT 103
213 MAPLE STREET
213 MAPLE STREET, WEEHAWKEN, NEW JERSEY, 07086

CONSULTANTS:
STRUCTURAL ENGINEER
FLEX ENGINEERING GROUP LLC
3133 CENTRAL AVE #202, UNION CITY, NJ 07087
T: 201-974-9570
E: flexengineer@yahoo.com


MECHANICAL ENGINEER
FLEX ENGINEERING GROUP LLC
3133 CENTRAL AVE #202, UNION CITY, NJ 07087
T: 201-974-9570
E: flexengineer@yahoo.com

GENERAL CONTRACTOR
HOBOKEN KITCHEN & BATH
2 14TH ST PH 32, HOBOKEN NJ, 07030
T: 201-472-0425
E: theodore@hobokenkitchenandbath.com

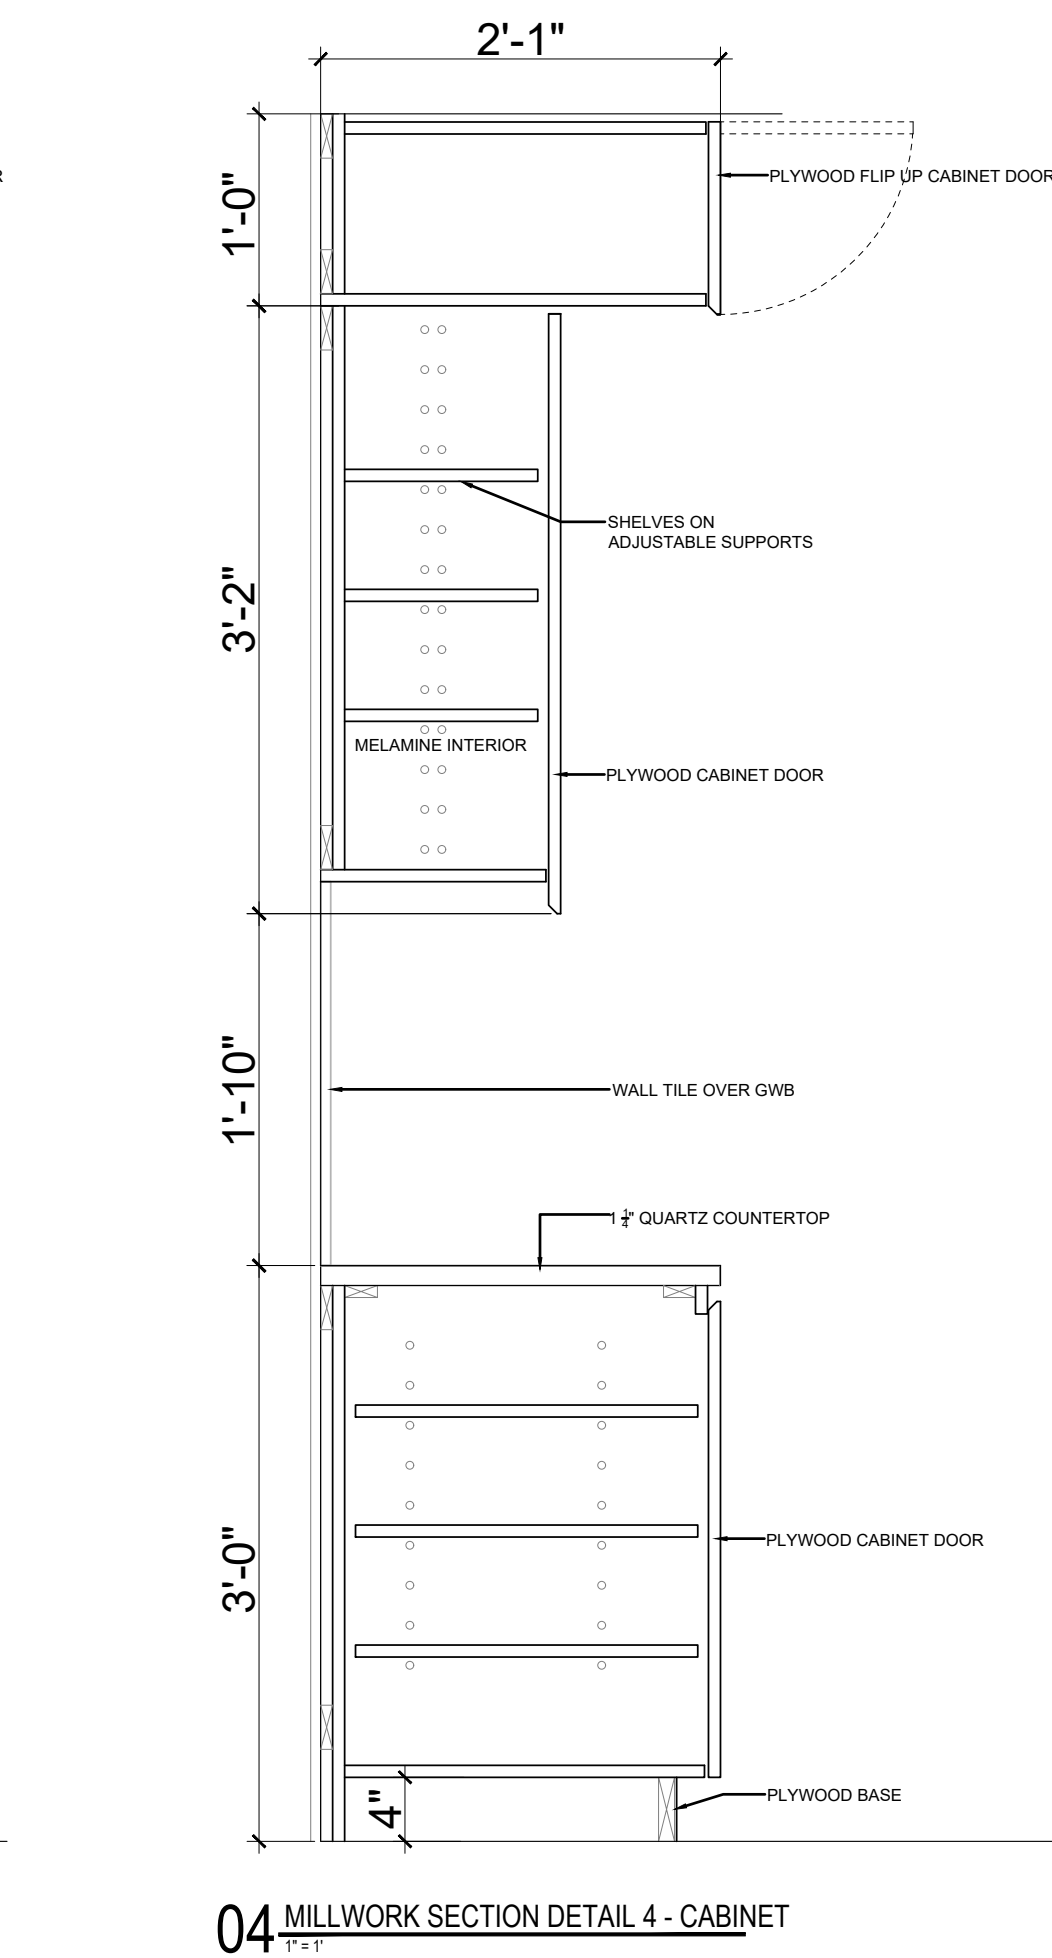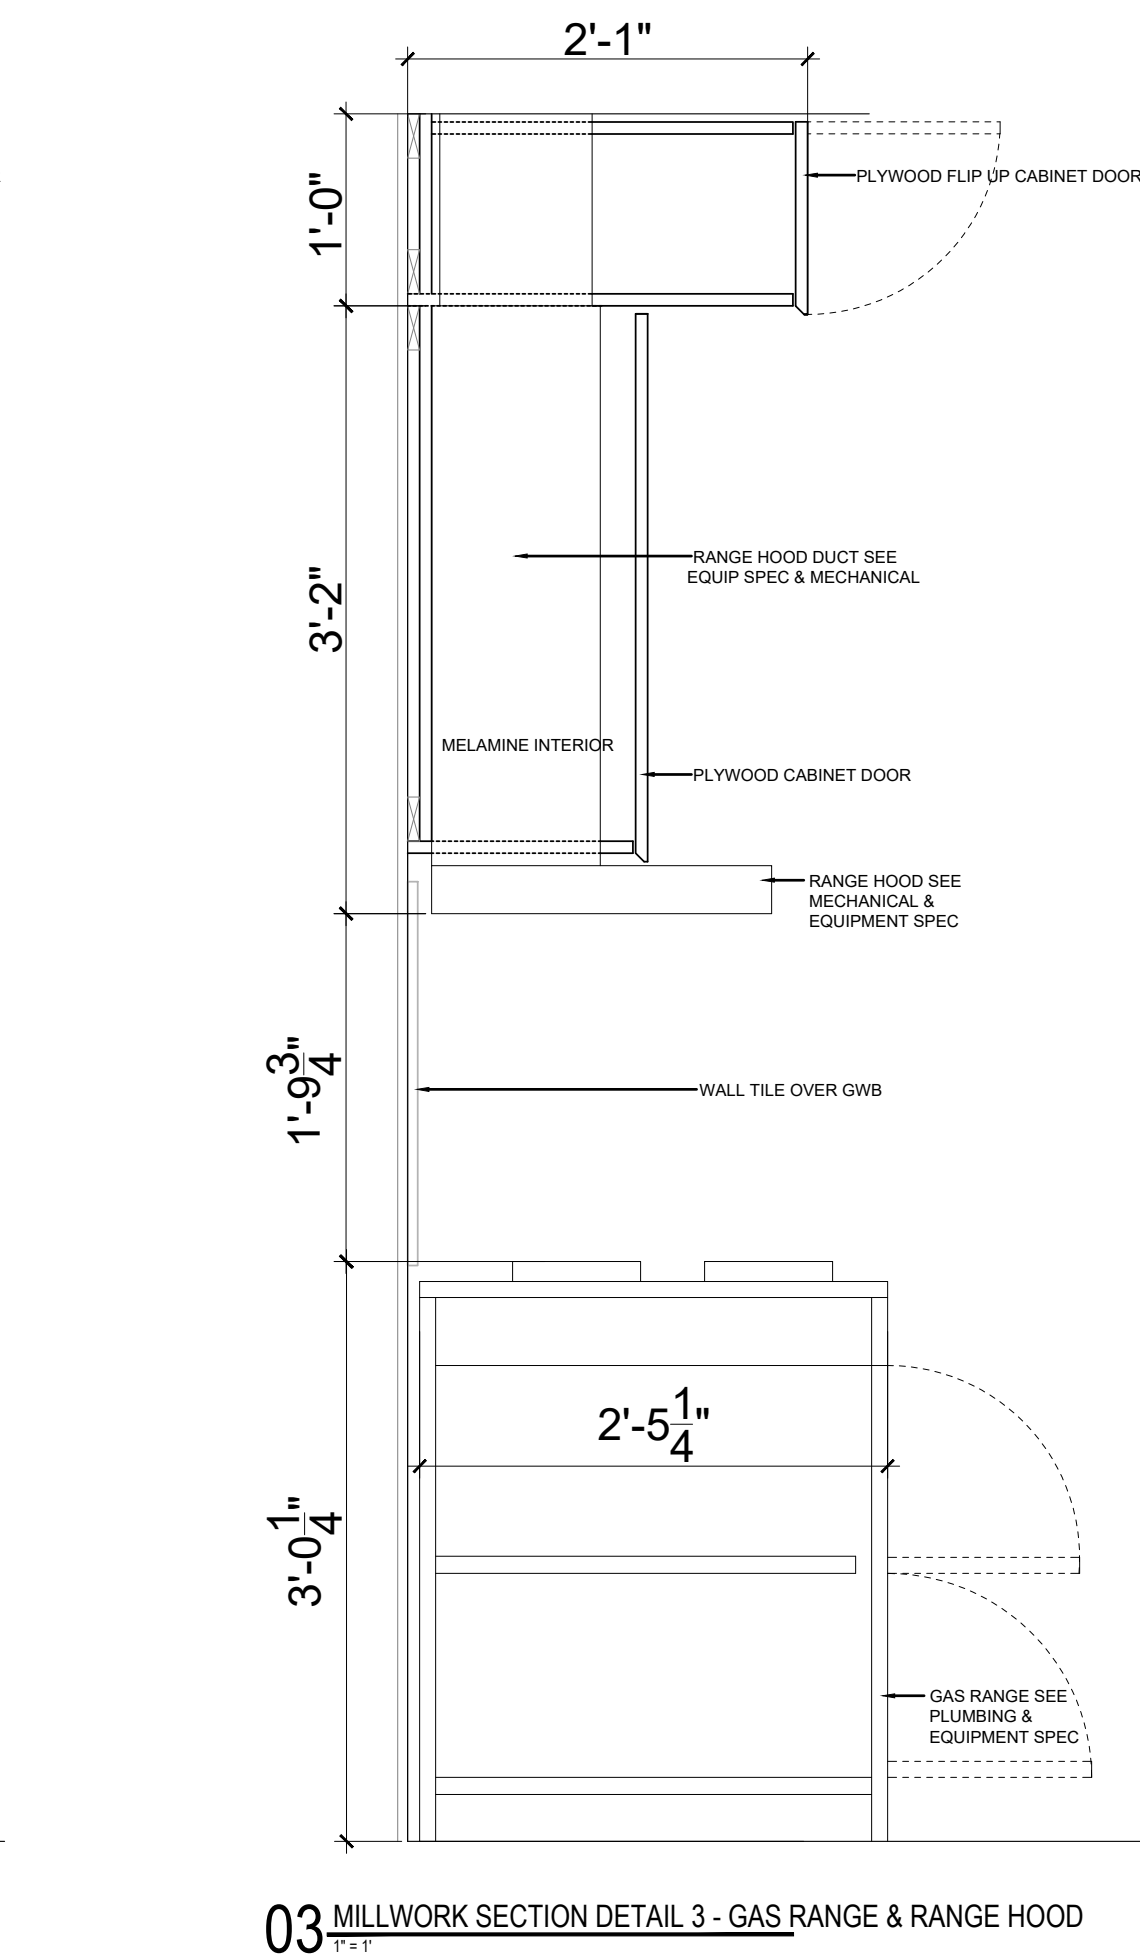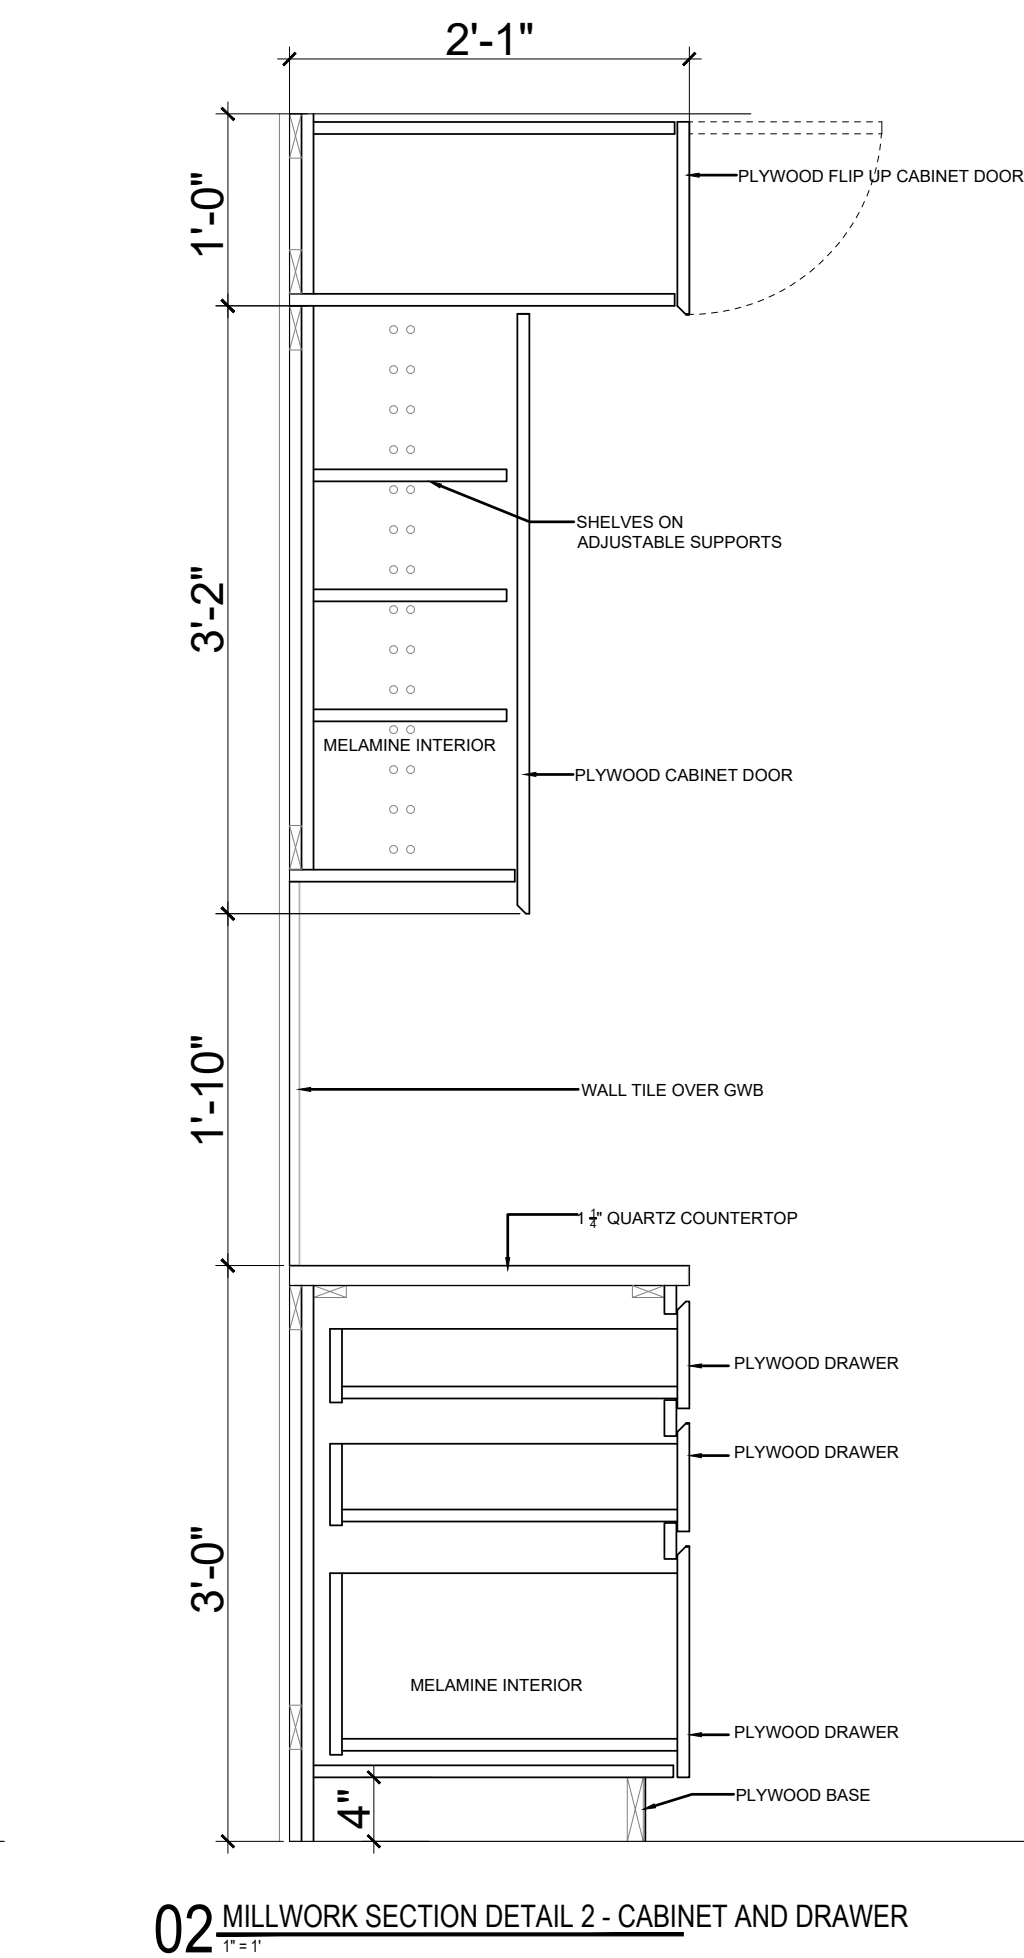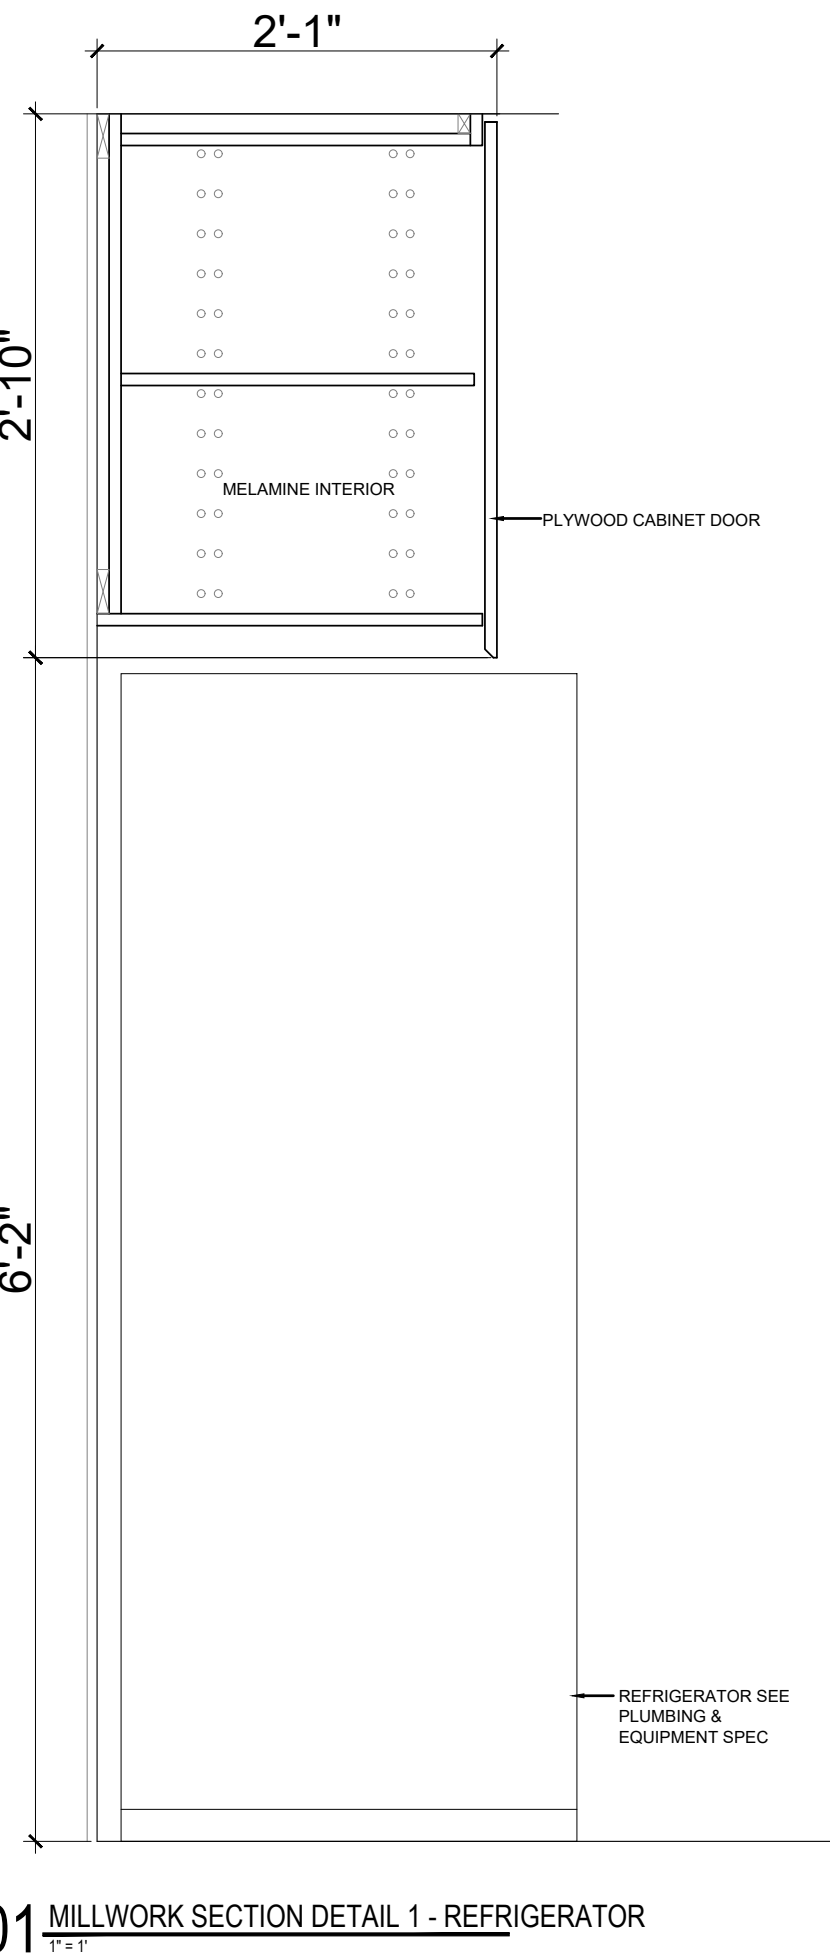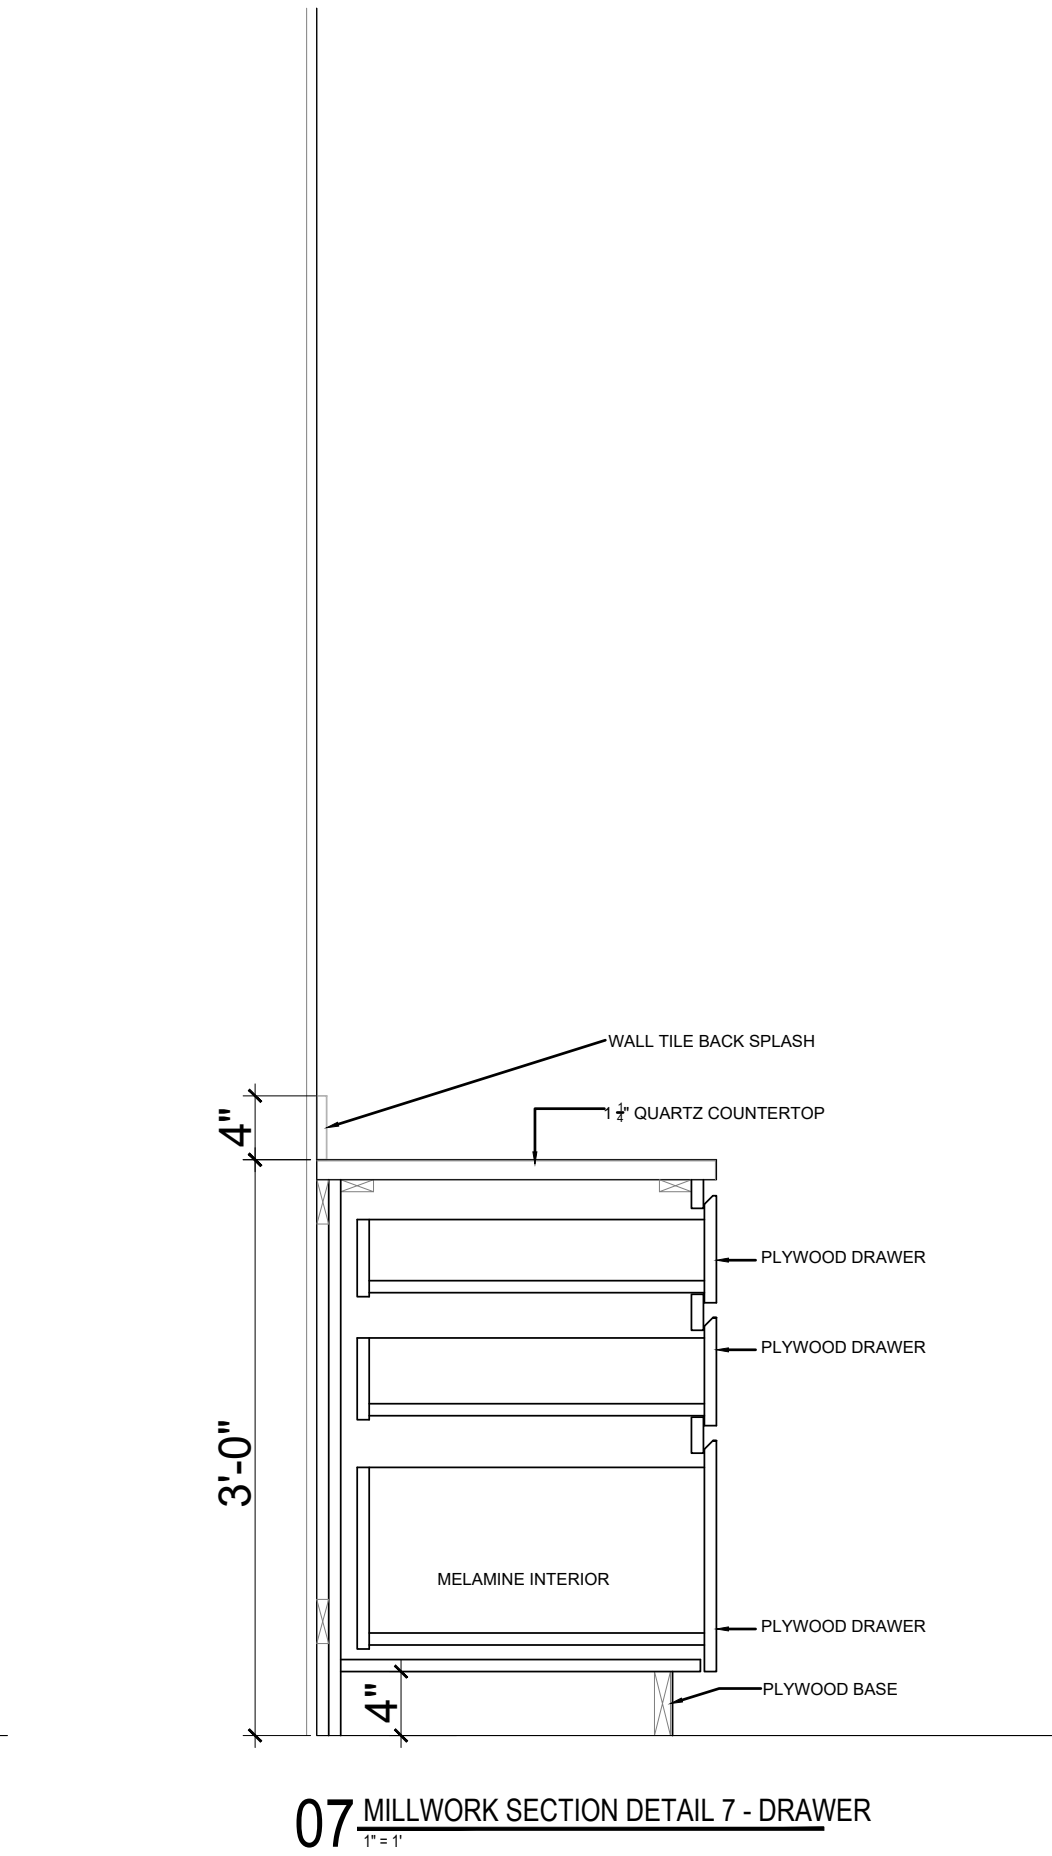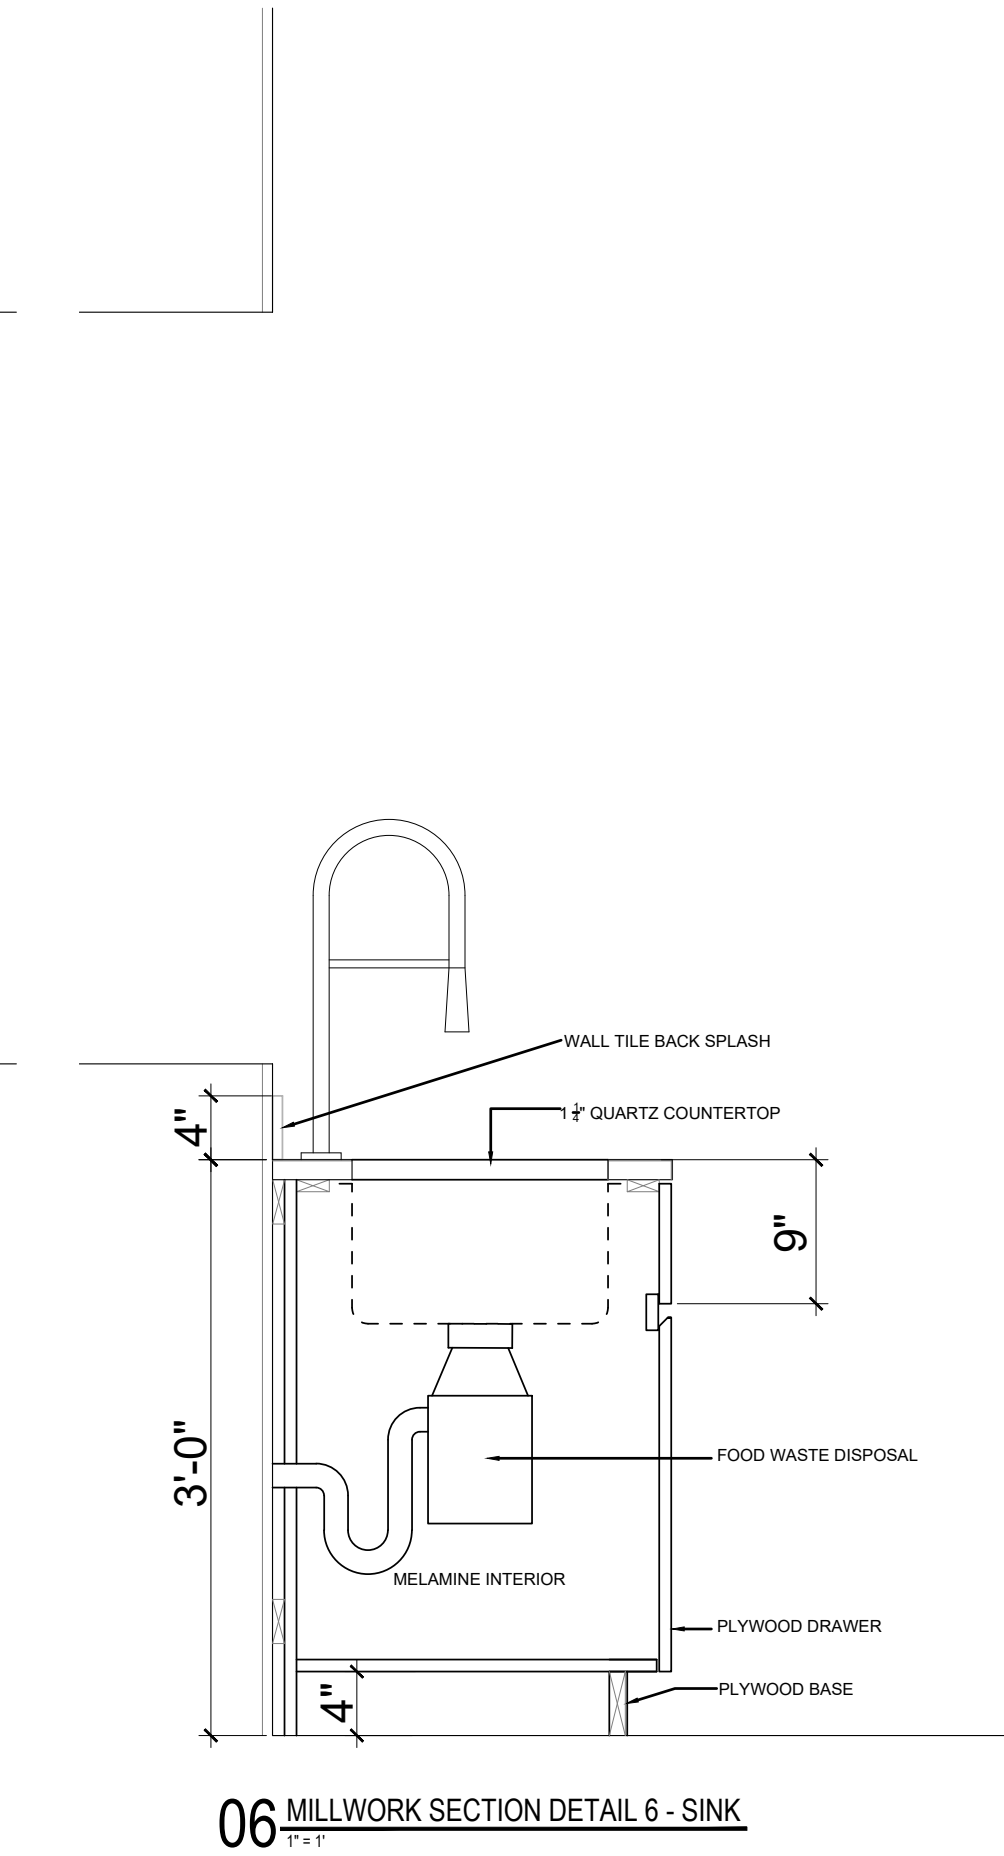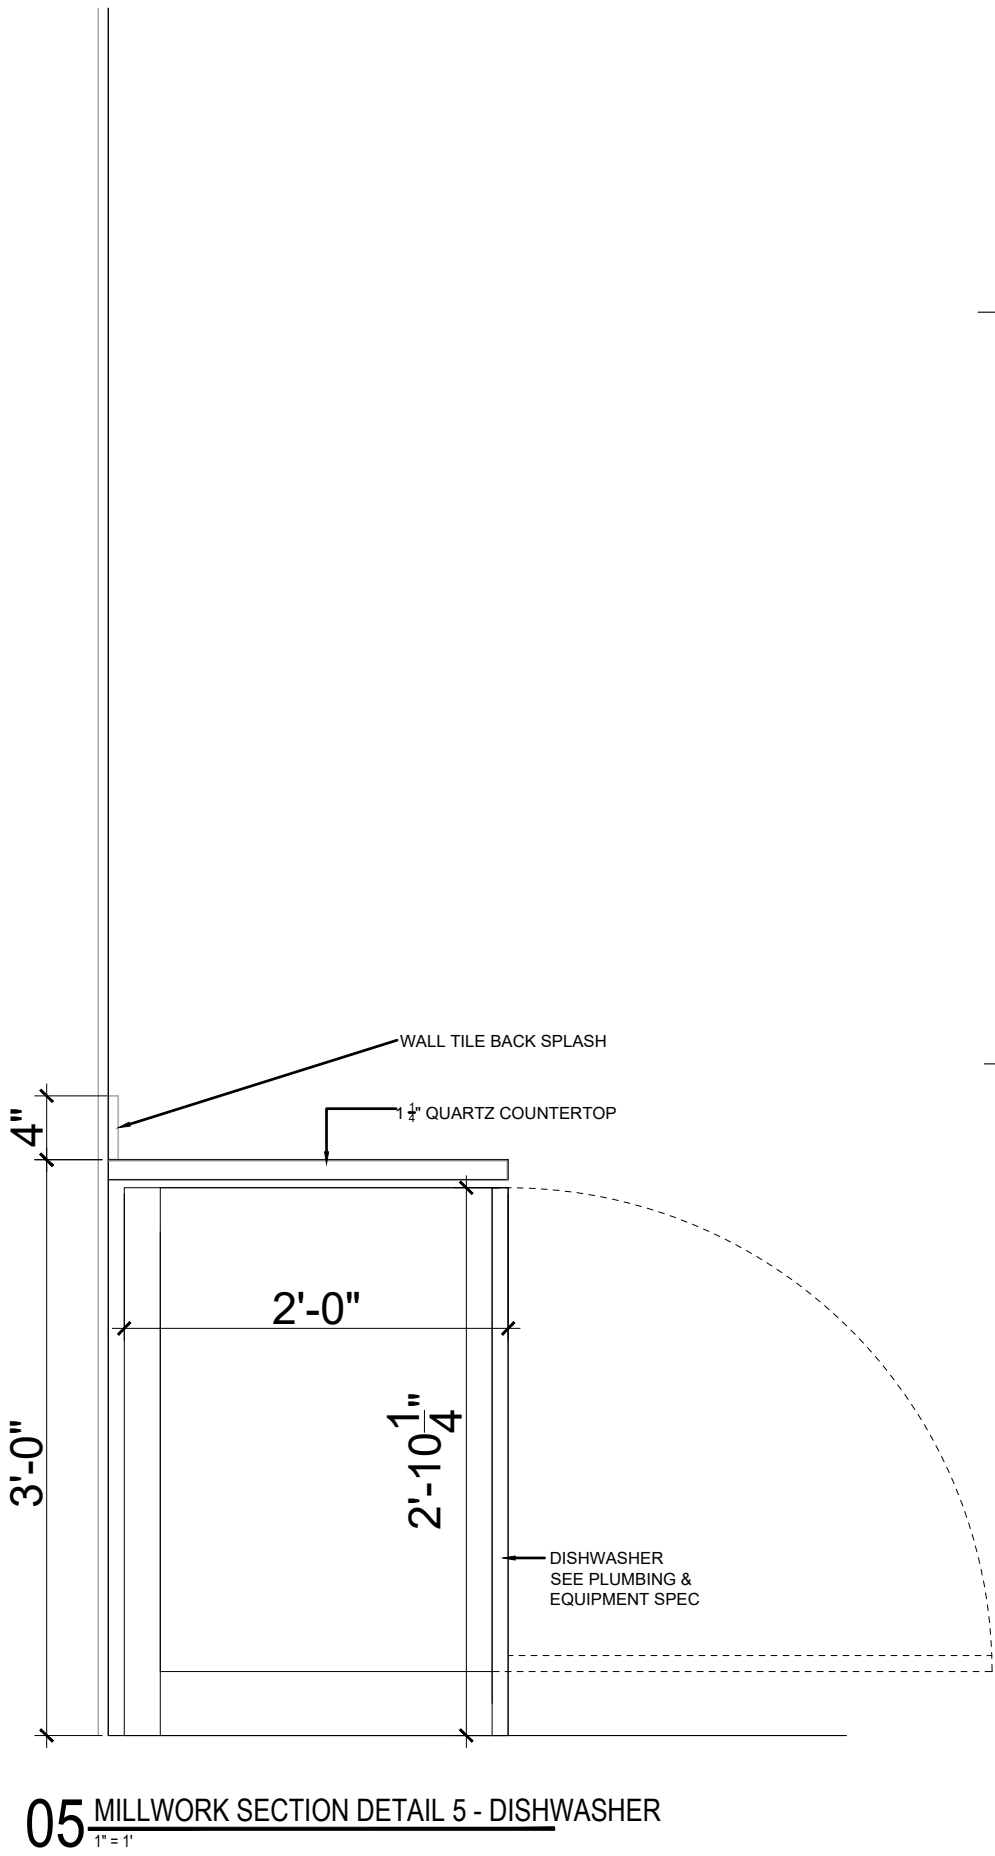


#	DATE	DESCRIPTION
DOB STAMP AND SIGNATURE		
SEAL AND SIGNATURE		
DRAWING TITLE: I-110 MILLWORK SECTION DETAIL - FIRST FLOOR		
FOR CONSTRUCTION		


ALL MILLWORK CABINETRY MATERIAL AND INSTALLATION BY OWNER
IN WALL WOOD BLOCKING FOR ALL CABINETRY BY HKB

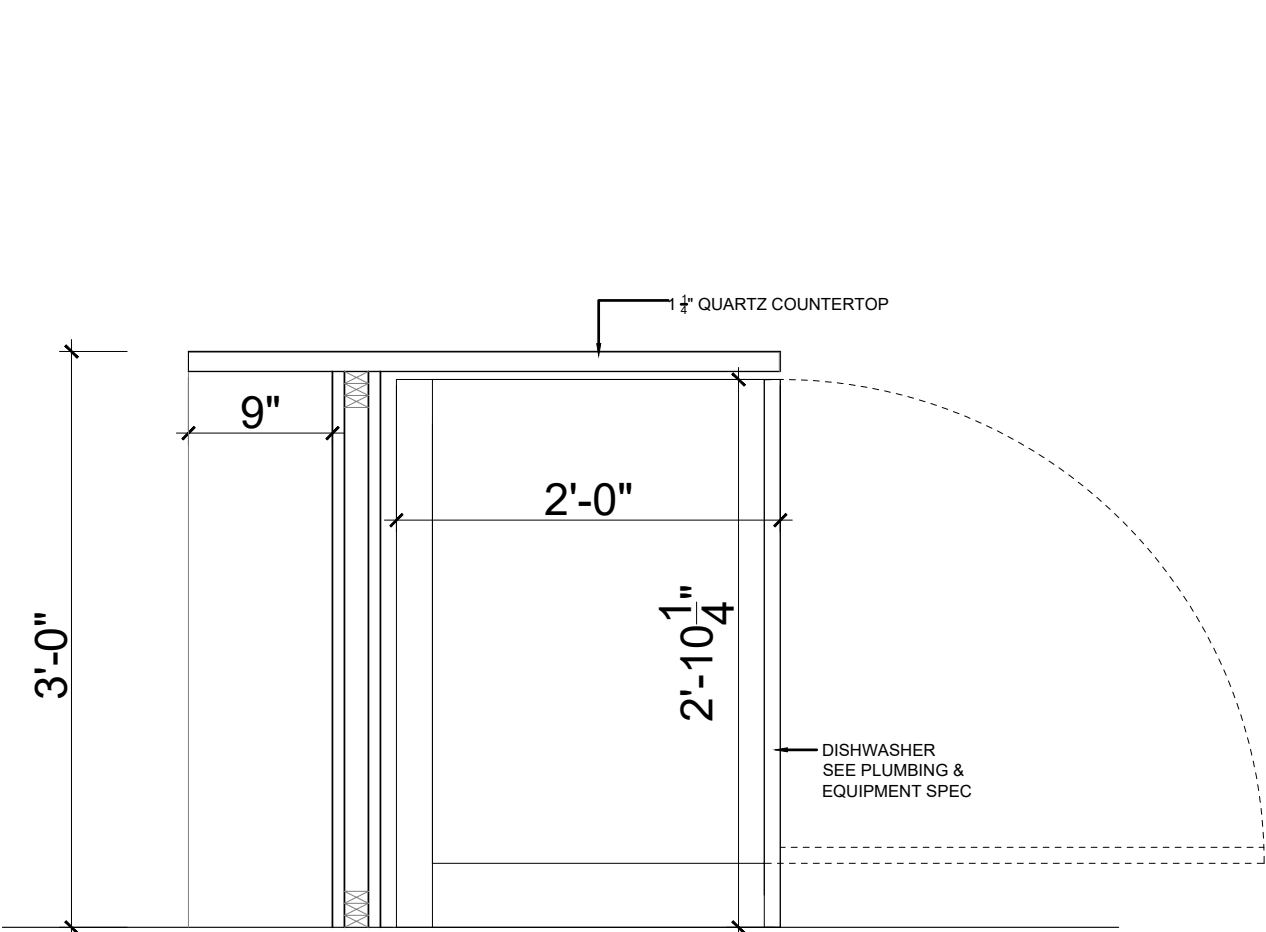


04 MILLWORK SECTION DETAIL 4 - DISHWASHER

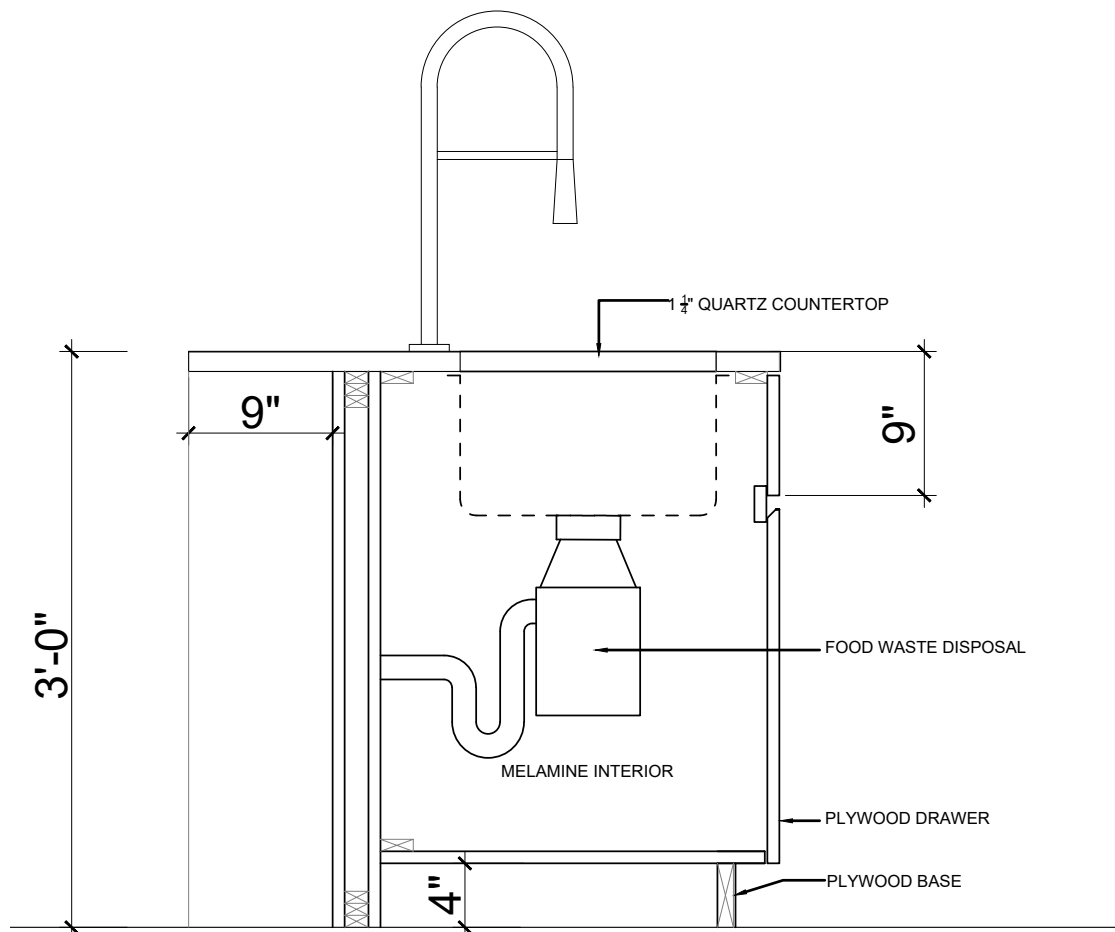


05 MILLWORK SECTION DETAIL 5 - SINK

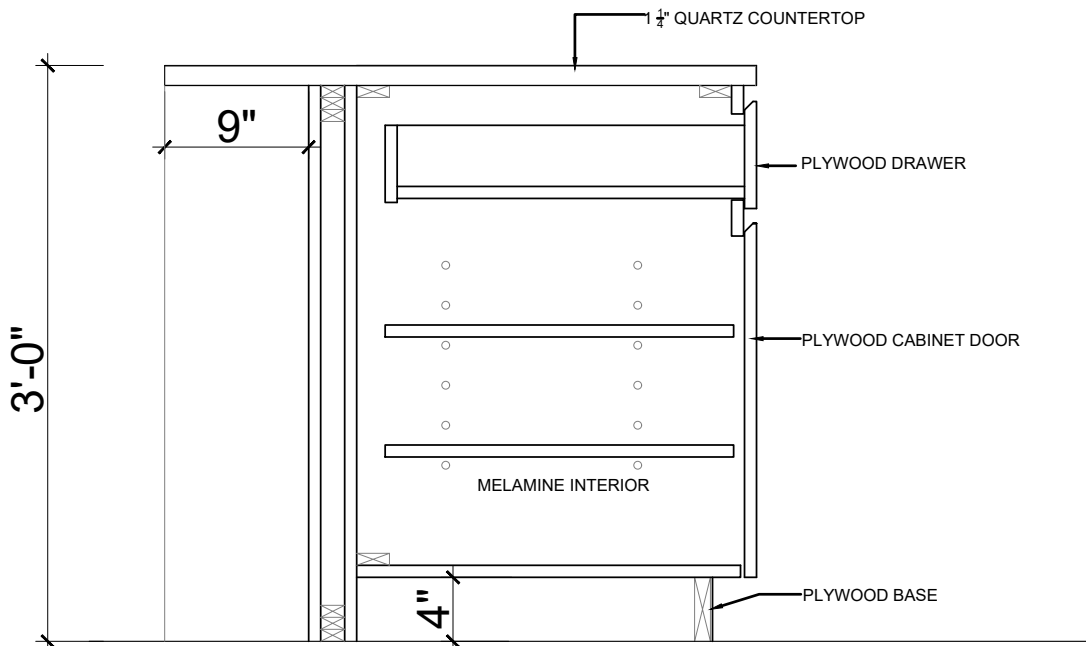


06 MILLWORK SECTION DETAIL 6 - DRAWER AND CABINET

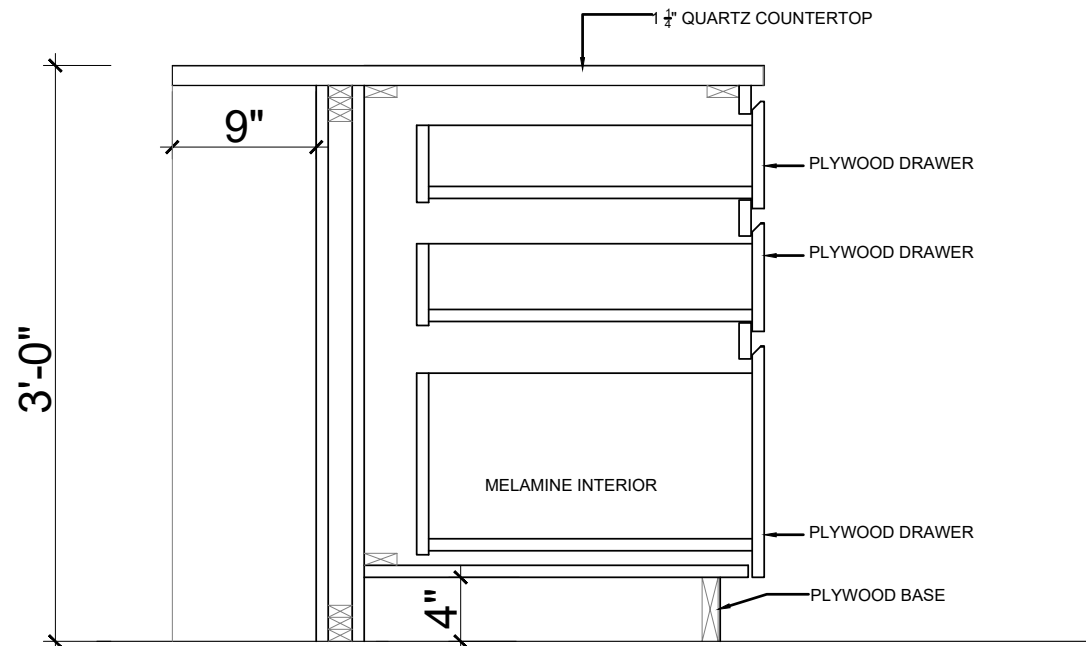


07 MILLWORK SECTION DETAIL 7 - DRAWER

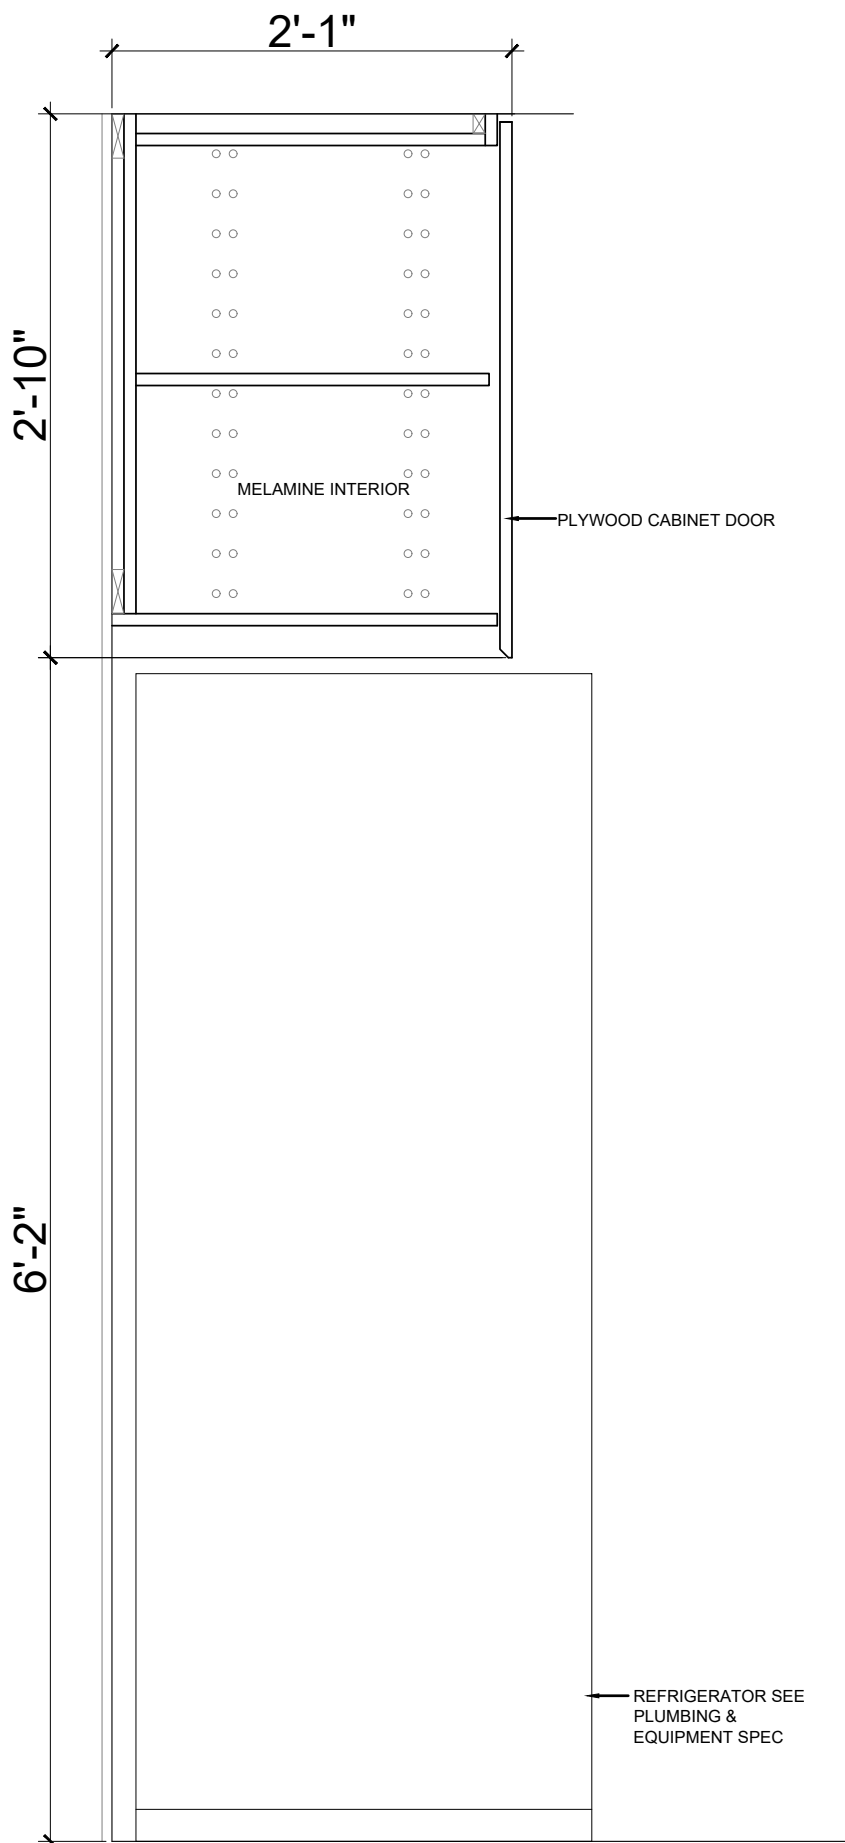

01 MILLWORK SECTION DETAIL 1 - REFRIGERATOR

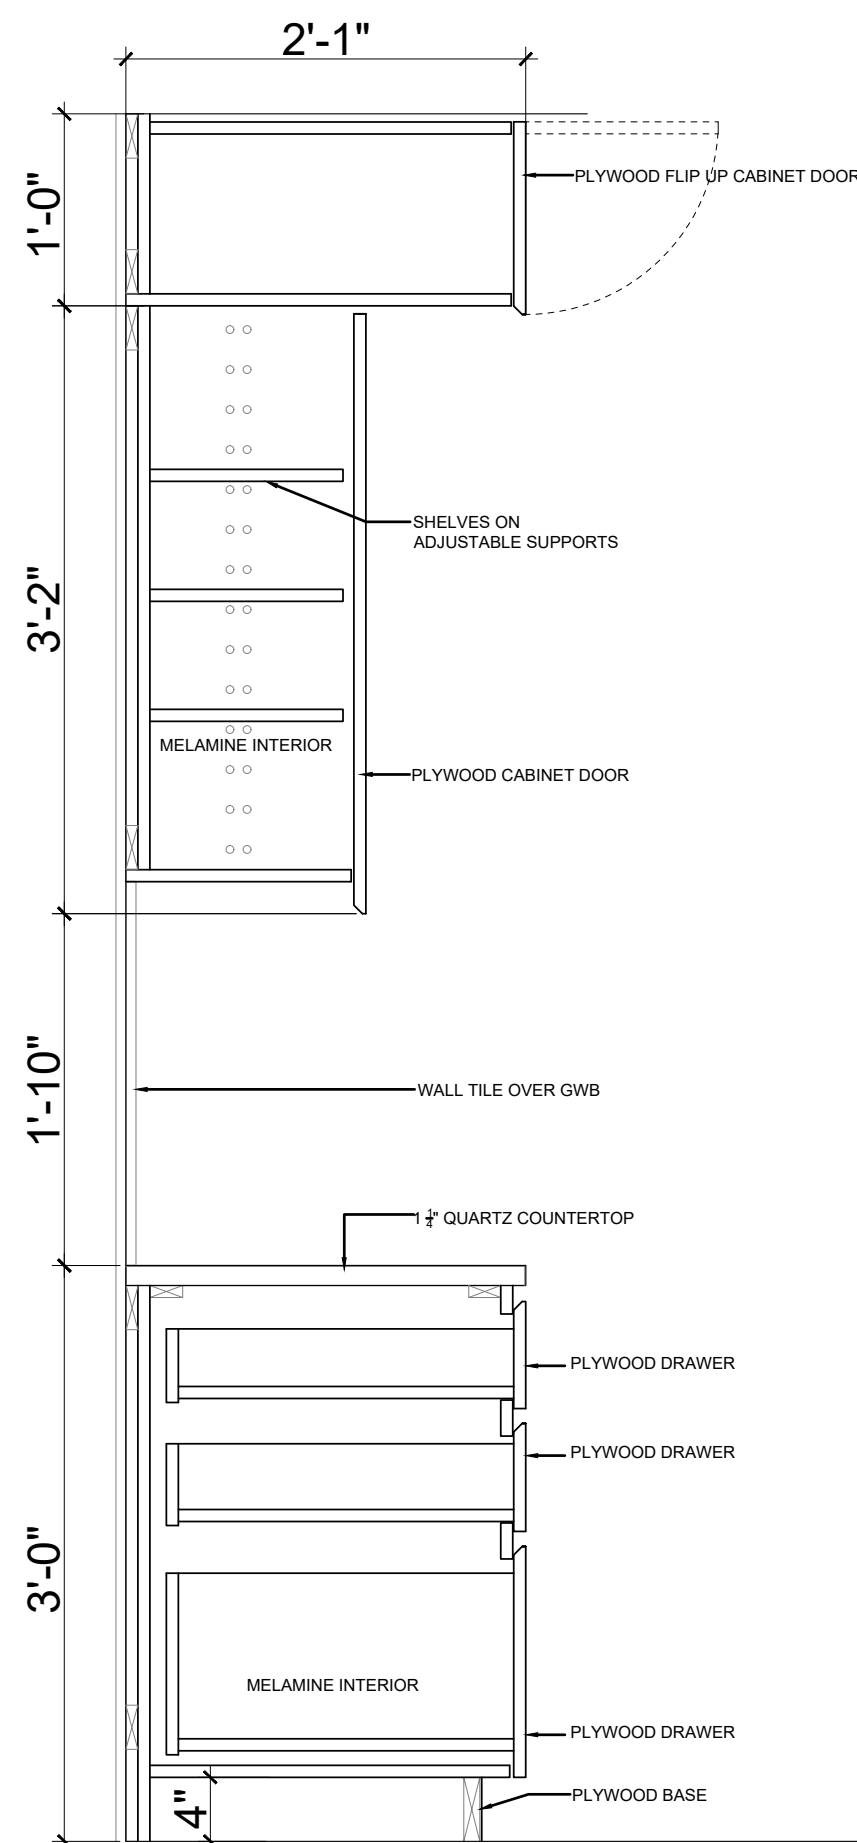

02 MILLWORK SECTION DETAIL 2 - CABINET AND DRAWER

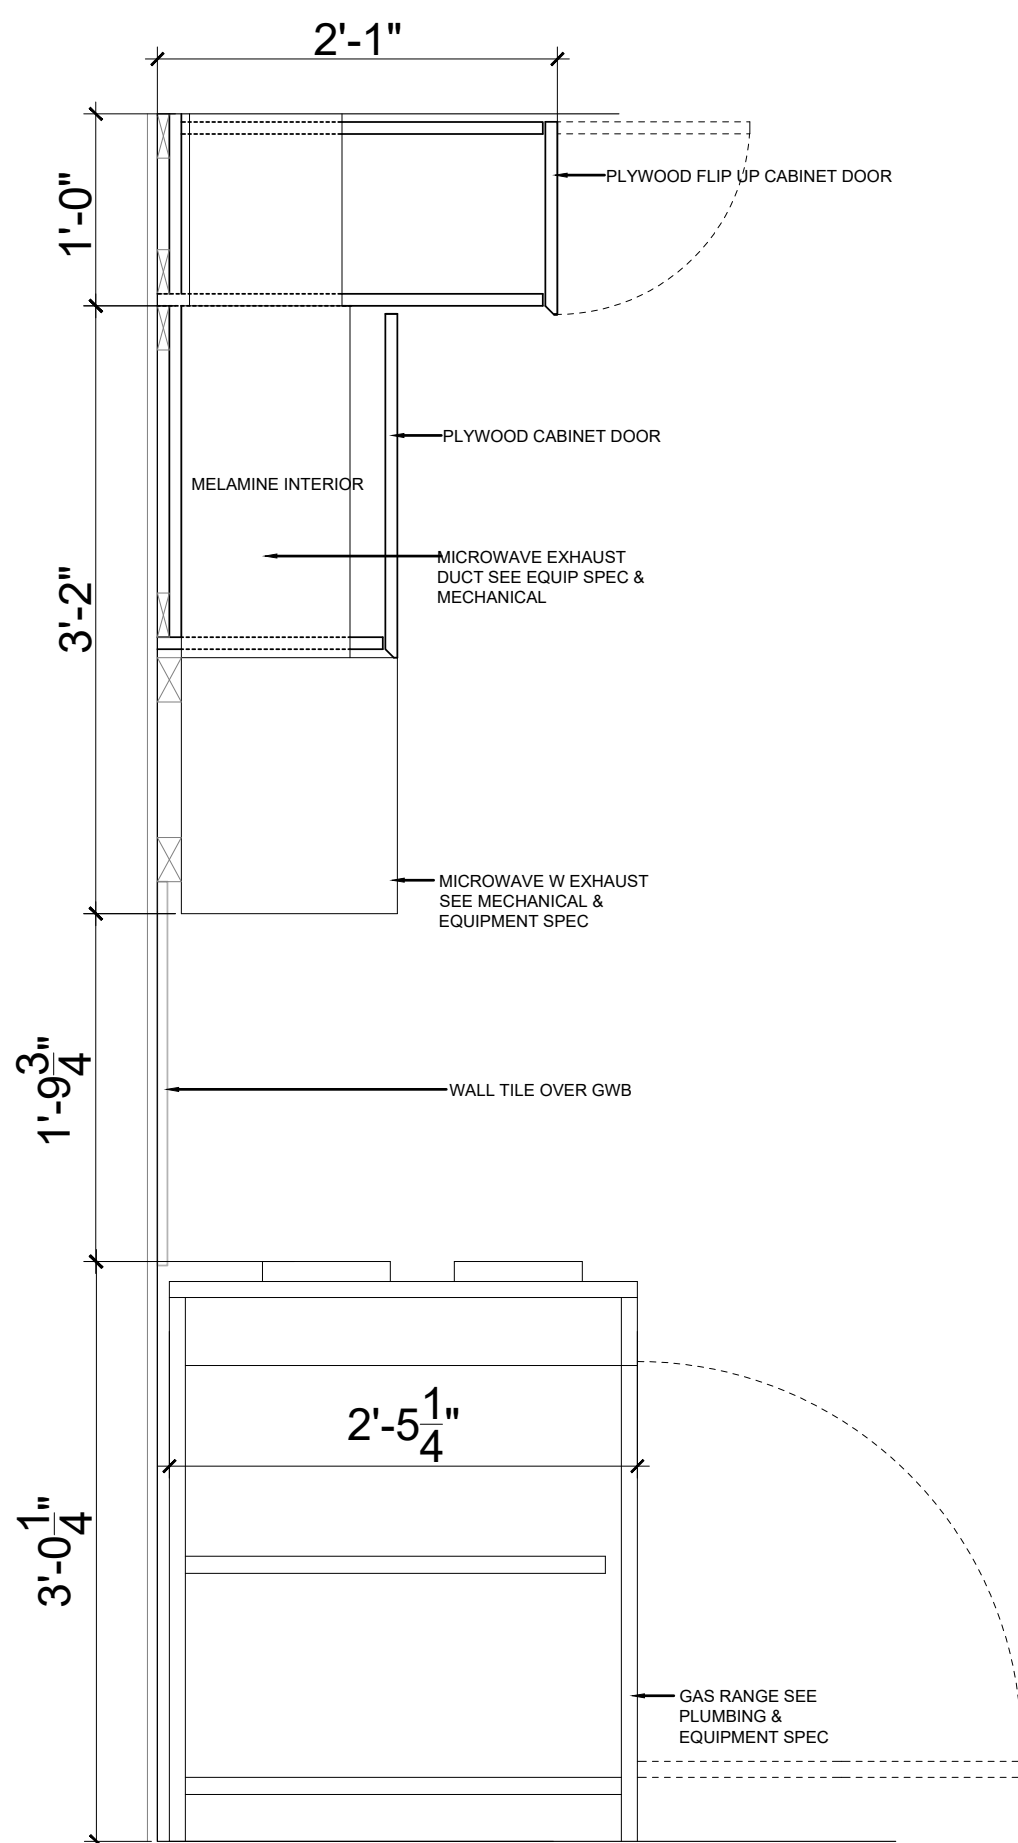

03 MILLWORK SECTION DETAIL 3 - GAS RANGE & MICROWAVE

PROJECT 103

213 MAPLE STREET

213 MAPLE STREET, WEHAWKEN, NEW JERSEY, 07086

CONSULTANTS:

STRUCTURAL ENGINEER
FLEX ENGINEERING GROUP LLC
3133 CENTRAL AVE #202, UNION CITY, NJ 07087
T: 201-974-9570
E: flexengineer@yahoo.com

MECHANICAL ENGINEER
FLEX ENGINEERING GROUP LLC
3133 CENTRAL AVE #202, UNION CITY, NJ 07087
T: 201-974-9570
E: flexengineer@yahoo.com

GENERAL CONTRACTOR
HOBOKEN KITCHEN & BATH
2 14TH ST PH 32, HOBOKEN NJ, 07030
T: 201-472-0425
E: theodore@hobokenkitchenandbath.com

DATE DESCRIPTION

DOB STAMP AND SIGNATURE

SEAL AND SIGNATURE

CONTRACTORS SHALL ONLY UTILIZE WRITTEN DIMENSIONS. CONTRACTORS SHALL VERIFY AND BE RESPONSIBLE FOR ALL DIMENSIONS AND CONDITIONS ON THE JOB, AND OWNER MUST BE NOTIFIED OF ANY VARIATIONS FROM DIMENSIONS AND CONDITIONS SHOWN BY THESE DRAWINGS. SCALED SHOP DRAWINGS MUST BE SUBMITTED TO OWNER FOR APPROVAL, BEFORE PROCEEDING WITH ANY FABRICATION.

ALL DRAWINGS, SPECIFICATIONS, ETC. SUBMITTED TO CONTRACTORS, BIDDERS, GOVERNMENTAL AGENCIES, ETC. ARE NOT FOR GENERAL USE OR PUBLICATION BY OTHERS. ALL RIGHTS RESERVED. NONE OF THE IDEAS, DESIGN, ARRANGEMENTS OR PLANS IN THESE DRAWINGS SHALL BE USED BY OR DISCLOSED TO ANY PERSONS, FIRM OR CORPORATION FOR ANY PURPOSE WITHOUT THE CURRENT AND WRITTEN PERMISSION OF OWNER.

DRAWING TITLE:

I-111

MILLWORK SECTION DETAIL - SECOND FLOOR

FOR CONSTRUCTION




01 1ST FLOOR ENTRY, STAIR TO 2ND FLOOR
N.T.S.



02 1ST FLOOR KITCHEN & LIVING ROOM
N.T.S.




03 1ST FLOOR, STAIR TO BASEMENT
N.T.S.

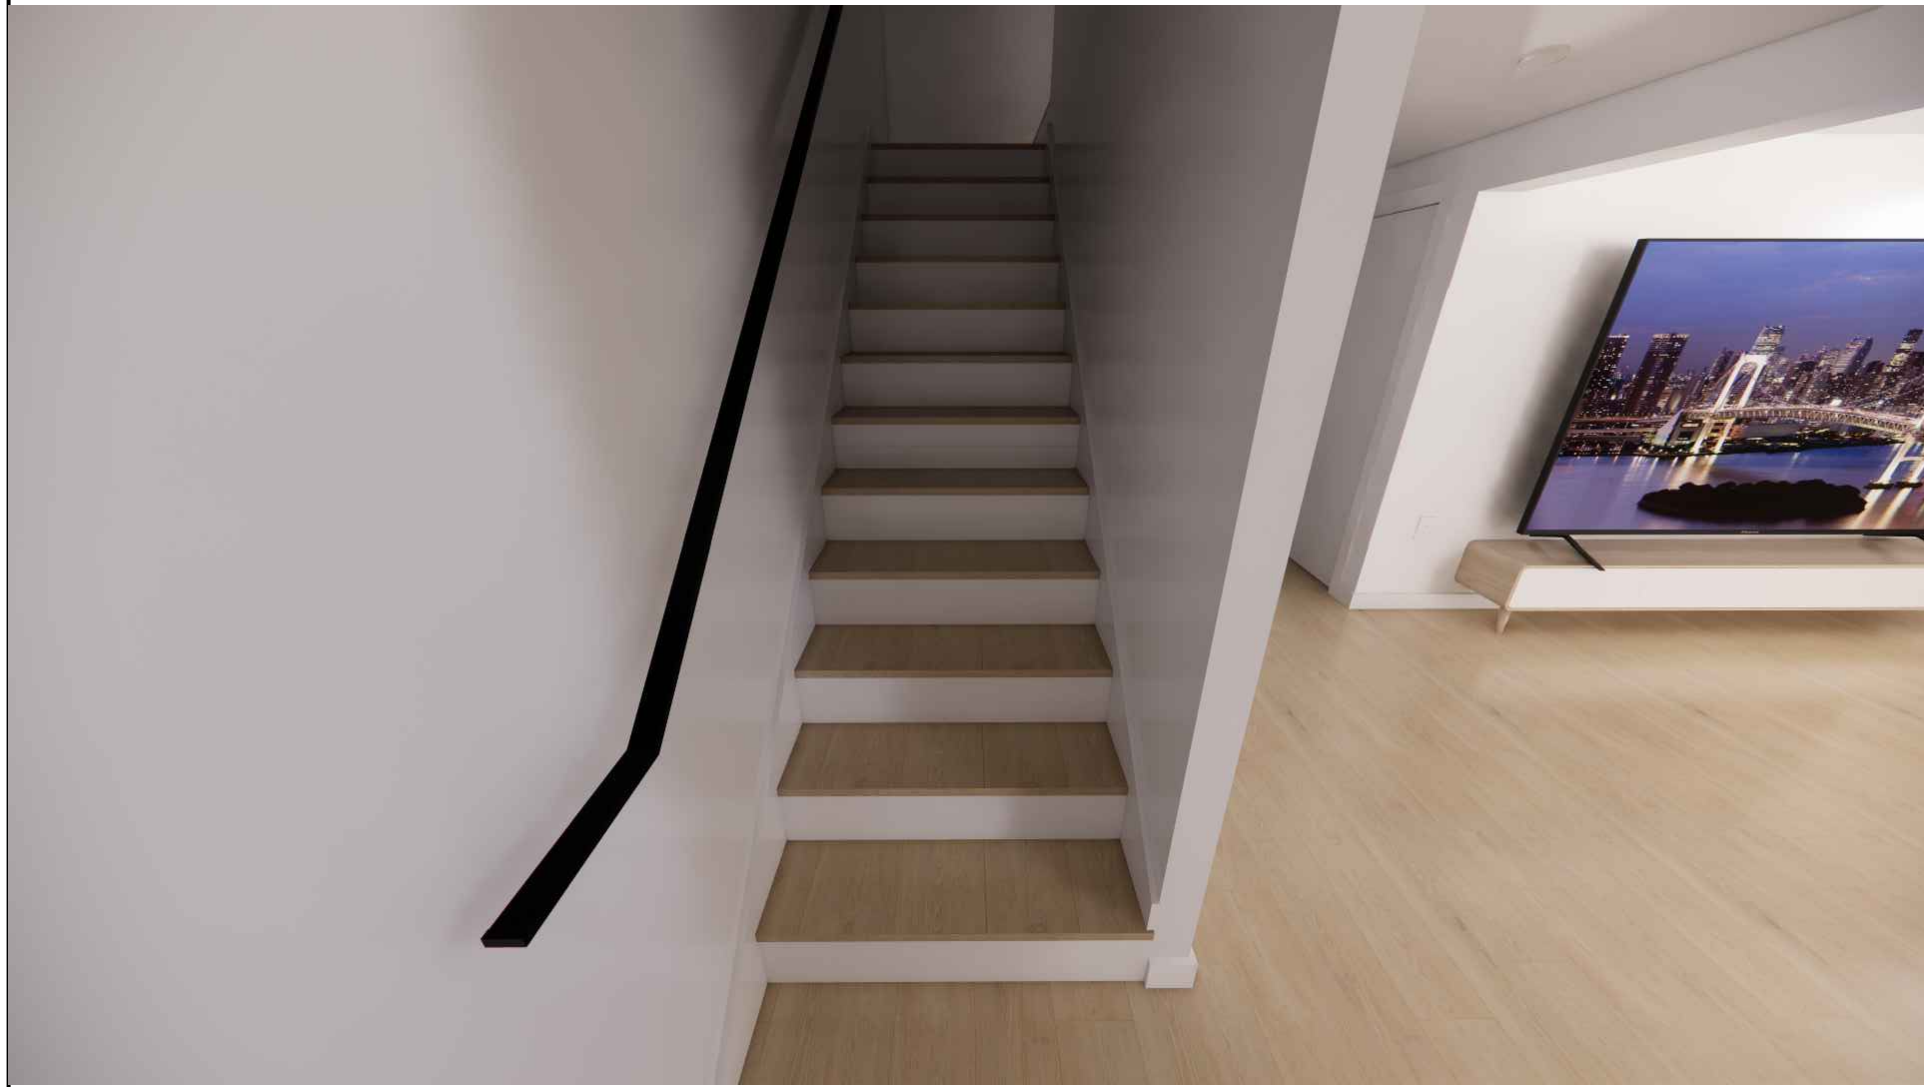

04 BASEMENT STAIR AND REC ROOM
N.T.S.



05 BASEMENT REC ROOM
N.T.S.

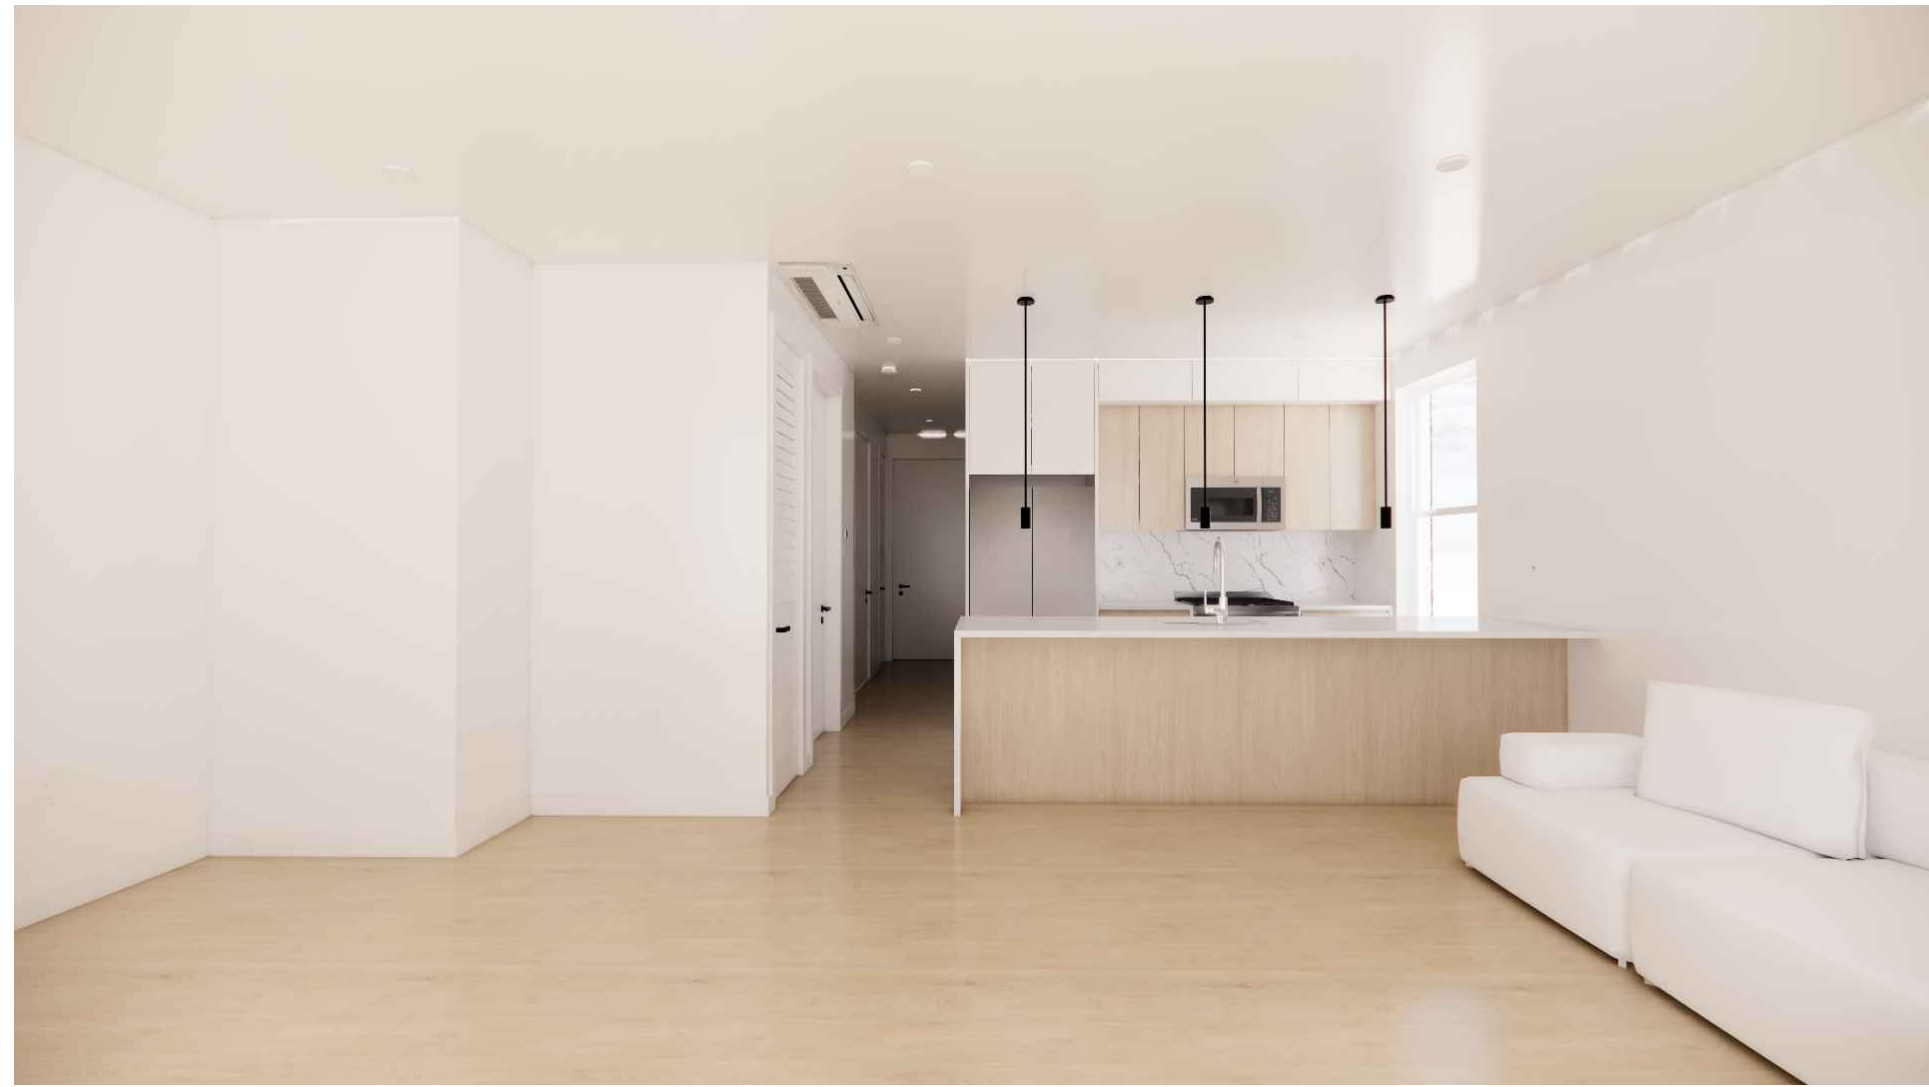

06 2ND FLOOR KITCHEN AND LIVING ROOM
N.T.S.



07 2ND FLOOR, STAIR TO 1ST FLOOR
N.T.S.



08 2ND FLOOR, SKYLIGHT AND NEW HATCH
N.T.S.



09 2ND FLOOR KITCHEN
N.T.S.

PROJECT:03

213 MAPLE STREET

213 MAPLE STREET, WEHAWKEN, NEW JERSEY, 07086

CONSULTANTS:

STRUCTURAL ENGINEER

FLEX ENGINEERING GROUP LLC

3133 CENTRAL AVE #202, UNION CITY, NJ 07087

T: 201-974-9570

E: flexengr@flexengr.com

MECHANICAL ENGINEER

FLEX ENGINEERING GROUP LLC

3133 CENTRAL AVE #202, UNION CITY, NJ 07087

T: 201-974-9570

E: flexengr@flexengr.com

GENERAL CONTRACTOR





HOBOKEN KITCHEN & BATH

2 14TH ST PH 32, HOBOKEN NJ, 07030

T: 201-472-0425

E: theodore@hobokenkitchenandbath.com

#	DATE	DESCRIPTION
DOB STAMP AND SIGNATURE		
SEAL AND SIGNATURE		
CONTRACTOR SHALL ONLY UTILIZE WRITTEN DIMENSIONS. CONTRACTOR SHALL VERIFY AND BE RESPONSIBLE FOR ALL DIMENSIONS AND CONDITIONS ON THE JOB. AND OWNER MUST BE NOTIFIED OF ANY VARIATIONS FROM DIMENSIONS AND CONDITIONS SHOWN BY THESE DRAWINGS. SCALED SHOP DRAWINGS MUST BE SUBMITTED TO OWNER FOR APPROVAL, BEFORE PROCEEDING WITH ANY FABRICATION. ALL DRAWINGS, SPECIFICATIONS, ETC. CONTRIBUTED TO CONTRACTOR, BIDDERS, GOVERNMENTAL AUTHORITIES ETC. ARE NOT FOR GENERAL USE OR PUBLICATION BY OTHERS. ALL RIGHTS RESERVED. NONE OF THE DESIGN, ARRANGEMENTS OR PLANS IN THESE DRAWINGS SHALL BE USED BY OR FOR ANY PERSONS, FIRM OR CORPORATION FOR ANY PURPOSE WITHOUT THE CURRENT AND WRITTEN PERMISSION OF OWNER.		
DRAWING TITLE:		
I-300		
RENDERINGS		
FOR CONSTRUCTION		

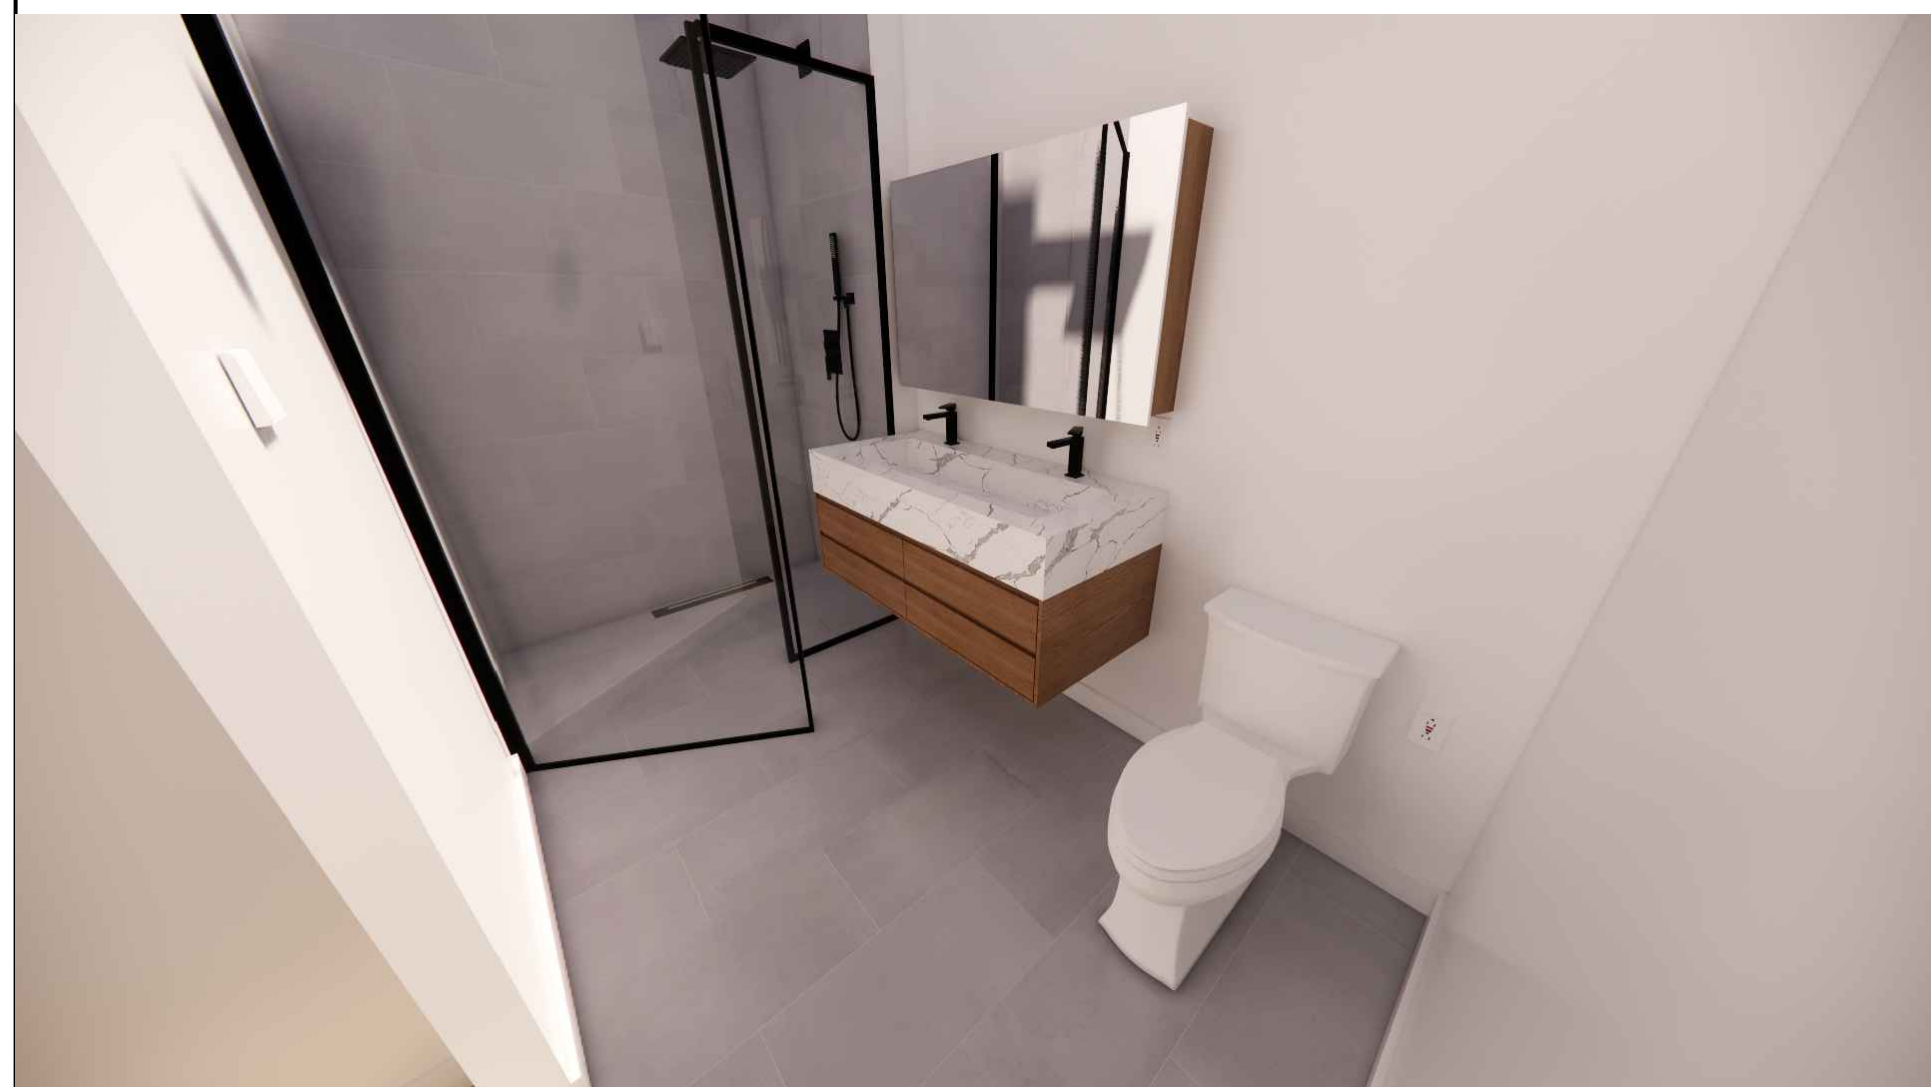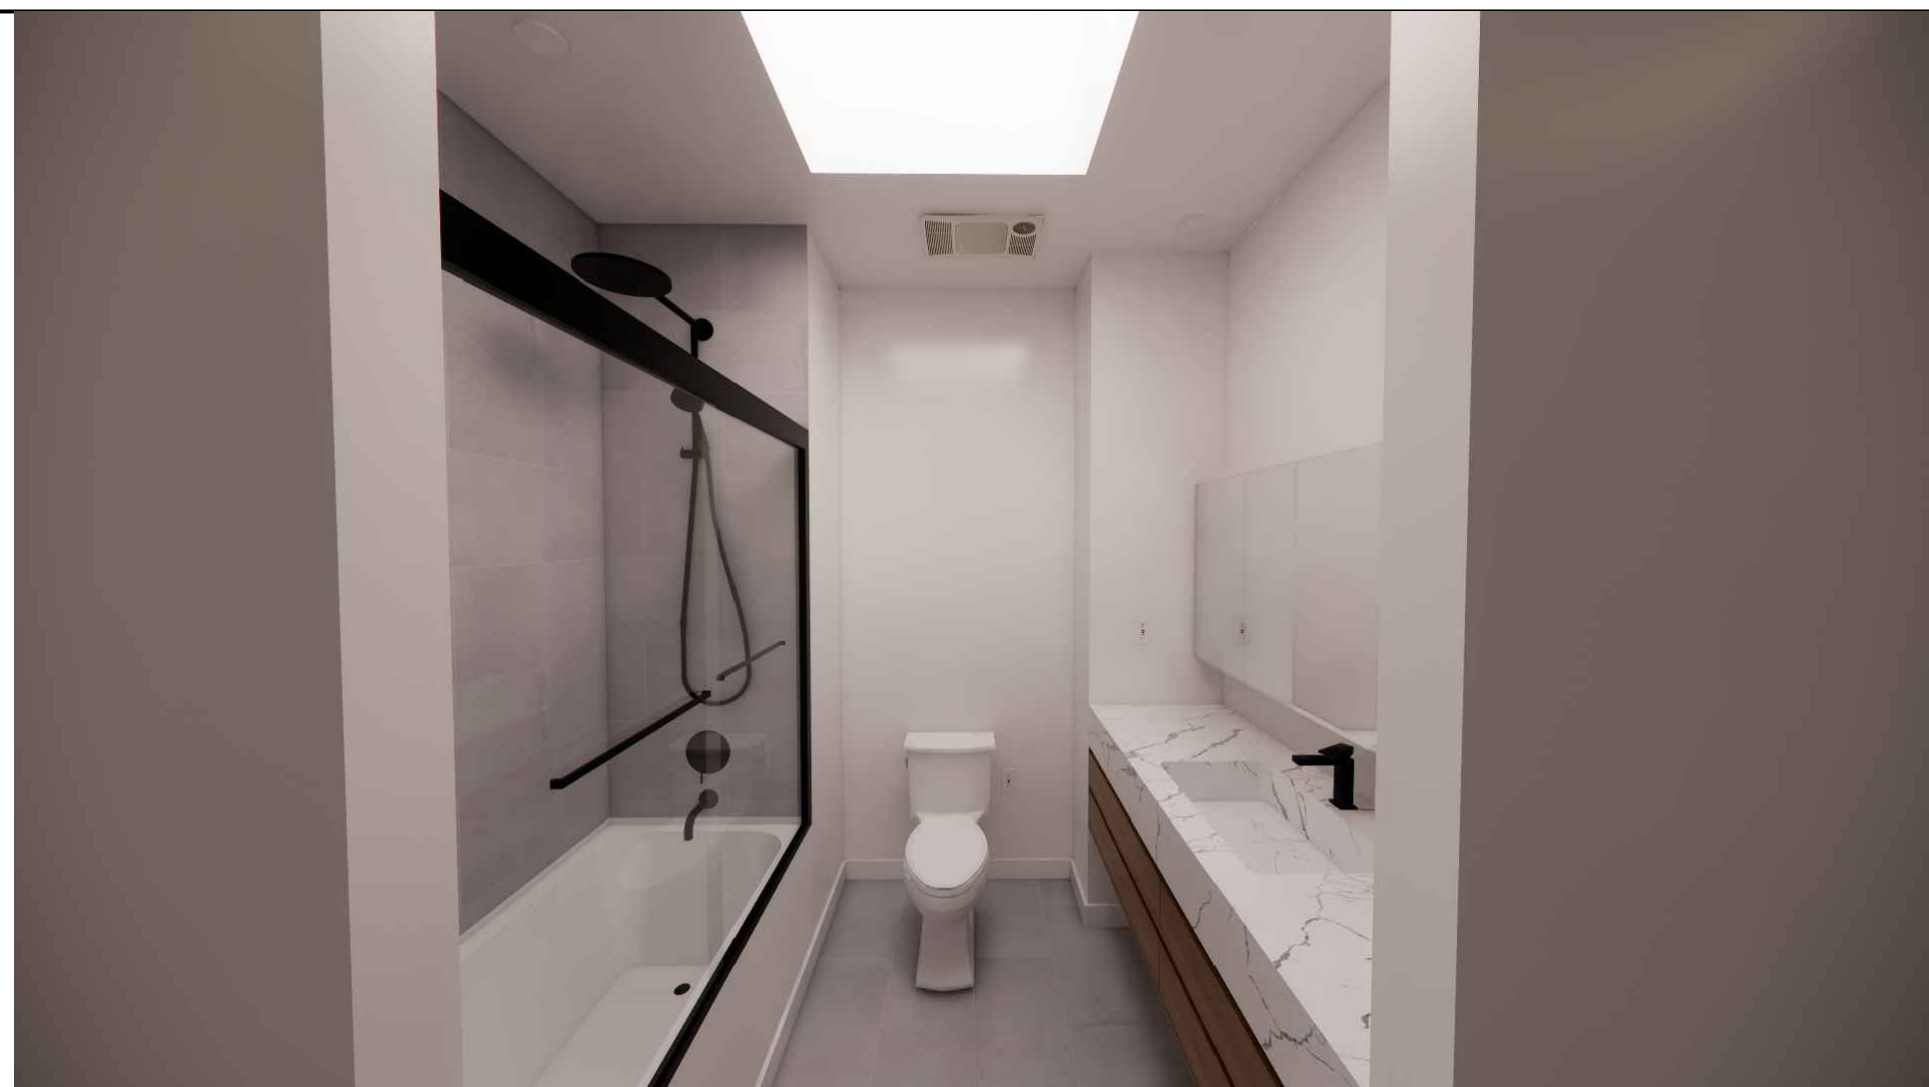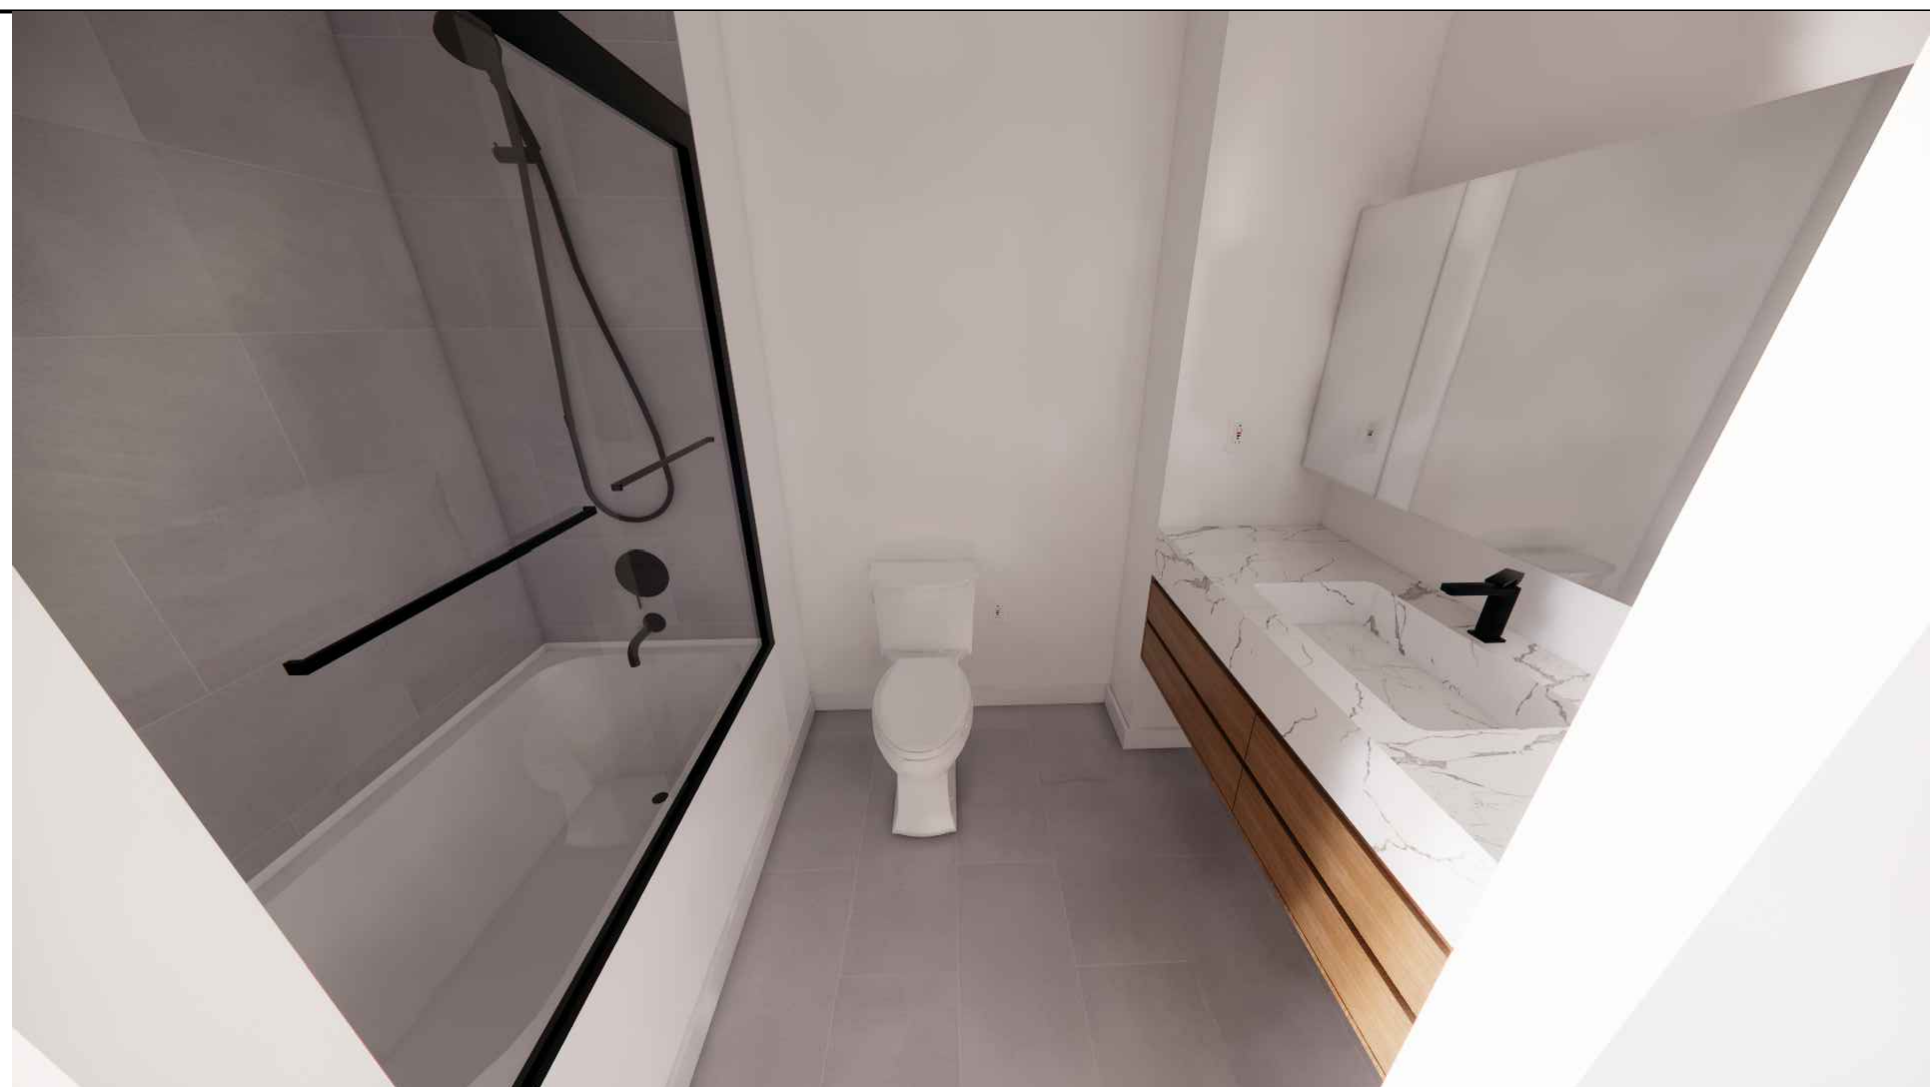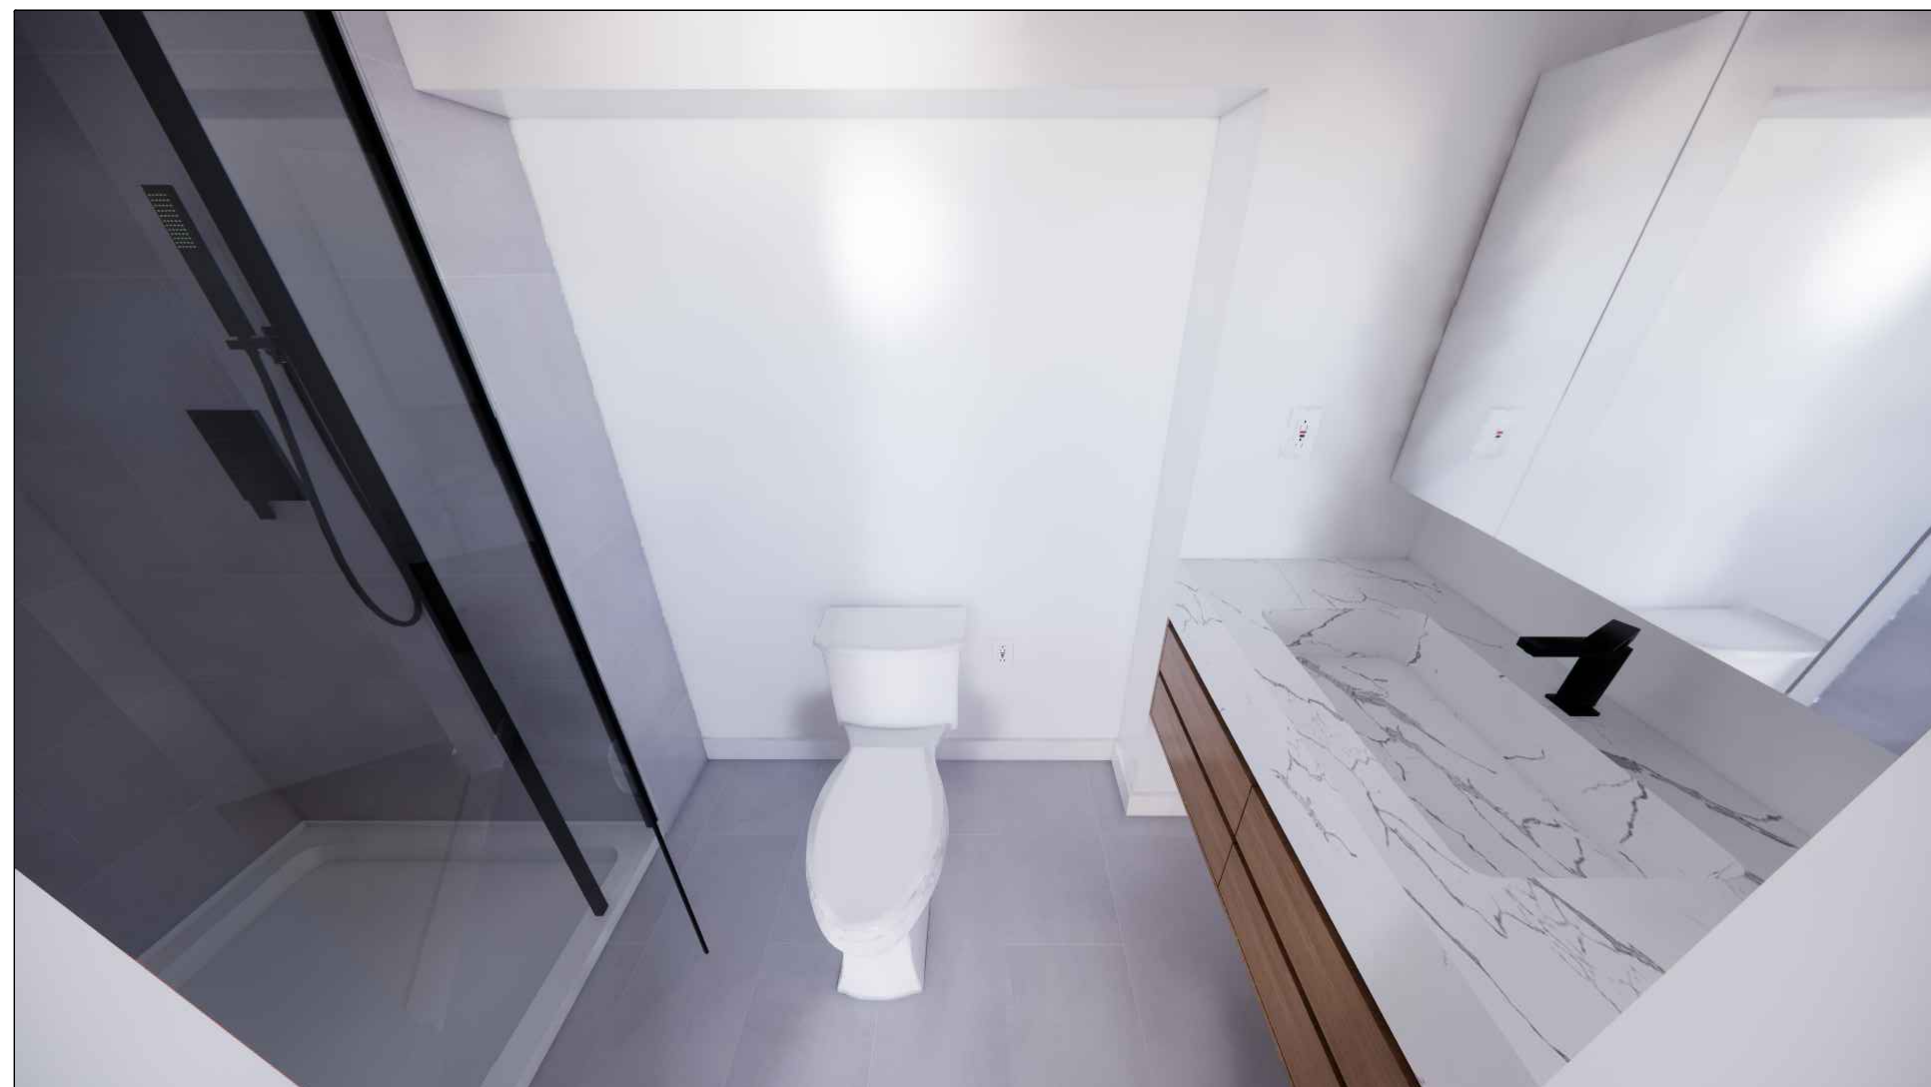

PROJECT-03

213 MAPLE STREET

213 MAPLE STREET, WEEHAWKEN, NEW JERSEY, 0706

CONSULTANTS:

STRUCTURAL ENGINEER
FLEX ENGINEERING GROUP LLC
3133 CENTRAL AVE #202, UNION CITY, NJ 0708
T: 201-974-9570
E: flexengineer@yahoo.com

MECHANICAL ENGINEER
FLEX ENGINEERING GROUP LLC
3133 CENTRAL AVE #202, UNION CITY, NJ 0708
T: 201-974-9570
E: flexengineer@yahoo.com

GENERAL CONTRACTOR
HOBOKEN KITCHEN & BATH
2 14TH ST PH 32, HOBOKEN NJ, 07030
T: 201-472-0425
E: theodore@hobokenkitchenandbath.com

#	DATE	DESCRIPTION
---	------	-------------

DOB STAMP AND SIGNATURE

SEAL AND SIGNATURE

CONTRACTORS SHALL ONLY UTILIZE WRITTEN DIMENSIONS. CONTRACTORS SHALL VERIFY AND BE RESPONSIBLE FOR ALL DIMENSIONS AND CONDITIONS ON THE JOB, AND OWNER MUST BE NOTIFIED OF ANY VARIATIONS FROM DIMENSIONS AND CONDITIONS SHOWN BY THESE DRAWINGS. SCALED SHOP DRAWINGS MUST BE SUBMITTED TO OWNER FOR APPROVAL BEFORE PROCEEDING WITH ANY FABRICATION.

ALL DRAWINGS, SKETCHES, SPECIFICATIONS ETC. DISTRIBUTED TO CONTRACTORS, BIDDERS, GOVERNMENTAL AUTHORITIES ETC. ARE NOT FOR GENERAL USE OR PUBLICATION BY OTHERS. ALL RIGHTS RESERVED. NONE OF THE IDEAS, DESIGNS, ARRANGEMENTS OR PLANS IN THIS DRAWINGS SHALL BE USED BY OR DISCLOSED TO ANY PERSONS, FIRM OR CORPORATION FOR ANY PURPOSE WITHOUT THE CONSENT AND WRITTEN PERMISSION OF OWNER.

DRAWING TITLE:

I-301

RENDERINGS

FOR CONSTRUCTION