



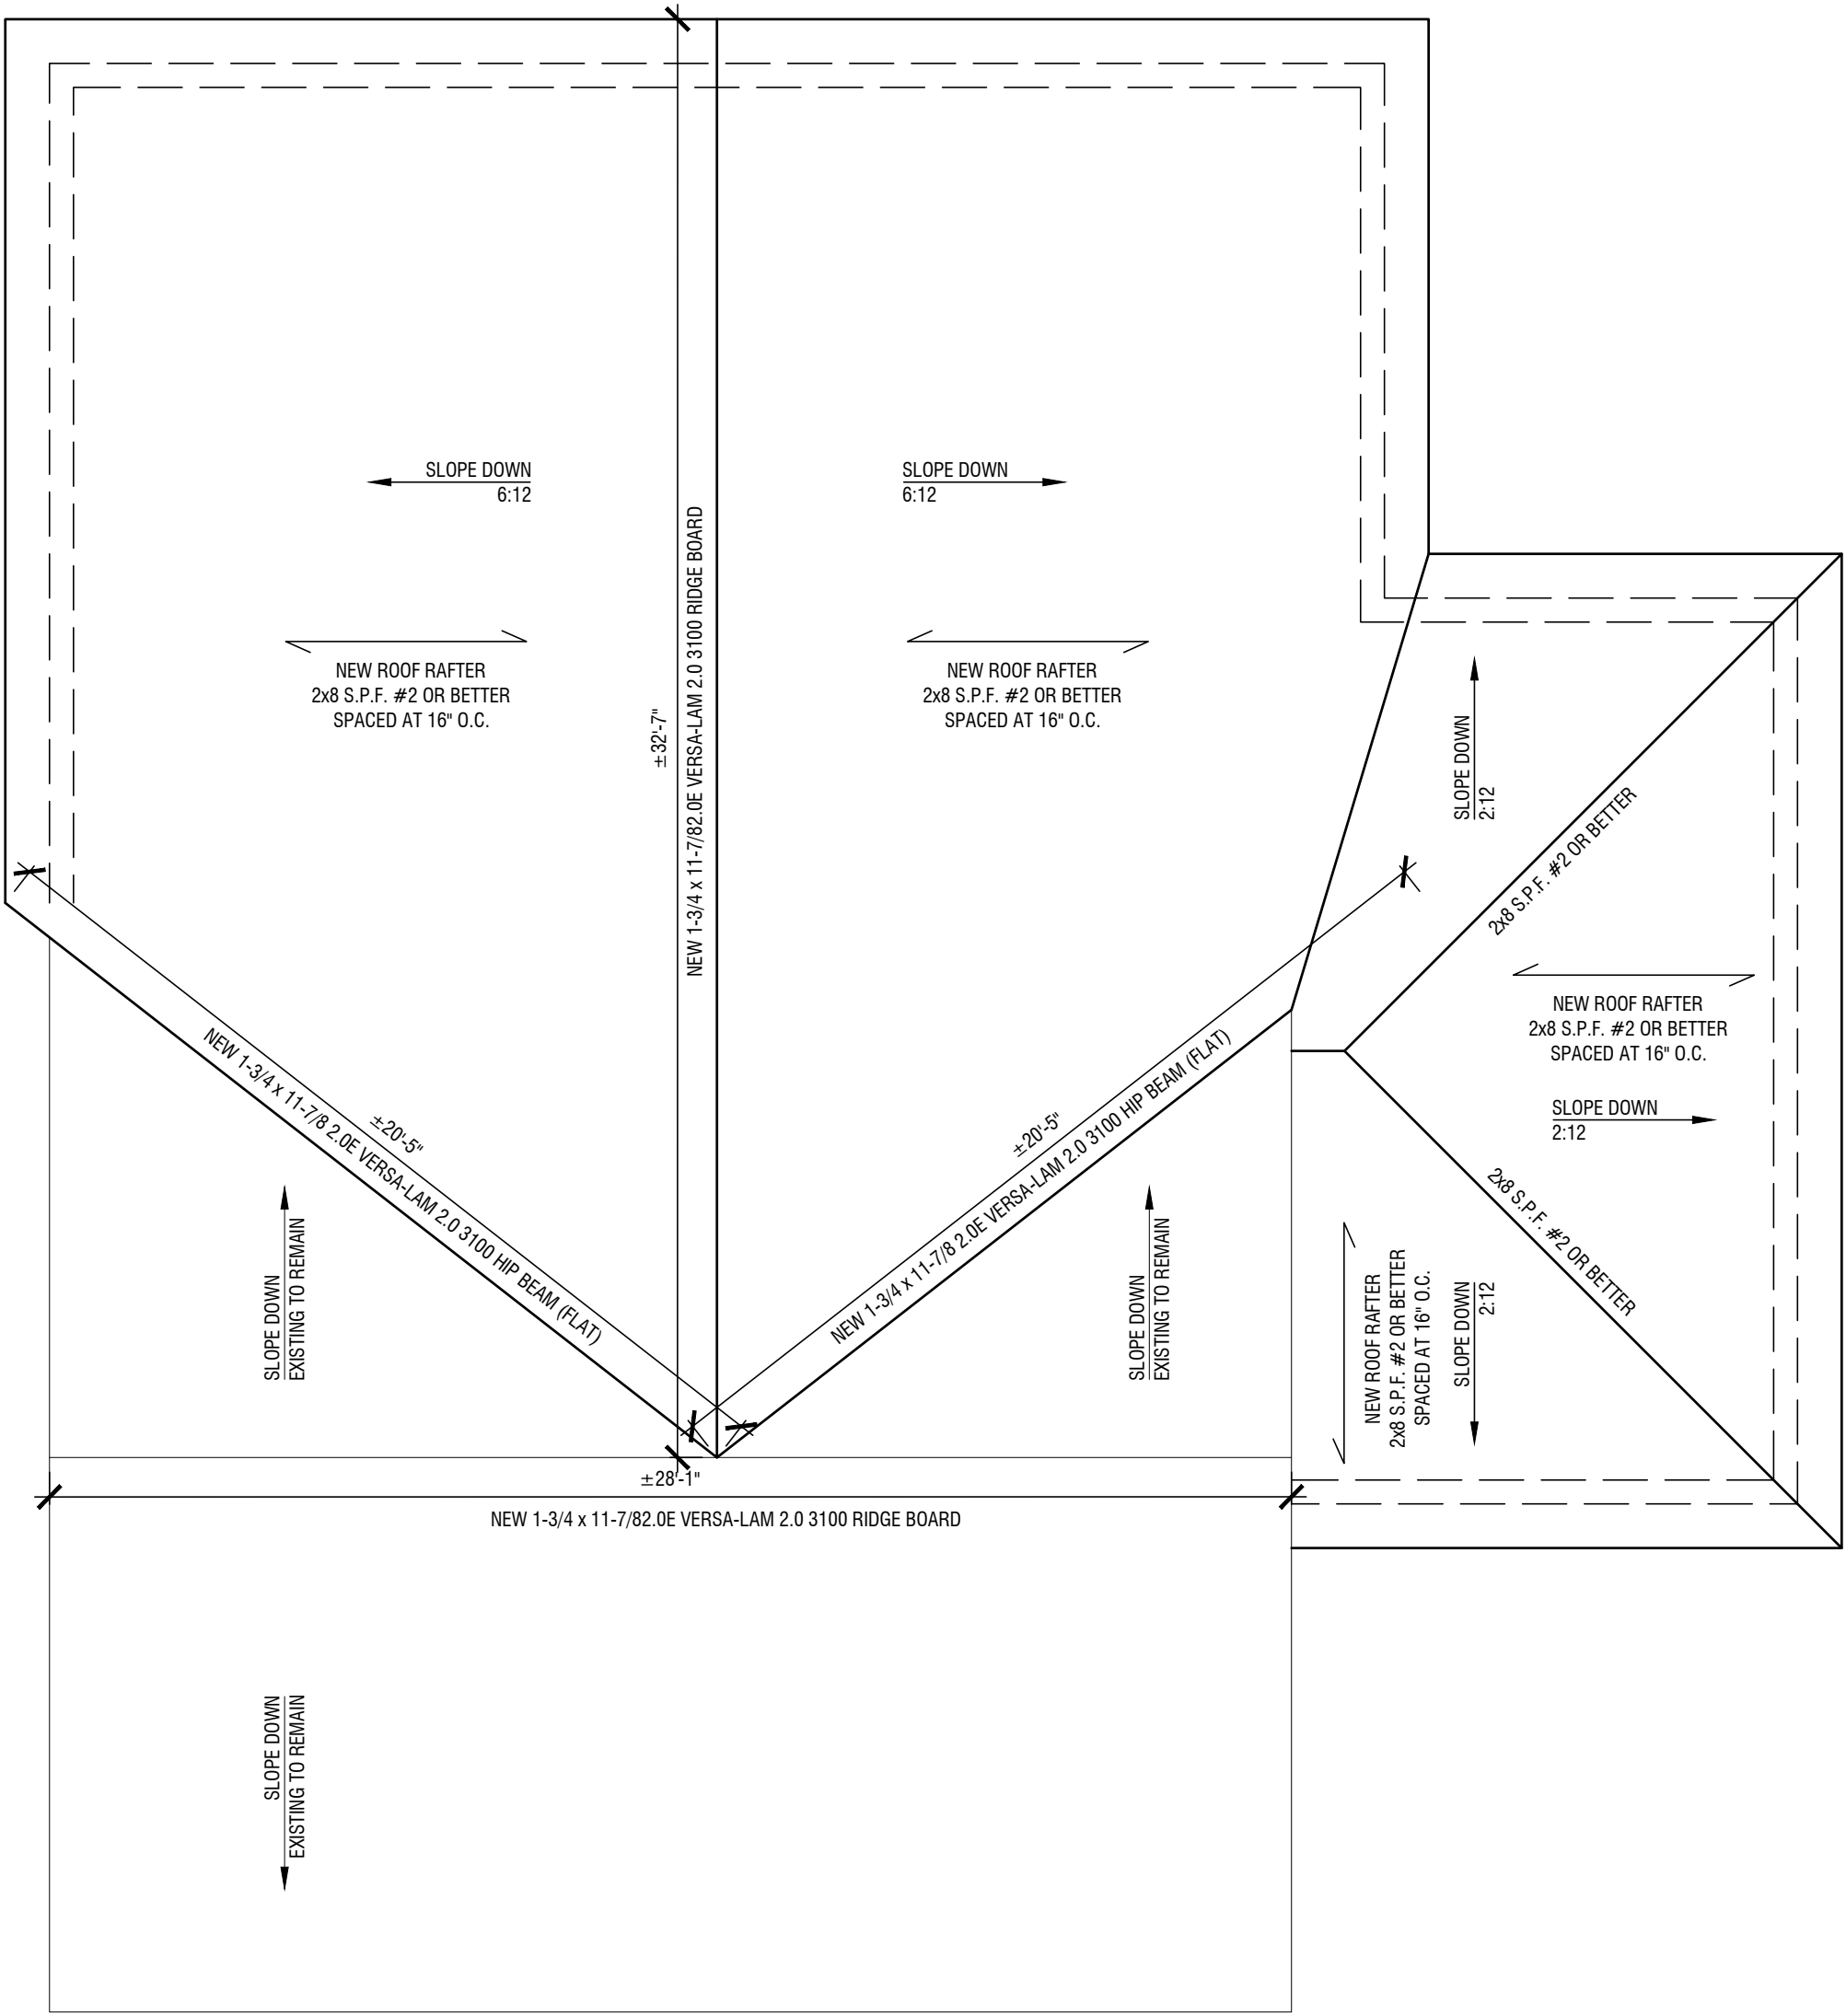

3 PROPOSED PLAN - ROOF
SCALE: 1/4"=1'-0"

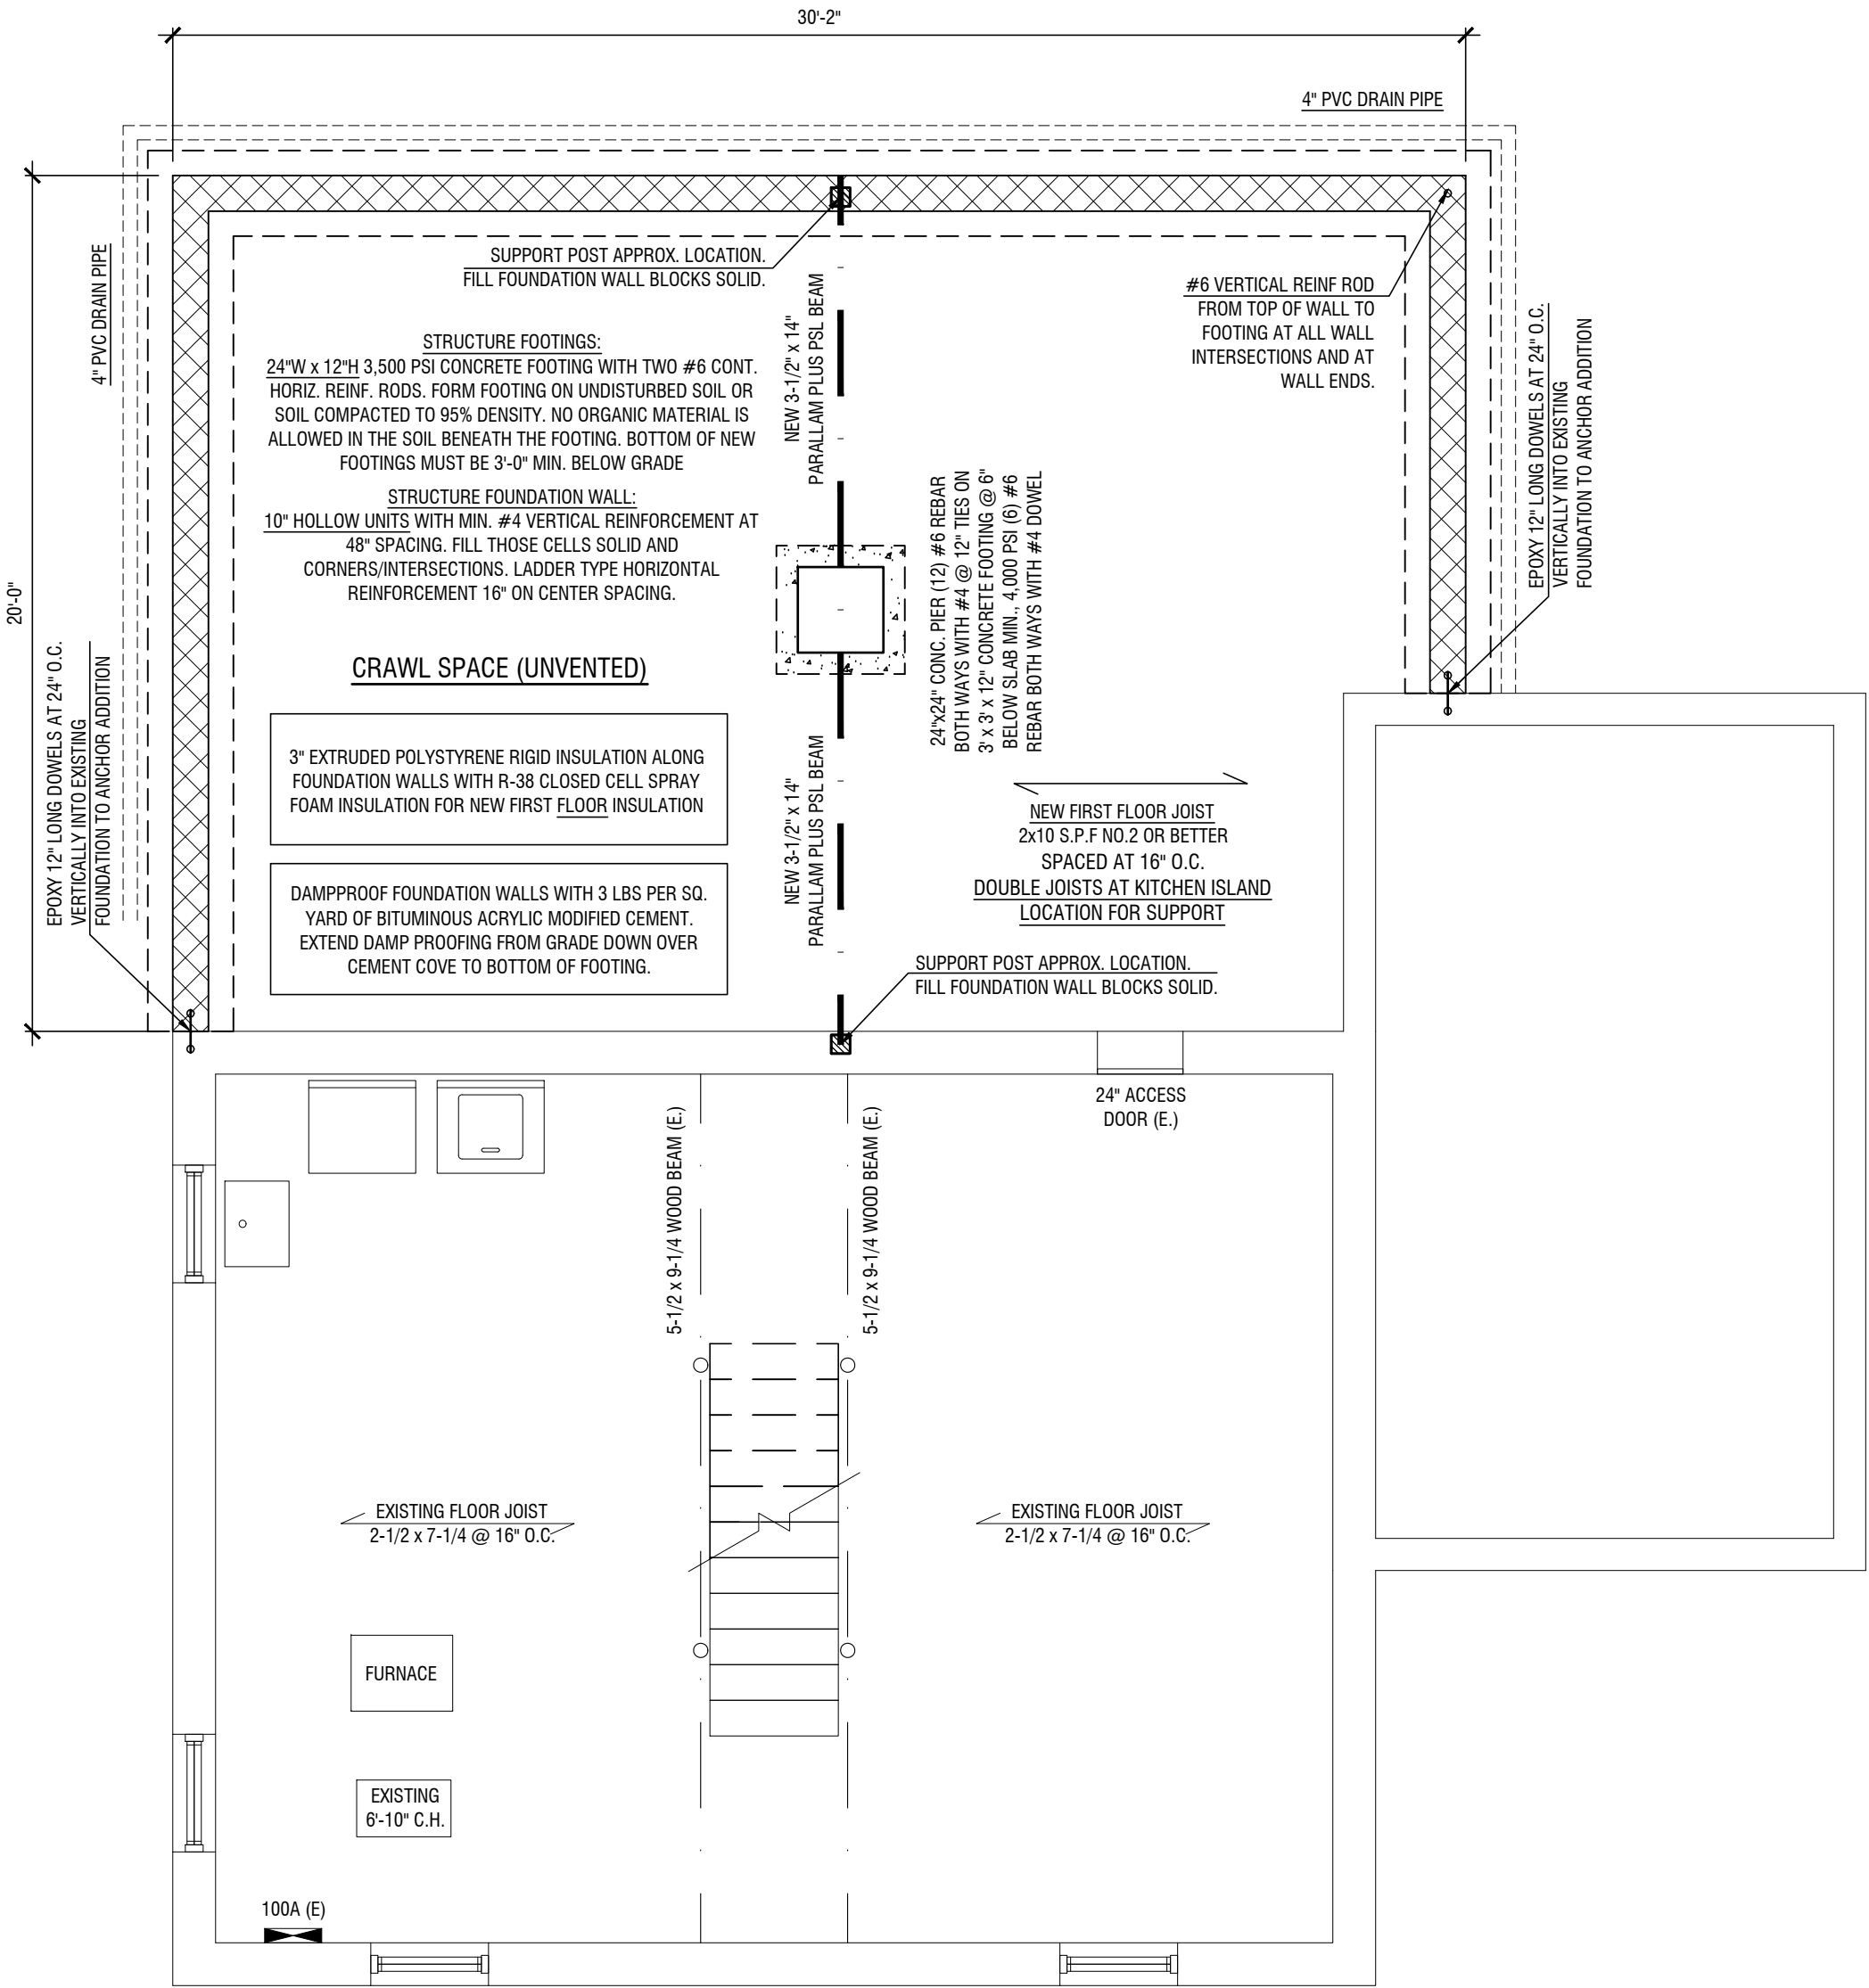

0 PROPOSED PLAN - BASEMENT
SCALE: 1/4"=1'-0"

CONSTRUCTION LEGEND

- NEW DOOR AS PER OWNER.
- NEW WINDOW AS PER OWNER.
- NEW SMOKE DETECTOR, HARDWIRED 120-V
- NEW CARBON MONOXIDE DETECTOR
- DUPLEX ELECTRICAL RECEPTACLE
- DUPLEX ELECTRICAL RECEPTACLE WITH GROUND FAULT PROTECTION
- ELECTRICAL PANEL
- TELEPHONE, DATA, AND/OR HDMI WALL RECEPTACLE. CONTRACTOR TO COORDINATE RECEPTACLE TYPE AND LOCATION WITH OWNER.
- QUAD ELECTRICAL RECEPTACLE
- LIGHT SWITCH
- LIGHT SWITCH 3 OR 4 WAY (AS NOTED)
- RECESSED LIGHT FIXTURE
- WALL MOUNTED LIGHT FIXTURE
- HANGING PENDANT LIGHT FIXTURE
- ELECTRICAL DEVICE UL LISTED FOR EXPOSURE TO WEATHER
- LIGHT FIXTURE / EXHAUST FAN / COMBINATION CEILING MOUNTED. VENT TO EXTERIOR OF BUILDING.
- 8\"/>

RESCHECK- THIS PROJECT UTILIZES THE PRESCRIPTIVE PACKAGES APPROACH. THE ENERGY SUBCODE (TABLE 402.1.2 OF 2021 IECC) ALLOWS FOR THE USE OF A PRESCRIPTIVE PACKAGE BASED ON CLIMATE ZONE LOCATION (ZONE #5A) & WINDOW-TO-WALL RATIOS. THIS APPLIES FOR TO TYPICAL WOOD-FRAMED CONSTRUCTION. SEE G-100 FOR MORE INFORMATION.

CONSTRUCTION NOTES

- ALL FINISHES TO BE SELECTED BY OWNER.
- ALL NEW LIGHT FIXTURES TO BE SELECTED BY OWNER.
- FINAL LIGHTING LAYOUT SHALL BE APPROVED BY OWNER PRIOR TO INSTALLATION.
- FINAL ELECTRICAL & TELEPHONE RECEPTACLES LAYOUT SHALL BE APPROVED BY OWNER PRIOR TO INSTALLATION.
- ALL WORK MUST COMPLY TO ALL LOCAL AND STATE CODES.
- ALL EXISTING FRAMING SIZES & EXISTING WINDOW ROUGH OPENINGS TO BE CONFIRMED PRIOR TO CONSTRUCTION.

THIS DRAWING IS APPROVED ONLY FOR THE SCOPE OF WORK INDICATED ON THE DRAWINGS. ALL OTHER MATTERS SHOWN ARE NOT TO BE RELIED UPON OR CONSIDERED AS EITHER BEING APPROVED BY THIS ARCHITECT AND HIS CONSULTANTS OR IN ACCORDANCE WITH APPLICABLE CODES AND STANDARDS

REVISIONS:

REV. #	DESCRIPTION:	DATE:
	SUBMITTED FOR FILING	10.31.25

ADDITION/ALTERATION OF
BARNES RESIDENCE
44 BROOKVIEW TERRACE
BOROUGH OF BERGENFIELD
BERGEN COUNTY
BLOCK #291 LOT #101

DWG. TITLE:

CONSTRUCTION PLAN AND NOTES -
BASEMENT AND ROOF

ARCHITECTURAL LICENSE NUMBERS:

NJ 21A102225000
FL 101849
NY 1533422
PA RA-402635

BID SET ONLY.
NOT FOR CONSTRUCTION!

GRZEGORZ HASAJ, AIA - ARCHITECT

c. 973-508-2461
ghasaj.hdc@gmail.com

THIS DRAWING AND THE INFORMATION CONTAINED HEREIN ARE FOR THE EXCLUSIVE USE OF THE PARTY FOR WHOM THE WORK WAS CONTRACTED OR CERTIFIED. REPRODUCTION, DISTRIBUTION, OR RELIANCE BY OTHERS IS PROHIBITED WITHOUT THE PRIOR WRITTEN CONSENT OF HIGHLAND DESIGN & CONSULTING, LLC. ALL RIGHTS RESERVED.

DATE:
02.24.26
SCALE:
AS NOTED
DWN. BY:
GH

JOB NO.
026-001

CHK. BY:
GH

DWG. NO.

A-0

3 OF 8

SELECTIVE DEMOLITION

- THIS SECTION REQUIRES THE SELECTIVE REMOVAL AND THE SUBSEQUENT LEGAL OFFSITE DISPOSAL OF PORTIONS OF THE EXISTING BUILDING INDICATED ON DRAWINGS AND AS REQUIRED TO ACCOMMODATE NEW CONSTRUCTION.
- RELOCATE PIPES, DUCTS CONDUITS AND OTHER MECHANICAL AND ELECTRICAL ITEMS AS REQUIRED AND AS INDICATED ON ARCHITECTURAL AND ENGINEERING DRAWINGS TO COMPLETE THE WORK OF THIS CONTRACT.
- CONDITION OF STRUCTURE: OWNER ASSUMES NO RESPONSIBILITY FOR ACTUAL CONDITION OF ITEMS OR STRUCTURES TO BE DEMOLISHED.
- DAMAGES: PROMPTLY REPAIR DAMAGES CAUSED TO ADJACENT FACILITIES BY DEMOLITION WORK.
- FLAME CUTTING: THE USE OF CUTTING TORCHES OR OPEN FLAME TO REMOVE MATERIALS FROM THE BUILDING IS NOT PERMITTED.
- MAINTAIN FIRE PROTECTION SERVICES DURING SELECTIVE DEMOLITION OPERATIONS.
- CEASE OPERATIONS AND NOTIFY OWNER'S REPRESENTATIVE IMMEDIATELY IF SAFETY OF STRUCTURE APPEARS TO BE ENDANGERED. TAKE PRECAUTIONS TO SUPPORT STRUCTURE UNTIL DETERMINATION IS MADE FOR CONTINUING OPERATIONS.
- COVER AND PROTECT FURNITURE, EQUIPMENT AND FIXTURES FROM SOILAGE OR DAMAGE WHEN DEMOLITION WORK IS PERFORMED IN AREAS WHERE SUCH ITEMS HAVE NOT BEEN REMOVED.
- IF UNANTICIPATED MECHANICAL, ELECTRICAL OR STRUCTURAL ELEMENTS THAT CONFLICT WITH INTENDED FUNCTION OR DESIGN ARE ENCOUNTERED, INVESTIGATE AND MEASURE BOTH NATURE AND EXTENT OF THE CONFLICT. SUBMIT REPORT TO OWNER'S REPRESENTATIVE IN WRITTEN, ACCURATE DETAIL. PENDING RECEIPT OF DIRECTIVE FROM OWNER'S REPRESENTATIVE, REARRANGE SELECTIVE DEMOLITION SCHEDULE AS NECESSARY TO CONTINUE OVERALL JOB PROGRESS WITHOUT UNDUE DELAY.
- UPON COMPLETION OF DEMOLITION WORK, REMOVE TOOLS, EQUIPMENT AND DEMOLISHED MATERIALS FROM SITE. REMOVE PROTECTIONS AND LEAVE INTERIOR AREAS BROOM CLEAN.
- REPAIR DEMOLITION PERFORMED IN EXCESS OF THAT REQUIRED. RETURN ELEMENTS OF CONSTRUCTION AND SURFACES TO REMAIN TO CONDITION EXISTING PRIOR TO START OF OPERATIONS. REPAIR ADJACENT SURFACES SOILED OR DAMAGED BY SELECTIVE DEMOLITION WORK.

DEMOLITION LEGEND

EXISTING PARTITION TO REMAIN. PATCH & REFINISH ALL SURFACES DISTURBED OR DAMAGED AS A RESULT OF THIS CONTRACT.

WALL, FINISH MATERIAL OR ITEM TO BE REMOVED.

CONSTRUCTION LEGEND


- NEW DOOR AS PER OWNER.
- NEW WINDOW AS PER OWNER.
- NEW SMOKE DETECTOR, HARDWIRED 120-V.
- NEW CARBON MONOXIDE DETECTOR.
- DUPLEX ELECTRICAL RECEPTACLE.
- DUPLEX ELECTRICAL RECEPTACLE WITH GROUND FAULT PROTECTION.
- ELECTRICAL PANEL.
- TELEPHONE, DATA, AND/OR HDMI WALL RECEPTACLE. CONTRACTOR TO COORDINATE RECEPTACLE TYPE AND LOCATION WITH OWNER.
- QUAD ELECTRICAL RECEPTACLE.
- LIGHT SWITCH.
- LIGHT SWITCH 3 OR 4 WAY (AS NOTED).
- RECESSED LIGHT FIXTURE.
- WALL MOUNTED LIGHT FIXTURE.
- HANGING PENDANT LIGHT FIXTURE.
- ELECTRICAL DEVICE UL LISTED FOR EXPOSURE TO WEATHER.
- LIGHT FIXTURE / EXHAUST FAN / COMBINATION CEILING MOUNTED, VENT TO EXTERIOR OF BUILDING.
- 8" LED STRIP FIXTURE.
- DOOR BELL (EXTERIOR) OR CHIME (INTERIOR).
- GARAGE DOOR MOTOR CEILING MOUNTED.
- PROPOSED THERMOSTAT LOCATION.

RESCHECK- THIS PROJECT UTILIZES THE PRESCRIPTIVE PACKAGES APPROACH. THE ENERGY SUBCODE (TABLE 402.1.2 OF 2021 IECC) ALLOWS FOR THE USE OF A PRESCRIPTIVE PACKAGE BASED ON CLIMATE ZONE LOCATION (ZONE #5A) & WINDOW-TO-WALL RATIOS. THIS APPLIES FOR TO TYPICAL WOOD-FRAMED CONSTRUCTION. SEE G-100 FOR MORE INFORMATION.


CONSTRUCTION NOTES

- ALL FINISHES TO BE SELECTED BY OWNER.
- ALL NEW LIGHT FIXTURES TO BE SELECTED BY OWNER.
- FINAL LIGHTING LAYOUT SHALL BE APPROVED BY OWNER PRIOR TO INSTALLATION.
- FINAL ELECTRICAL & TELEPHONE RECEPTACLES LAYOUT SHALL BE APPROVED BY OWNER PRIOR TO INSTALLATION.
- ALL WORK MUST COMPLY TO ALL LOCAL AND STATE CODES.
- ALL EXISTING FRAMING SIZES & EXISTING WINDOW ROUGH OPENINGS TO BE CONFIRMED PRIOR TO CONSTRUCTION.


THIS DRAWING IS APPROVED ONLY FOR THE SCOPE OF WORK INDICATED ON THE DRAWINGS. ALL OTHER MATTERS SHOWN ARE NOT TO BE RELIED UPON OR CONSIDERED AS EITHER BEING APPROVED BY THIS ARCHITECT AND HIS CONSULTANTS OR IN ACCORDANCE WITH APPLICABLE CODES AND STANDARDS

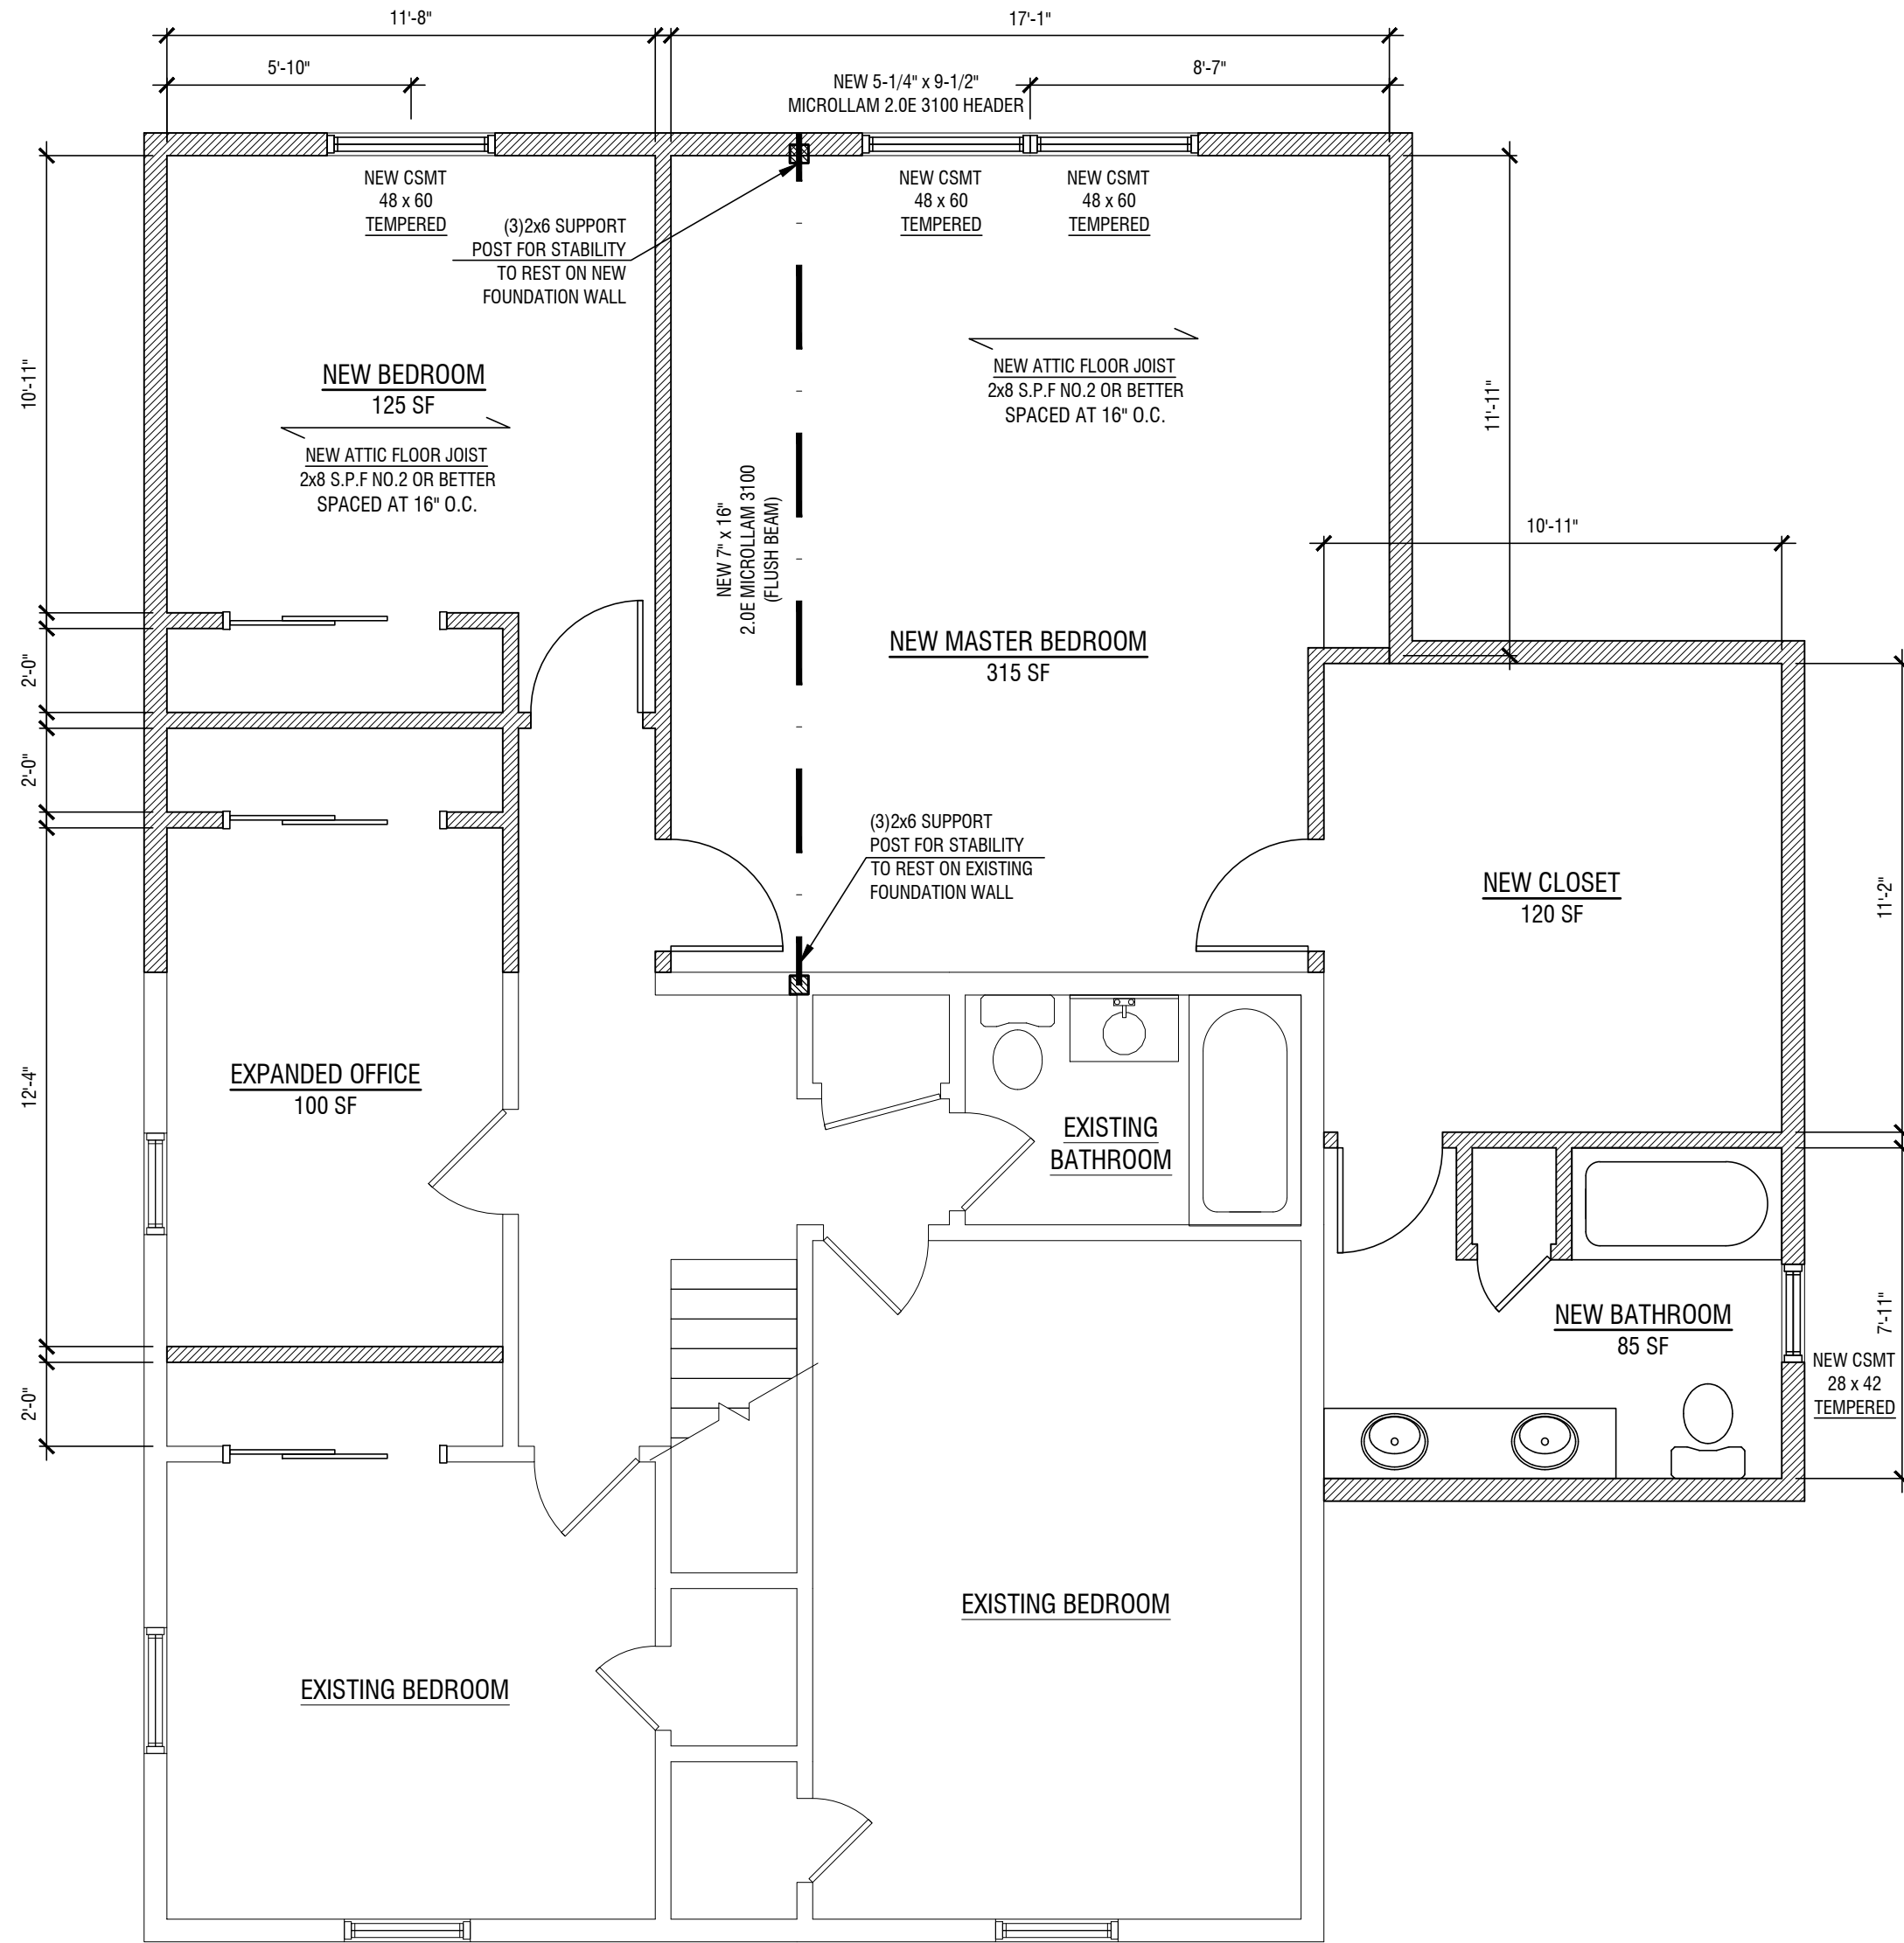

2 CONSTRUCTION PLAN - SECOND FLOOR
SCALE: 1/4"=1'-0"

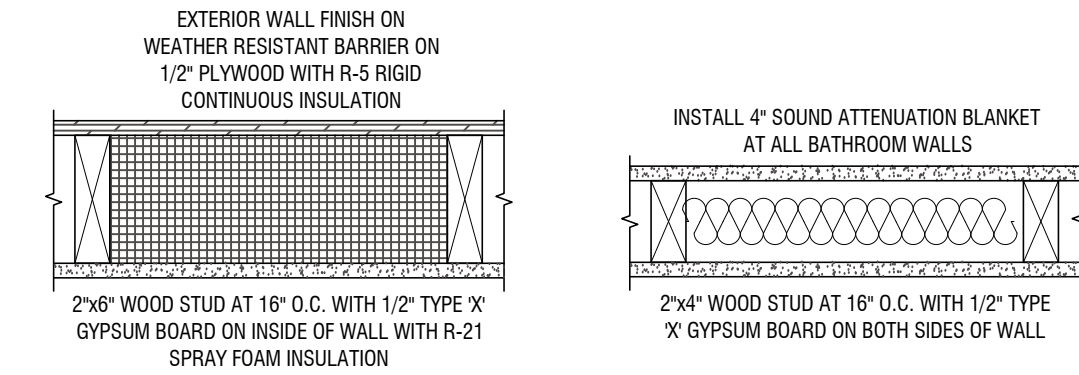


1 EXTERIOR WALL TYPE TYPICAL

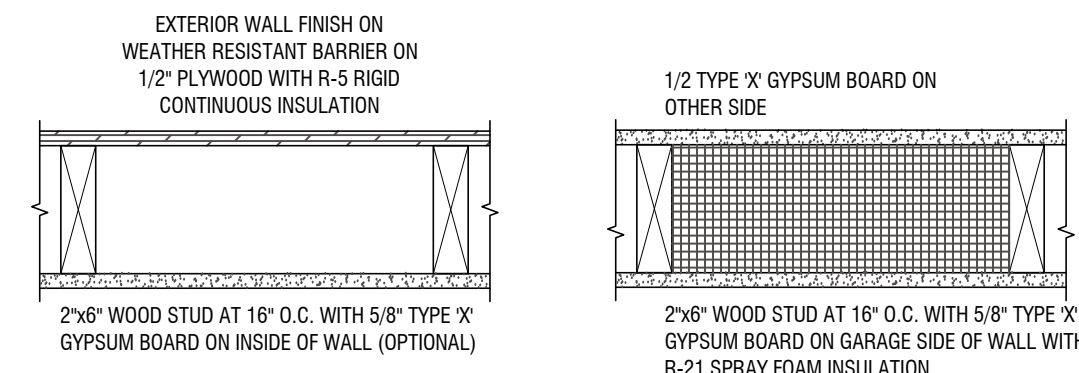


3 EXTERIOR WALL TYPE AT GARAGE

2 INTERIOR WALL TYPE

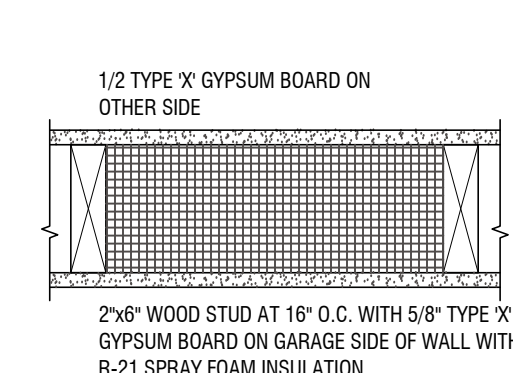

4 INTERIOR WALL TYPE AT GARAGE (FIRE RATED)

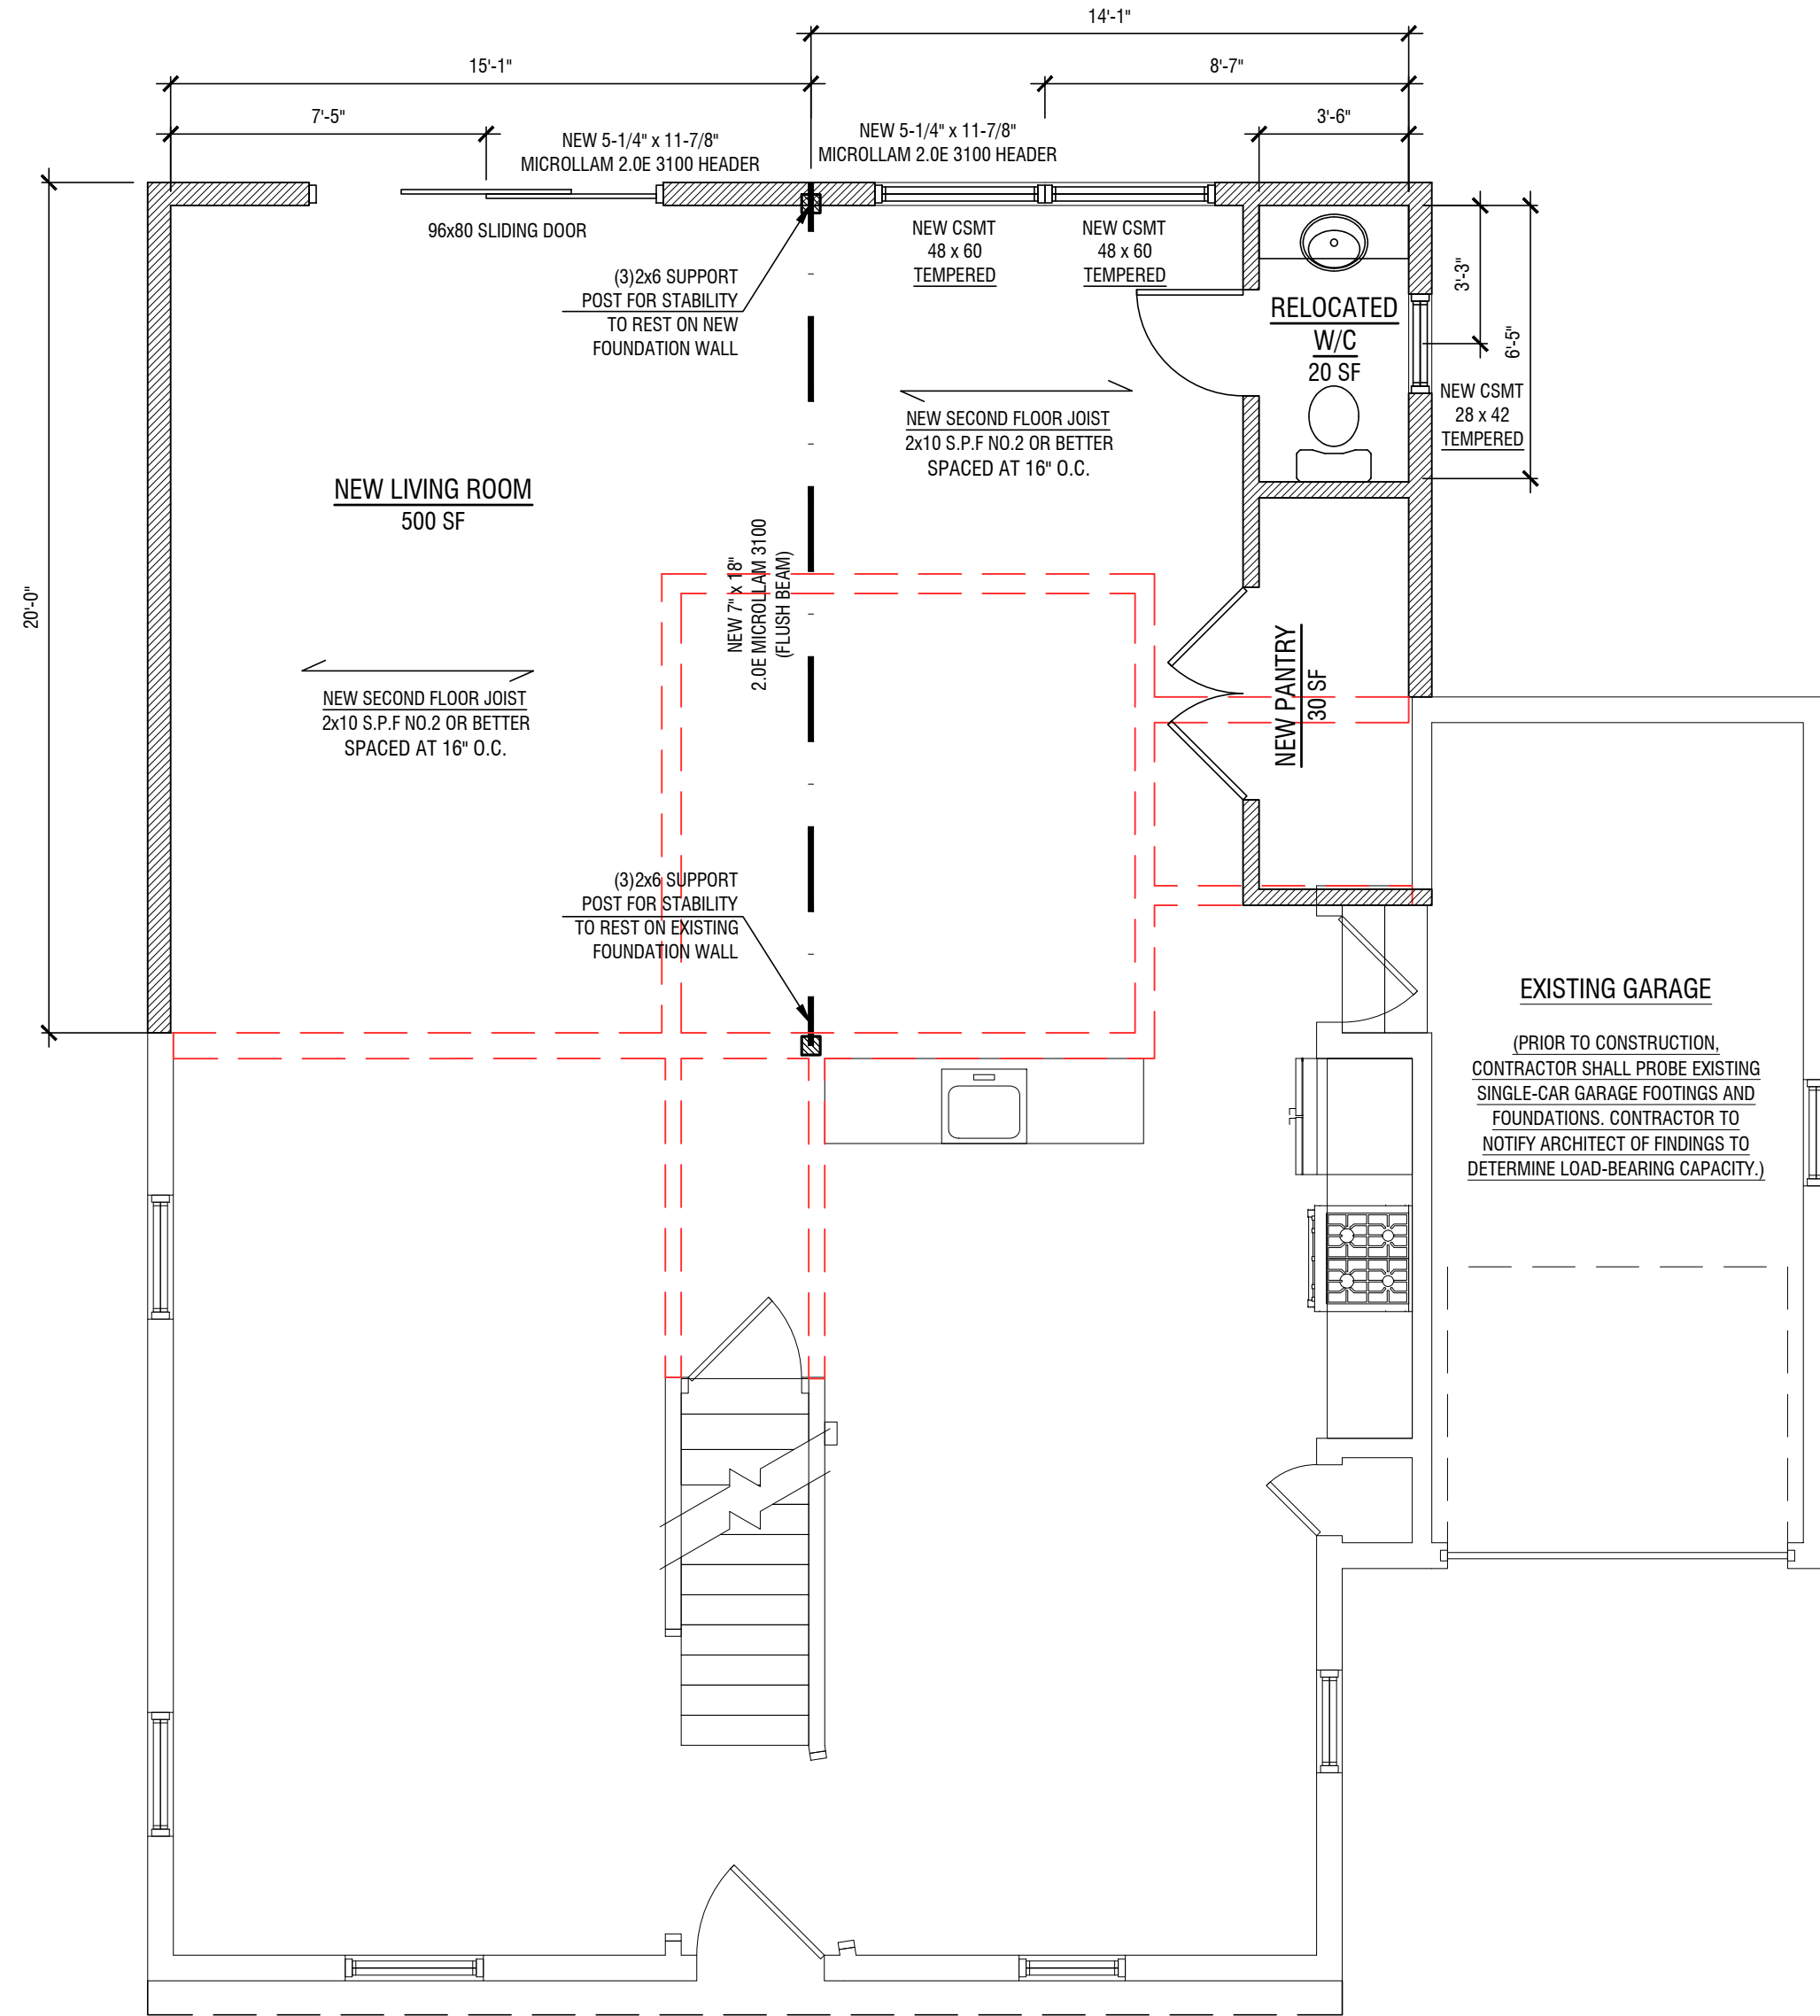

1 CONSTRUCTION PLAN - FIRST FLOOR
SCALE: 1/4"=1'-0"

REVISIONS:

REV. #	DESCRIPTION:	DATE:
	SUBMITTED FOR FILING	10.31.25

ADDITION/ALTERATION OF
BARNES RESIDENCE
44 BROOKVIEW TERRACE
BOROUGH OF BERGENFIELD
BERGEN COUNTY
BLOCK #291 LOT #101

DWG. TITLE:

CONSTRUCTION PLAN AND NOTES -
FIRST & SECOND FLOOR

ARCHITECTURAL LICENSE NUMBERS:
NJ 21A102225000
FL 101849
NY 1533422
PA RA-402635

BID SET ONLY.
NOT FOR CONSTRUCTION!

GRZEGORZ HASAJ, AIA - ARCHITECT

c. 973-508-2461
ghasaj.hdc@gmail.com

THIS DRAWING AND THE INFORMATION CONTAINED HEREIN ARE FOR THE EXCLUSIVE USE OF THE PARTY FOR WHOM THE WORK WAS CONTRACTED OR CERTIFIED. REPRODUCTION, DISTRIBUTION, OR RELIANCE BY OTHERS IS PROHIBITED WITHOUT THE PRIOR WRITTEN CONSENT OF HIGHLAND DESIGN & CONSULTING, LLC. ALL RIGHTS RESERVED.

DATE:
02.24.26
SCALE:
AS NOTED
DWN. BY:
GH

JOB NO.
026-001

CHK. BY:
GH

DWG. NO.

A-1

4 OF 8