




DRAFT

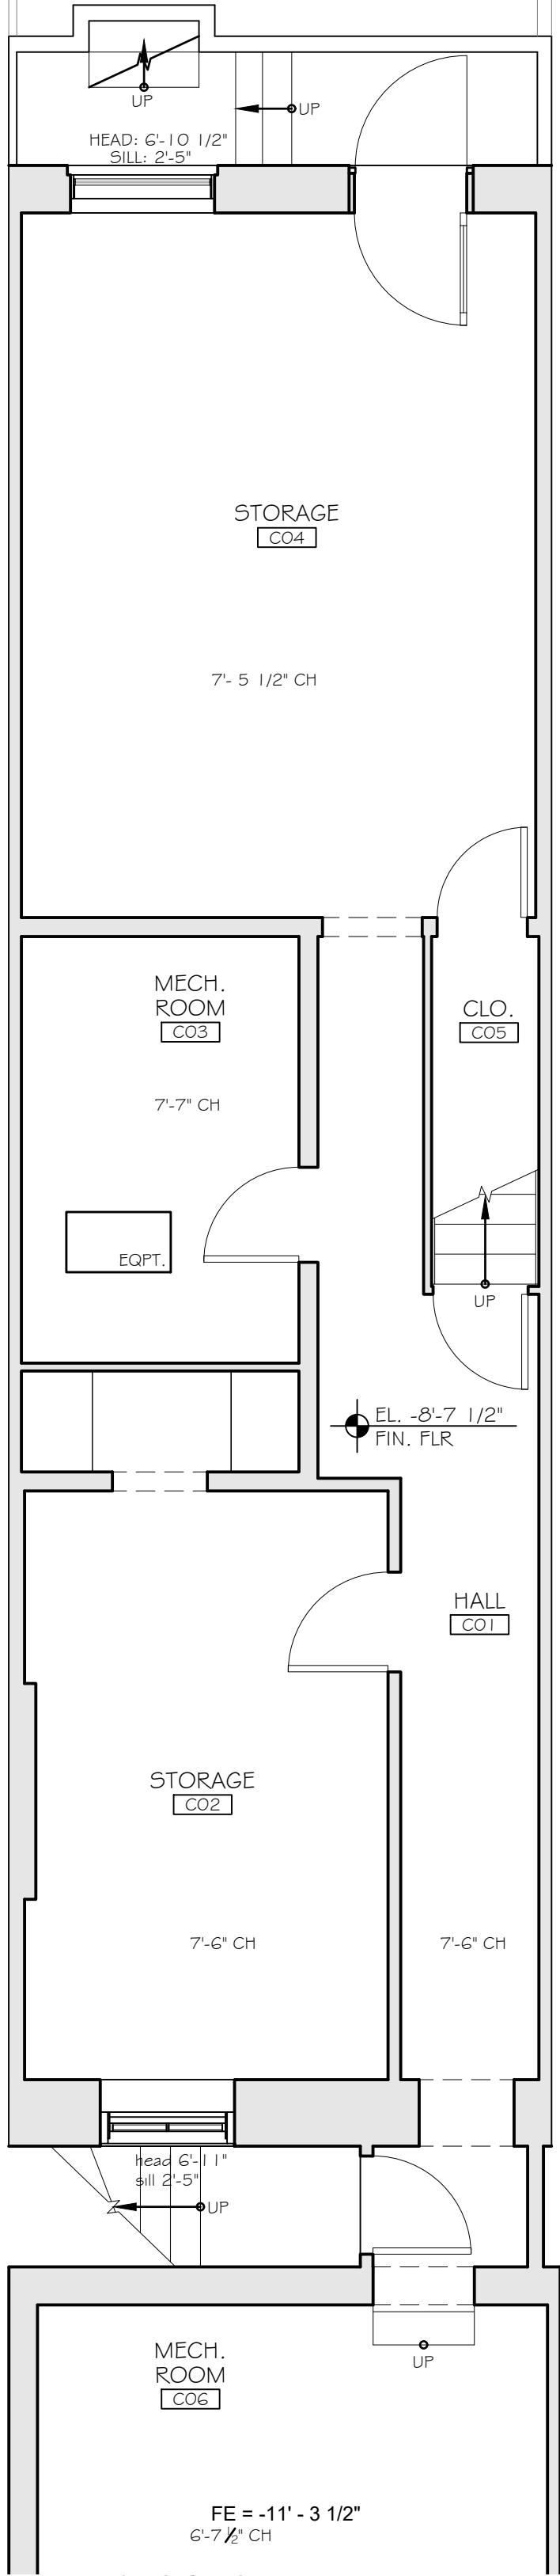


1 EXISTING CELLAR FLOOR PLAN
SCALE: 1/4" = 1'-0"

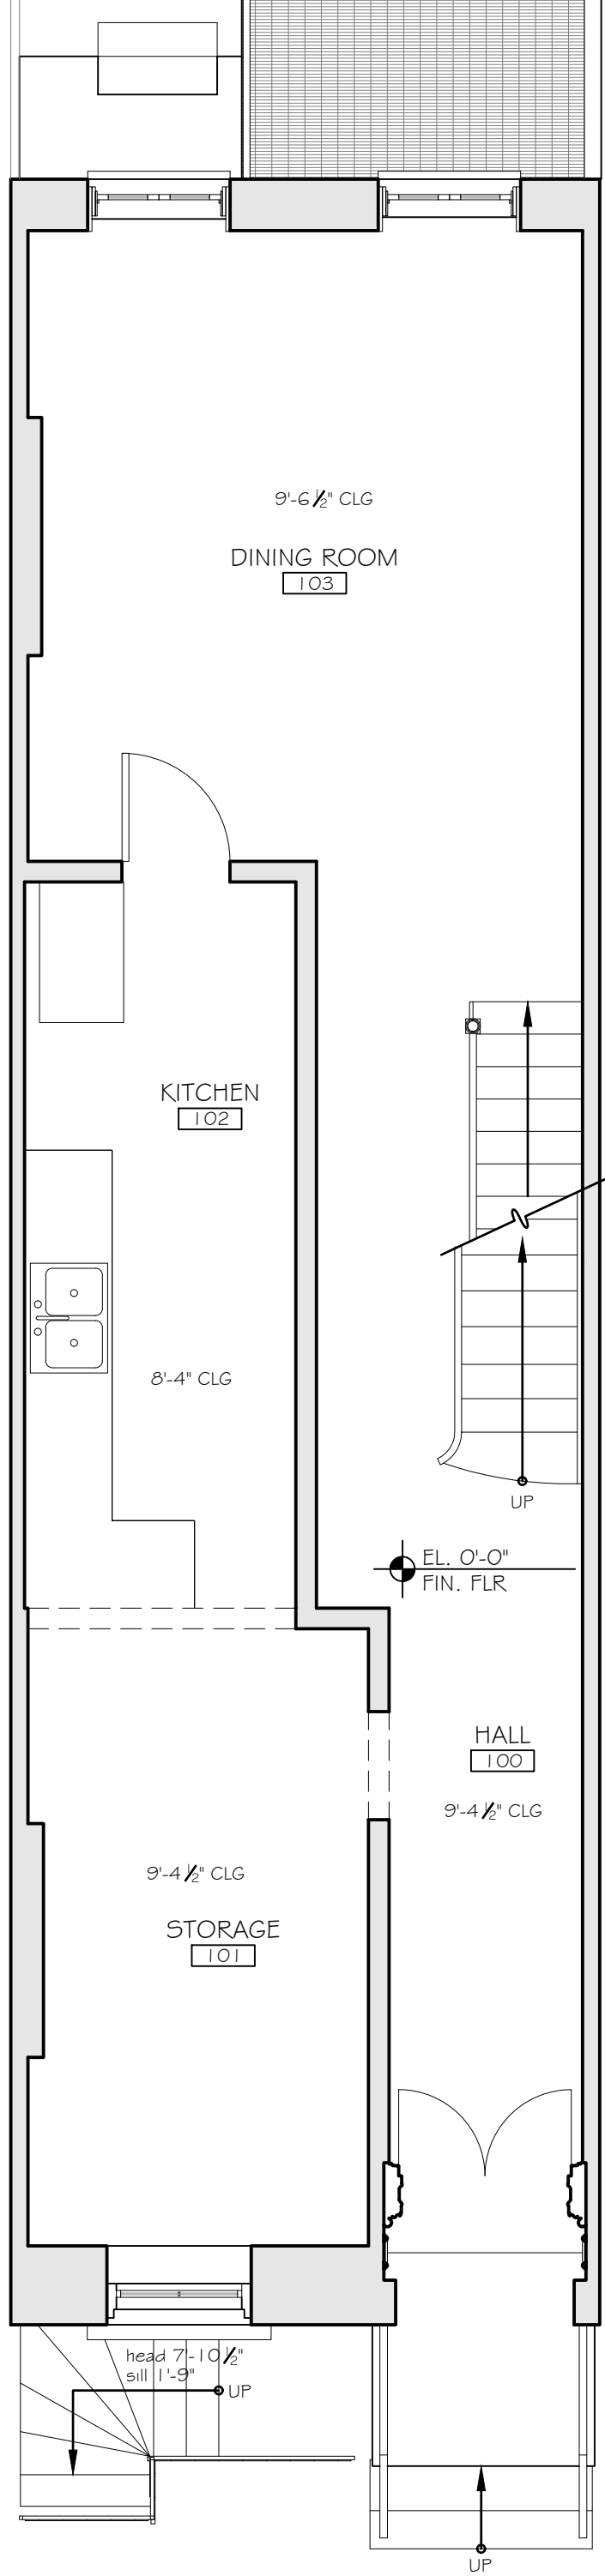


2 EXISTING GROUND FLOOR PLAN
SCALE: 1/4" = 1'-0"

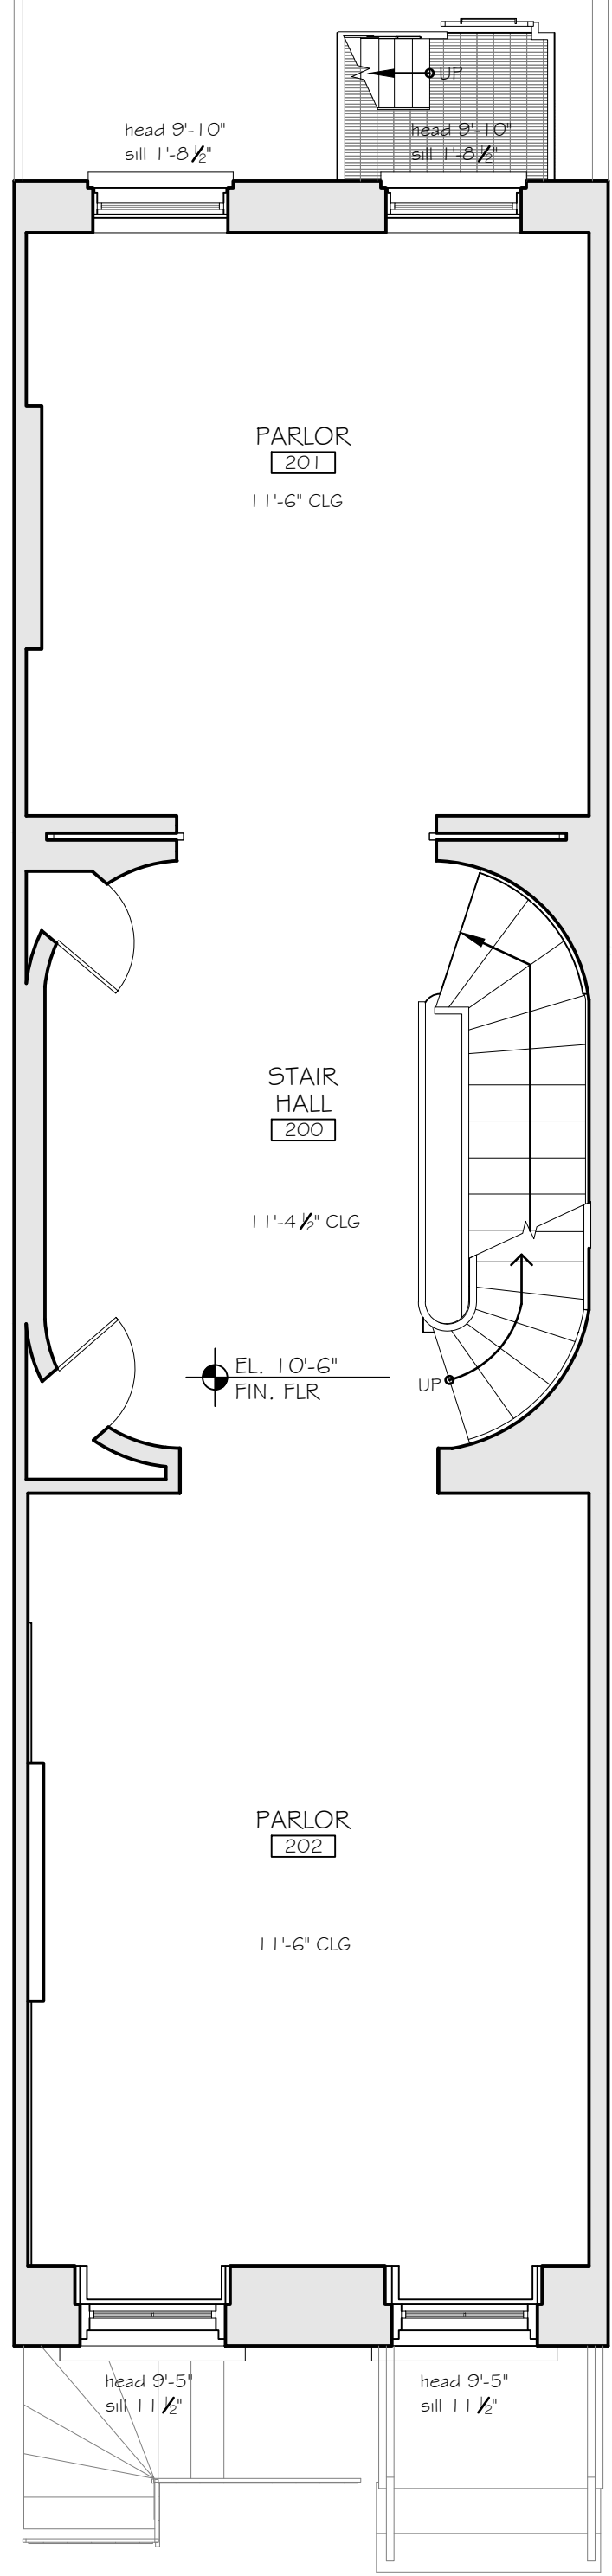


3 EXISTING 2ND FLOOR PLAN
SCALE: 1/4" = 1'-0"

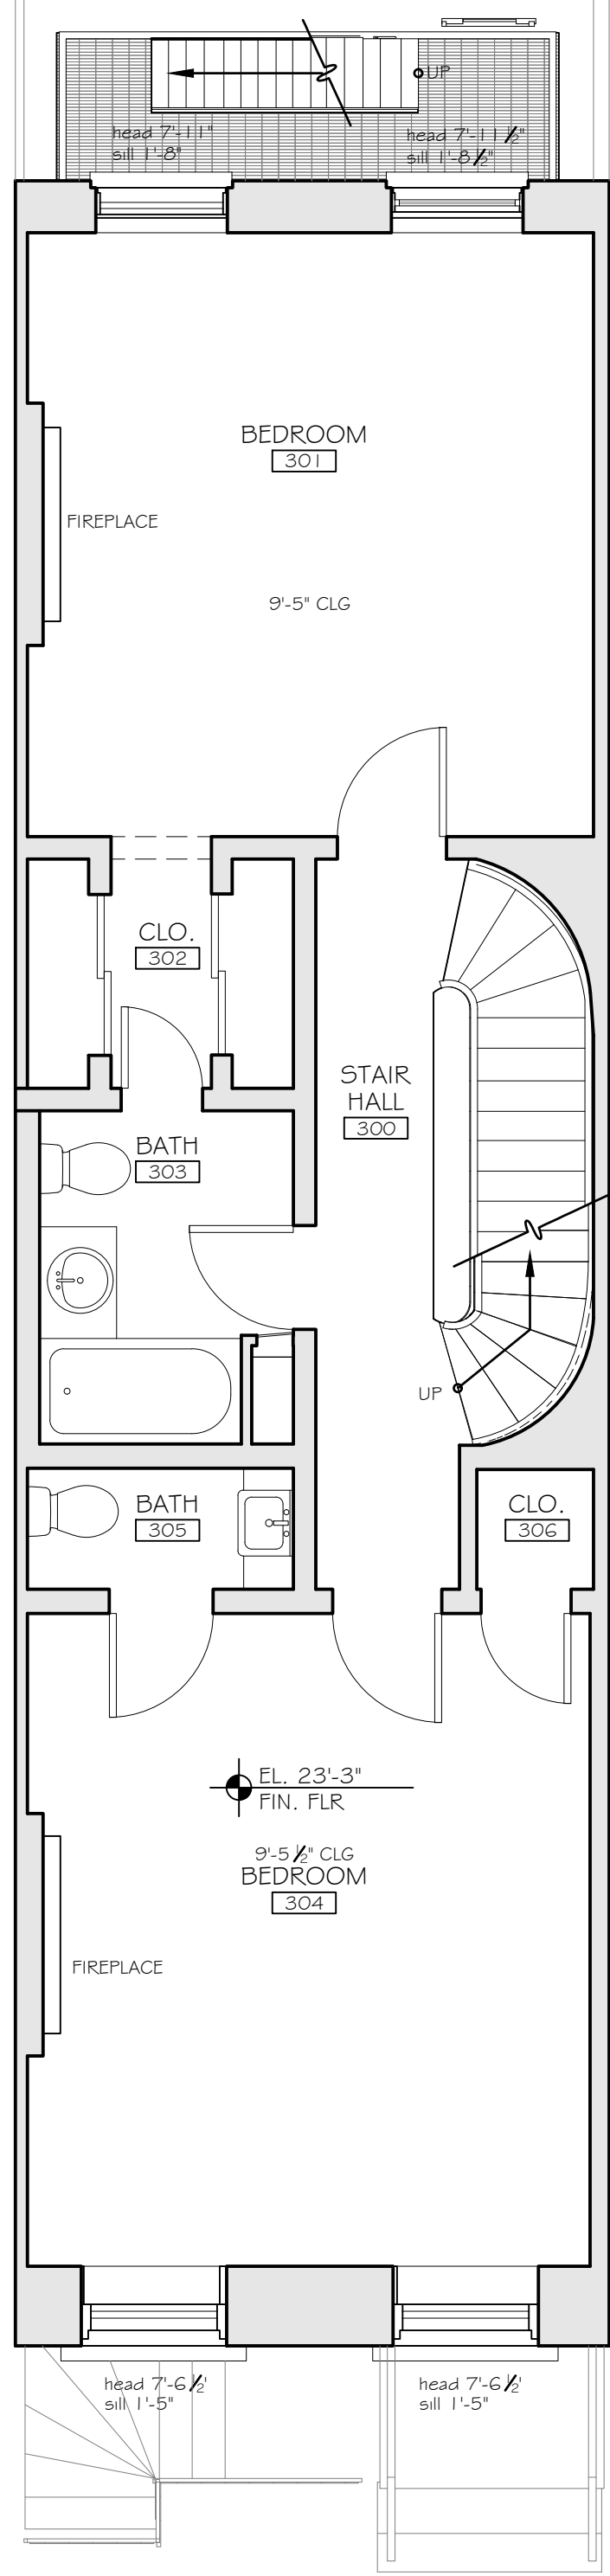

4 EXISTING 3RD FLOOR PLAN
SCALE: 1/4" = 1'-0"

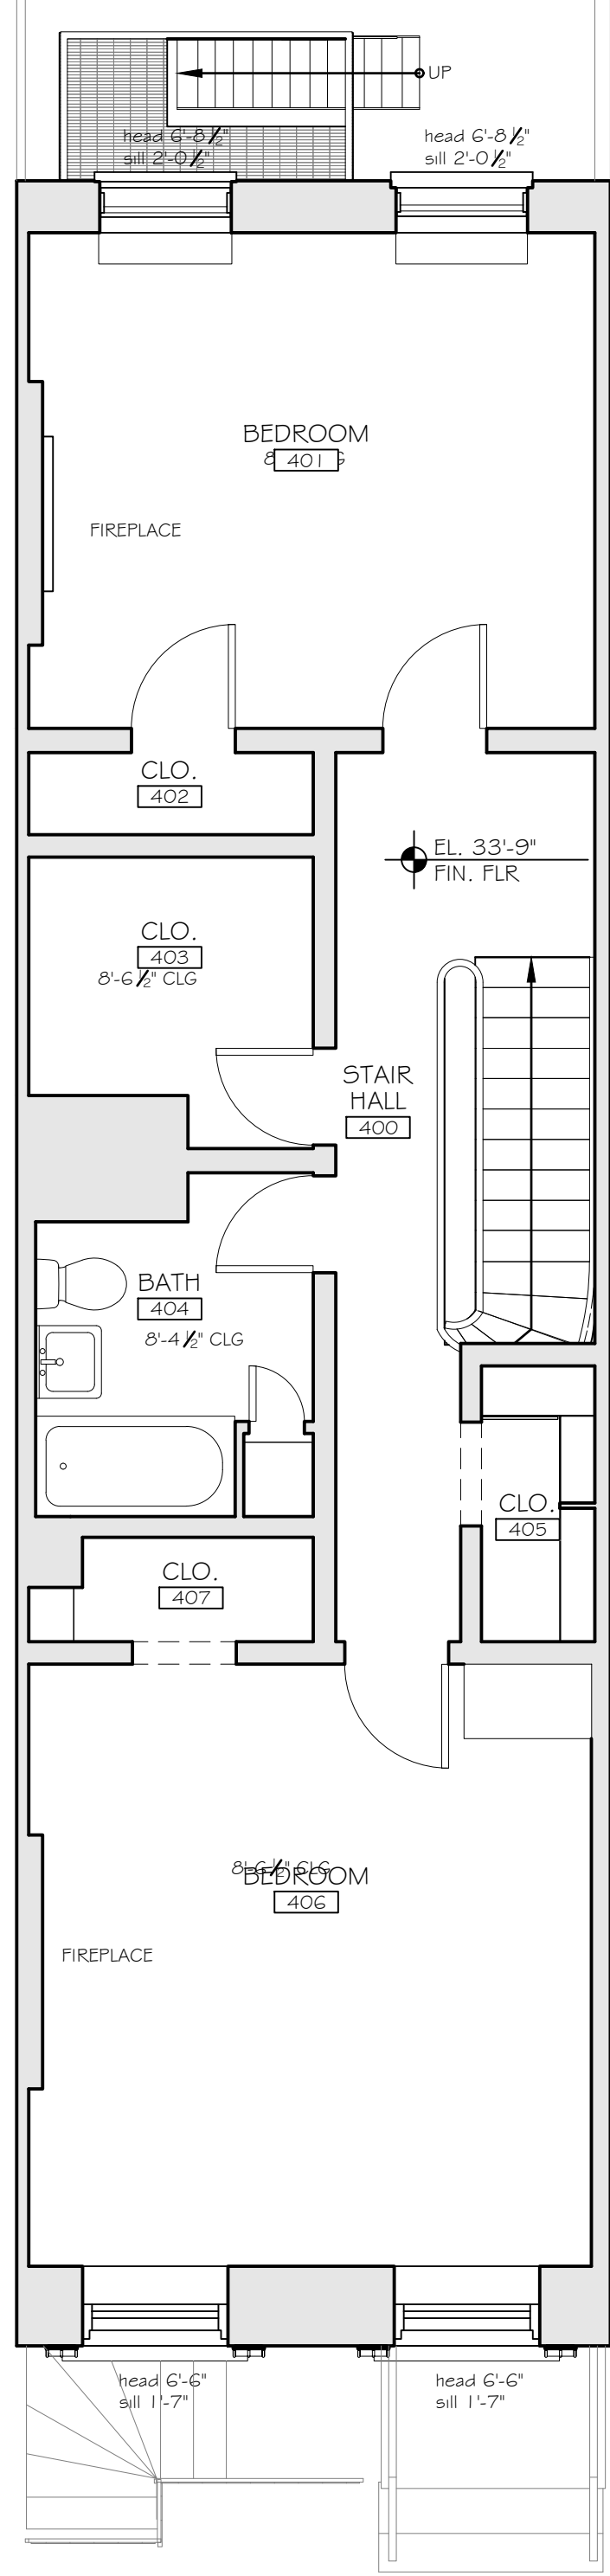

5 EXISTING 4TH FLOOR PLAN
SCALE: 1/4" = 1'-0"

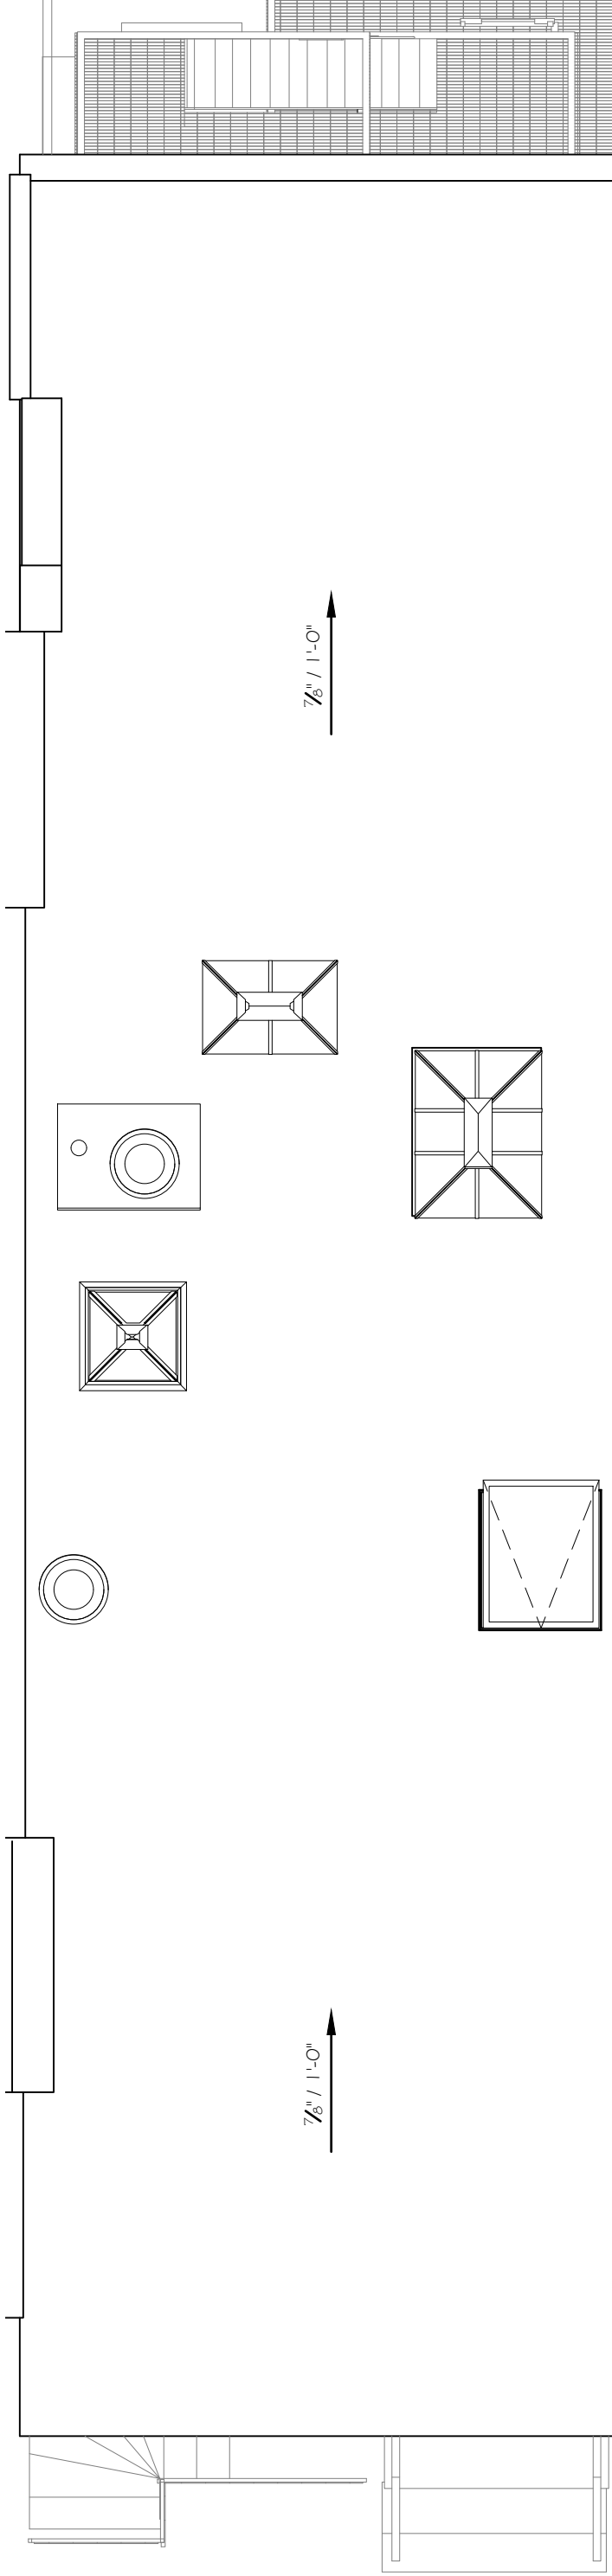

6 EXISTING ROOF PLAN
SCALE: 1/4" = 1'-0"

ISSUE: DATE:


NOTES:

ALEX TAYLOR ARCHITECTURE
241 CENTRAL PARK WEST (13B)
NEW YORK, NY 10024

TOWNHOUSE IN
GRAMERCY PARK
135 EAST 18TH STREET,
NEW YORK, NY 10003

EXISTING PLANS

DATE	AUG-13-2025	X-100
SCALE	AS NOTED	
DRAWN BY	AW	
PROJECT	2025.03	

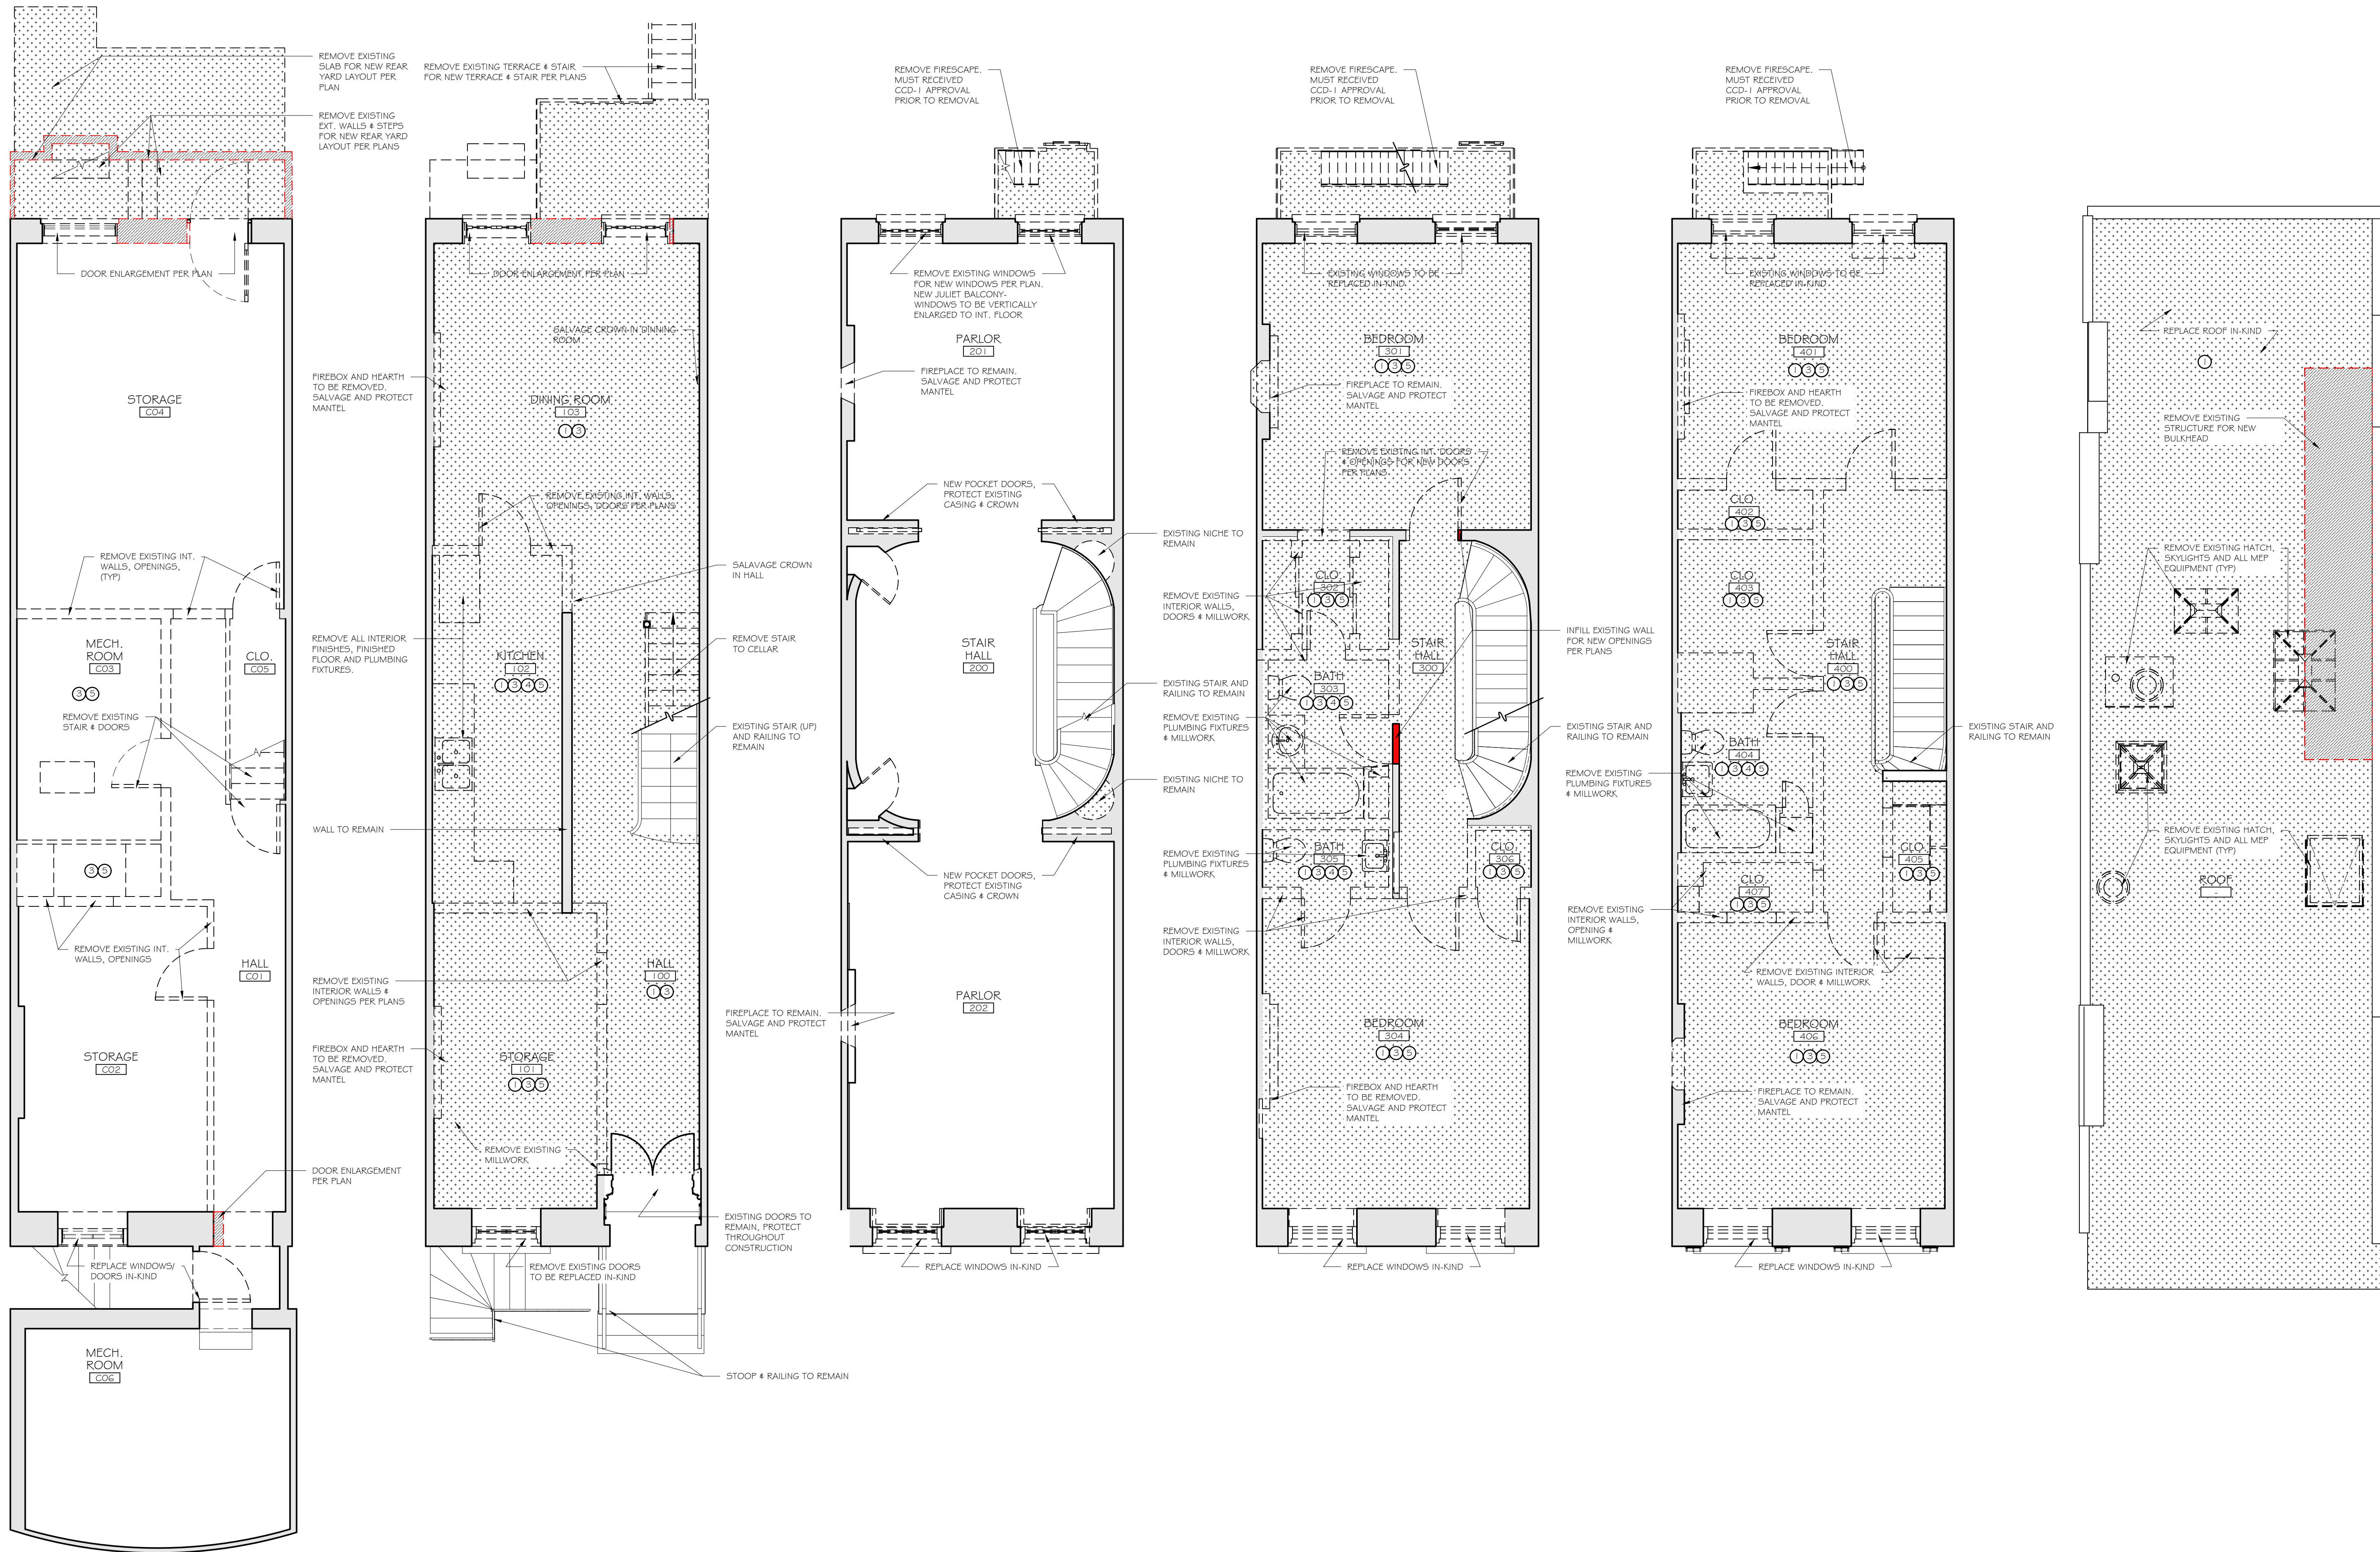

- NOTES:
- NOTE IN SCOPE OF WORK
 - EXISTING WALL TO REMAIN
 - EXISTING WALL TO BE INFILLED
 - EXISTING MECHANICAL TO REMAIN
 - EXISTING MECHANICAL TO BE REMOVED
 - EXISTING WALL TO BE REMOVED
 - EXISTING FLOOR TO BE REMOVED (AND SUBFLOOR IF REQUIRED)
 - EXISTING PARTITION WALL TO BE REMOVED
 - EXISTING PARTITION WALL TO REMAIN, FINISHES TO BE REMOVED
 - EXISTING DOOR TO BE REMOVED
 - EXISTING DOOR TO REMAIN
 - EXISTING EXTERIOR WINDOW TO BE REMOVED UNLESS OTHERWISE NOTED
 - EXISTING EXTERIOR WINDOW TO REMAIN UNLESS OTHERWISE NOTED
 - REMOVE FLOOR & SUBFLOOR (WATERPROOF IF REQ'D)
 - REMOVE CEILING FINISHES, TRIMS, LIGHTS & HANGARS
 - REMOVE ALL EXISTING MILLWORK
 - REMOVE ALL PLUMBING FIXTURES, FITTINGS & APPLIANCES
 - REMOVE EXISTING TRIM & WALL PANELING, TYP
1. ALL INTERIOR DOORS TO BE REMOVED.
2. ALL EXTERIOR WINDOWS & DOORS TO BE REMOVED U.O.N.
3. PRIOR TO REMOVING ANY STRUCTURAL BEARING WALLS, DISCUSS TEMP. SHORING REQUIREMENTS
4. PARTI WALL TO REMAIN UNTOUCHED


ALEX TAYLOR ARCHITECTURE
241 CENTRAL PARK WEST (13B)
NEW YORK, NY 10024

TOWNHOUSE IN
GRAMERCY PARK
135 EAST 18TH STREET,
NEW YORK, NY 10003

DEMO PLANS

DATE	AUG-13-2025	D-100
SCALE	AS NOTED	
DRAWN BY	AW	
PROJECT	2025.03	

NOTES:

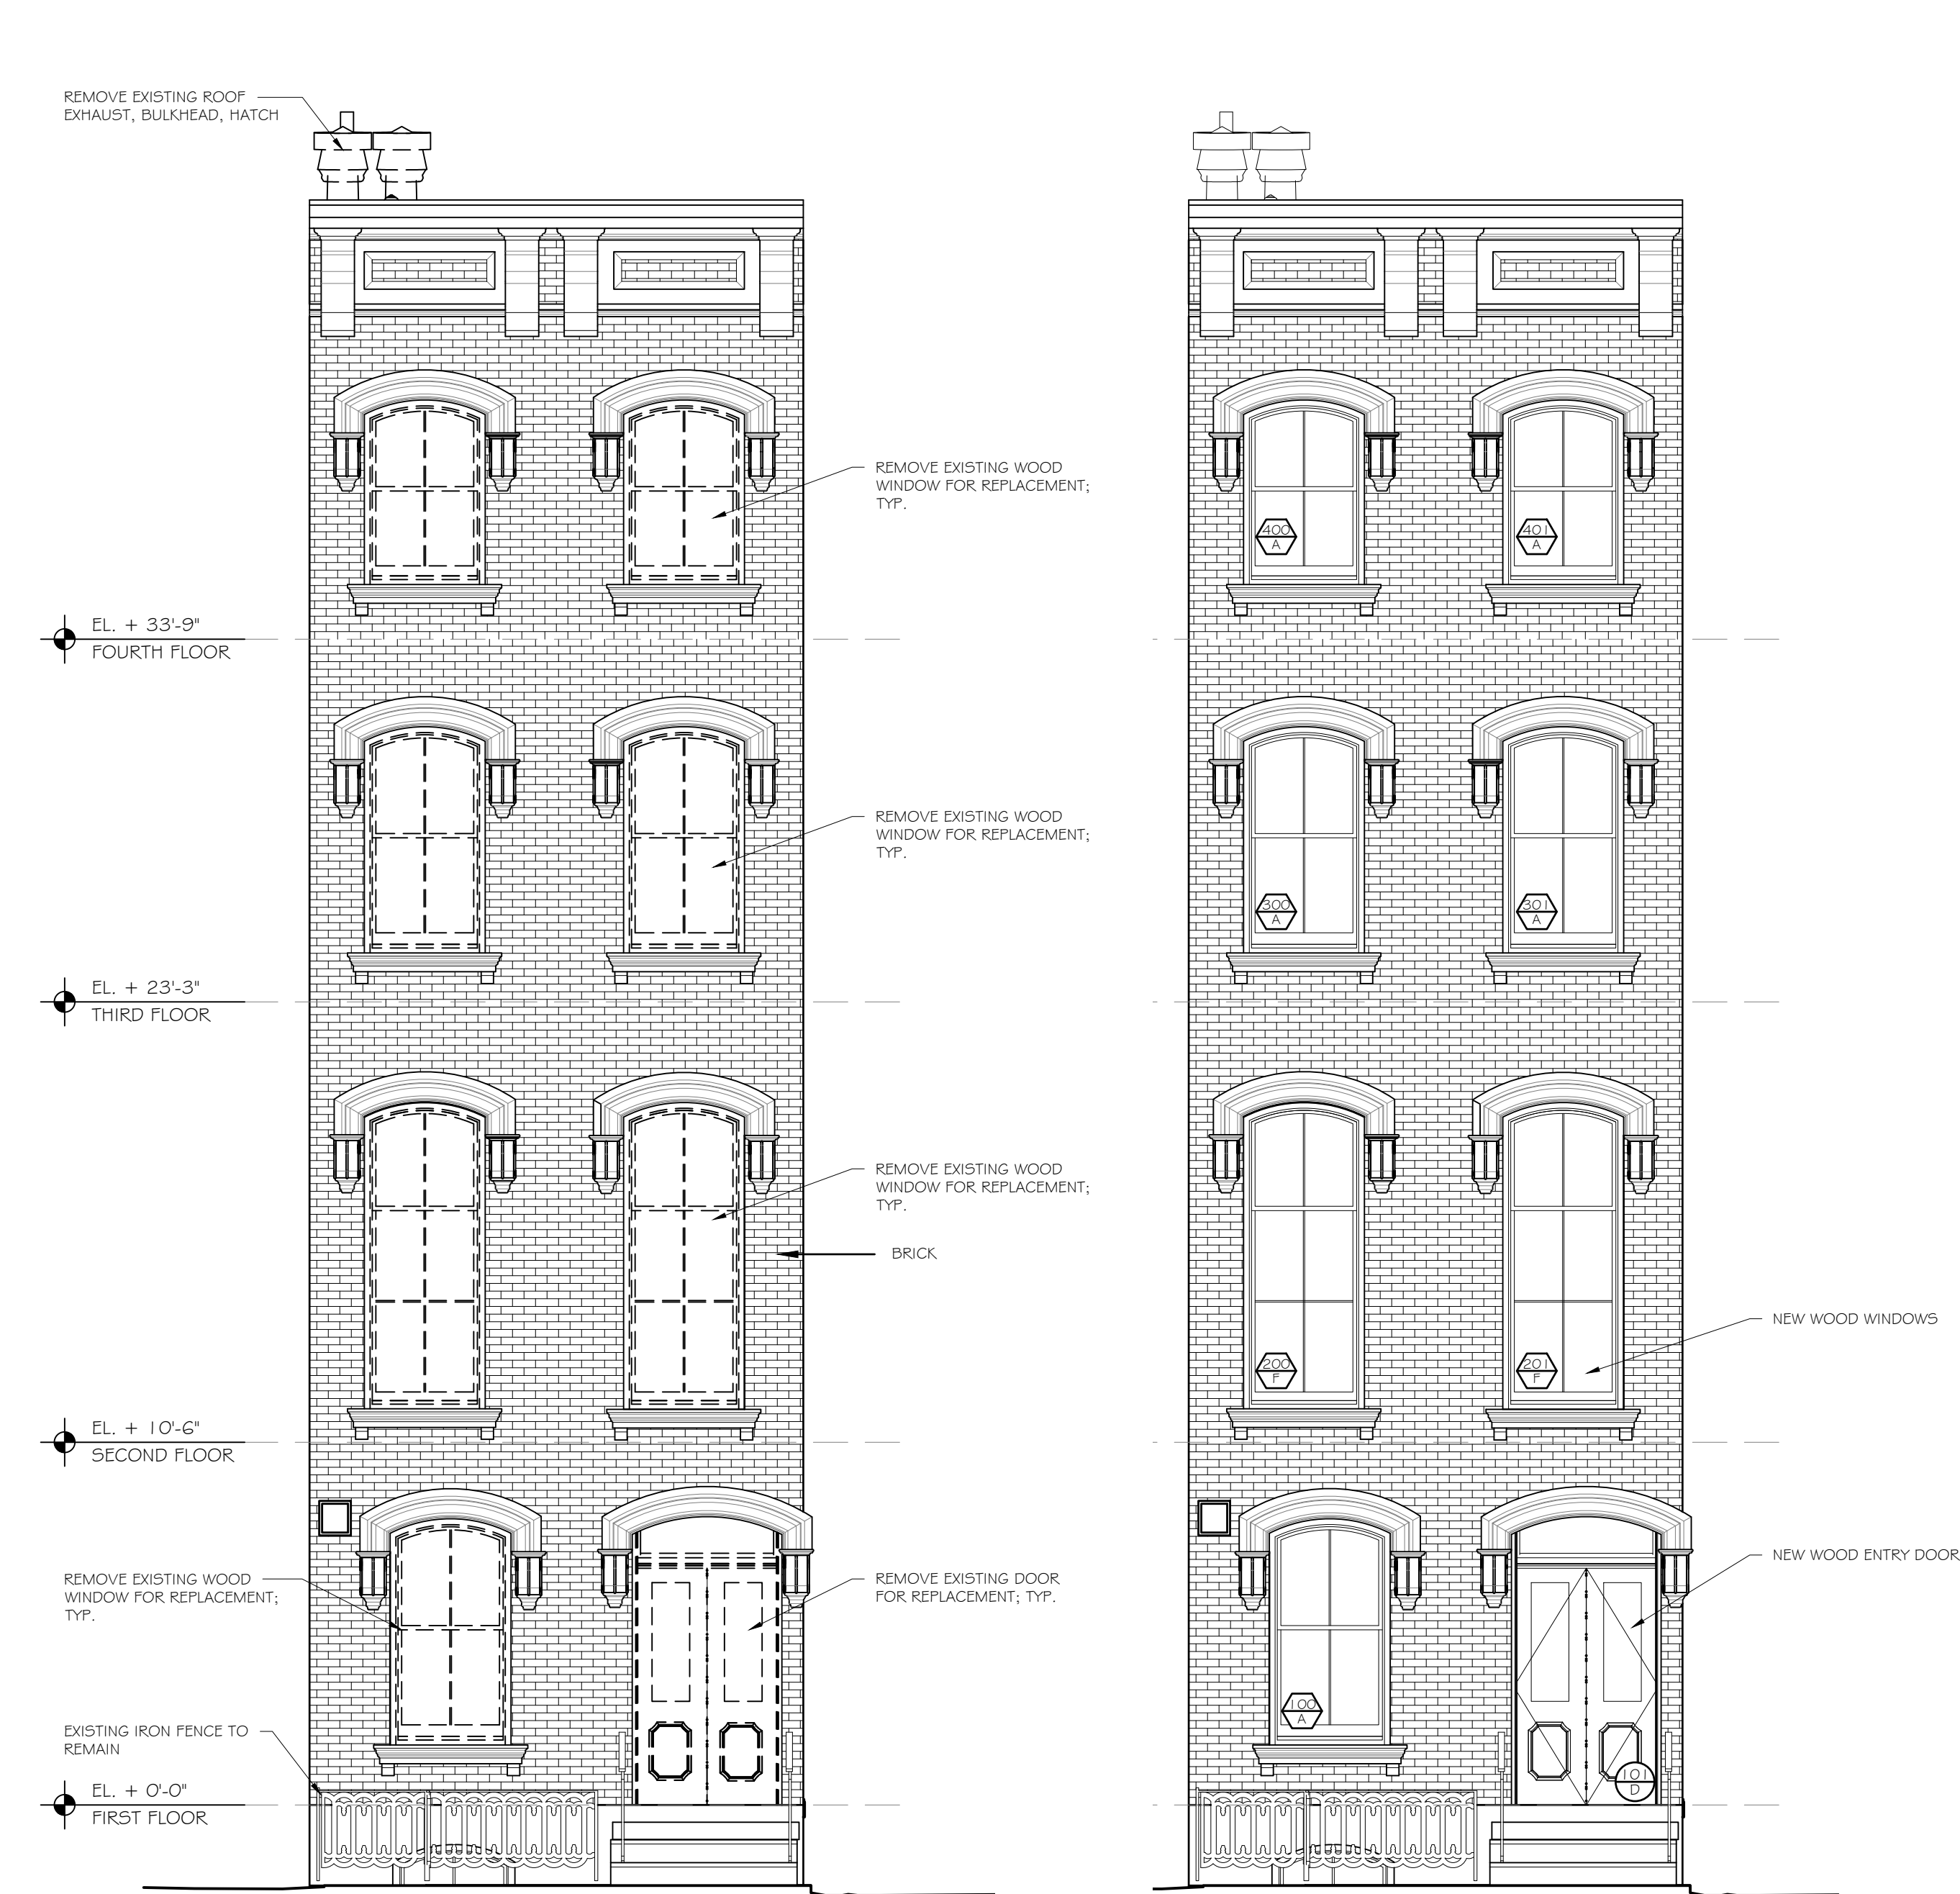

1 DEMO FRONT ELEVATION
A-200 SCALE: 1/4"= 1'-0"

2 PROPOSED FRONT ELEVATION
A-200 SCALE: 1/4"= 1'-0"



3 DEMO REAR ELEVATION
A-200 SCALE: 1/4"= 1'-0"

4 PROPOSED REAR ELEVATION
A-200 SCALE: 1/4"= 1'-0"


ALEX TAYLOR ARCHITECTURE
241 CENTRAL PARK WEST (13B)
NEW YORK, NY 10024

TOWNHOUSE IN
GRAMERCY PARK
135 EAST 18TH STREET,
NEW YORK, NY 10003


DEMO & PROPOSED
EXTERIOR ELEVATIONS

DATE	AUG-13-2025	A-200
SCALE	AS NOTED	
DRAWN BY	AW	
PROJECT	2025.03	


DRAFT

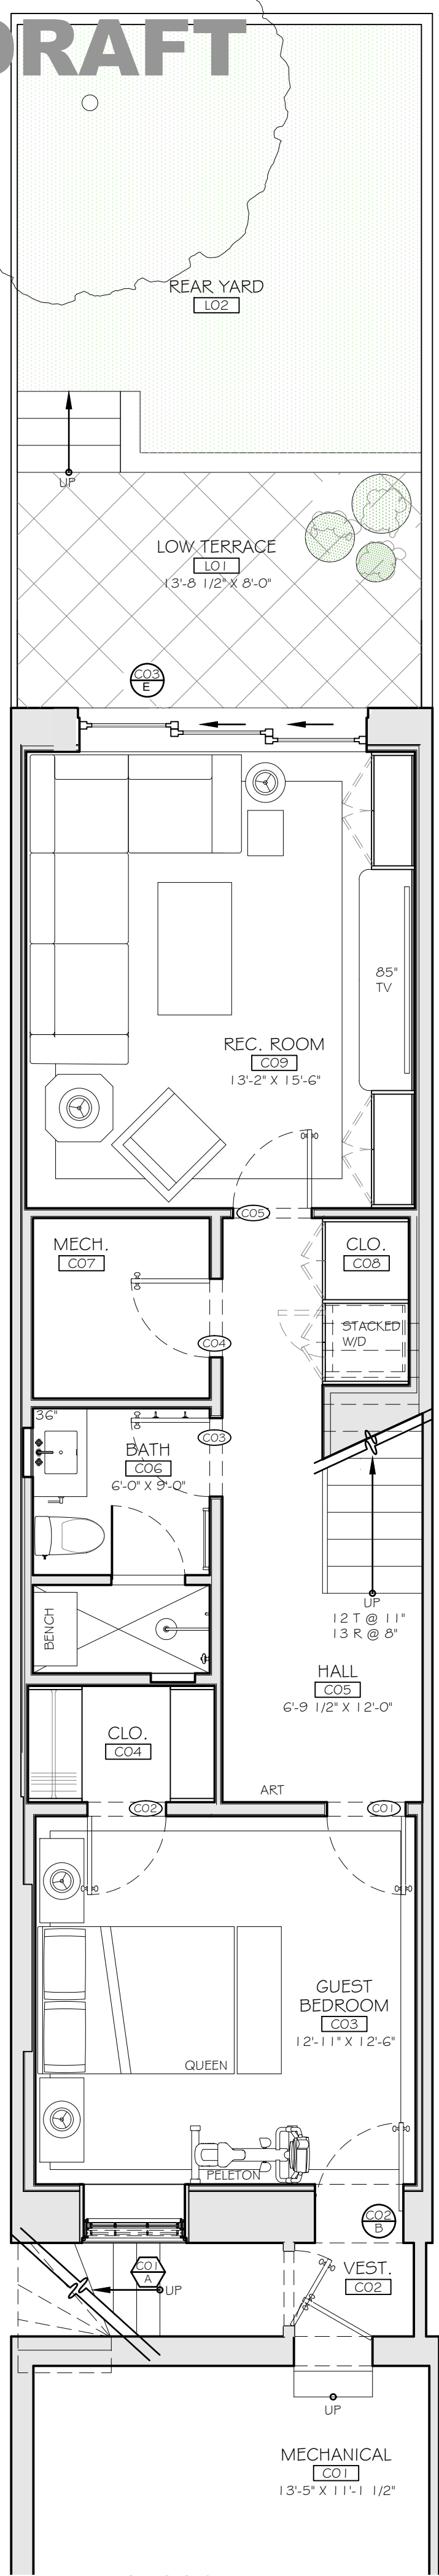


1 PROPOSED CELLAR PLAN
A-100 SCALE: 1/4"=1'-0"

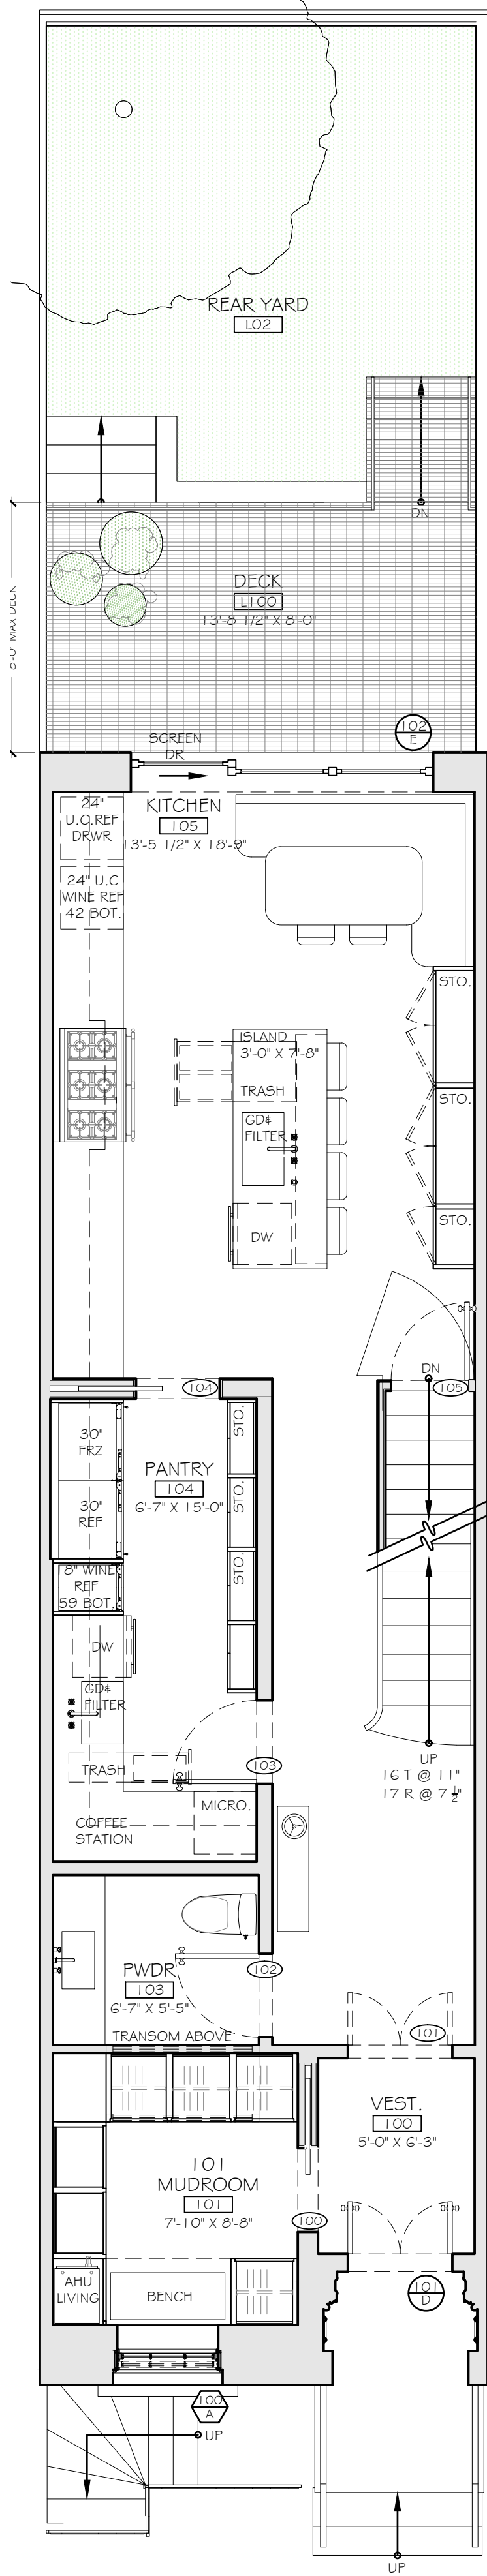


2 PROPOSED GROUND FLOOR PLAN
A-100 SCALE: 1/4"=1'-0"

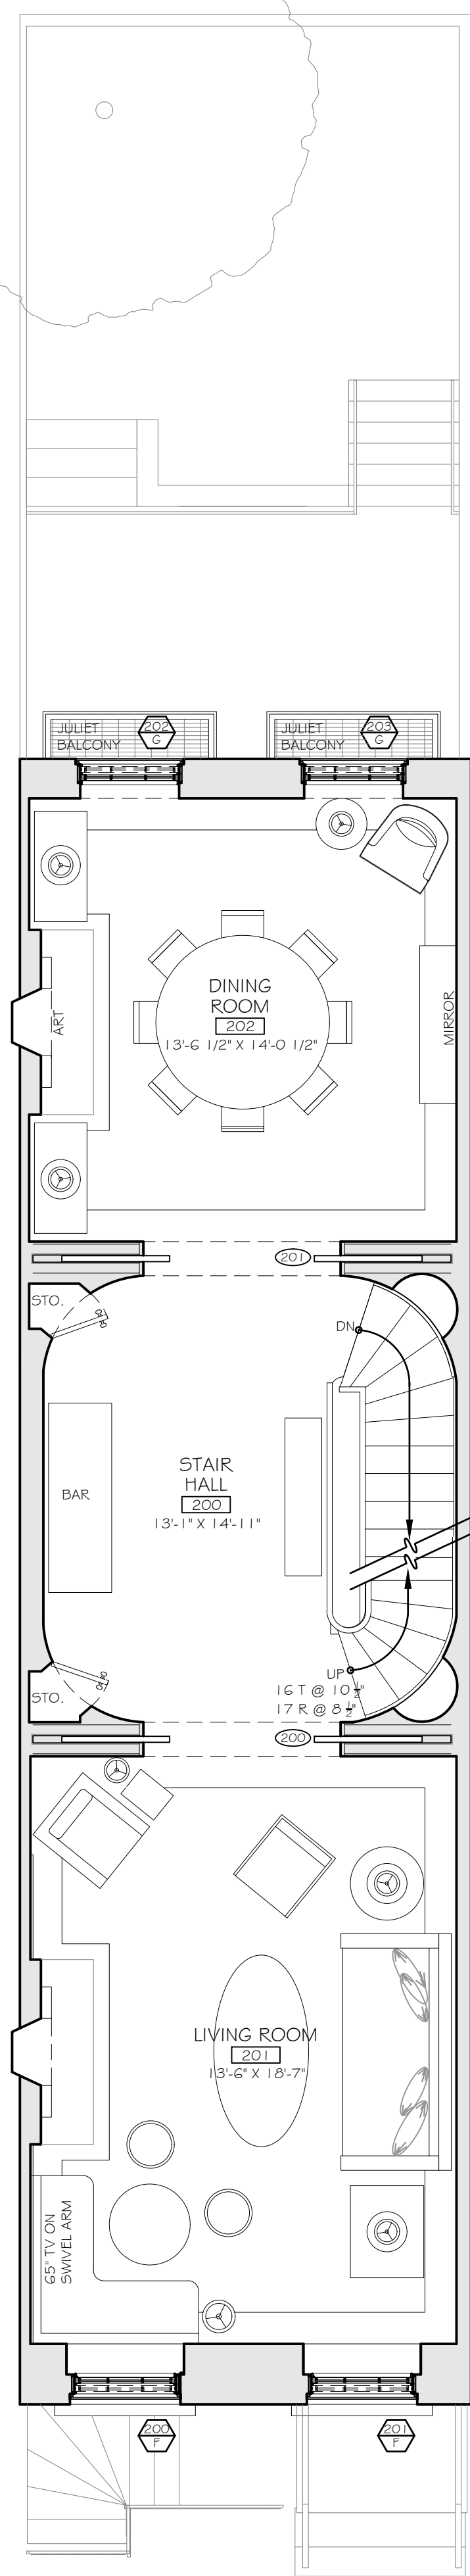


3 PROPOSED 2ND FLOOR PLAN
A-100 SCALE: 1/4"=1'-0"

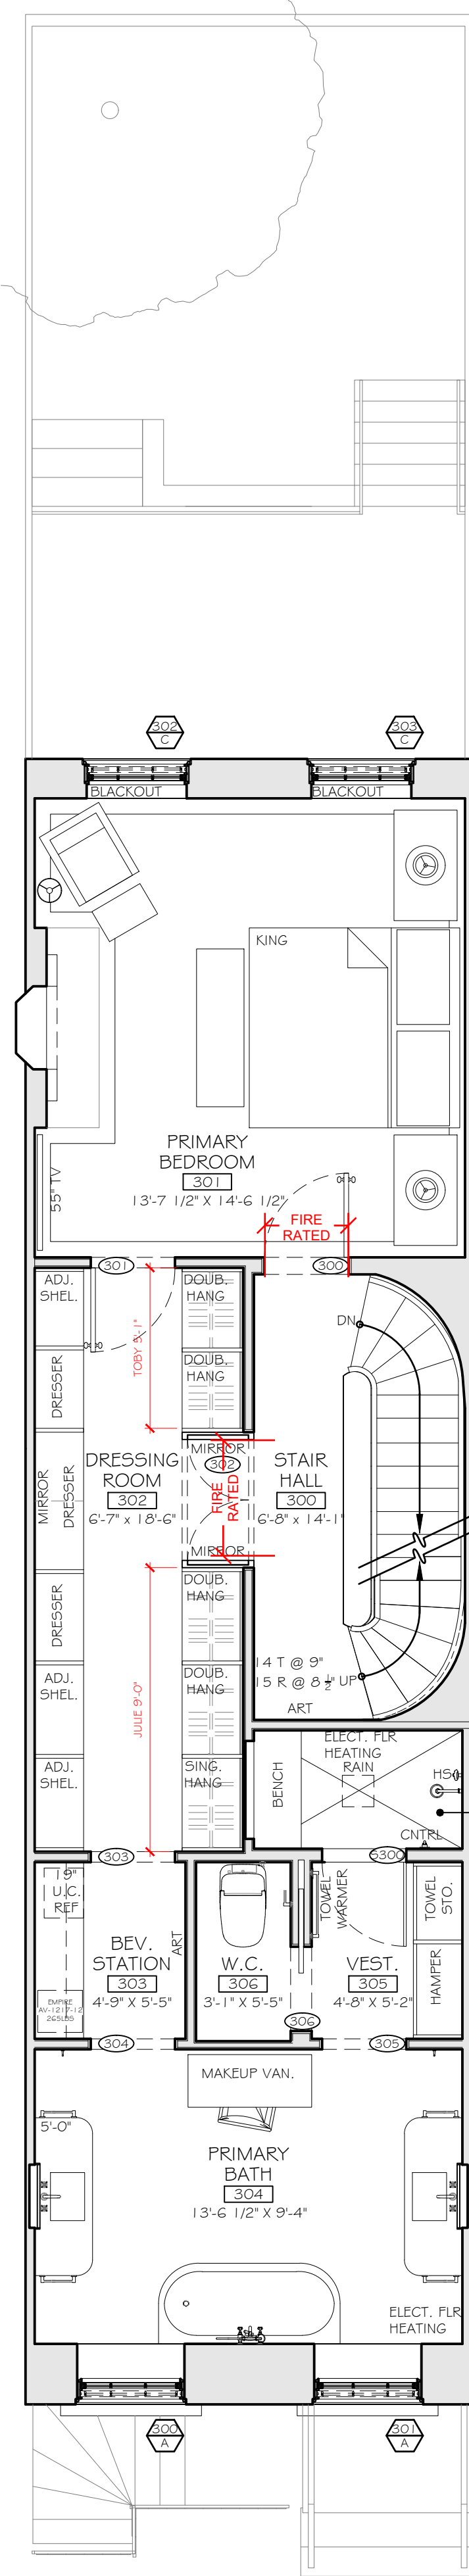

4 PROPOSED 3RD FLOOR PLAN
A-100 SCALE: 1/4"=1'-0"

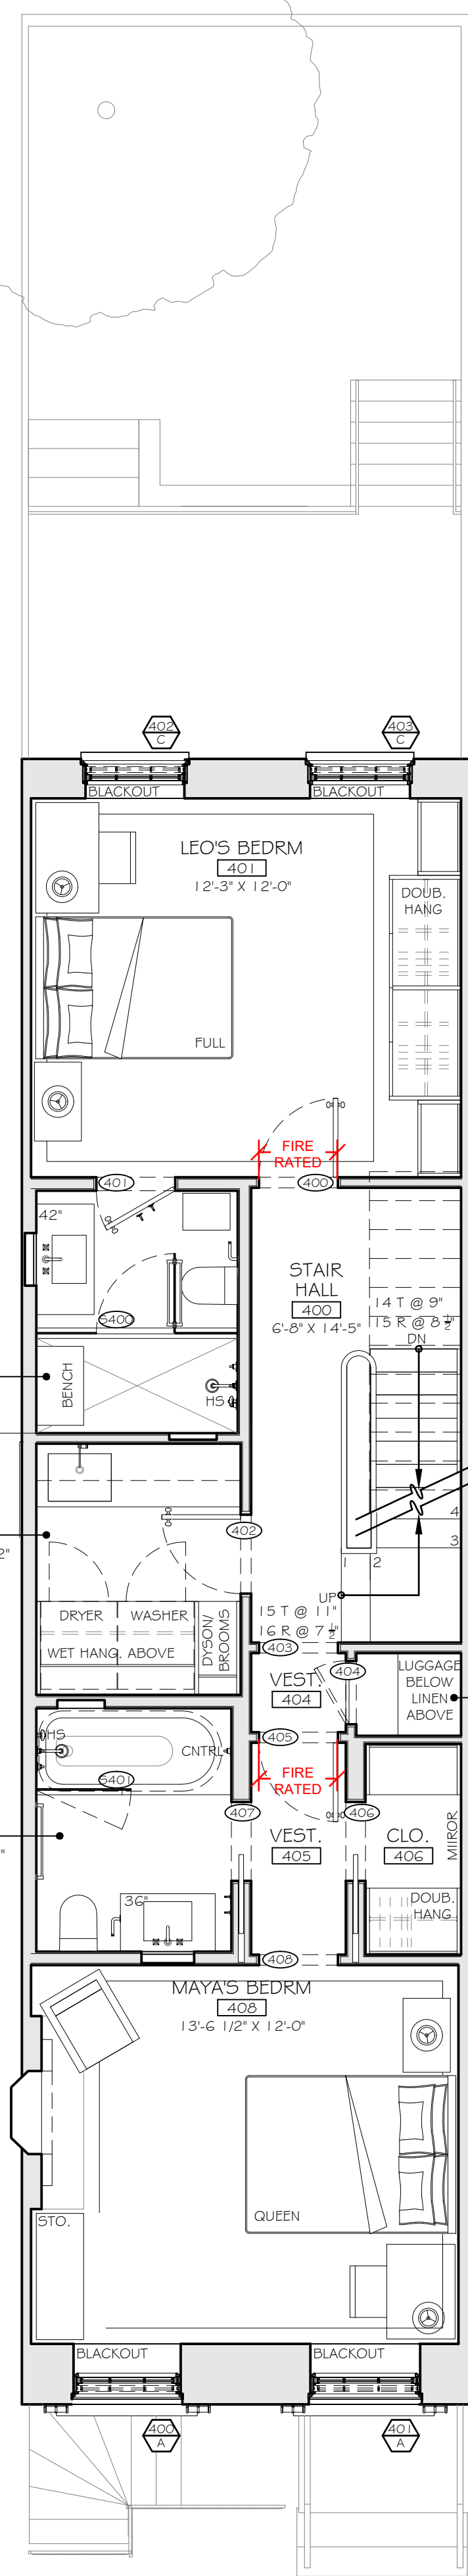

5 PROPOSED 4TH FLOOR PLAN
A-100 SCALE: 1/4"=1'-0"

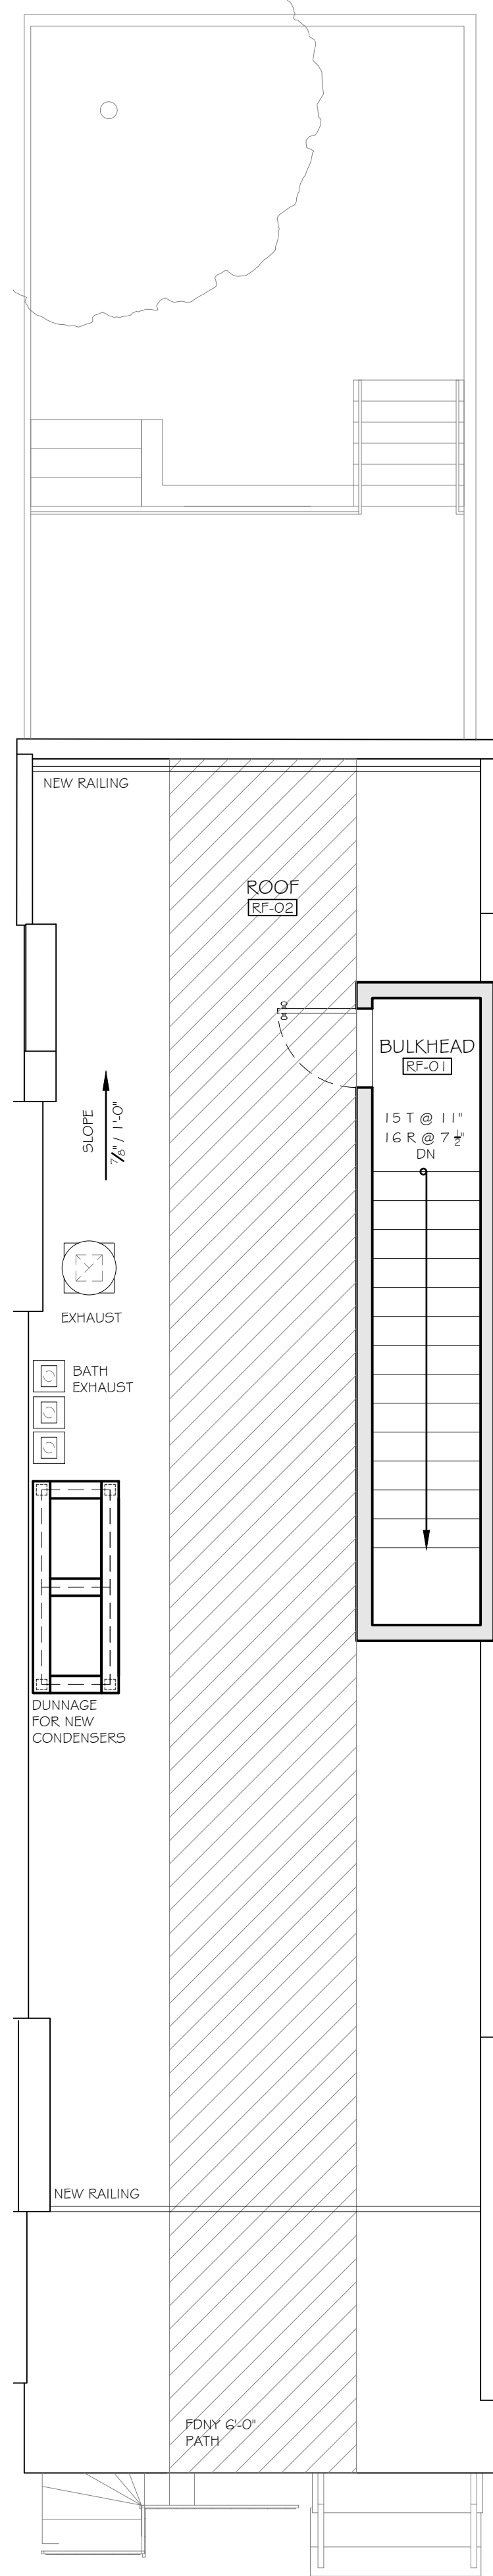

6 PROPOSED ROOF PLAN
A-100 SCALE: 1/4"=1'-0"

ISSUE: DATE:

NOTES:


ALEX TAYLOR ARCHITECTURE
241 CENTRAL PARK WEST (13B)
NEW YORK, NY 10024

TOWNHOUSE IN
GRAMERCY PARK
135 EAST 18TH STREET,
NEW YORK, NY 10003


PROPOSED PLANS

DATE	AUG-13-2025	A-100
SCALE	AS NOTED	
DRAWN BY	AW	
PROJECT	2025.03	


DRAFT

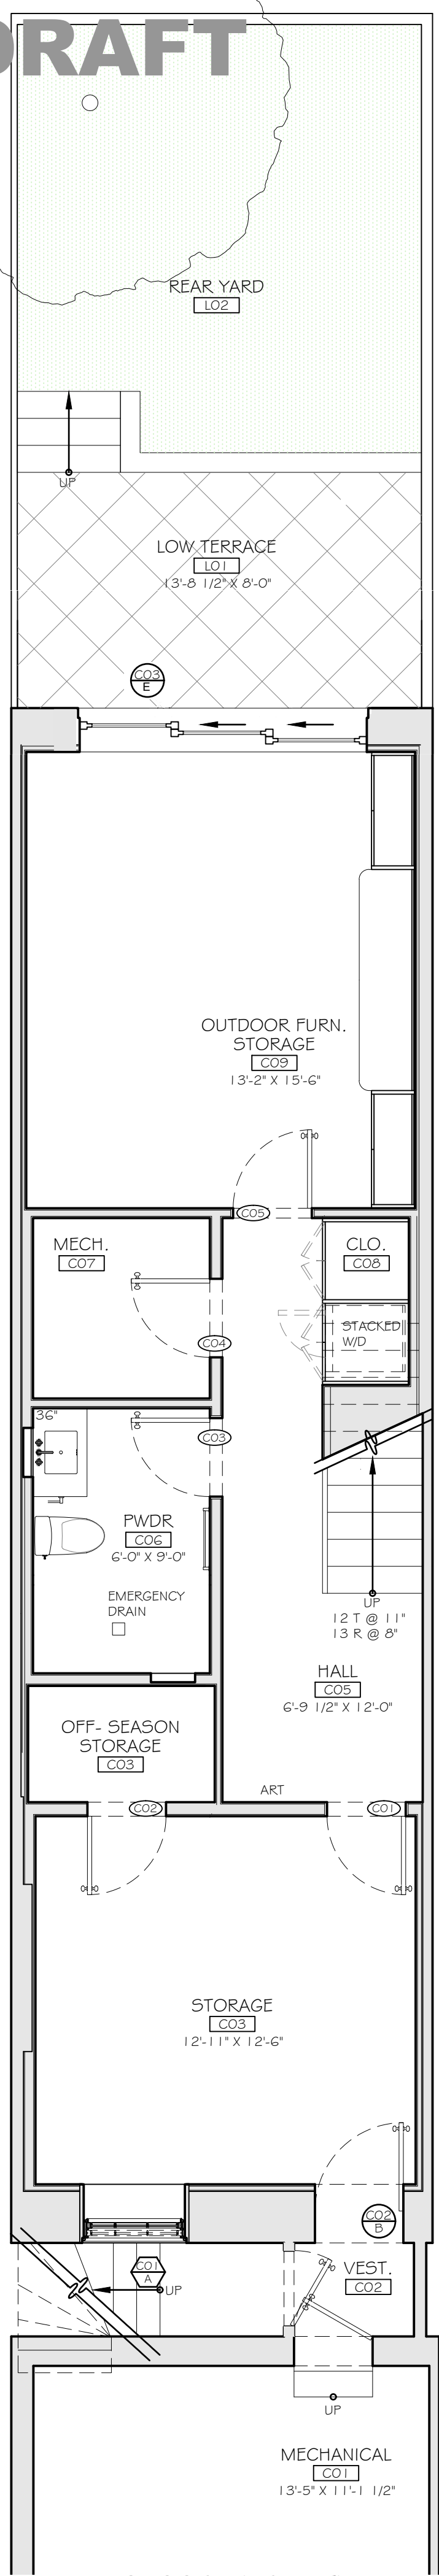


1 PROPOSED (PERMIT) CELLAR PLAN
SCALE: 1/4"=1'-0"

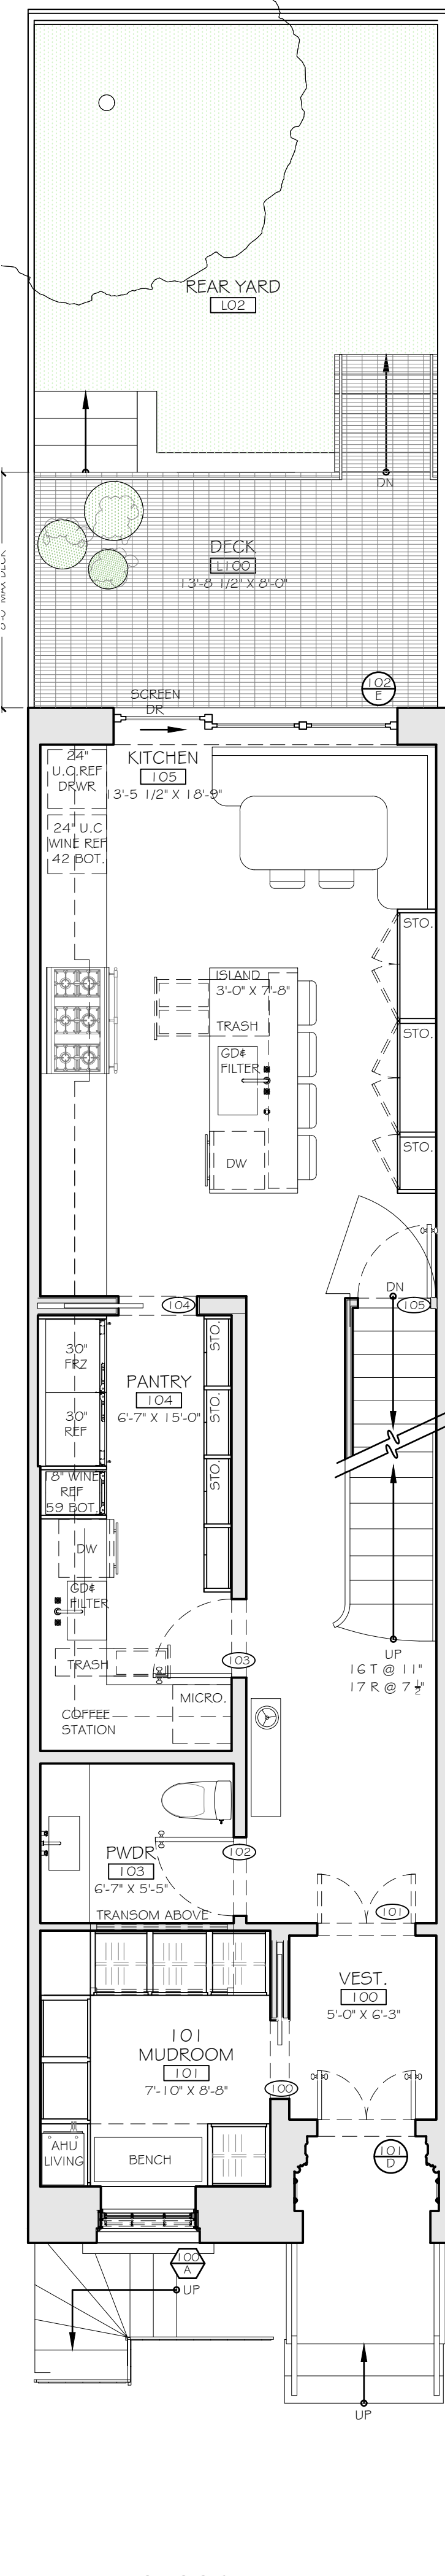


2 PROPOSED GROUND FLOOR PLAN
SCALE: 1/4"=1'-0"

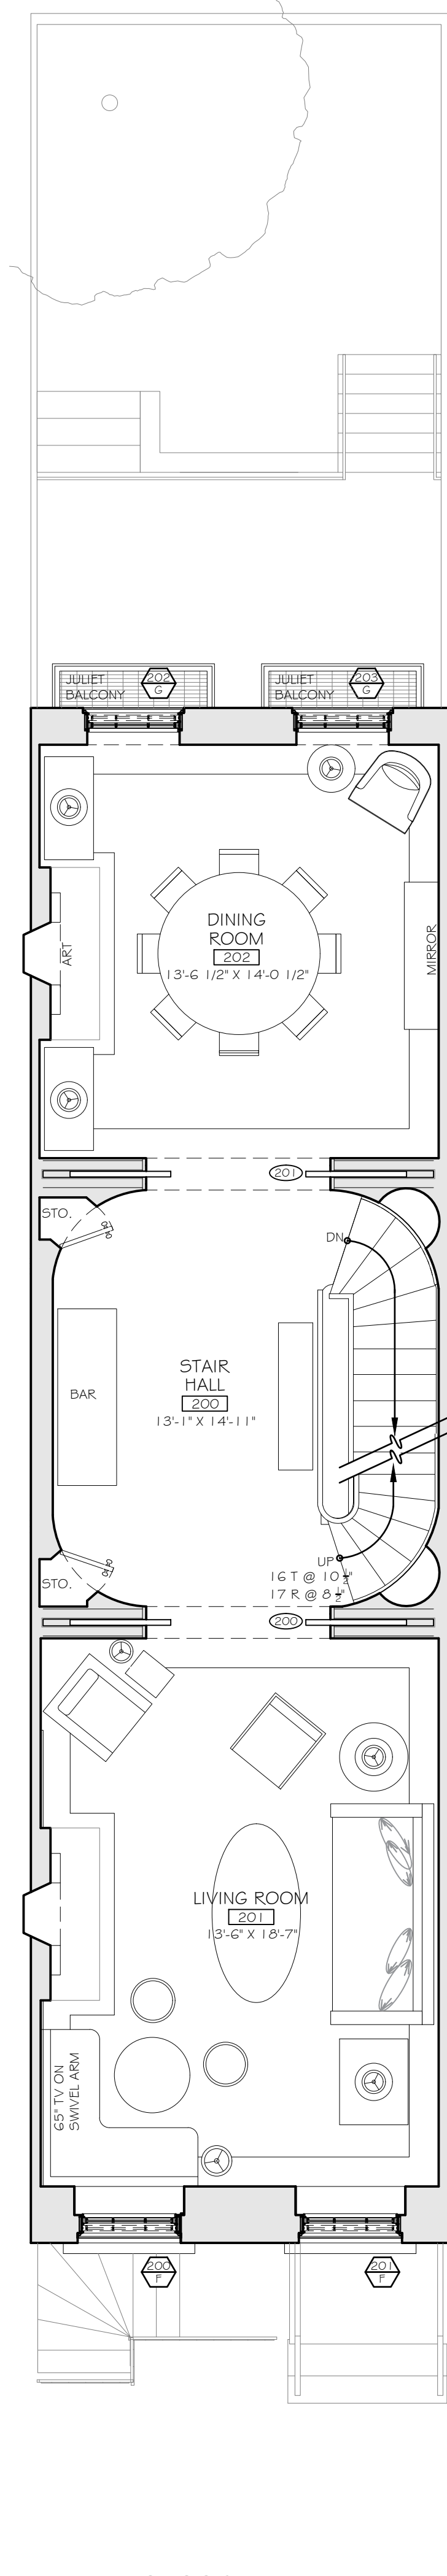


3 PROPOSED 2ND FLOOR PLAN
SCALE: 1/4"=1'-0"

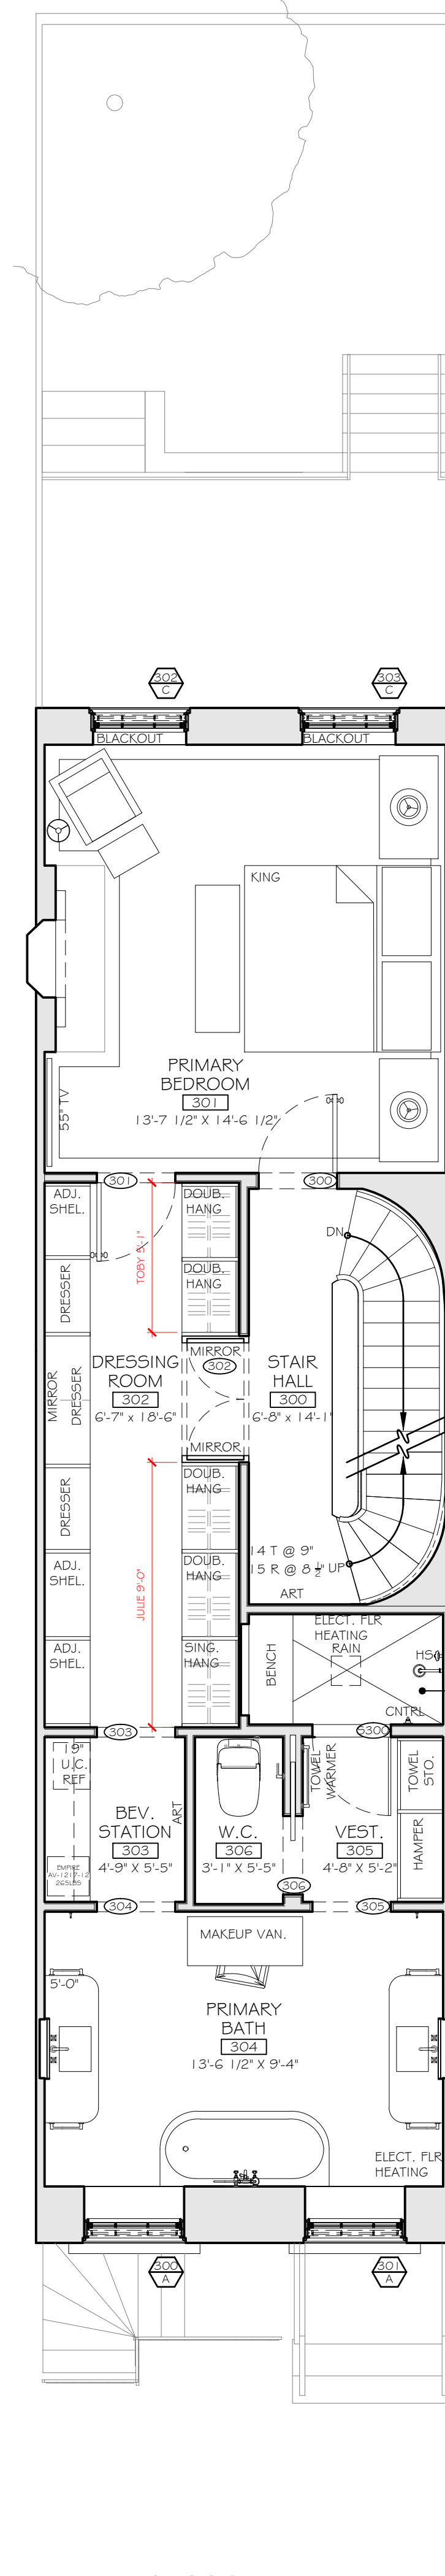

4 PROPOSED 3RD FLOOR PLAN
SCALE: 1/4"=1'-0"

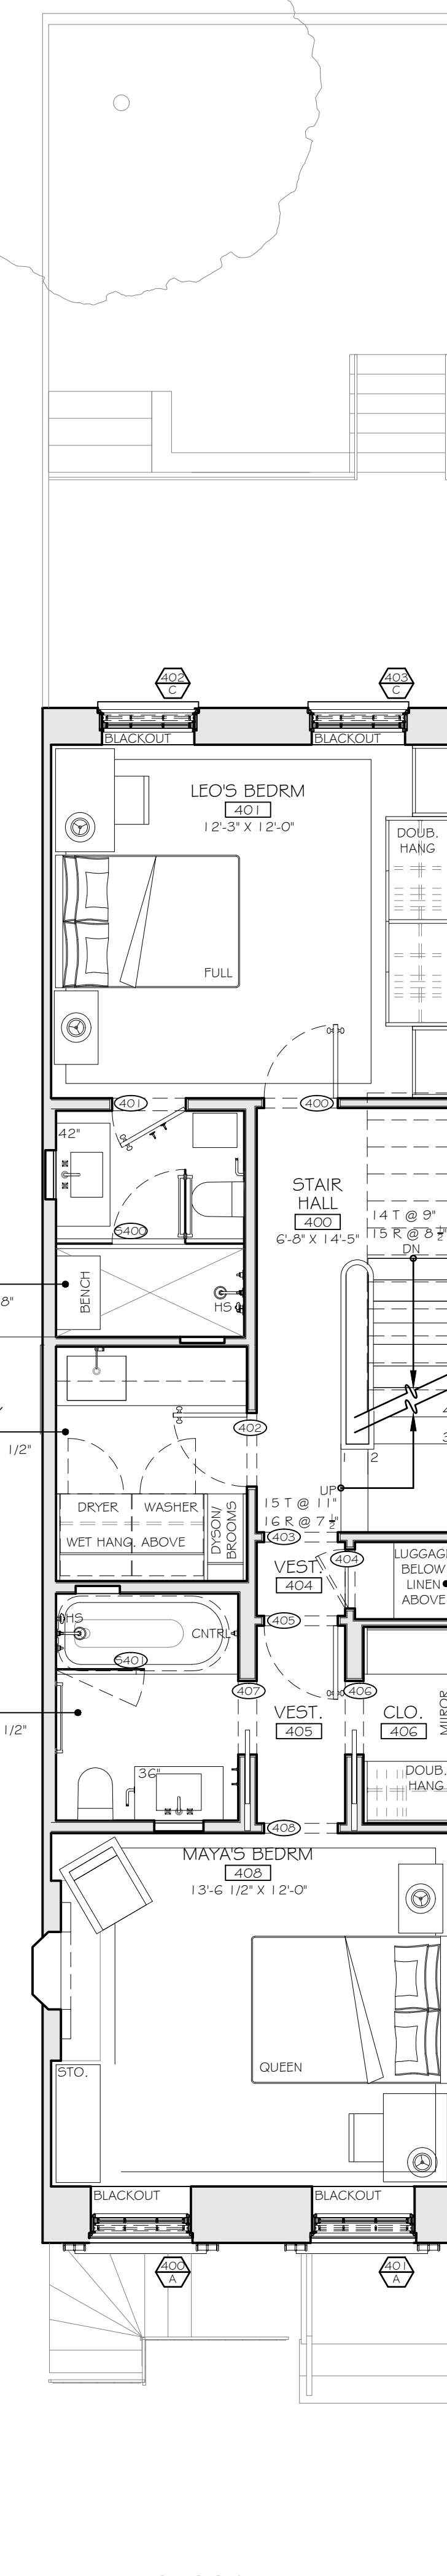

5 PROPOSED 4TH FLOOR PLAN
SCALE: 1/4"=1'-0"

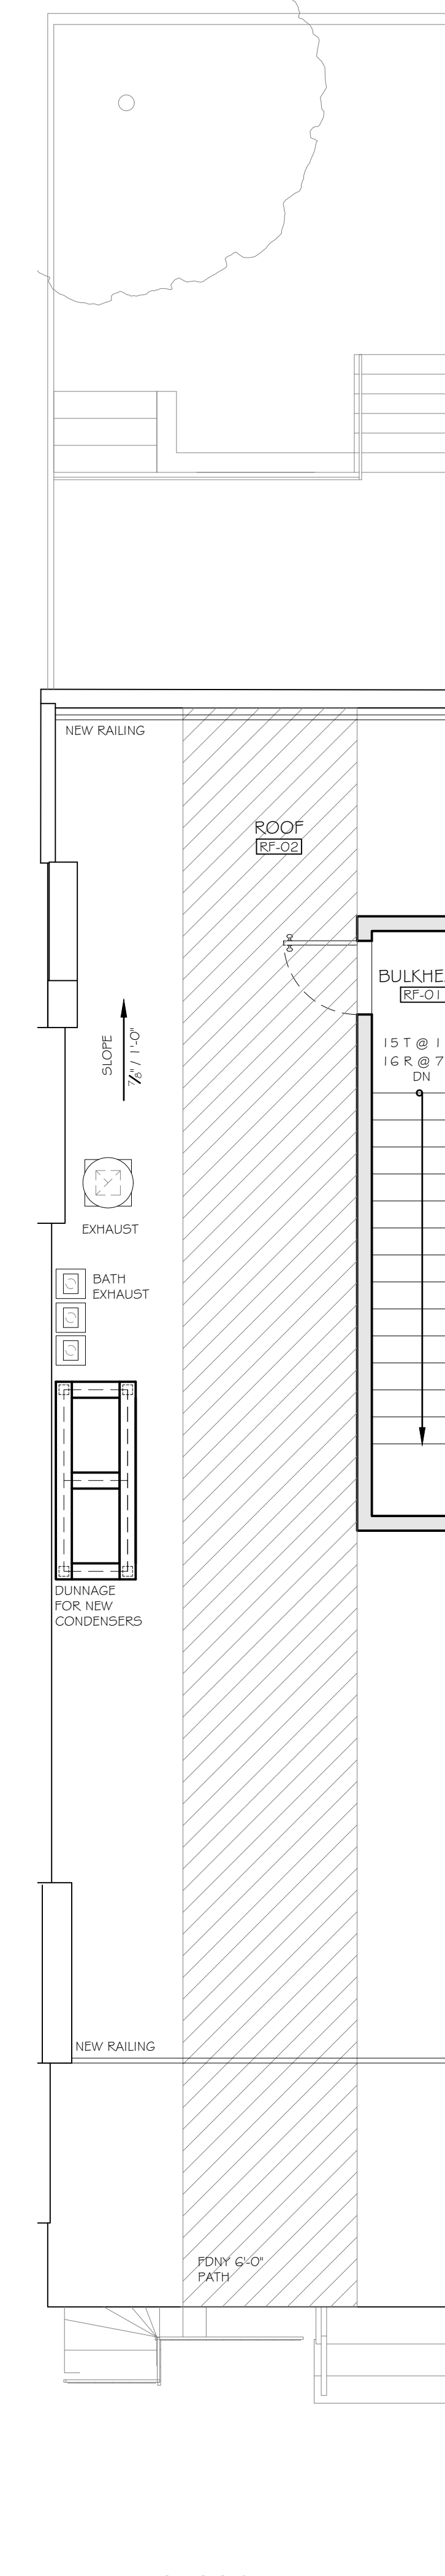

6 PROPOSED ROOF PLAN
SCALE: 1/4"=1'-0"

ISSUE: DATE:

NOTES:

ALEX TAYLOR ARCHITECTURE
241 CENTRAL PARK WEST (13B)
NEW YORK, NY 10024

TOWNHOUSE IN
GRAMERCY PARK
135 EAST 18TH STREET,
NEW YORK, NY 10003

PROPOSED PLANS

DATE	AUG-13-2025	A-100
SCALE	AS NOTED	
DRAWN BY	AW	
PROJECT	2025.03	